हिन्दुस्तान पेट्रोलियम HP इंजीनियर्स इंडिया लिमिटेड (भारत सरकार का उपक्रम) ENGINEERS INDIA LIMITED (A Govt. of India Undertaking)	**Residue Upgradation Facility (RUF)** **EPCC-3 Package for** **Visakh Refinery Modernization Project (VRMP)**	L&T Hydrocarbon Engineering **L&T- CHIYODA LIMITED**
Title: (504-LZ-930A/B) CIVIL DRAWING FOR DOCK LEVELER **Doc. No.: BO16-RUF-LT-504-MP-DW-NTPL(1)-13005**		**Rev. No.:** **Page No: 1 of 4**

OWNER : HINDUSTAN PETROLEUM CORPORATION LIMITED (HPCL)
PMC : ENGINEERS INDIA LIMITED, NEW DELHI (EIL)
UNIT : 504
PMC JOB NO. : B016
EQUIPMENT DESCRIPTION : DOCK LEVELER
EQUIPMENT TAG : 504-LZ-930A/B
P. R. NO. : BO16-RUF-LT-504-MP-PR-0014
VENDOR NAME : NIHVA TECHNOLOGIES PVT LTD
VENDOR DOCUMENT NO. : NIHVA_20-21_0158

DOCUMENT SUBMISSION STATUS – LTHE/VENDOR	**REVIEW STATUS**	
	LTHE	**EIL**
DOC. CATEGORY: (USE TICK MARK) ☑ R ☐ I	☐ Code 1 – No Comments. Proceed With Manufacture / Fabrication / Construction As Per The Document.	☐ Code 1 – No Comments. Proceed With Manufacture / Fabrication / Construction As Per The Document.
ISSUED FOR	☑ Code 2 – Proceed With Manufacture/Fabrication/Construction As Per Commented Document. Revised Document Required.	☐ Code 2 – Proceed With Manufacture/Fabrication/Construction As Per Commented Document. Revised Document Required.
☐ INFORMATION ☑ REVIEW ☐ CONSTRUCTION ☐ AS BUILT	☐ Review Code 3 – Document Does Not Conform To Basic Requirements As Marked. Resubmit For Review	☐ Review Code 3 – Document Does Not Conform To Basic Requirements As Marked. Resubmit For Review
	☐ Code R– Document Is Retained For Records. Proceed With Manufacture / Fabrication	☐ Code R– Document Is Retained For Records. Proceed With Manufacture / Fabrication
	☐ Code V- Void (Submission Required / Not Required)	☐ Code V- Void (Submission Required / Not Required)
	DISCIPLINE | SIGN | DAT	DISCIPLINE | SIGN | DATE

01	Issued for Approval	Shilpa	Amit K	Amit K			24/09/2021
Revision No.	**Description**	**Prepared by**	**Reviewed by**	**Approved by**	**Reviewed by**	**Approved by**	**Approved Date**

REVISION HISTORY SHEET

REV. NO.	REV. DATE	REVISED PAGE	REVISION DESCRIPTION
01	24/09/2021	NA	ISSUED FOR APPROVAL

DWG. NO.

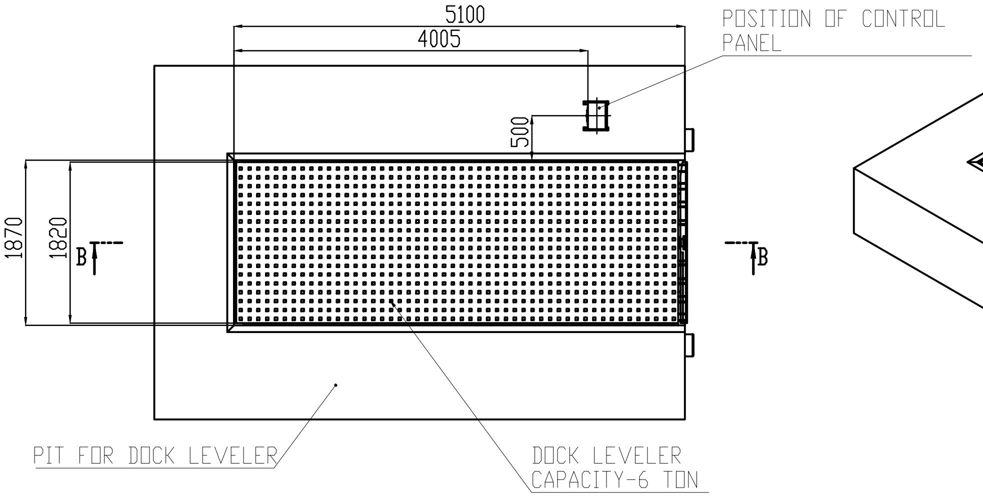

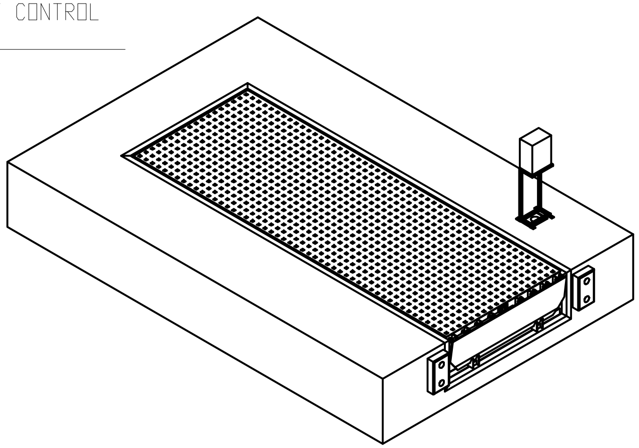

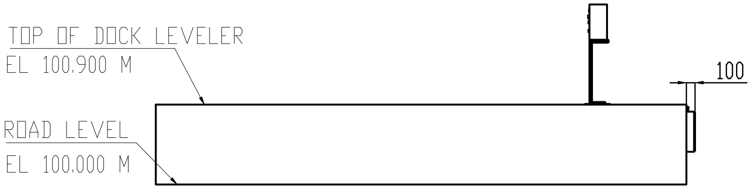

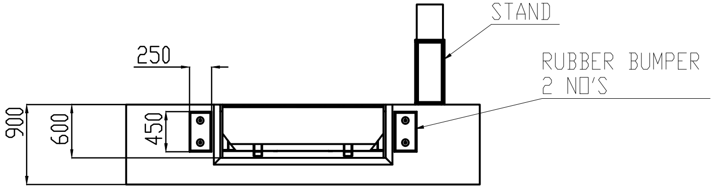

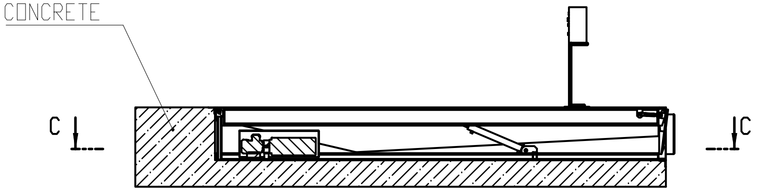

SECTION B-B
SCALE 1 : 28

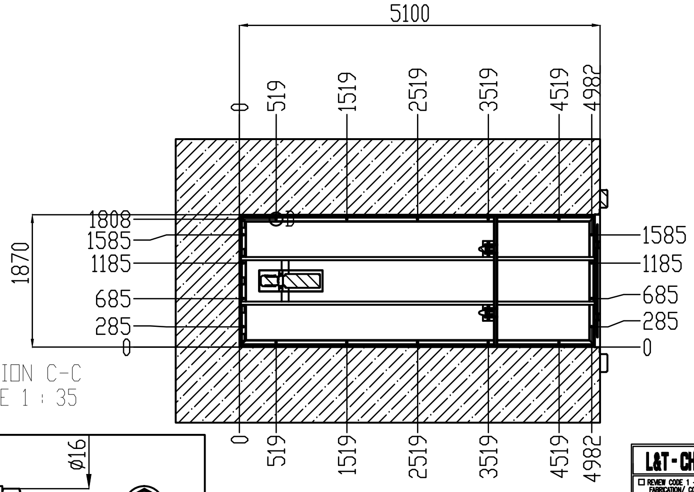

SECTION C-C
SCALE 1 : 35

PRODUCT DESCRIPTION -

1. DOCK LEVELER - PIT MOUNTED ELECTRO-HYDRAULIC TYPE
2. CAPACITY- 6 TON POINT LOAD
3. QTY- 2 NOS
4. PRODUCT SIZE- 5100mm(L)X1820mm(W)X600mm(D)
5. PIT SIZE-5100mm(L)X1870mm(W)X600mm(D)

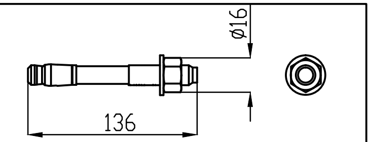

DETAILS OF ANCHOR WEDGE BOLT M16

DETAIL D
SCALE 1 : 35

L&T - CHIYODA LIMITED

☐ REVIEW CODE 1 - NO COMMENTS PROCEED WITH MANUFACTURE / FABRICATION/ CONSTRUCTION AS PER THE DOCUMENT.
☐ REVIEW CODE 2 - PROCEED WITH MANUFACTURE/ FABRICATION /CONSTRUCTION AS PER THE COMMENTED DOCUMENT. REVISED DOCUMENT REQUIRED.
☐ REVIEW CODE 3 - DOCUMENT DOES NOT CONFORM TO BASIC REQUIREMENTS AS MARKED. RESUBMIT FOR REVIEW.
☐ R - DOCUMENT IS RETAINED FOR RECORDS. PROCEED WITH MANUFACTURE / FABRICATION
☐ V-VOID

COMMENTED BY	REVIEWED BY	APPROVED BY	DATE

THIS REVIEW / APPROVAL DOES NOT RELIEVE THE VENDOR / MANUFACTURER OF THE FULL RESPONSIBILITY AS TO DESIGN CORRECTNESS OF DIMENSIONS & COMPLIANCE WITHALL APPLICABLE REGULATIONS AND WITH THE REQUIREMENTS MADE IN PURCHASER SPECIFICATIONS.

DRAWING NO.	DRAWING TITLE	REV
504-LZ-930A/B	GAD OF DOCK LEVELER	

REFERENCE DOCUMENTS / DRAWINGS

DRG. CATEGORY: (USE TICK MARK) ☐ R ☑ I
SCH. DATE OF SUBMISSION
EIL REVIEW/APPROVAL CODE:
VPTL NO.:

DOCUMENT STATUS
STATEMENT OF SUB: 1st 2nd 3rd
☐ FINAL FOR CODE-1 ☐ AS BUILT

ISSUED FOR
☐ AS BUILT ☑ INFORMATION
☐ CONSTRUCTION ☐ REVIEW

SIGN: DATE:

☐ REVIEW CODE 1 - NO COMMENTS PROCEED WITH MANUFACTURE / FABRICATION/ CONSTRUCTION AS PER THE DOCUMENT.
☐ REVIEW CODE 2 - PROCEED WITH MANUFACTURE / FABRICATION / CONSTRUCTION AS PER THE COMMENTED DOCUMENT. REVISED DOCUMENT REQUIRED.
☐ REVIEW CODE 3 - DOCUMENT DOES NOT CONFORM TO BASIC REQUIREMENTS AS MARKED. RESUBMIT FOR REVIEW.
☐ R - DOCUMENT IS RETAINED FOR RECORDS. PROCEED WITH MANUFACTURE / FABRICATION
☐ V-VOID

NAME DICIPLINE SIGN. DATE

REV.	DESCRIPTION	DRN	CHECKED	APPROVED	REVIEWED	APPROVED	DATE
00	ISSUED FOR APPROVAL	SMS	VJ	AK			

OWNER **HINDUSTAN PETROLEUM CORPORATION LIMITED**
VISAKH REFINERY MODERNIZATION PROJECT
EPCC-03 PACKAGE FOR RESIDUE UP-GRADATION FACILITY (RUF)

PMC : इंजीनियर्स इंडिया लिमिटेड ENGINEERS INDIA LIMITED
(A Govt. of India Undertaking)

LSTK CONTRACTOR: L&T Hydrocarbon Engineering

DETAILED ENGINEERING CENTER: L&T - CHIYODA LIMITED

VENDOR : NIHVA TECHNOLOGIES PVT LTD
VENDOR PO NO: REFINARY/75000-82256/VMM
VENDOR DWG. NO: NIHVA_20-21_0158

DATE 31.05.21
SCALE 1:1
DEPT: DESIGN
TITLE: CIVIL DRAWING FOR DOCK LEVELER (504-LZ-930A/B)
DRN BY: SMS
CHK BY: VJ
APP BY: AK
PROJECT: L&T-RUF
PWO NO.:
DRG. NO.: 3016-RUF-LT-504-MP-SV-NTPL(D)-13005
SH. 1 OF 2
REV. 00
CAD REVISE THIS DRG. USING CAD SYSTEM ONLY FILE:

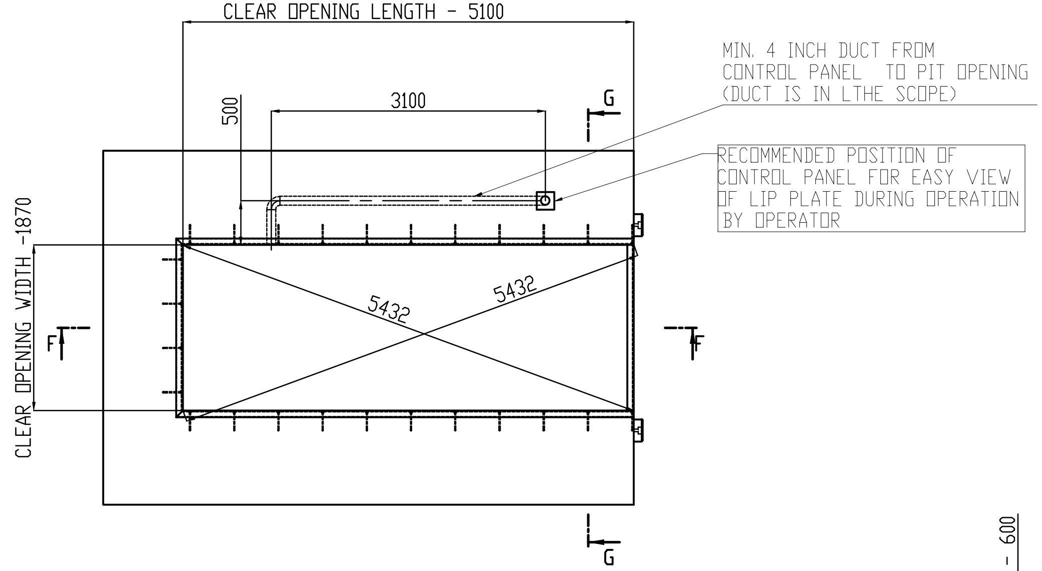
CLEAR OPENING LENGTH - 5100
3100
500
G
MIN. 4 INCH DUCT FROM
CONTROL PANEL TO PIT OPENING
(DUCT IS IN LTHE SCOPE)
RECOMMENDED POSITION OF
CONTROL PANEL FOR EASY VIEW
OF LIP PLATE DURING OPERATION
BY OPERATOR
CLEAR OPENING WIDTH -1870
5432
5432
F
F
G

TOP VIEW OF DOCK PIT

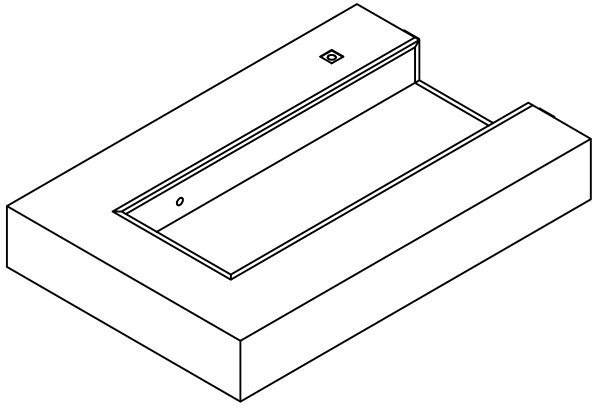

ISOMETRIC VIEW OF DOCK LEVELER PIT

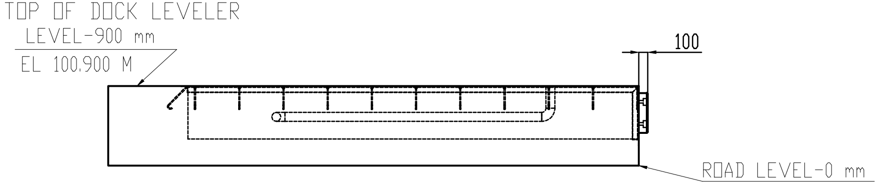

FRONT VIEW OF DOCK PIT

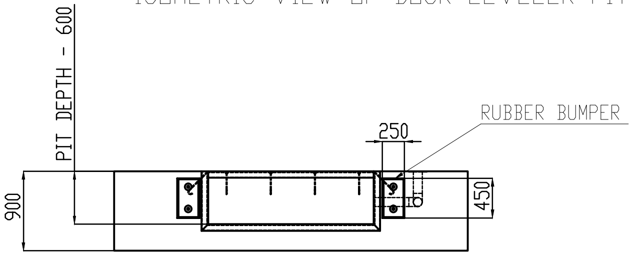

SIDE VIEW OF DOCK PIT

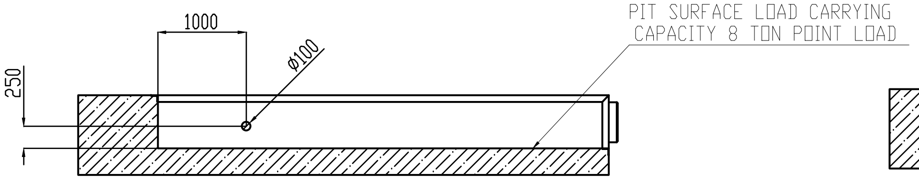

SECTION F-F
SCALE 1 : 28

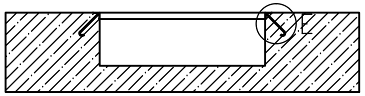

SECTION G-G
SCALE 1 : 28

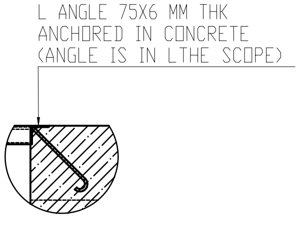

DETAIL E
SCALE 1 : 10

NOTES -

1. PIT & ALL CIVIL WORK IS IN LTHE SCOPE .
2. AT ALL EDGES OF PIT ANGLE 75X6 MM THK(ANGLE IN LTHE SCOPE) TO BE ANCHORED IN CONCRETE .
3. PIT SURFACE SHOULD BE PLAIN & LOAD CARRYING CAPACITY FOR PIT SURFACE SHOULB OF 8 TON POINT LOAD .
4. MINIMUM 4 INCH DUCT TO BE PROVIDED FROM CONTROL PANEL TO PIT OPENING BY LTHE FOR ELECTRICAL CABLE ROUTING . REQUIRED DUCT IS IN LTHE SCOPE.
5. CONTROL PANEL IS PROVIDED WITH ELECTRICAL CABLE LENGTH OF 5 METER AS STANDARD . CONTROL PANEL SHOULD BE LOCATED NEAR DOCK LEVELER FOR EASY VIEW OF LIP RESTING ON VEHICLE .

L&T - CHIYODA LIMITED

☐ REVIEW CODE 1 – NO COMMENTS PROCEED WITH MANUFACTURE / FABRICATION/ CONSTRUCTION AS PER THE DOCUMENT.
☐ REVIEW CODE 2 – PROCEED WITH MANUFACTURE/ FABRICATION /CONSTRUCTION AS PER THE COMMENTED DOCUMENT. REVISED DOCUMENT REQUIRED.
☐ REVIEW CODE 3 – DOCUMENT DOES NOT CONFORM TO BASIC REQUIREMENTS AS MARKED. RESUBMIT FOR REVIEW.
☐ R – DOCUMENT IS RETAINED FOR RECORDS. PROCEED WITH MANUFACTURE / FABRICATION
☐ V–VOID

COMMENTED BY	REVIEWED BY	APPROVED BY	DATE

THIS REVIEW / APPROVAL DOES NOT RELIEVE THE VENDOR / MANUFACTURER OF THE FULL RESPONSIBILITY AS TO DESIGN CORRECTNESS OF DIMENSIONS & COMPLIANCE WITHALL APPLICABLE REGULATIONS AND WITH THE REQUIREMENTS MADE IN PURCHASER SPECIFICATIONS.

DRAWING NO.	DRAWING TITLE	REV
504-LZ-930A/B	GAD OF DOCK LEVELER	

REFERENCE DOCUMENTS / DRAWINGS

DRG. CATEGORY: (USE TICK MARK) R I
SCH. DATE OF SUBMISSION
EIL REVIEW/APPROVAL CODE:
VPTL NO.:

DOCUMENT STATUS
STATEMENT OF SUB: 1st 2nd 3rd
☐ FINAL FOR CODE-1 ☐ AS BUILT
ISSUED FOR
☐ AS BUILT ☐ INFORMATION
☐ CONSTRUCTION ☐ REVIEW
SIGN: DATE:

☐ REVIEW CODE 1 – NO COMMENTS PROCEED WITH MANUFACTURE / FABRICATION/ CONSTRUCTION AS PER THE DOCUMENT.
☐ REVIEW CODE 2 – PROCEED WITH MANUFACTURE / FABRICATION / CONSTRUCTION AS PER THE COMMENTED DOCUMENT. REVISED DOCUMENT REQUIRED.
☐ REVIEW CODE 3 – DOCUMENT DOES NOT CONFORM TO BASIC REQUIREMENTS AS MARKED. RESUBMIT FOR REVIEW.
☐ R – DOCUMENT IS RETAINED FOR RECORDS. PROCEED WITH MANUFACTURE / FABRICATION
☐ V–VOID
NAME DICIPLINE SIGN. DATE

REV.	DESCRIPTION	DRN	CHECKED	APPROVED	REVIEWED	APPROVED	DATE
00	ISSUED FOR APPROVAL	SMS	VJ	AK			

OWNER: **HINDUSTAN PETROLEUM CORPORATION LIMITED**
VISAKH REFINERY MODERNIZATION PROJECT
EPCC-03 PACKAGE FOR RESIDUE UP-GRADATION FACILITY (RUF)

PMC : इंजीनियर्स इंडिया लिमिटेड ENGINEERS INDIA LIMITED (A Govt. of India Undertaking)

LSTK CONTRACTOR: L&T Hydrocarbon Engineering

DETAILED ENGINEERING CENTER: L&T - CHIYODA LIMITED

VENDOR : NIHVA TECHNOLOGIES PVT LTD
VENDOR PO NO: REFINARY/75000-82256/VMM
VENDOR DWG. NO: NIHVA_20-21_0158

DATE 29.5.21
SCALE 1:1
TITLE: CIVIL DRAWING FOR DOCK LEVELER (504-LZ-930A/B)
DEPT: DESIGN
DRN BY: SMS
CHK BY: VJ
APP BY: AK
PROJECT: L&T-RUF
PWO NO.:
DRG. NO.: B066-RUF-LT-504-MP-DV-NTPL(1)-13005
SH. 2 OF 2
REV.00
CAD REVISE THIS DRG. USING CAD SYSTEM ONLY FILE: