


DRAWING

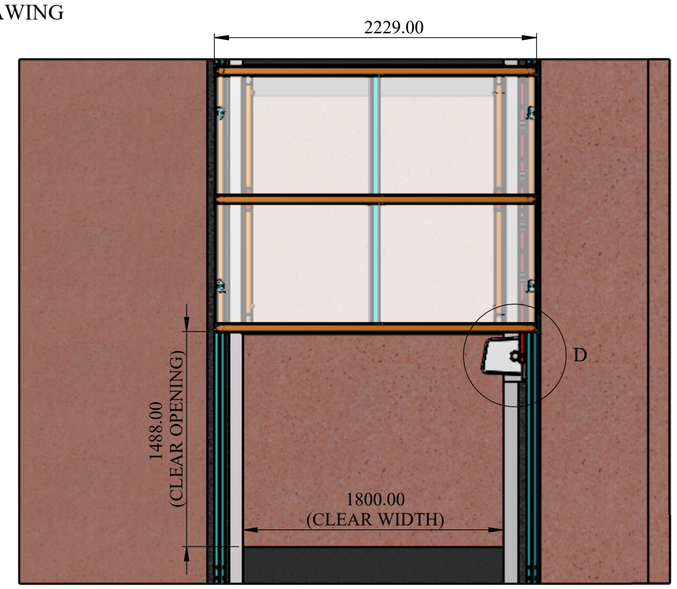


T.V.

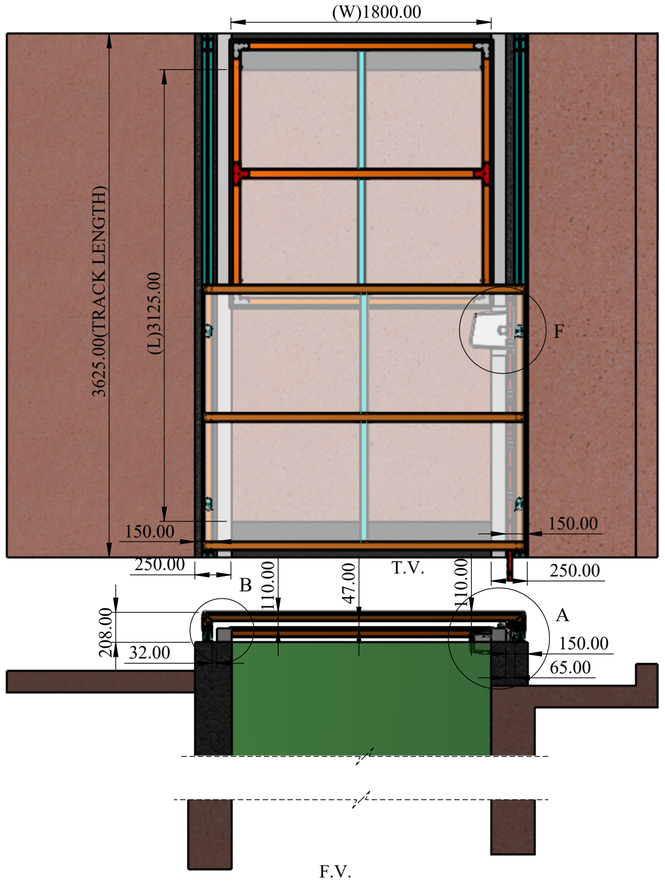


F.V.

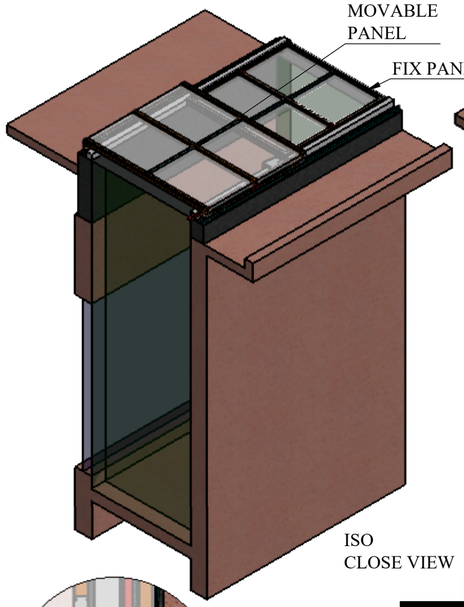


ISO
CLOSE VIEW

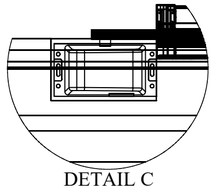


DETAIL C
SCALE 1 : 14

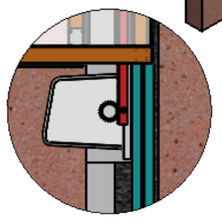

DETAIL D
SCALE 1 : 15

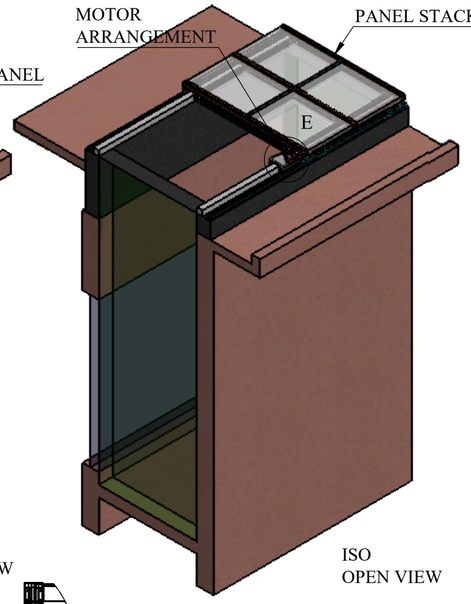


ISO
OPEN VIEW

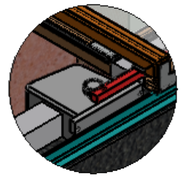


DETAIL E
SCALE 1 : 15


MOTOR MOUNTING
ARRANGEMENT

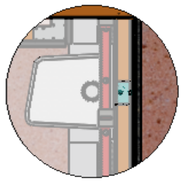


DETAIL F
SCALE 1 : 15

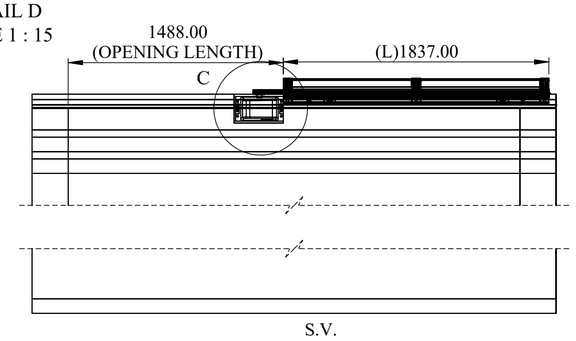


S.V.

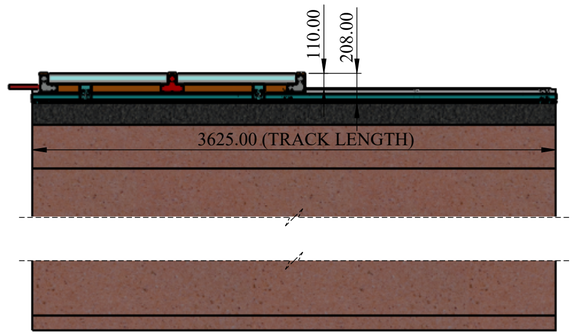

S.V.

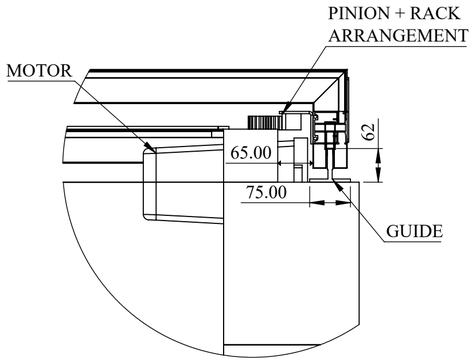

DETAIL A
SCALE 1 : 8

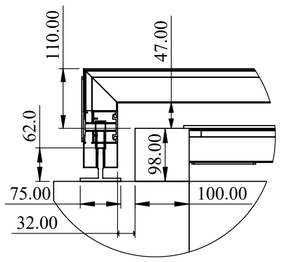

DETAIL B
SCALE 1 : 8

RETRACTABLE ROOF (AL+PC SHEET)			
SIZES	WIDTH (MM)	LENGTH (MM)	HEIGHT(MM)
1.	W1,800MM	3,125 MM	-

REV DESCRIPTION	DATE	REV NO
1.	11-08-2026	REV 00

NOTE :

THIS DRAWING IS ONLY FOR CLIENT APPROVAL
BASE STRUCTURE IN CLINT SCOPE.
EPDM RUBBER FLAPPER PROVIDED FOR AIR & WATER SEAL.
FOR MOTOR MOUNTING POCKET TO BE PROVIDED AT SITE BY CLIENT.

SPECIAL INSTRUCTION'S :

This drawing & design is the property of NIHVA TECHONOLOGIES PVT. LTD. Not to be sold or copied to any other concern

TITLE - RETRACTABLE ROOF

DWG NO - NTPL-

NIHVA TECHNOLOGIES PVT.LTD.PUNE
Website - www.nihva.com

	NAME	SIGNATURE	DATE
DRAWN	V.W.		11-08-2026
CHK'D	S.P.		12-08-2026
APPV'D	V.T.		12-08-2026

PRODUCT - RETRACTABLE ROOF
CLIENT NAME - K. RAHEJA
SITE LOCATION - MUMBAI
MATRIAL -
QTY - 1
If any queries contact - info@nihva.com
PROJECTION METHOD:
SCALE :
ALL DIMENSION ARE IN mm
A2
SHEET 1 OF 1