THIS DRAWING & DESIGN IS THE SOLE PROPERTY OF VMS & SHALL NOT BE COPIED, TRACED OR REPRODUCED BY ANY MEANS WITHOUT PRIOR WRITTEN CONSENT OF THE FIRM.

GENERAL NOTES :

1. ALL THE DIMENSIONS ARE UNFINISHED DIMENSIONS.
2. ALL DIMENSIONS ARE IN MM AND LEVELS ARE IN MT, UNLESS OTHERWISE MENTIONED.
3. ALL THE DIMENSIONS SHALL BE READ & NOT TO BE MEASURED.
4. IN CASE OF ANY DISCREPANCY, BRING IT TO THE NOTICE OF THE ARCHITECT IMMEDIATELY.
5. DETAIL DRAWING PRECEDES THE GENERAL DRAWING

STANDARD DRAWING SYMBOLS :

FINISHED LEVEL
UNFINISHED LEVEL

SECTION SYMBOL
UPPER HALF INDICATES DIAGRAM NO. (NUMERICAL VALUE) IN DRAWING SHEET & LOWER HALF INDICATES DRAWING NO.

ELEVATION SYMBOL
UPPER HALF INDICATES DIAGRAM NO. IN DRAWING SHEET & LOWER HALF INDICATES DRAWING NO.


WINDOW SYMBOL
UPPER HALF INDICATES WINDOW NO. & LOWER HALF INDICATES DRAWING NO.

DOOR SYMBOL
UPPER HALF INDICATES DOOR NO. & LOWER HALF INDICATES DRAWING NO.

GRAPHIC LEGEND :

MASONRY CUT IN PLAN/SECTION.

RCC COLUMN CUT IN PLAN.

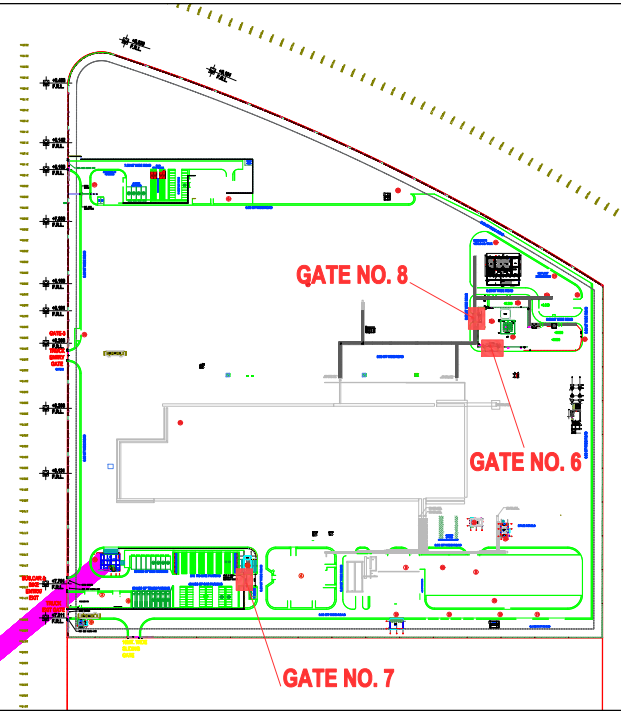


FOR REFERENCE

NO.	DATE	DESCRIPTION	DRAWN BY	CHECKED BY

REVISION HISTORY

KEY PLAN
SCALE : N.T.S.

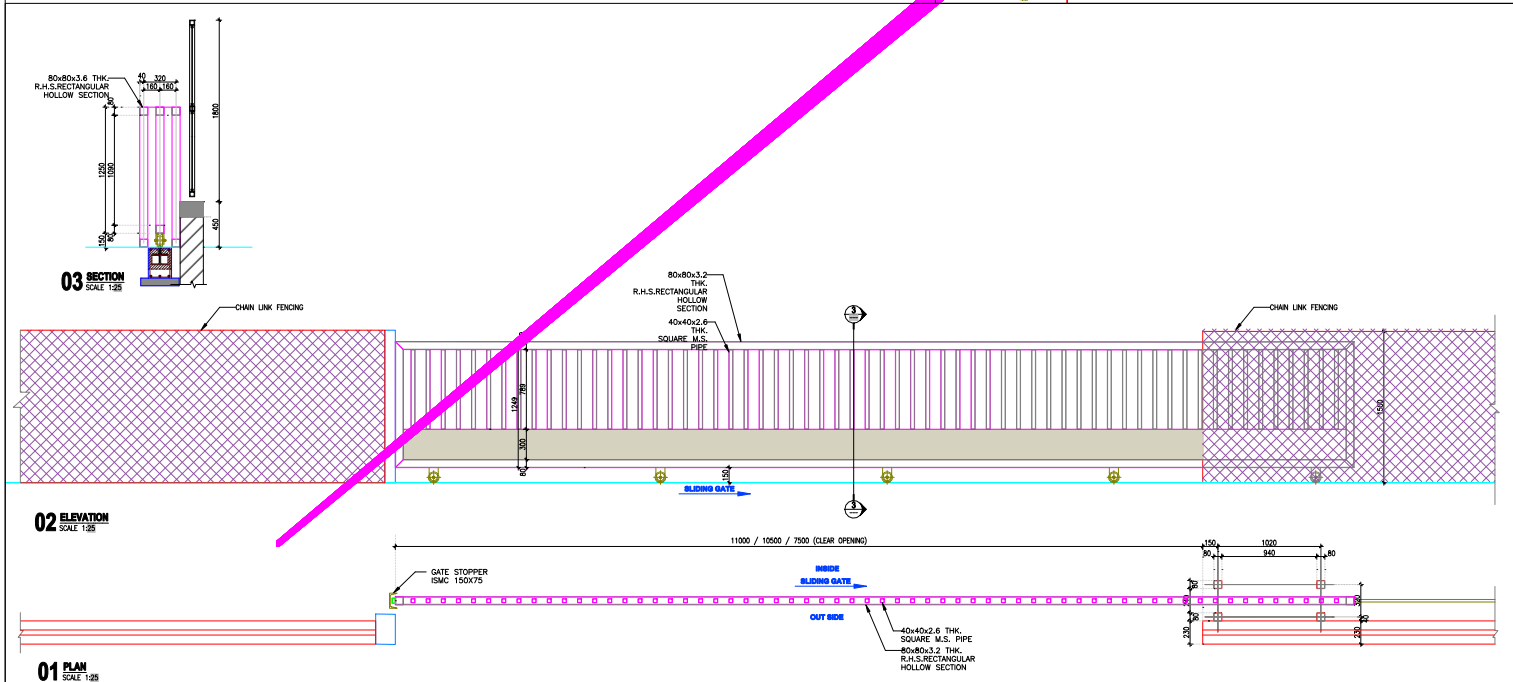

GATE NO. 6,7 & 8

REFERENCE DRAWINGS :

01. ARCHITECTURAL :	A.G.104
02. STRUCTURAL :	
03. HVAC :	-
04. ELECTRICAL :	-
05. UTILITIES :	-

SLIDING GATE DETAIL

PROJECT NAME : PHOTON
CLIENT : RENEW PHOTOVOLTAIC PVT. LTD.AT DHOLERA

PROJECT NO.	SCALE :	DRAWN : V.CHAUHAN
1521	AS NOTED	CHECKED: D.DOSHI
	DATE : 23-02-2024	APPROVED: D.DOSHI
		COORDINATION CHECKED: D.DOSHI

VMS ENGINEERING & DESIGN SERVICES (P) LTD.
CHITRAKOOT FLATS, B/H TIMES OF INDIA, OFF ASHRAM ROAD,
AHMEDABAD-380 009. PHONE +91 (079) 2658-4808, 4023-8238
WWW.VMSCONSULTANTS.COM

SHEET SIZE	DRAWING NO.	FOR	REVISION:
A2	A.G.902	R	R0