


FOUNDATION DETAILS

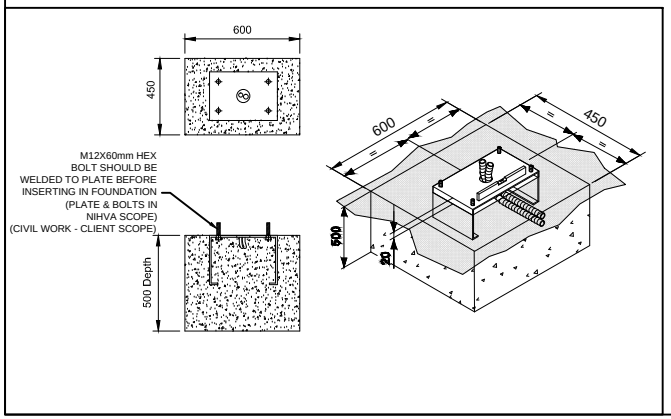

BOOM BARRIER QTY : 1 NO

TOLERANCE - ±10mm

This drawing & design is the property of NIHVA TECHNOLOGIES. Not to be sold or copied to any other concern.

REV NO	DATE	DRAWN	REMARK
R01	23.07.20	P.A	1. BOOM STAND CHANGE

TITLE: 8 MTR BOOM BARRIER

	NAME	SIGN	DATE
DRAWN	P.A		22.07.2020
CHECK	G.J		22.07.2020
APPROVAL			

NIHVA TECHNOLOGIES PVT. LTD. PUNE
Tel : 020 66304033
Email:- info@nihva.com
Website:- www.nihva.com

CLIENT - WANI PROJECTS & INFRA PVT. LTD

PROJECT -

SITE LOCATION - VIMANNAGAR, PUNE

DWG. NO. : NIHVA/20-21/0035/R01 | REV-R01

If any queries contact : projectsupport@nihva.com

SCALE: NTS | WT: | SHEET: 01 OF 01

ALL DIMENSION ARE IN mm