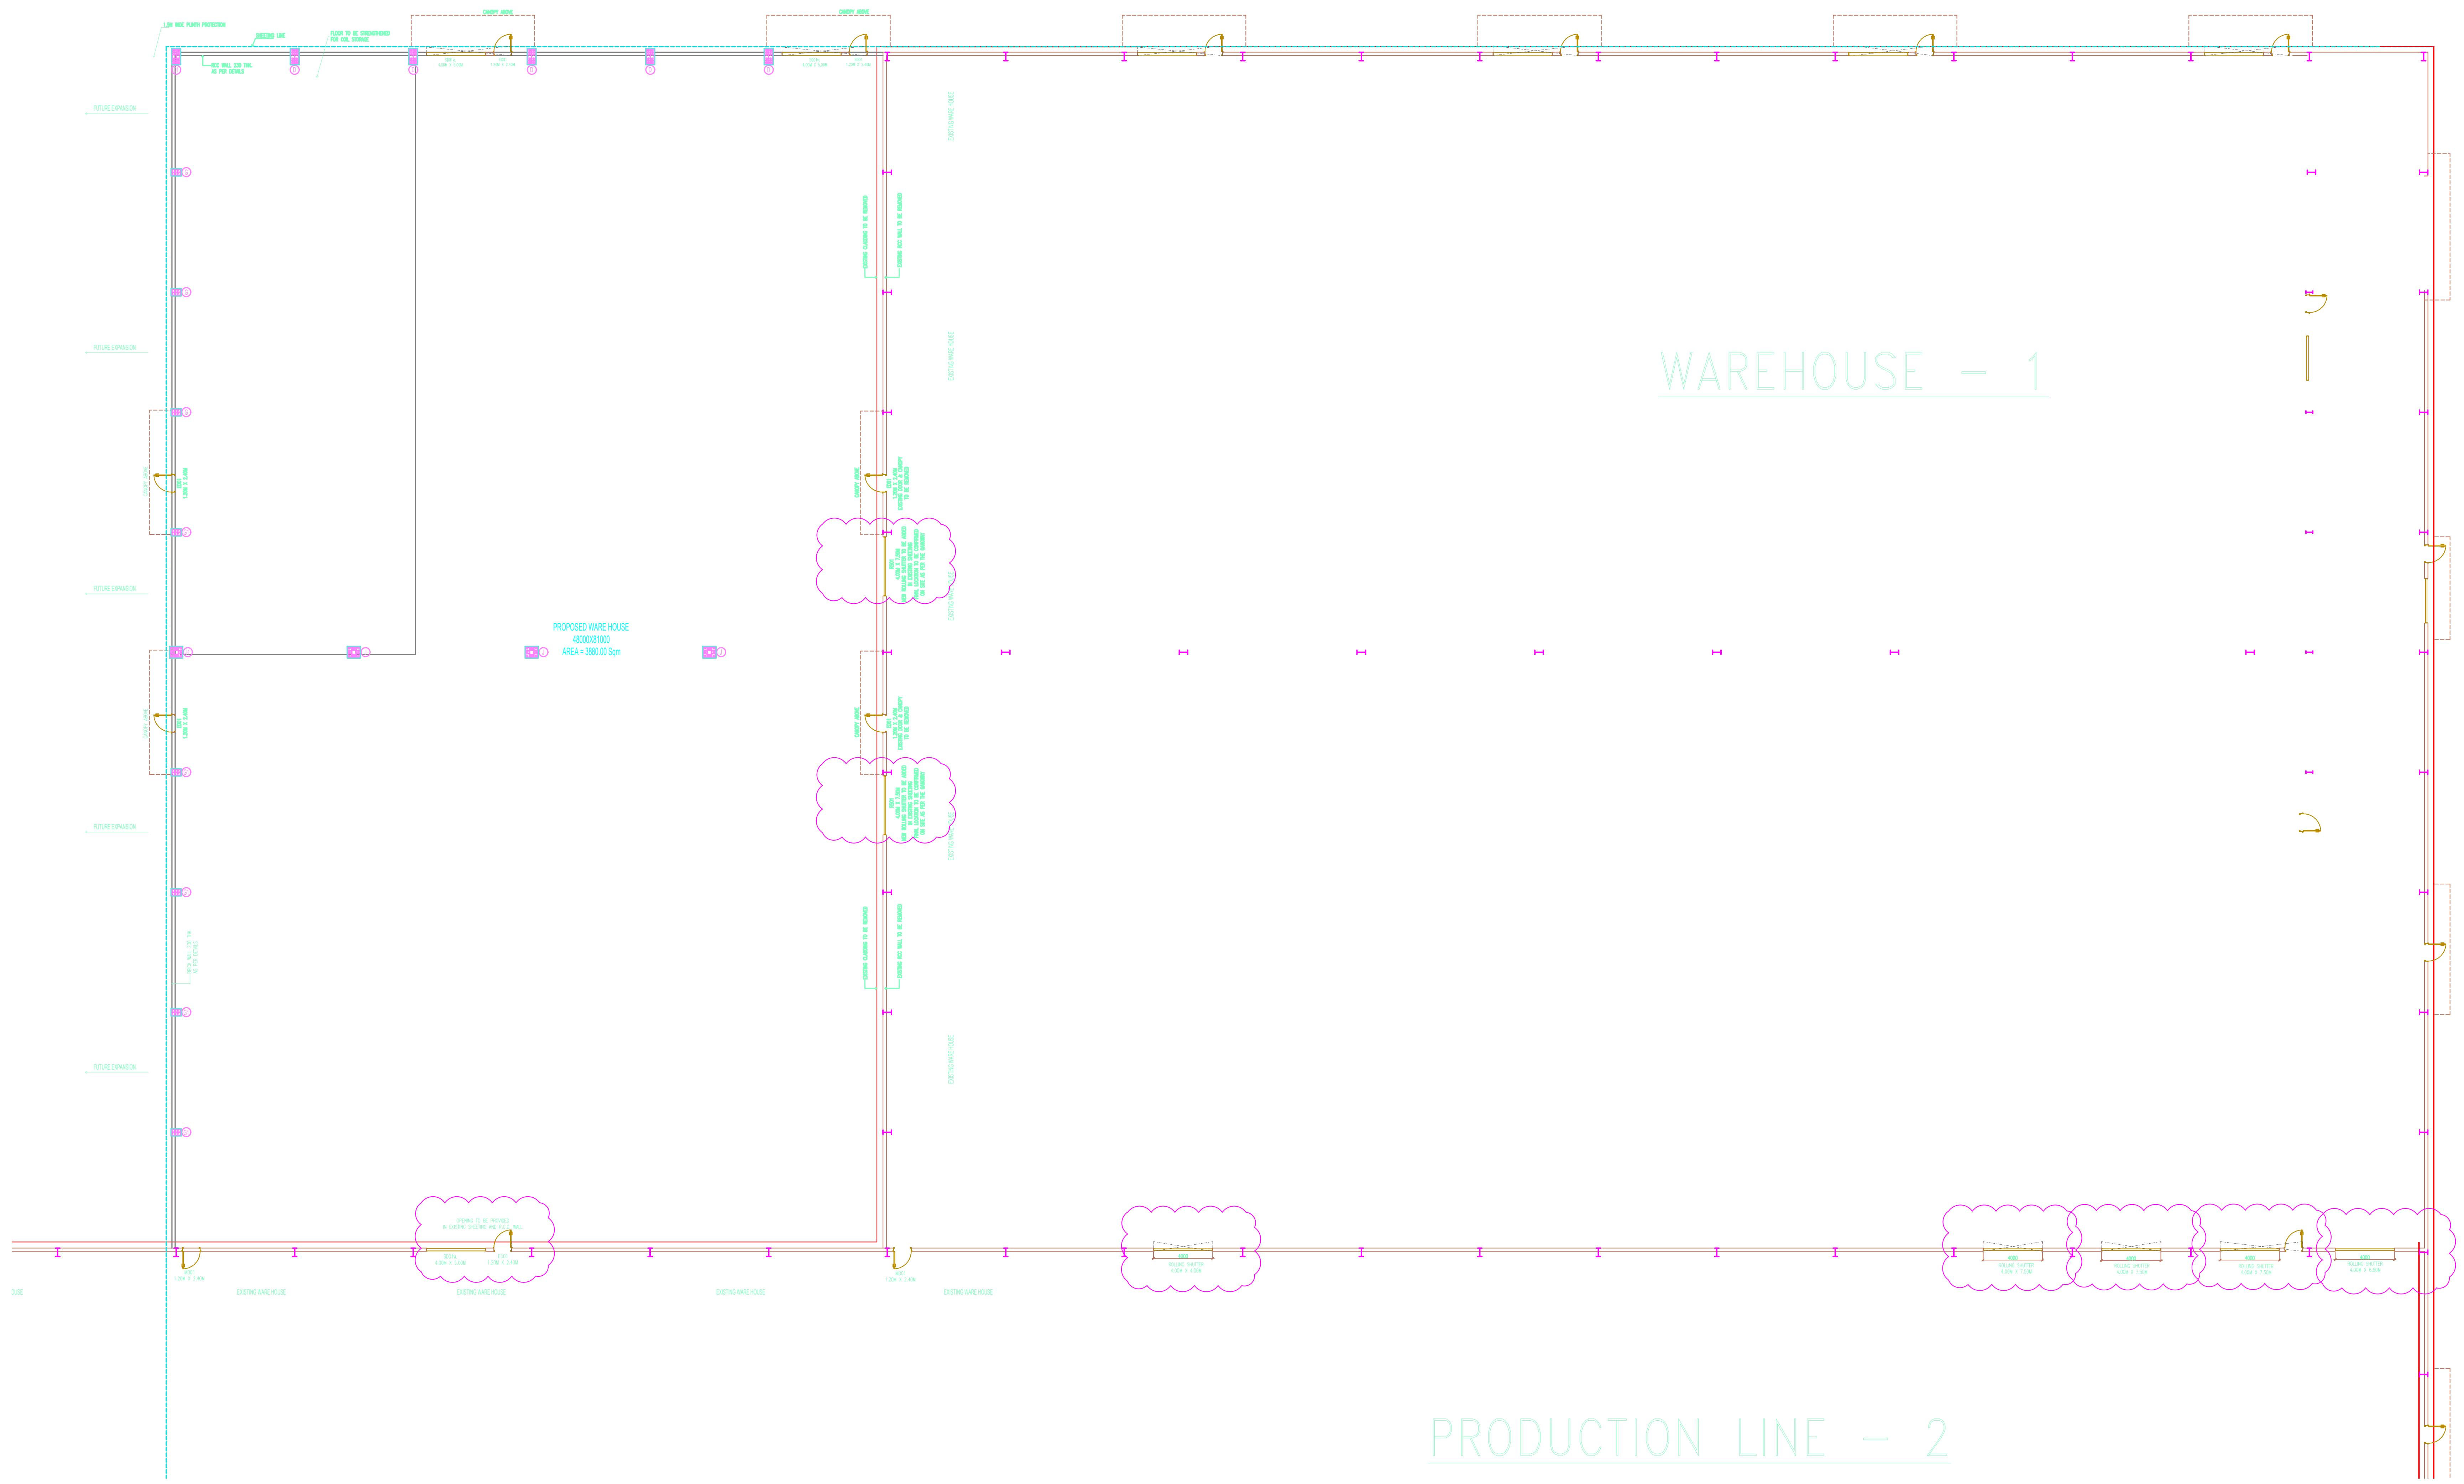

WARE HOUSE - GROUND FLOOR PART PLAN.

REVISIONS

NOS	REVISION DATE	DESCRIPTION
R0	31-07-2023	ORIGINAL

GENERAL NOTES

1) DRAWING SHALL NOT BE SCALED ONLY WRITTEN DIMENSIONS ARE TO BE FOLLOWED.
2) READ THIS DRAWING ALONG WITH THE STRUCTURAL / ENGINEER'S DRAWING.
3) ANY AMBIGUITY IN THIS DRAWING TO BE REFERRED TO THE ARCHITECT BEFORE THE EXECUTIONS OF THE WORK.
4) ALL DIMENSIONS ARE IN M.M. UNLESS OTHERWISE MENTIONED.
5) EVERY JOINT BETWEEN ANY R.C.C. MEMBER & BRICKWORK IS TO BE COVERED WITH WELDED MESH BEFORE PLASTERING.
6) PEB STRUCTURE & ROOFING CLADDING ARE NOT IN CIVIL CONTRACTOR'S SCOPE & SHOWN ONLY FOR THE INFORMATION. SHAPE OF ROOFING CLADDING MAY CHANGE AS PER PEB FINAL DESIGN.
7) FOR STRUCTURAL DETAILS REFER STRUCTURAL DRAWINGS.

CHECKED BY	DRAWN BY	SCALE	JOB NO	BUILDING	DRG. NO
		1:200			

TITLE : WARE HOUSE - GROUND FLOOR PLAN.

PROJECT :

CLIENT :

ARCHITECT'S NAME:

ARCHITECT: NIKHIL JOSHI. (CA/2012/56104)

SIGNATURE

ARCHICON
DESIGN
UNIT-601/602, Sai chambers, 5th. Floor,
Old Mumbai-Pune Highway Wakadewadi,
Pune 411 003, Maharashtra, India.
Tel:- +91 020 25542471 / 25542717
MAIL TO : architect@archicon.co.in