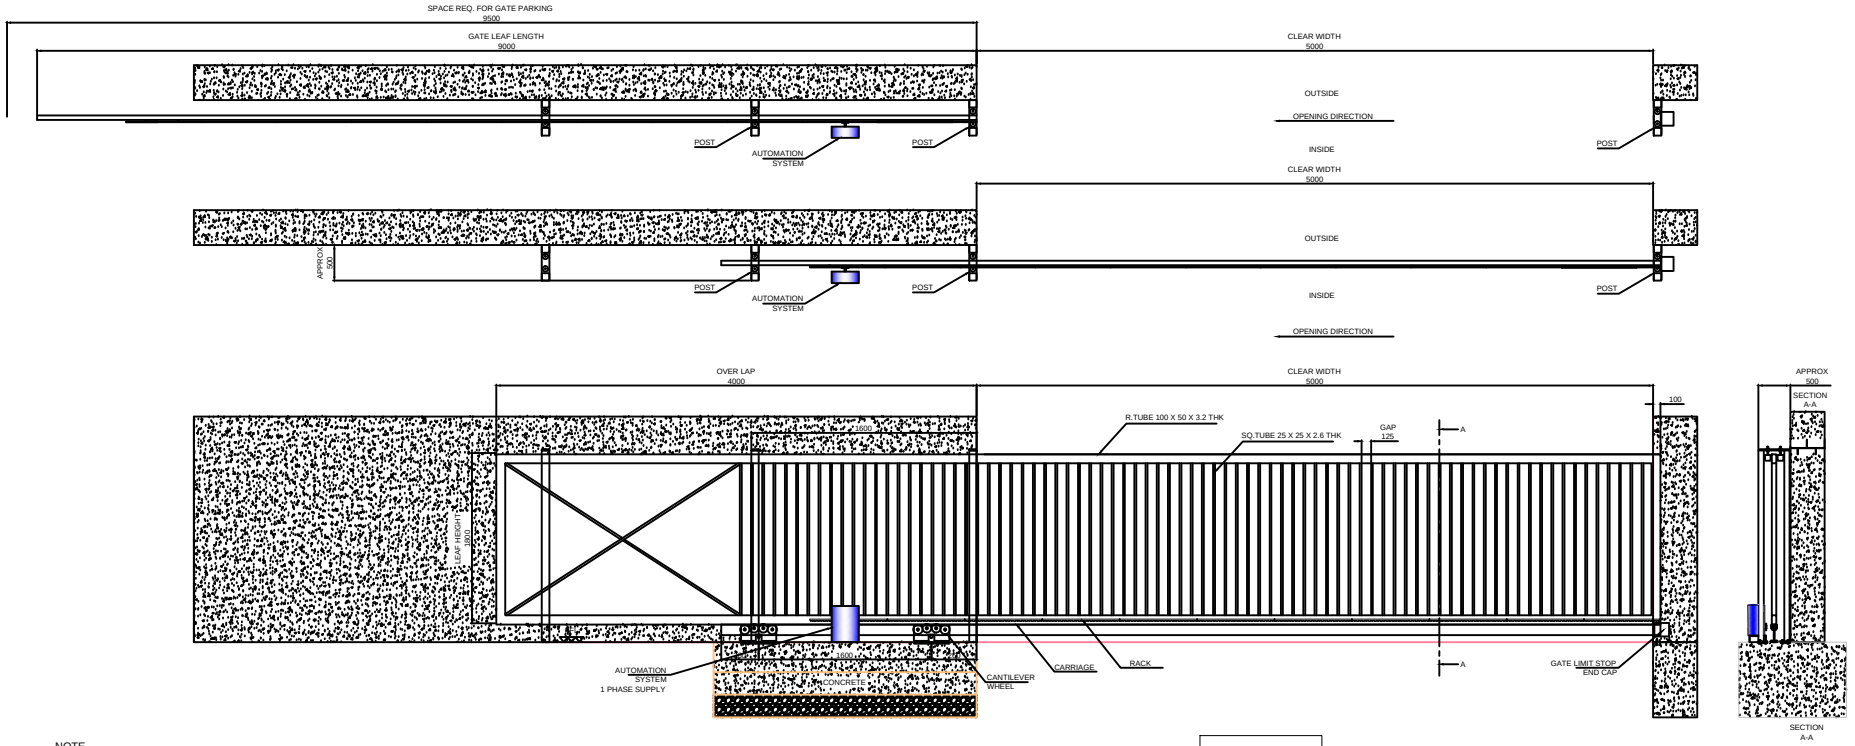


NOTE-
1. ALL REQUIRED CIVIL WORK WILL BE IN CLIENTS SCOPE.
2. TWO COATS OF PRIMER AND TWO COATS OF SYNTHETIC ENAMEL PAINT OF APPROVE SHADE.
3. SAFETY ACCESSORIES : FLASHING LIGHT, SAFETY PHOTOCELL.
4. GATE LEAF WILL BE IN TWO/THREE PARTS FOR TRANSPORTATION & WILL BE WELD TOGETHER ON SITE.

QTY : 2 NOS

TOLERANCE - ±10mm

This drawing & design is the property of NIHVA TECHNOLOGIES, Not to be used or copied for any other purpose.

REV NO	DATE	DRAWN	REMARK
R01	08.01.2020	P.A	1. GATE LEAF LENGTH CHANGE

TITLE
AUTOMATIC CANTILEVER GATE

NIHVA
NIHVA TECHNOLOGIES PVT. LTD.

NIHVA TECHNOLOGIES PVT. LTD. PUNE
Tel : 020 66304033
Email - info@nihva.com
Website:- www.nihva.com

	NAME	SIGN	DATE
DRAWN	P.A		23.12.2019
CHECK	G.J		23.12.2019
APPRD.			

CLIENT - DESAI CONSTRUCTION
PROJECT -
SITE LOCATION - GUJARAT
If any queries contact : design@nihva.com
DWG. NO. : NIHVA/1 9-20/0183/R01 REV- R01
ALL DIMENSION ARE IN mm
SCALE: NTS WT: SHEET: 01 OF 01