


2B	Reviewed. Comments enclosed. Incorporate the comments and re-submit for review.


Anuja Raje
Digitally signed by Anuja Raje
Date: 2025.05.16 11:29:22 +05'30'

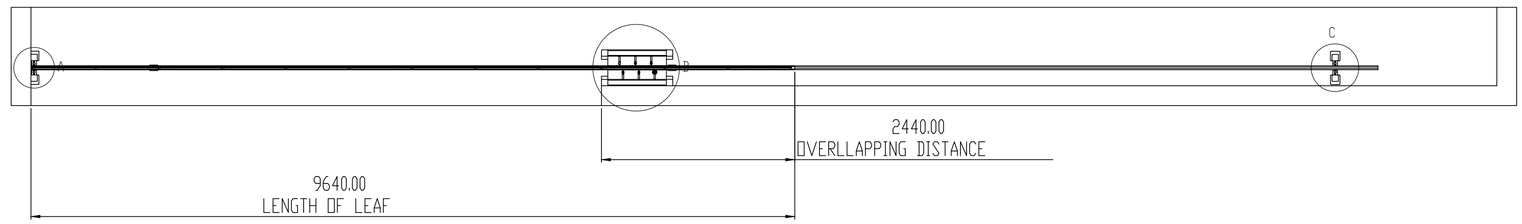

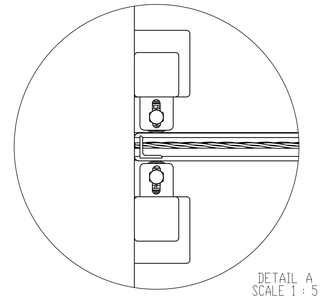


POST 1 & NYLON ROLLER ASM

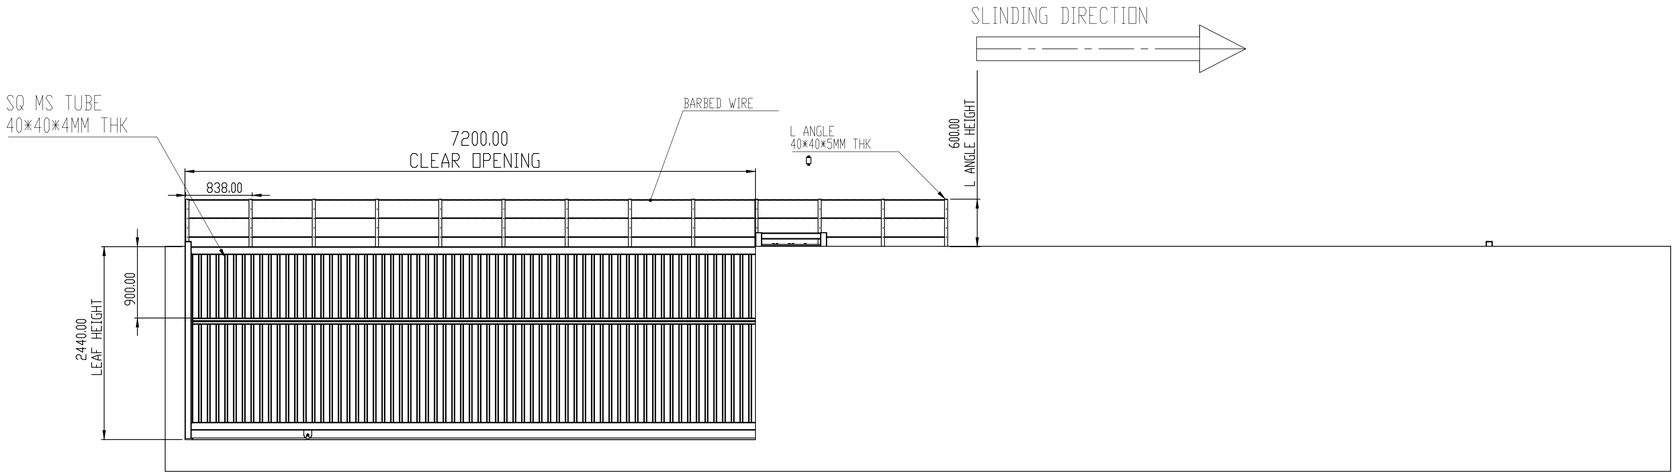

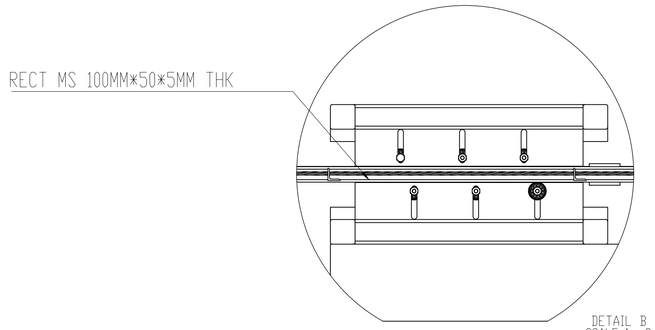

POST 2 & NYLON ROLLER ASM

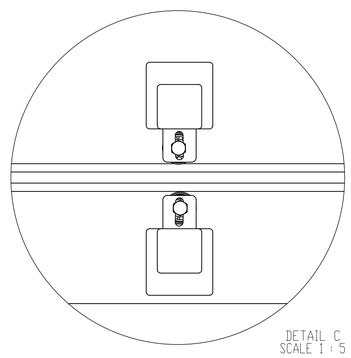

POST 3 & NYLON ROLLER ASM

TYPE 05

SINGLE SLIDING GATE

TCE COMMENTS:

1. Please refer to the latest master layout for the exact site dimensions and space availability.
2. Barbed wire fencing above the sliding gate is under finalization with the Air India team. TCE will confirm shortly.
3. Please specify whether the elevation view is from the inside or outside. It is currently unclear.
4. As the door sizes are as per the requirement, kindly consider the weight and design the sections accordingly.
   Also, the wheel should be a double wheel, as shown in the architectural layout.
   Locking arrangement details are missing from the GA drawing.

UNLESS OTHERWISE SPECIFIED: DIMENSIONS ARE IN MILLIMETERS SURFACE FINISH TOLERANCES: LINEAR: ANGULAR:	FINISH	DEBURR AND BREAK SHARP EDGES	NIHVA Technologies Pvt. Ltd.
NAME / SIGNATURE / DATE			TITLE: SINGLE SLINDING GATE
DRAWN			
CHK'D			
APPV'D			
MFG			
Q.A			
MATERIAL			DWG NO. GA DRAWING TYPE 05
WEIGHT:			SCALE:0.000 SHEET 1 OF 1