

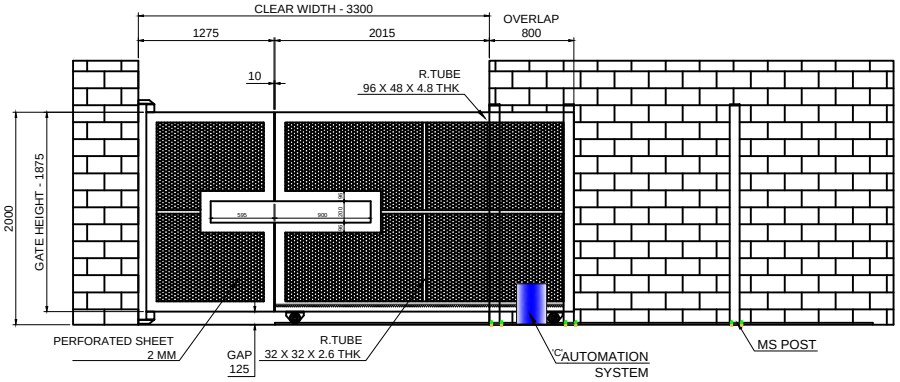



PLAN

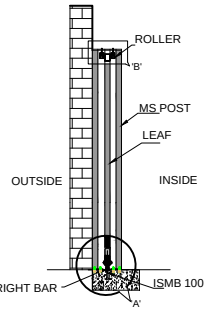



VIEW FROM INSIDE

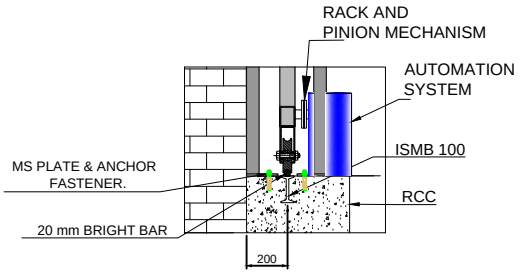


DETAIL VIEW OF A

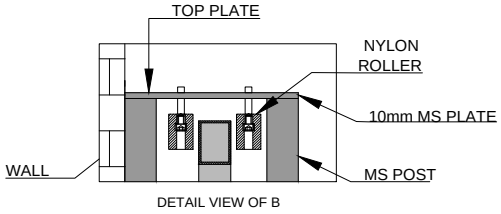


DETAIL VIEW OF B

| REV NO | REV DATE | DRAWN | REMARK |
|---|---|---|---|
| R01 | 18.09.2019 | P.V.A | 1. GATE POSITION CHANGE |

| SR.NO | RAL CODE | RAL COLOR |
|---|---|---|
| 04 | RAL 7035 | LIGHT GREY |
| 03 | RAL 5002 | ULTRAMARINE BLUE |
| 02 | RAL 9002 | GREY WHITE |
| 01 | RAL 1004 | GOLDEN YELLOW |

DIMENSION :

| CLEAR WIDTH | CLEAR HEIGHT | QUANTITY |
|---|---|---|
| 2015 mm | 1875mm | 1 NO |
| 1200 mm | 1875mm | 1 NO |

MATERIAL: MS

THICKNESS :

NOTE-
1. ALL REQUIRED CIVIL WORK WILL BE IN CLIENTS SCOPE.

TOLERANCE:- ± 05mm

NIHVA TECHNOLOGIES PVT. LTD.
Website:- www.nihva.com
NIHVA TECHNOLOGIES PVT. LTD. PUNE
Email:- info@nihva.com
TEL :020 66304033

TITLE:
# AUTOMATIC SINGLE LEAF SLIDING GATE & MANUAL WICKET GATE

CLIENT'S APPROVAL :

CLIENT - DHAMALE

PROJECT -

SITE LOCATION - NIGADI

DWG. NO. : NIHVA/19-20/0088/R01 | REV. : R01

SCALE: NTS | WT: | SHEET:1 OF 1

| | | | |
|---|---|---|---|
| DRAWN | P.A | | 17.09.2019 |
| CHECK | G.J | | 17.09.2019 |
| APPROVED | | | |

IF ANY QUERIES CONTACT:- design@nihva.com

NOTE: ALL DIMENSIONS ARE IN mm

THIS DRAWING & DESIGN IS THE PROPERTY OF NIHVA TECHNOLOGIES. NOT TO BE SOLD OR COPIED TO ANY OTHER CONCERN.