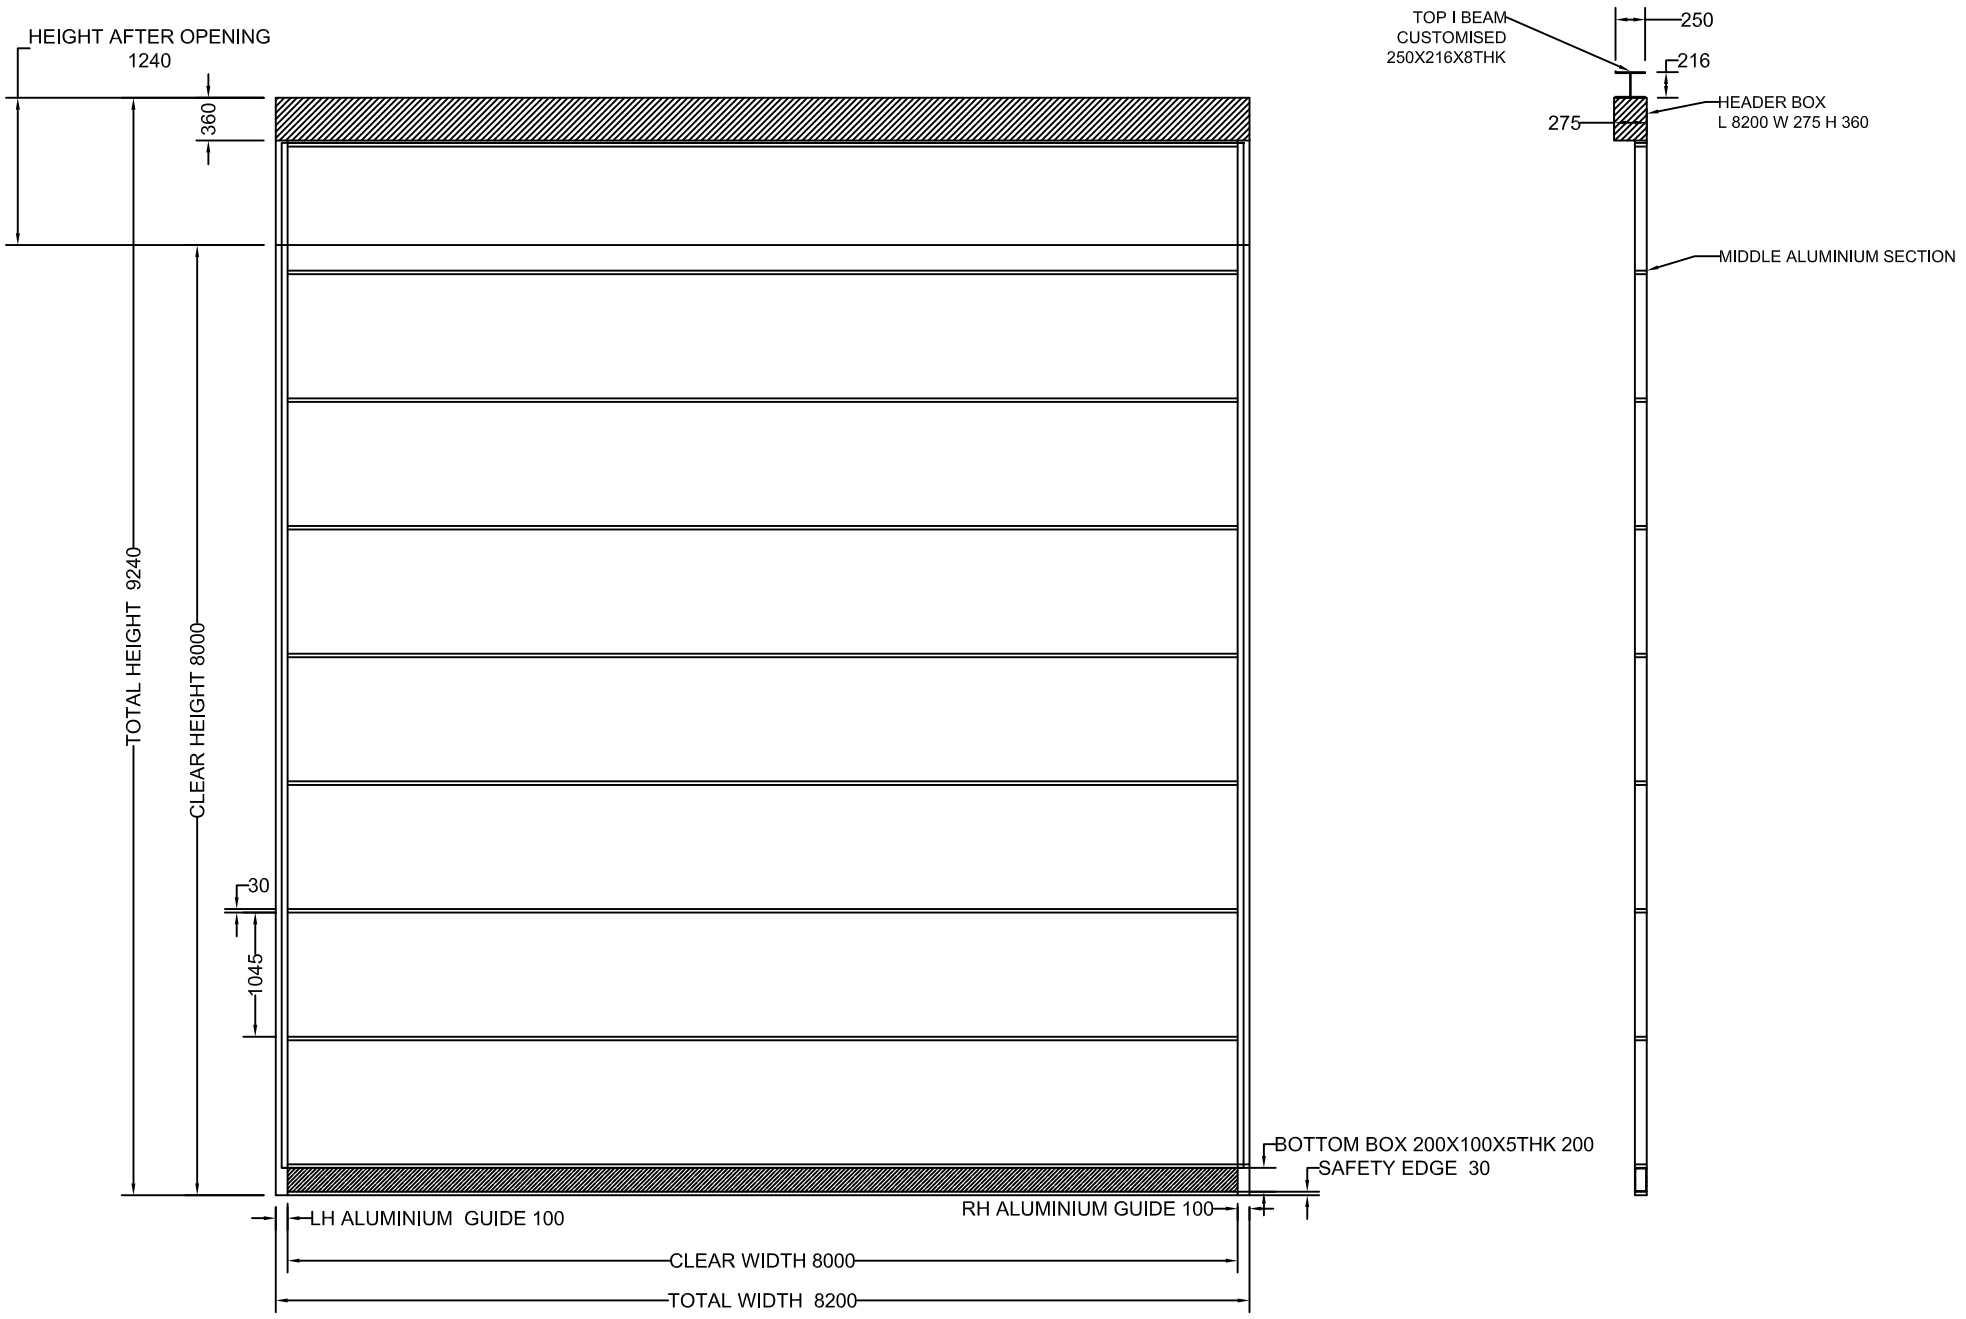
HEIGHT AFTER OPENING
1240
360
TOTAL HEIGHT 9240
CLEAR HEIGHT 8000
30
1045
TOP I BEAM
CUSTOMISED
250X216X8THK
250
216
275
HEADER BOX
L 8200 W 275 H 360
MIDDLE ALUMINIUM SECTION
BOTTOM BOX 200X100X5THK 200
SAFETY EDGE 30
LH ALUMINIUM GUIDE 100
RH ALUMINIUM GUIDE 100
CLEAR WIDTH 8000
TOTAL WIDTH 8200