

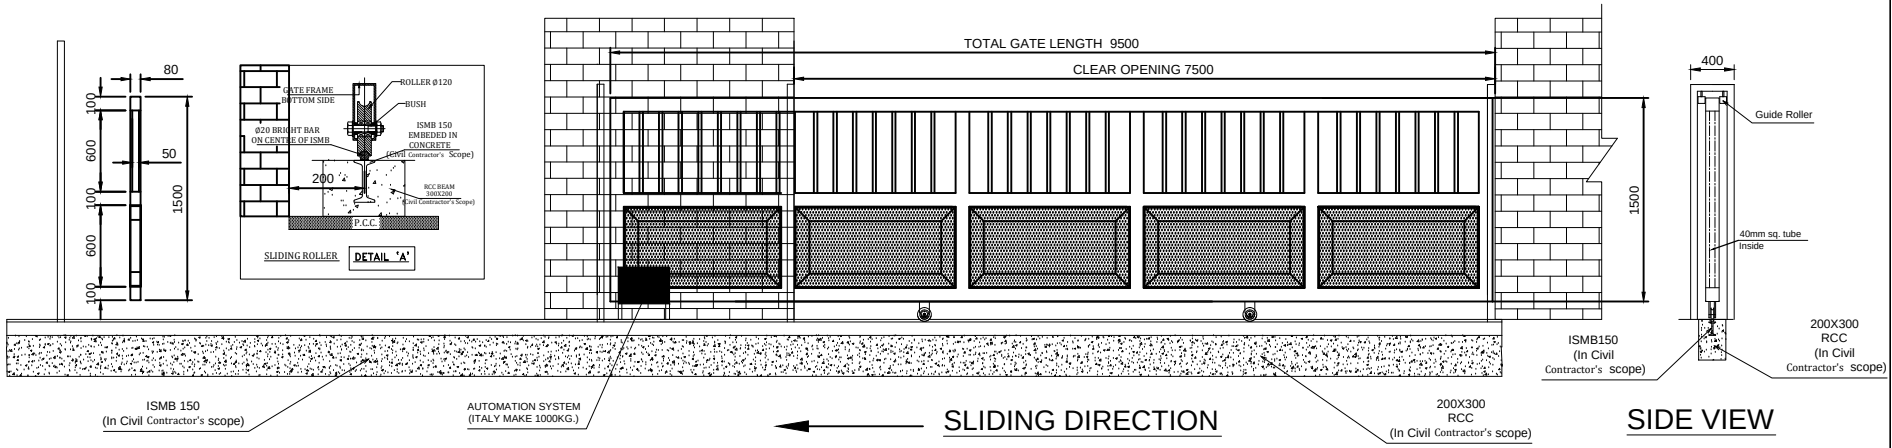


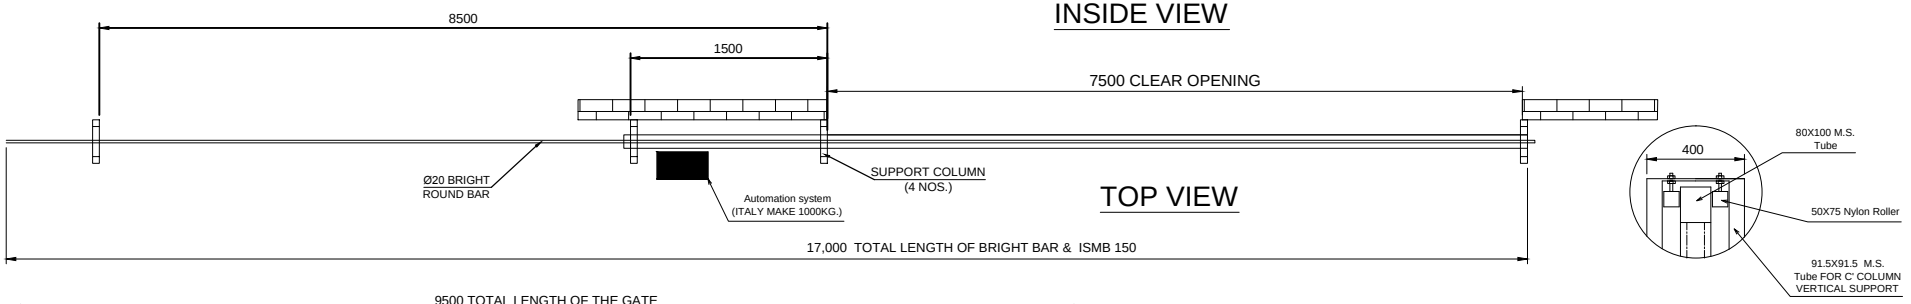

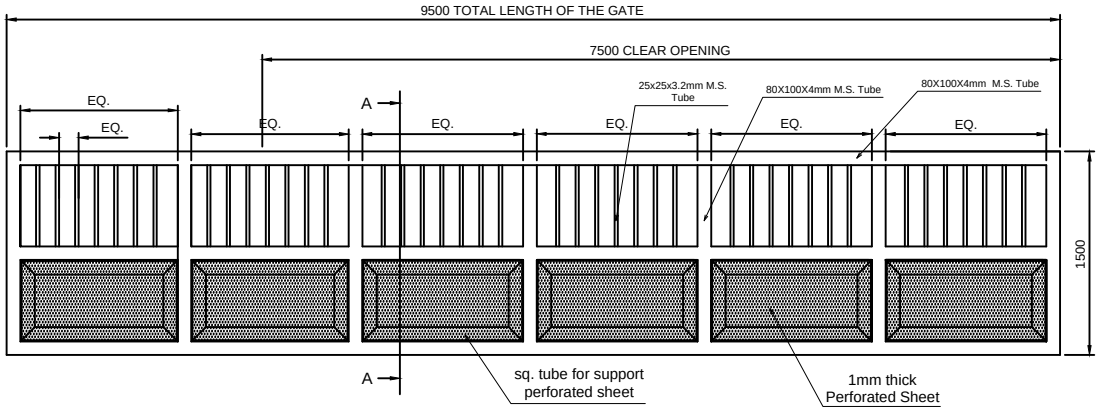

Clear Opening size - 7500X1500mm
Total length of gate - 9500X1500mm
No. Of Column - 4 nos.
Factory paint finish - Red oxide primer coat with Enamel paint Finish
NOTE :- *ALL REQ. CIVIL WORK WILL BE IN YOUR CONTRACTOR'S SCOPE.
NOTE:- As per calculation only 2 wheels are required for Motorized Sliding Gate.

☑ FINAL CERTIFIED

This drawing & designing is the property of NIHVA TECHNOLOGIES. Not be sold or copy to any other concern.

TITLE: MOTORIZED SLIDING GATE

	SIGN	DATE
DRAWN	ABHIJIT	05/11/15
CHECK	ANIL	05/11/15
REV.	04	
APPROVAL		

NIHVA TECHNOLOGIES PVT. LTD.
NIHVA TECHNOLOGY PVT. LTD. PUNE
Tel : 020 66304033
Email:- info@nihva.com
Website:- www.nihva.com

CLIENT - REWARD CONSTRUCTION
PROJECT - GIVAUDAN
SITE - RANJANGAON MIDC
DWG. NO. : NIHVA/15-16/106

If any queries contact : projects@nihva.com
SCALE: 01 | WT: | SHEET: 01 OF 01
ALL DIMENSION ARE IN mm