


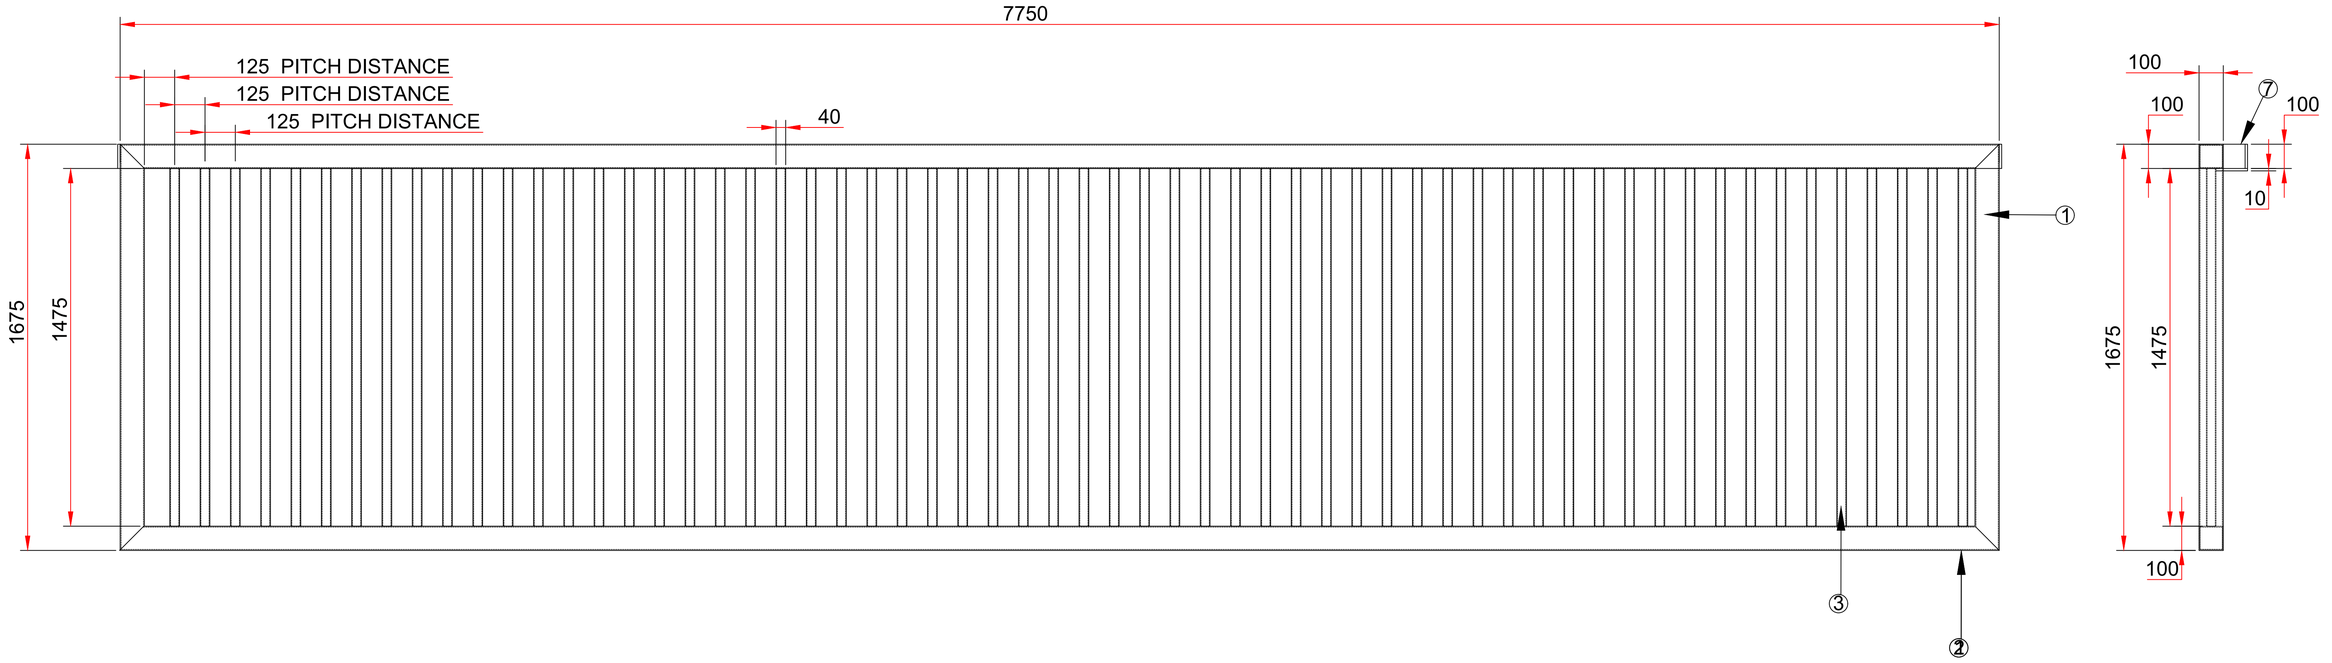

Note:-
1.All Dimension are in MM
2.Kindly Maintain the Given dimension

BOM FOR SINGLE LEAF			
SL NO.	DESCRIPTION	SPECIFICATION	QTY
1	MS SQ. TUBE	100X100X5X1675L	2NOS
2	MS SQ. TUBE	100X100X5X7750L	2NOS
3	MS SQ. TUBE	40X40X3.2X1475L	60NOS
4	MS FLAT	100 X 10 X 180L	2 NOS
5	MS FLAT	100 X 10 X 128L	10NOS
6	MS FLAT	100 X 10 X 6000L	1 NOS
7			

Rev No.	Revision	Date	Revised By

QTY- 01Nos

This drawing & design is the property of NIHVA TECHNOLOGIES. Not to be sold or copied to any other concern.

TITLE:-
MASTER LEAF TELE. SL. GATE

	NAME	DATE	SIGN
DRAWN	MAHESH S.	12/08/2022	
CHECK	MAHESH S.	12/08/2022	
APPRD.	AMIT K.	12/08/2022	

If any queries contact : design@nihva.com

ALL DIMENSION ARE IN mm

NIHVA
NIHVA TECHNOLOGIES PVT. LTD.

NIHVA TECHNOLOGIES PVT. LTD. PUNE
Tel : 020 66304033
Email:- info@nihva.com
Website:- www.nihva.com

CLIENT - NAVNEET EDUCATION LTD.
LOCATION - PALGHAR
PRODUCT - 3L-TELE. SL. GATE -16 MTR | QTY-00
DWG NO:- NIHVA/22-23/0060 | REV-00
SCALE: NTS | SCALE:-- 1:1 | SHEET: 01 OF 01