

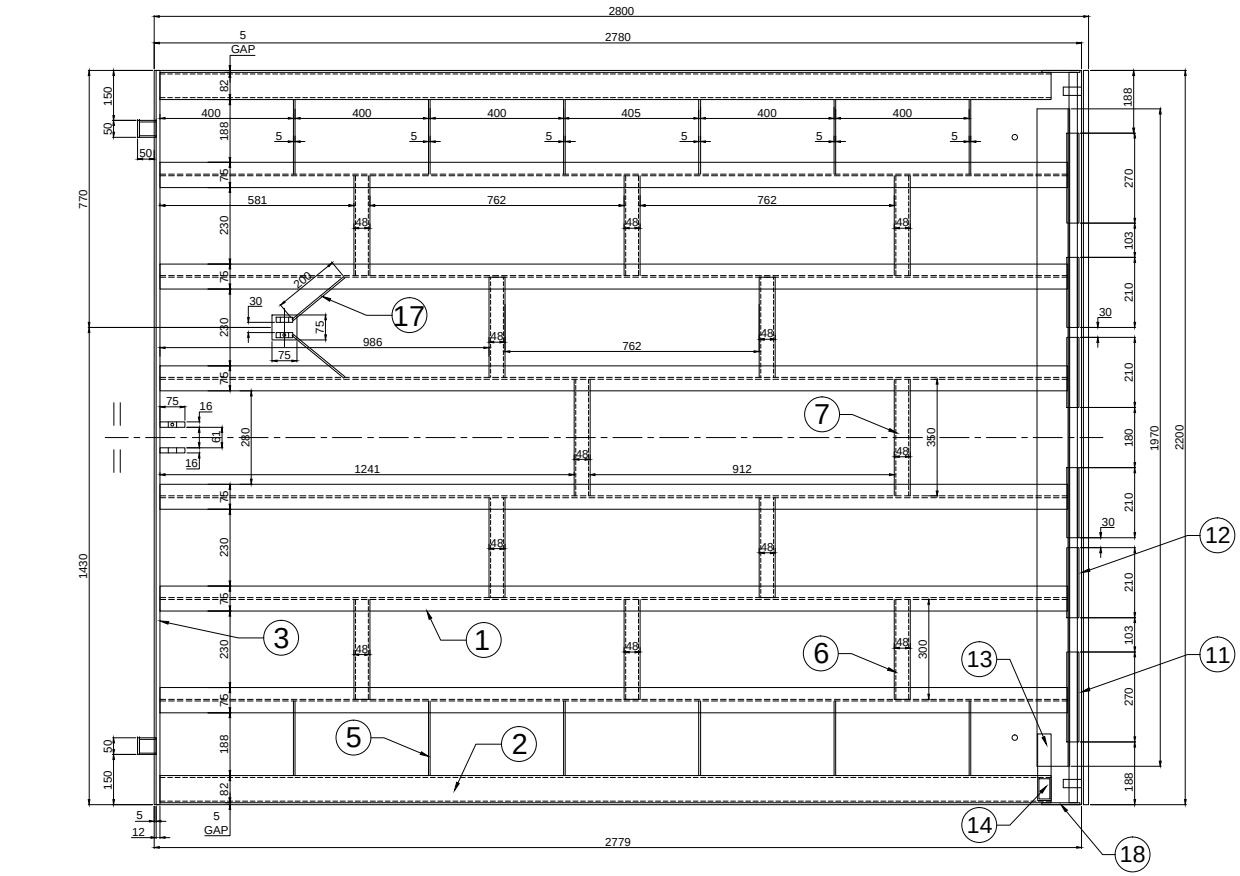


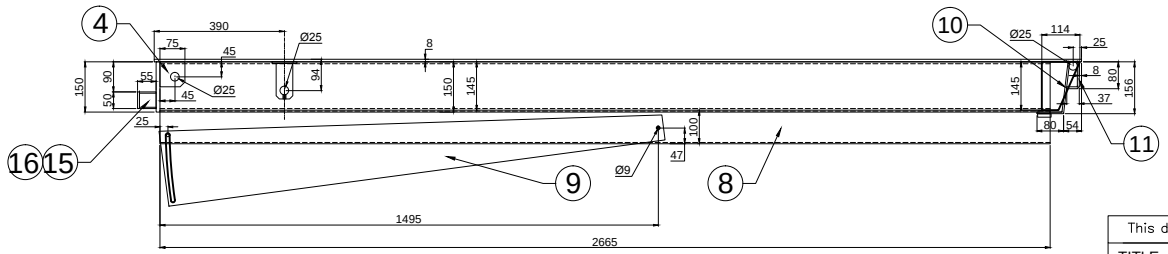

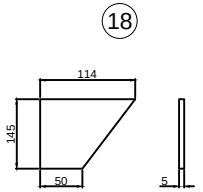

NOTE:~ MTL : MS

1. ISMC 150 X 75 X 2720L = 6 NOS (SEE DRG)
2. R.TUBE 145 X 82 X 5.4 X 2670L = 2 NOS
3. FLAT 150 X 12 X 2200L = 1 NO
4. FLAT 75 X 16 X 75L = 2 NOS (SEE DRG)
5. FLAT 150 X 6 X 222L = 12 NOS (NOTCH)
6. R.TUBE 96 X 48 X 300L = 10 NOS
7. R.TUBE 96 X 48 X 350L = 2 NOS
8. BEND 100 X 25 X 3 THK X 2665L = 2 NOS (SEE DRG)
9. SHEET 225 X 3 X 1500L = 2 NOS (SEE DRG)
10. BEND 156 X 5 THK X 1970L = 1 NOS (SEE DRG)
11. BEND 80 X 5 THK X 270L = 2 NOS (SEE DRG)
12. BEND 80 X 5 THK X 210L = 4 NOS (SEE DRG)
13. FLAT 40 X 10 X 200L = 2 NOS
14. FLAT 32 X 10 X 60L = 2 NOS (PACKING)
15. SQ.TUBE 50 X 50 X 3 X 50L = 2 NOS
16. FLAT 50 X 5 X 50L = 2 NOS
17. FLAT 75 X 5 X 200L = 2 NOS
18. SHEET 145 X 5 X 114L = 2 NOS (SEE DRG)

This drawing & design is the property of NIHVA TECHNOLOGIES. Not to be sold or copied to any other concern.

TITLE: DECK ASSLY			NIHVA TECHNOLOGIES PVT. LTD. PUNE Tel : 020 66304033 Email:- info@nihva.com Website:- www.nihva.com
NAME	SIGN	DATE	
DRAWN P.A			CLIENT -
CHECK SHEKHAR			PROJECT - DLBJ1001
APPRD. SHEKHAR			SITE LOCATION -
If any queries contact : design@nihva.com			DWG. NO. : NIHVA/17-18/ REV- 0
ALL DIMENSION ARE IN mm			SCALE: NTS WT: SHEET: 01 OF 01