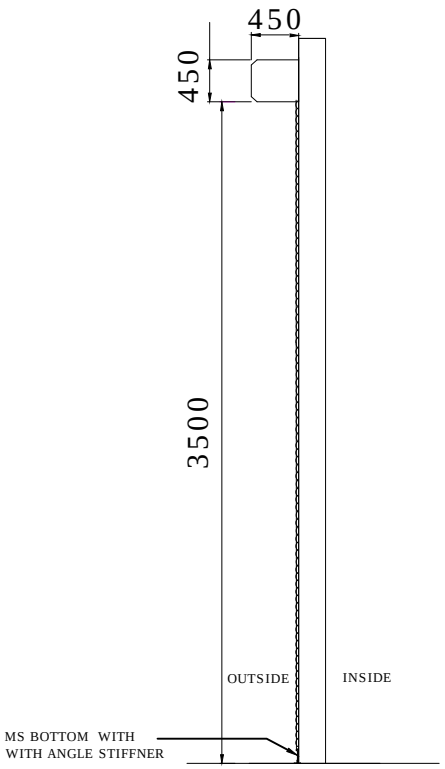

SIDE VIEW

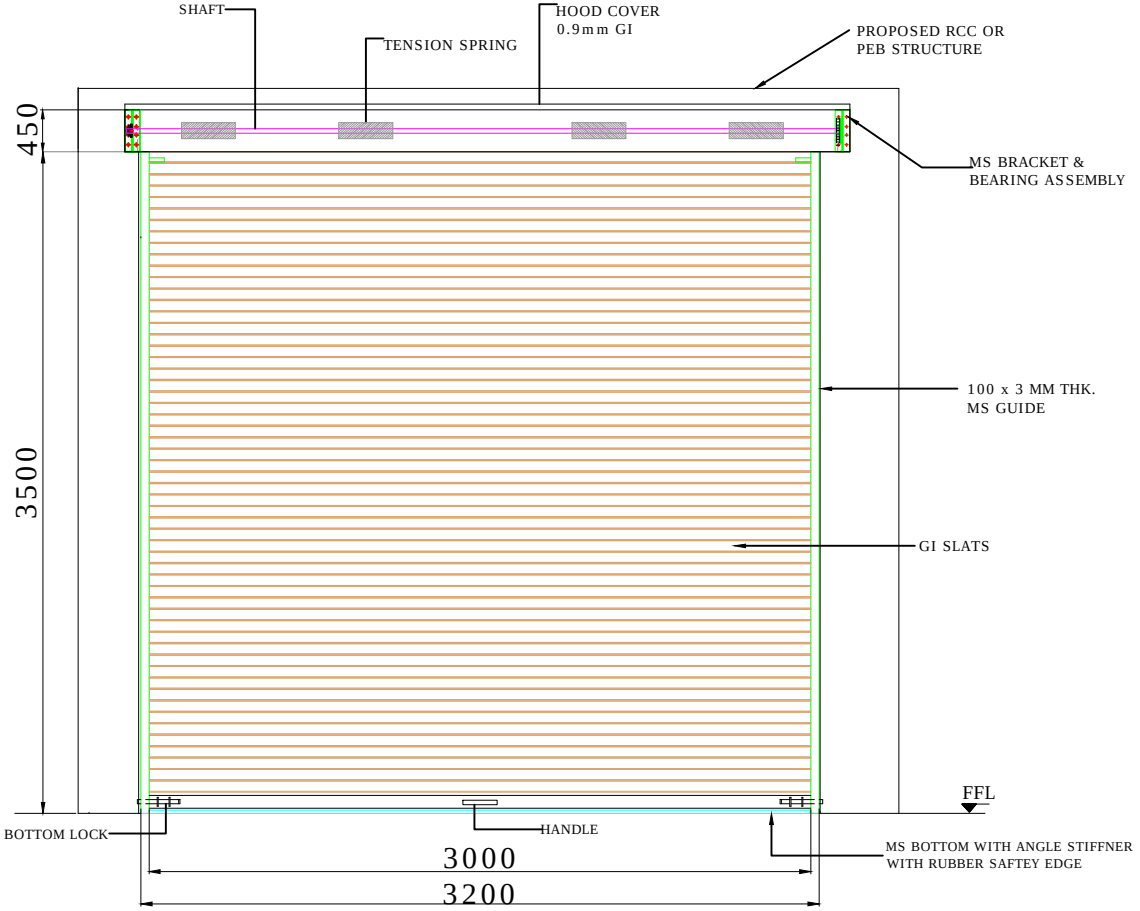

OUTSIDE ELEVATION

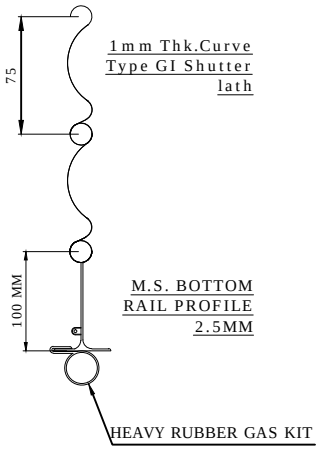

M.S. BOTTOM RAIL PROFILE 2.5MM

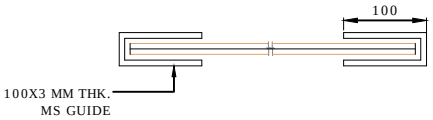

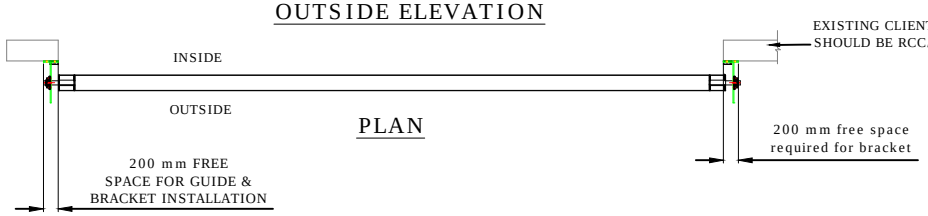

PLAN

NOTE:-
1. PAINTING WILL BE IN CLIENT'S SCOPE.
2. REQUIRED STRUCTURE WILL BE IN CLIENT SCOPE.

CLEAR WIDTH (CW)	CLEAR HEIGHT (CH)	QUANTITY
3000	3500	7

REV NO	DATE	DESCRIPTION
REV 0	18-11-2017	INITIAL DRAWING
REV 1	22-11-2017	GUIDE WIDTH CHANGED TO 100mm
REV 2	02-05-2018	SHUTTER MOUNTING WILL BE FROM OUTSIDE.

This drawing & designing is the property of NIHVA TECHNOLOGIES. Not to be sold or copied to any other concern.

TITLE
MANUAL ROLLING SHUTTER

	SIGN	DATE
DRAWN	OMKAR	18/11/17
CHECK	SHEKHAR	18/11/17
APPROVAL	SHEKHAR	18/11/17
MFG.		

If any queries contact : design@nihva.com

ALL DIMENSION ARE IN mm

NIHVA TECHNOLOGIES PVT. LTD.
NIHVA TECHNOLOGIES PVT. LTD. PUNE
Tel : 020 66304033
Email:- info@nihva.com
Website:- www.nihva.com

CLIENT - MITTAL PRECISION HITECH STEEL PVT.LTD

PROJECT -

SITE - CHAKAN,PUNE

DWG. NO. : NIHVA/17-18/0281/R02 | REV-2

SCALE: NTS | WT: | SHEET: 01 OF 01