
# MAINTENANCE STOPPER

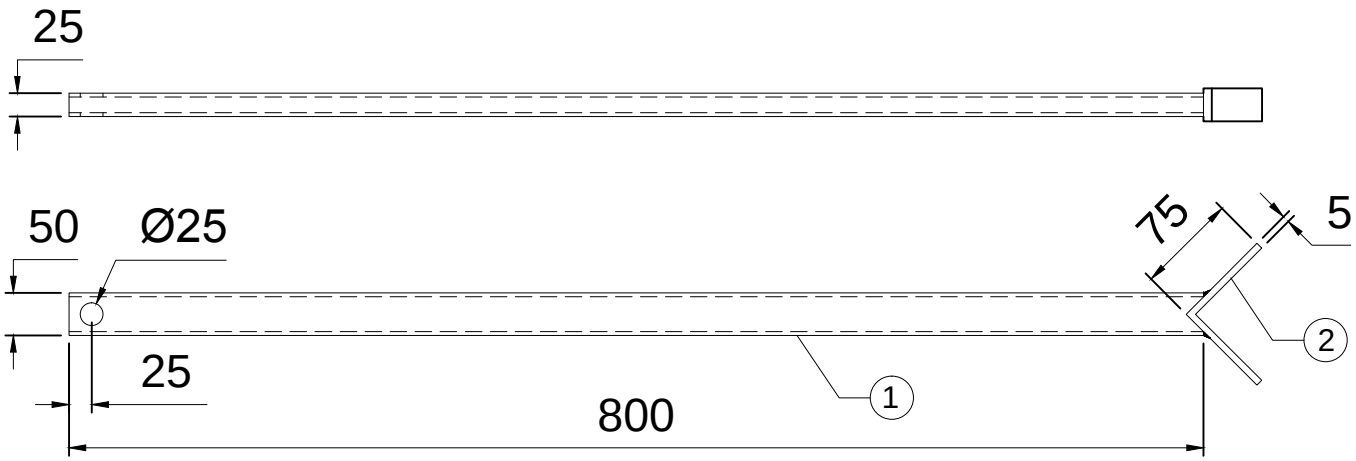


1. SQ .TUBE 50 X 25 X 3 THK X 800L = 2 NOS
2. ISA 75 X 75 X 5 X 35L = 2 NOS

TOLERANCE - ±5mm

This drawing & design is the property of NIHVA TECHNOLOGIES. Not to be sold or copied to any other concern.

| TITLE | | | | |
|---|---|---|---|---|
| MAINTENANCE STOPPER DRG | | | | NIHVA TECHNOLOGIES PVT. LTD. |
| | NAME | SIGN | DATE | |
| DRAWN | P.V.A | | 20.08.2020 | CLIENT - |
| CHECK | G.J | | 20.08.2020 | PROJECT - NDL_630_631 |
| APPRD. | | | | SITE LOCATION - |
| If any queries contact : design@nihva.com | | | | DWG. NO. : NIHVA/20-21/VDR/0054 |
| ALL DIMENSION ARE IN mm | | | | SCALE: NTS / WT: / REV- 0 |

NIHVA TECHNOLOGIES PVT. LTD. PUNE
Tel : 020 66304033
Email:- info@nihva.com
Website:- www.nihva.com