

GAME ZONE ROOF FABRICATION


PLAN

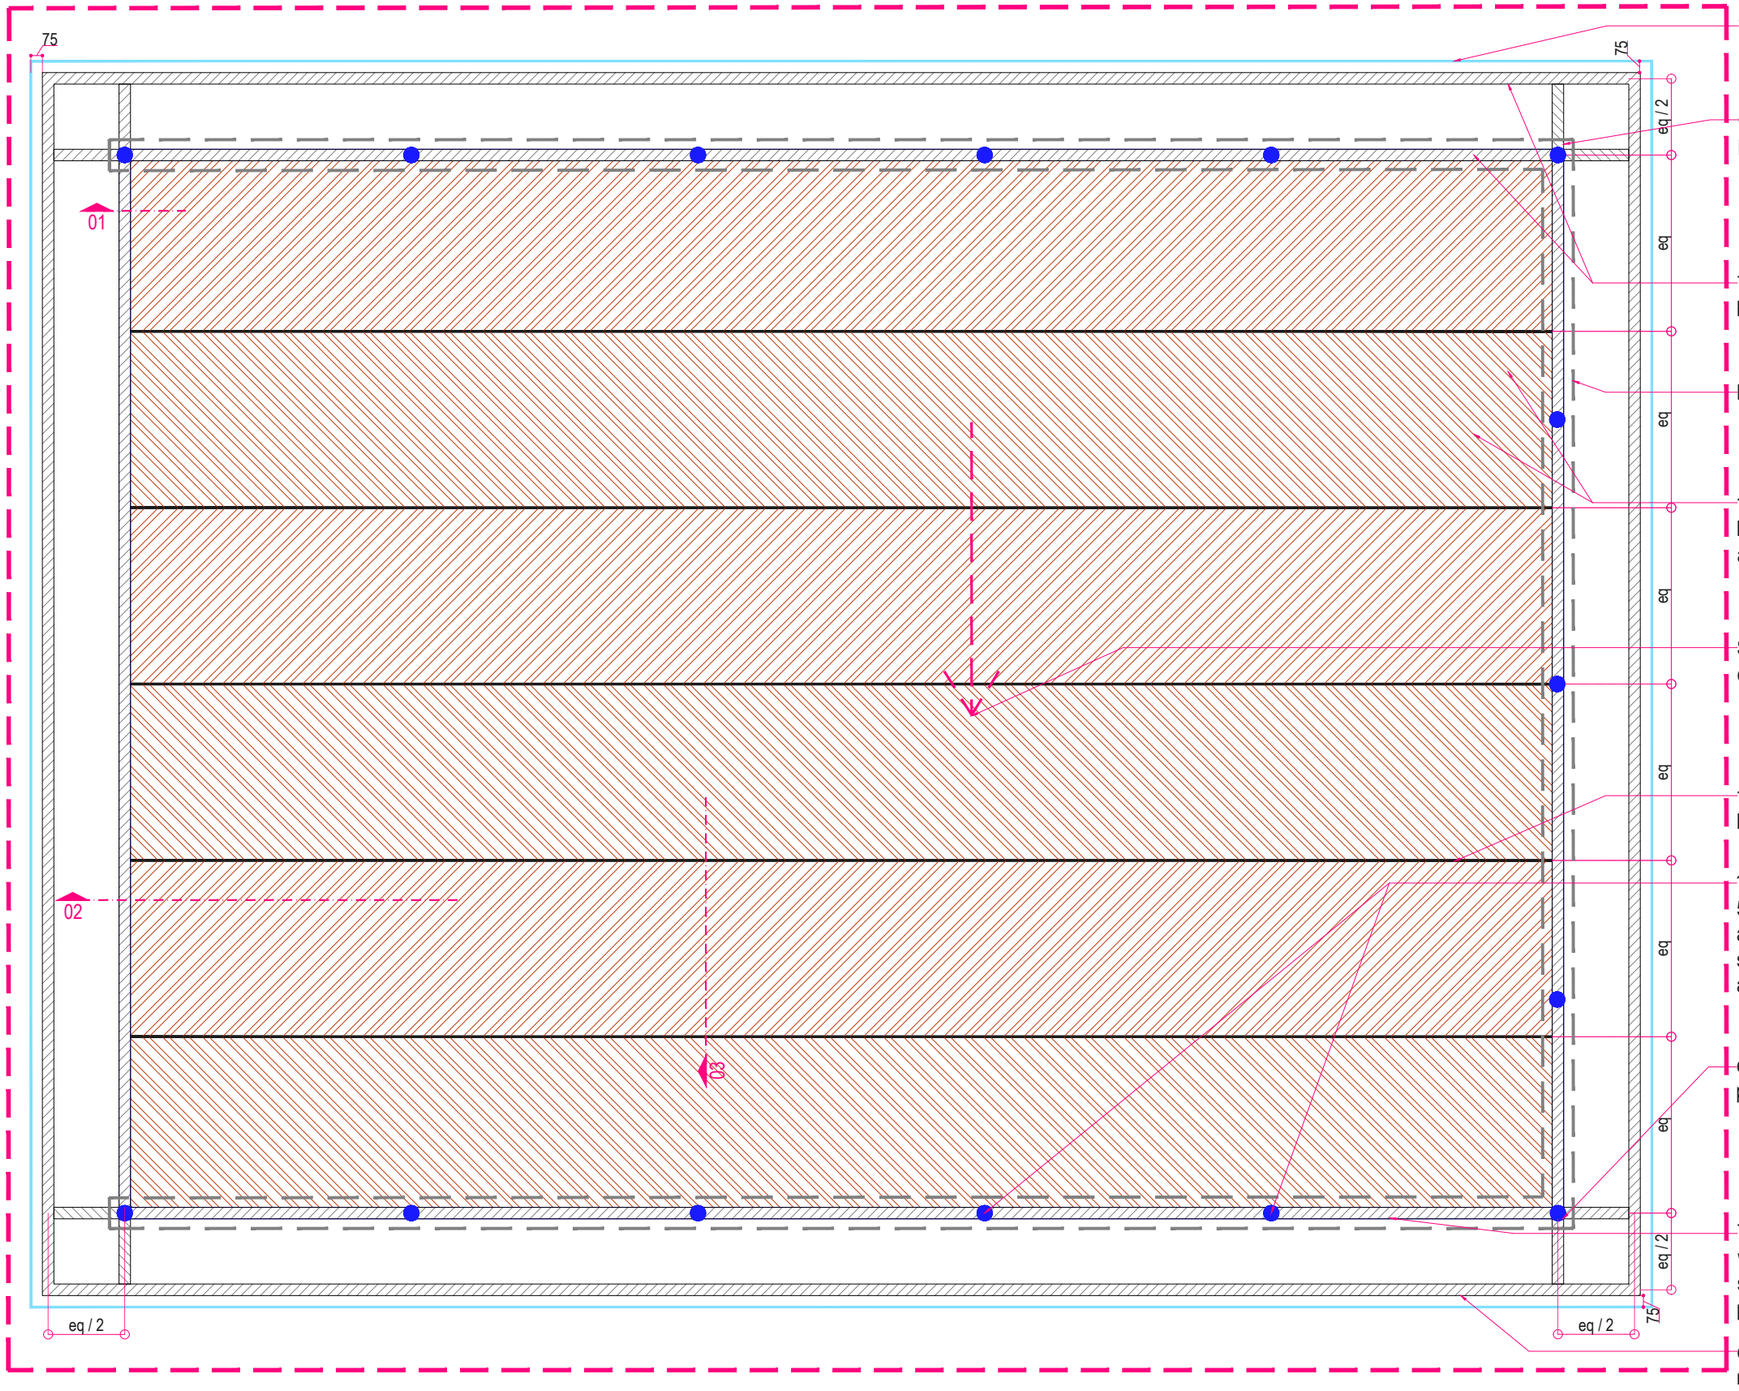


SECTION 1

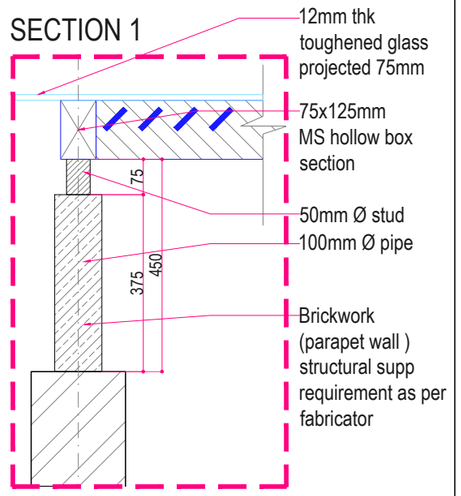


DETAIL

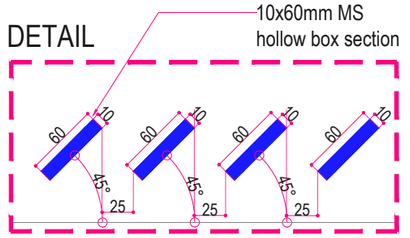

DETAIL

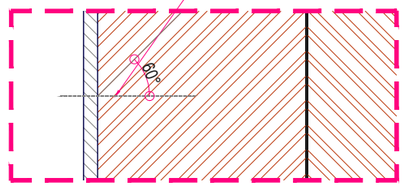


KEYPLAN

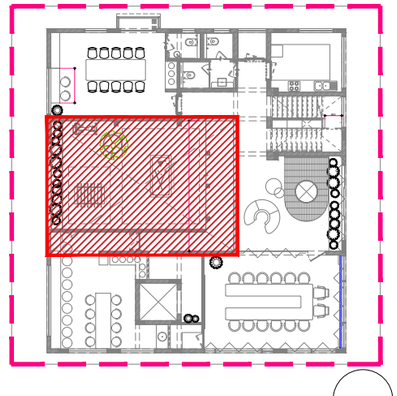

NOTE : Slope of the fabricated Roof has to be towards East for rainwater , slope to be done as per fabricator .
- All the fabrication sizes are indicative as per design and structurally they have to be done as per fabricator .

SECTION 2

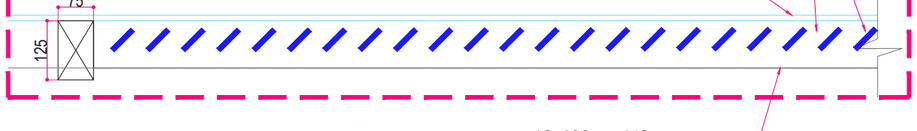

SECTION 3



REVISIONS:	NOS.
	REVISION DETAILS
DRAWING TITLE: Fabrication drawings	
DRAWING NOS:	ISSUED BY: Nagashree
	CHECKED BY: Devica
SCALE : NTS	GFC
DATE : 08.07.2024	
Architectural Design:	studio anagami
CLIENT:	Sanjeevini Builders.
PROJECT TITLE : OFFICE FOR SANJEEVINI BUILDERS	
LANDSCAPE	
STRUCURE	
MEP	
ELECTRICAL	Kiran

GENERAL NOTES:
- THIS DRAWING IS TO BE READ IN CONJUNCTION WITH THE RELEVANT SPECIFICATION & CONDITIONS OF CONTRACT.
- ALL DIMENSIONS ARE ONLY TO BE READ & NOT MEASURED OR SCALED. ALL DIMENSIONS ARE TO BE VERIFIED BY CONTRACTOR & ANY DISCREPANCIES SHALL BE BROUGHT TO PMC & ARCHITECT'S NOTICE IMMEDIATELY.
- ALL LEVELS INDICATED IN THIS DRAWING ARE FINISHED LEVELS UNLESS EXPRESSLY SPECIFIED.
- THIS DRAWING UNLESS SIGNED GOOD FOR CONSTRUCTION BY AGENCIES CONCERNED SHALL NOT BE USED FOR ANY SITE WORKS.
- ANY & ALL INFORMATION IN THIS DRAWING IS SUBJECT TO DUE VERIFICATION & ACCEPTANCE BY PMC/CLIENT. DISCREPANCIES IF ANY SHALL BE BROUGHT TO NOTICE IMMEDIATELY.

SPECIFIC NOTES:
- ALL DIMENSIONS ARE IN MM.