


SCISSOR LIFT SIZE	WIDTH (W)	LENGTH (L)	HEIGHT (H)	LIP (C) LENGTH
	2000	2500	500	400

PIT DIMENSION	WIDTH (W 1)	LENGTH (L 1)	DEPTH (D)	ALL DIMENSIONS ARE IN mm
	2050	2550	505	

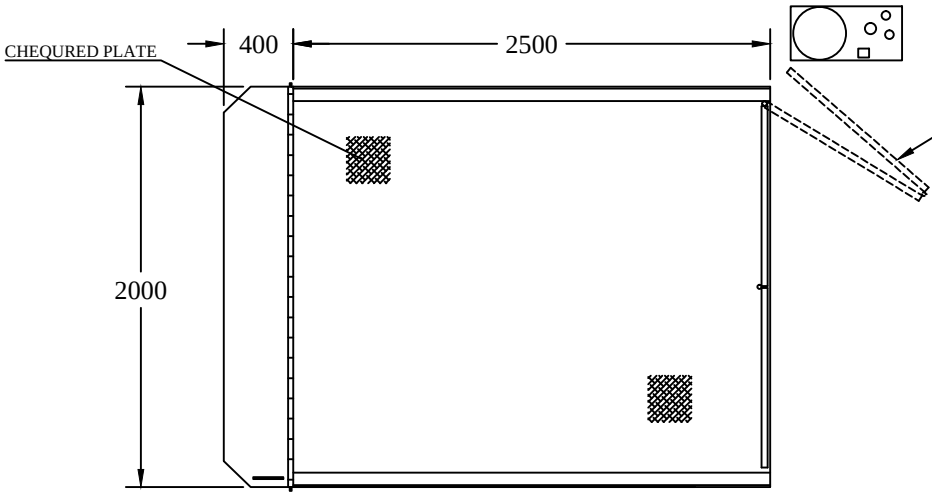

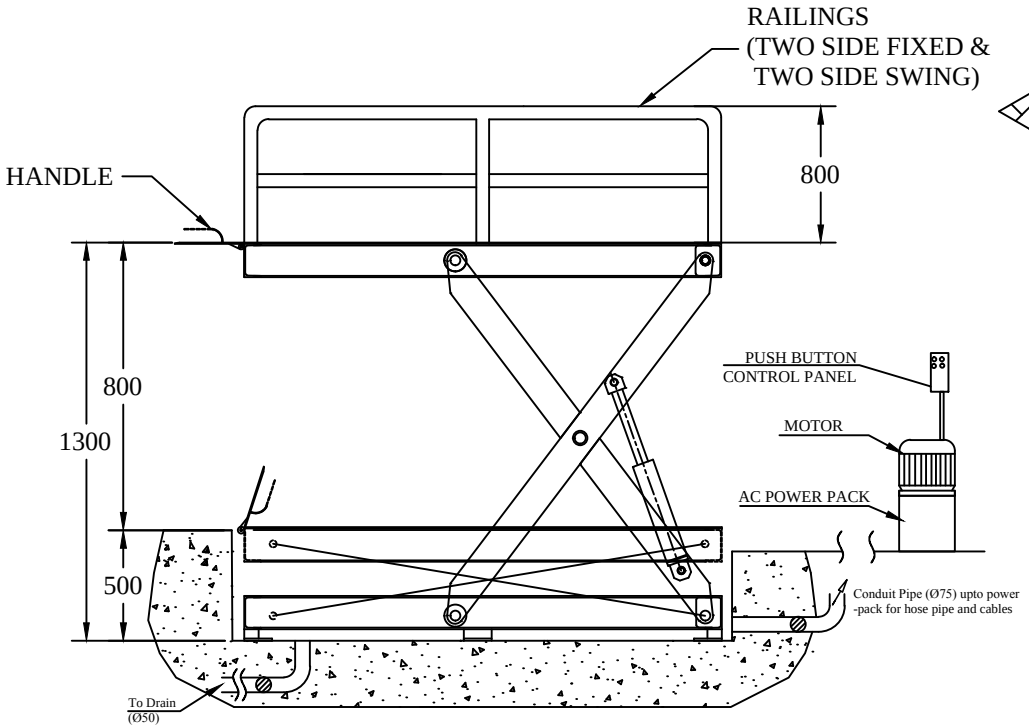

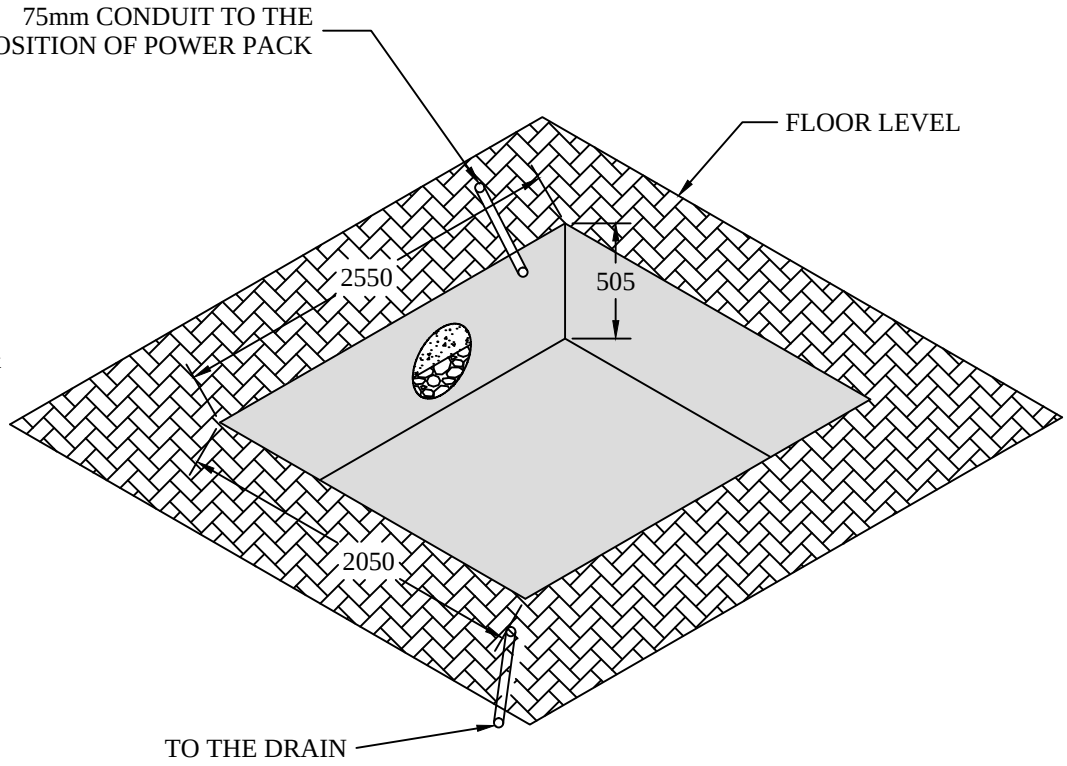

PIT DRAWING

SCISSOR LIFT- 1500KG CAPACITY

REVISION 1- ONE SIDE OPENABLE RAILING WILL BE PROVIDED AS OTHER SIDE PROTECTED BY LIP RESTING UPWARD.

This drawing & designing is the property of NIHVA TECHNOLOGIES. Not be sold or copy to any other concern.

TITLE: SCISSOR LIFT

NIHVA TECHNOLOGIES PVT. LTD.
NIHVA TECHNOLOGY PVT. LTD. PUNE
Tel : 020 66304033
Email:- info@nihva.com
Website:- www.nihva.com

	SIGN	DATE
DRAWN	OMKAR	10/12/16
CHECK	SAGAR P.	10/12/16
REV.	0	
APPROVAL		

CLIENT - EMCURE PHARMACEUTICALS
PROJECT -
SITE - SANAND, GUJRAT
DWG. NO. : NIHVA/16-17/0094/R01
If any queries contact : projects@nihva.com
SCALE: NTS | WT: | SHEET: 01 OF 01
ALL DIMENSION ARE IN mm