




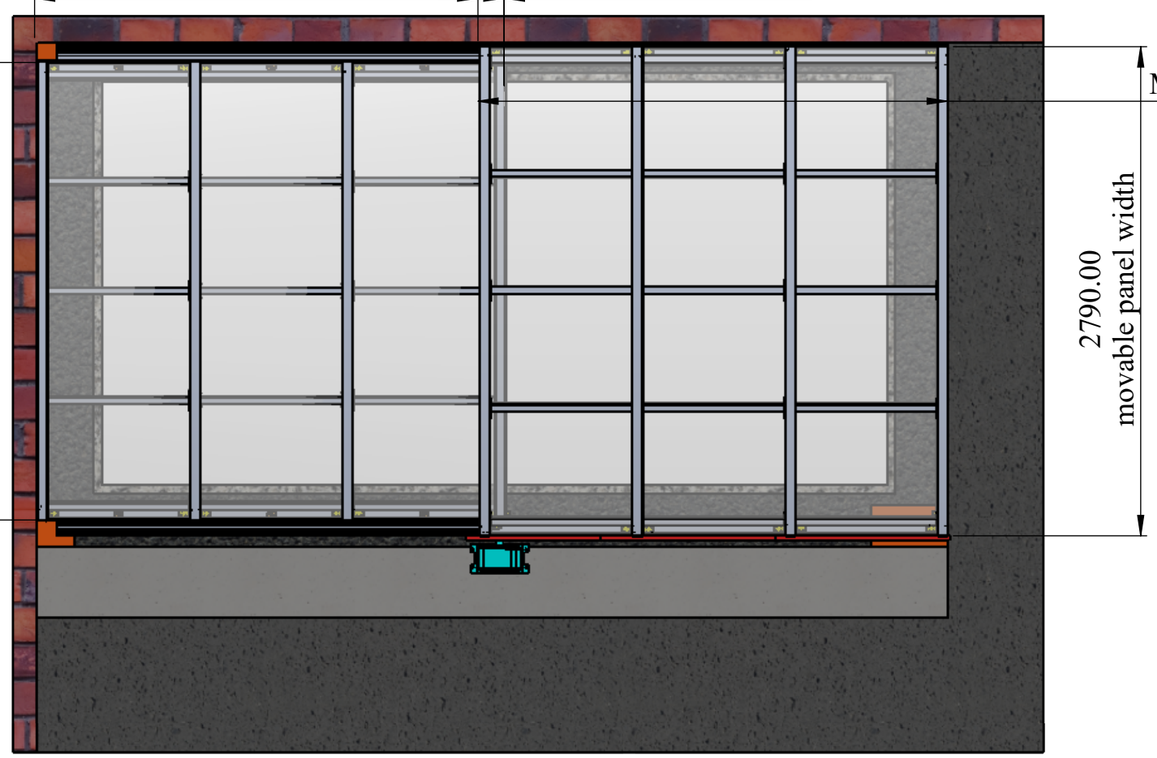


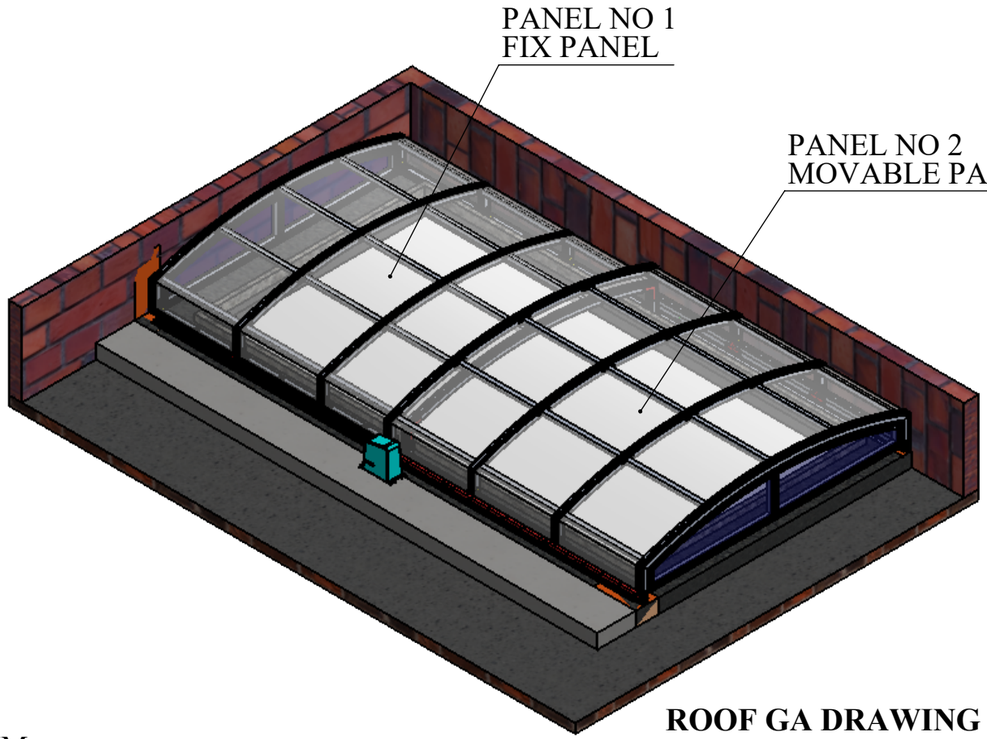

ROOF GA DRAWING

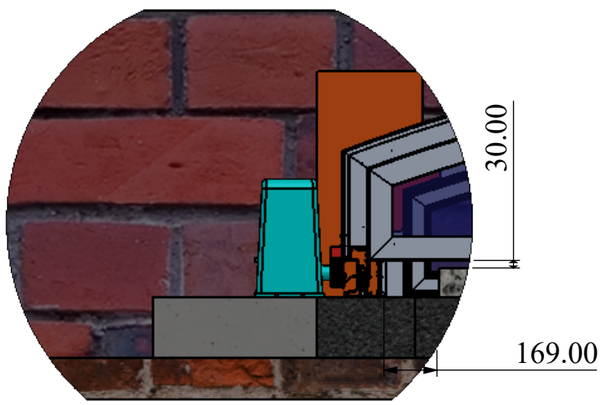


DETAIL A
SCALE 1 : 15

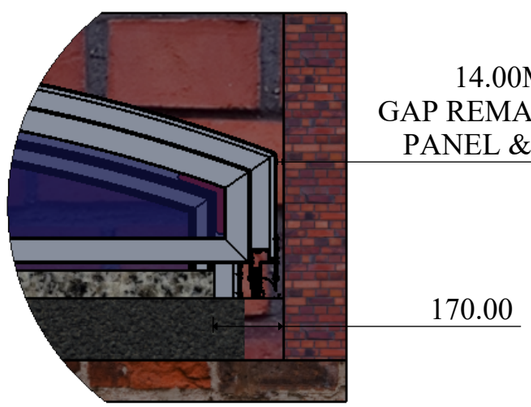



DETAIL B
SCALE 1 : 15

NOTE :
OPENING 2117MM WILL BE AVAILABLE

TITLE - ROOF AUTOMATION				NIHVA TECHNOLOGIES PVT.LTD.PUNE	
DWG NO - NTPL-283-PM-001-00-00-00				Website - www.nihva.com	
	NAME	SIGNATURE	DATE	PROJECT NO - NTPL-283-PM	
DRAWN	V.W		20-06-2025	PRODUCT - RETRACTABLE ROOF	WEIGHT -
CHK'D	S.W.		24-06-2025	SITE LOCATION - LUCKNOW	REVISION - 01
APPV'D	V.T.		24-06-2025	MATRIAL SPECIFICATION-	QTY - 1
if any queries contact - supportautomation@nihva.com				PROJECTION METHOD:	SCALE :
ALL DIMENSION ARE IN mm			A3		SHEET 1 OF 25

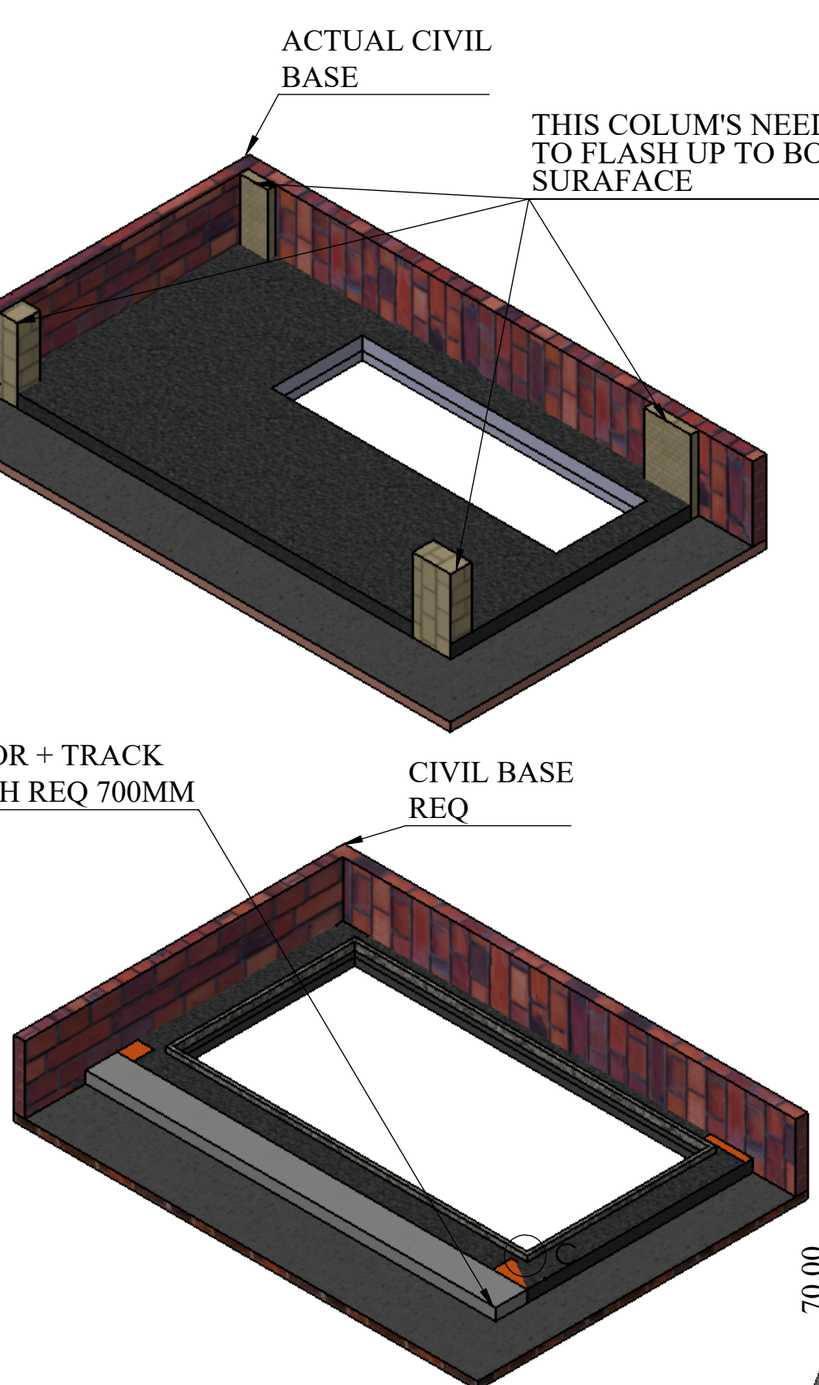

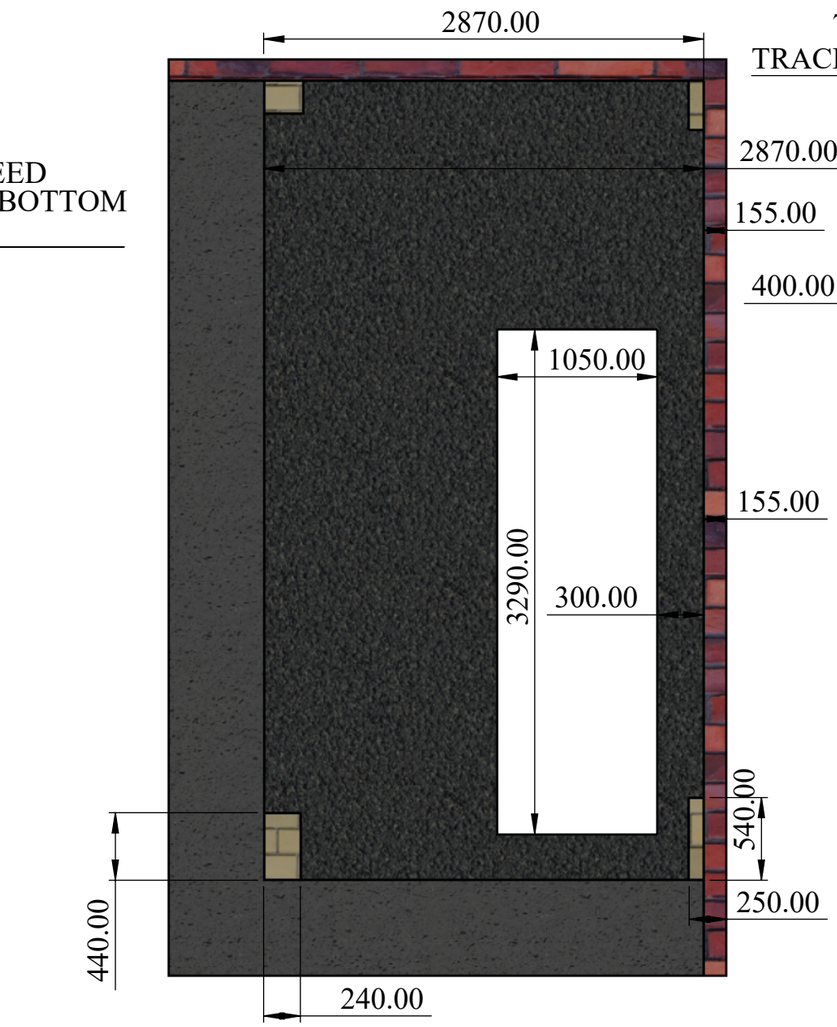

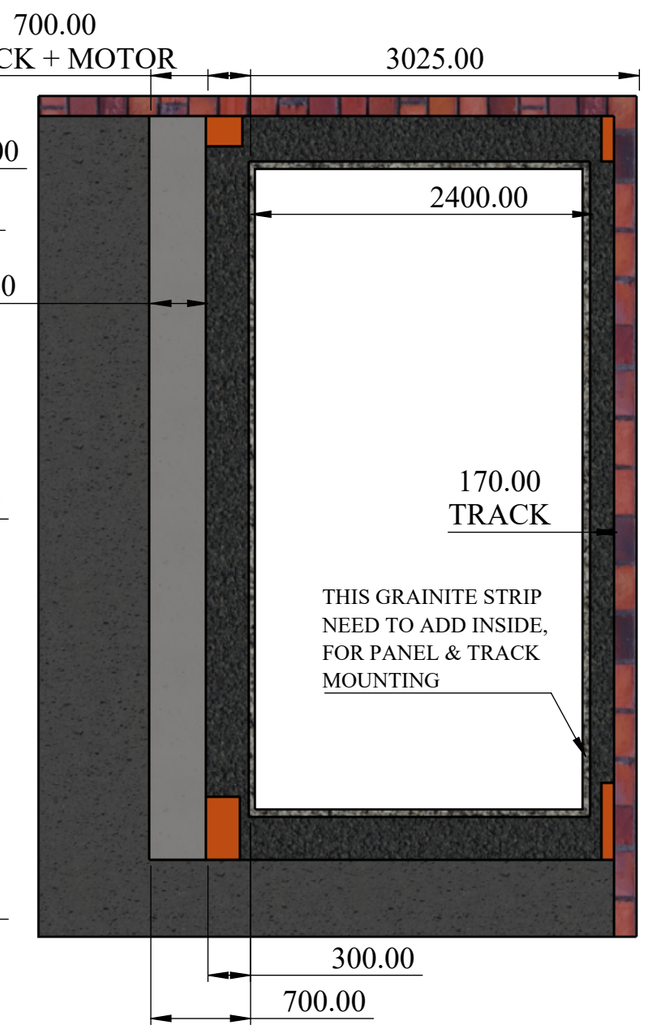




ACTUAL CIVIL
BASE



CIVIL BASE
REQ

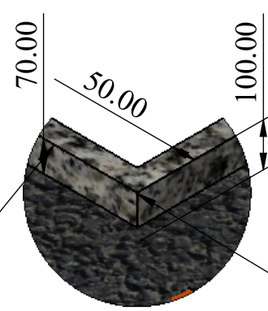


GRANITE STRIP
100*50MM

DETAIL C
SCALE 1 : 10

CIVIL DRAWING

TITLE - ROOF AUTOMATION				NIHVA TECHNOLOGIES PVT.LTD.PUNE	
DWG NO - NTPL-283-PM-001-00-00-00				Website - www.nihva.com	
	NAME	SIGNATURE	DATE	PROJECT NO - NTPL-283-PM	
DRAWN	V.W		20-06-2025	PRODUCT - RETRACTABLE ROOF	WEIGHT -
CHK'D	S.W.		24-06-2025	SITE LOCATION - LUCKNOW	REVISION -01
APPV'D	V.T.		24-06-2025	MATRIAL SPECIFICATION-	QTY - 1
if any queries contact - supportautomation@nihva.com				PROJECTION METHOD:	SCALE :
ALL DIMENSION ARE IN mm			A3		SHEET 2 OF 25

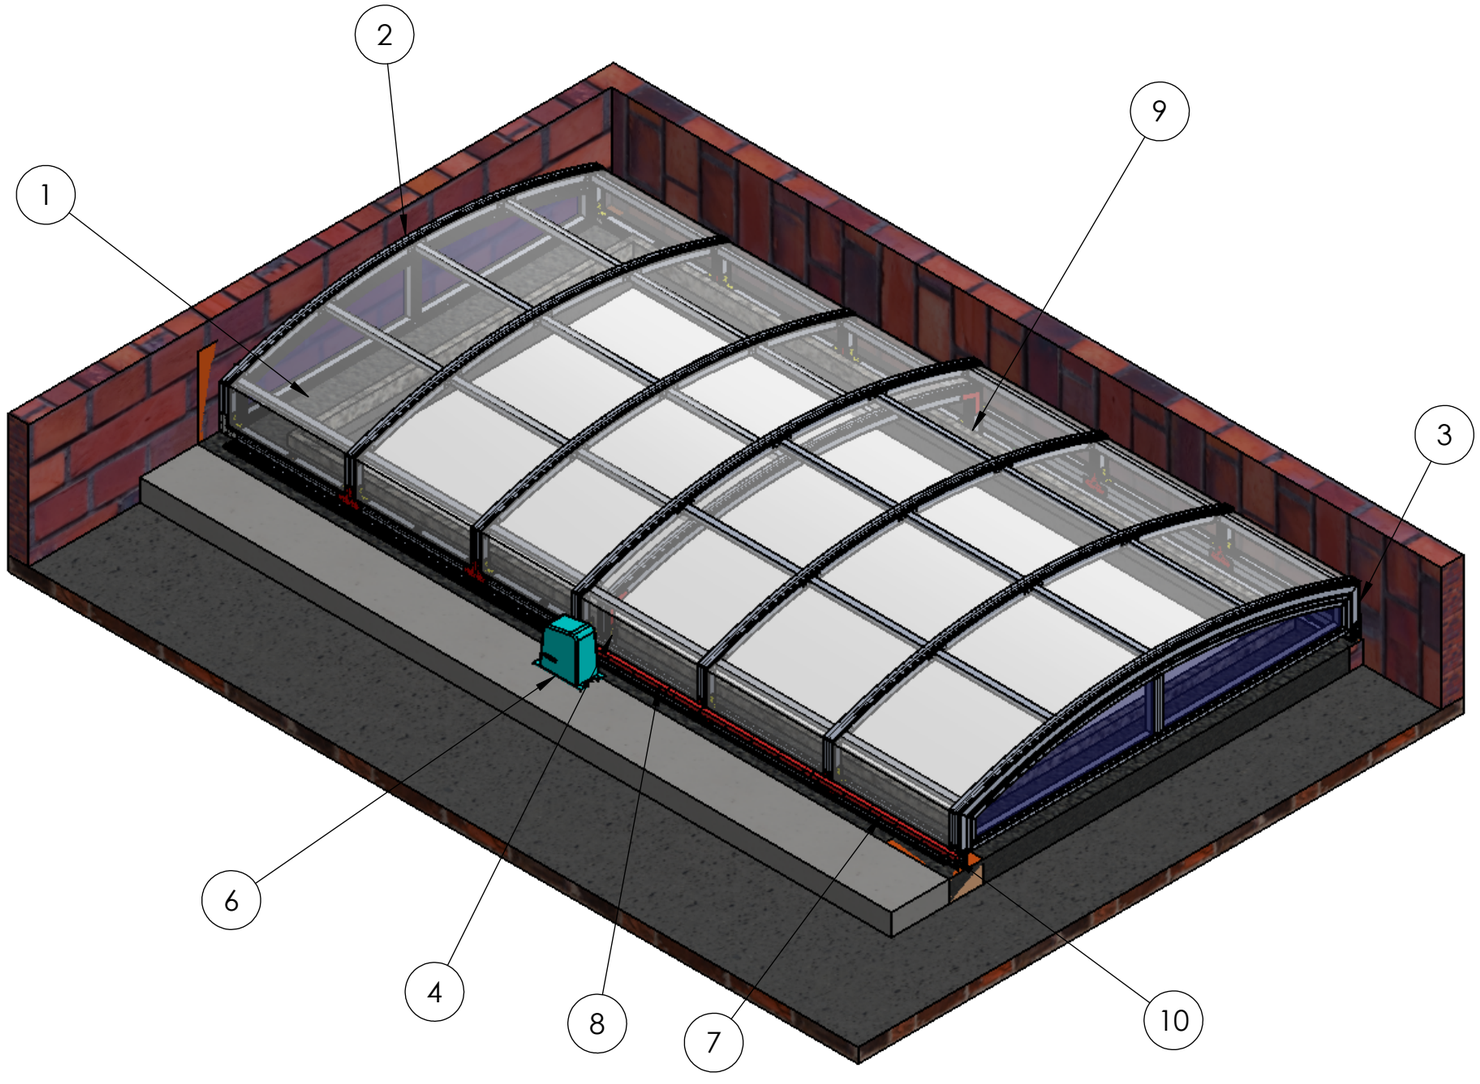

ITEM NO.	PART NUMBER	DESCRIPTION	QTY.
1	AS PER REQACTUAL CIVIL BASE		1
2	PANEL NO 1 FIX PANEL ASM		1
3	MOVABLE PANEL NO 2 ASM		1
4	NYLON STOPPER		2
5	IS 2269 - M6 x 40-N		4
6	RR_NICE RB 600		1
7	RR_RACK	STD (M4 RACK, 30x8x1000 mm, ZINC COATED WITH SPACERS AND SCREWS.)	2
8	RR_RACK	STD (M4 RACK, 30x8x1000 mm, ZINC COATED WITH SPACERS AND SCREWS.)	1
9	Track gnt 001		1
10	GNT001 TRACK 1		1

TITLE - ROOF AUTOMATION

DWG NO - NTPL-283-PM-001-00-00-00

NIHVA Technologies Pvt. Ltd.

NIHVA TECHNOLOGIES PVT.LTD.PUNE

Website - www.nihva.com

	NAME	SIGNATURE	DATE
DRAWN	V.W		20-06-2025
CHK'D	S.W.		24-06-2025
APPV'D	V.T.		24-06-2025

PROJECT NO - NTPL-283-PM

PRODUCT - RETRACTABLE ROOF | WEIGHT -

SITE LOCATION - LUCKNOW | REVISION - 01

MATRIAL SPECIFICATION- | QTY - 1


if any queries contact - supportautomation@nihva.com

ALL DIMENSION ARE IN mm | A3


PROJECTION METHOD:


SCALE :



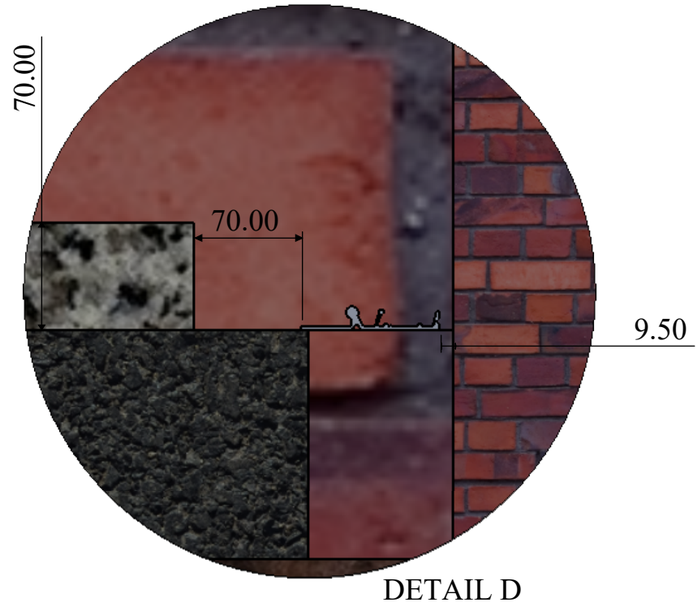

DETAIL D
SCALE 1 : 4

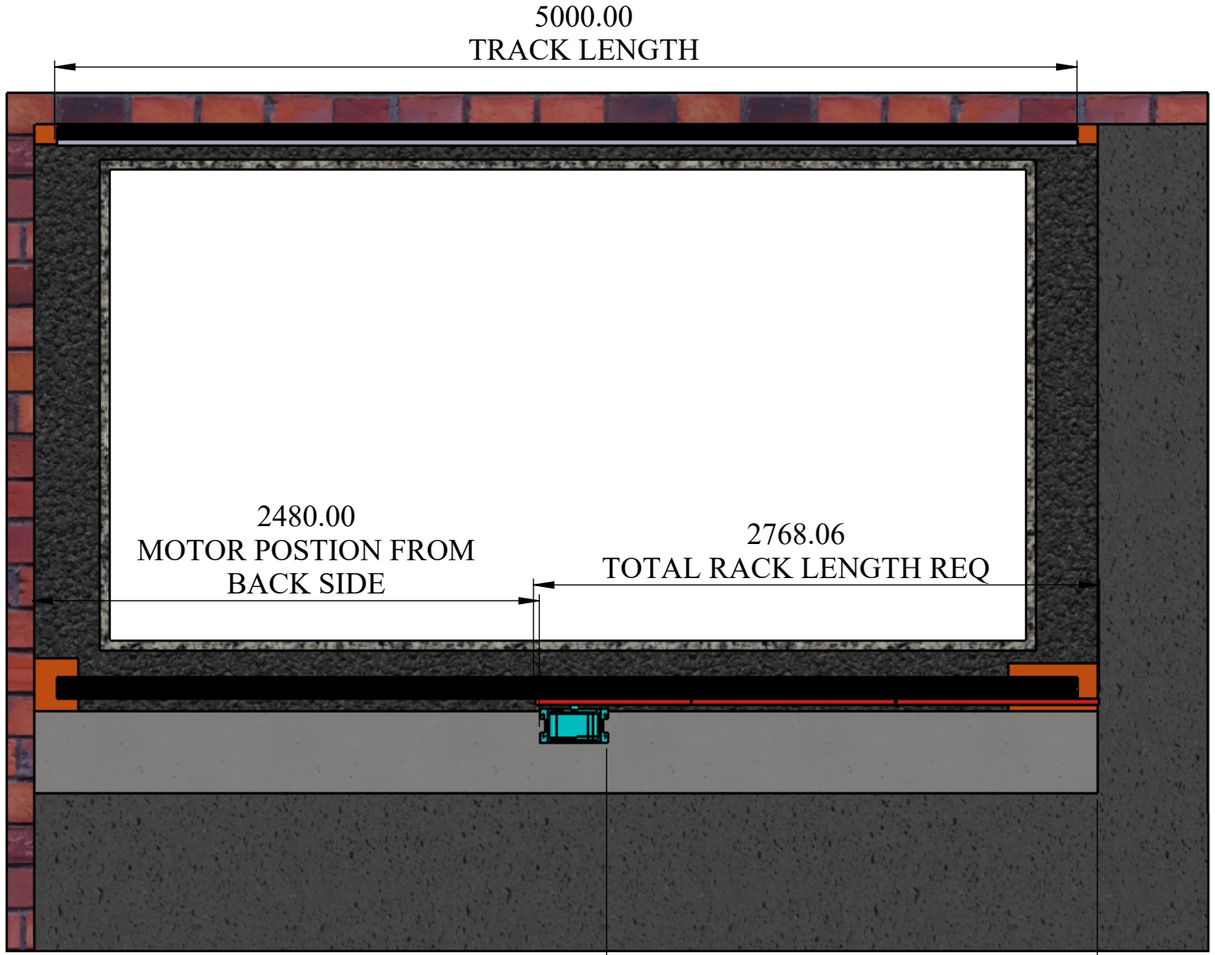


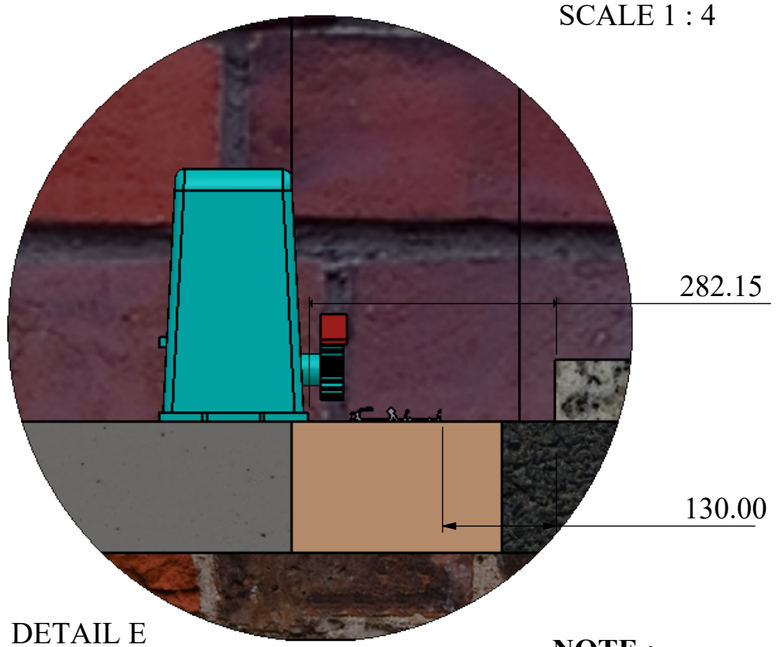


DETAIL E
SCALE 1 : 7


NOTE :
TRACK ASSEMBLY

TITLE - ROOF AUTOMATION				NIHVA TECHNOLOGIES PVT.LTD.PUNE	
DWG NO - NTPL-283-PM-001-00-00-00				Website - www.nihva.com	
	NAME	SIGNATURE	DATE	PROJECT NO - NTPL-283-PM	
DRAWN	V.W		20-06-2025	PRODUCT - RETRACTABLE ROOF	WEIGHT -
CHK'D	S.W.		24-06-2025	SITE LOCATION - LUCKNOW	REVISION - 01
APPV'D	V.T.		24-06-2025	MATRIAL SPECIFICATION-	QTY - 1
if any queries contact - supportautomation@nihva.com				PROJECTION METHOD:	SCALE :
ALL DIMENSION ARE IN mm			A3		SHEET 4 OF 25

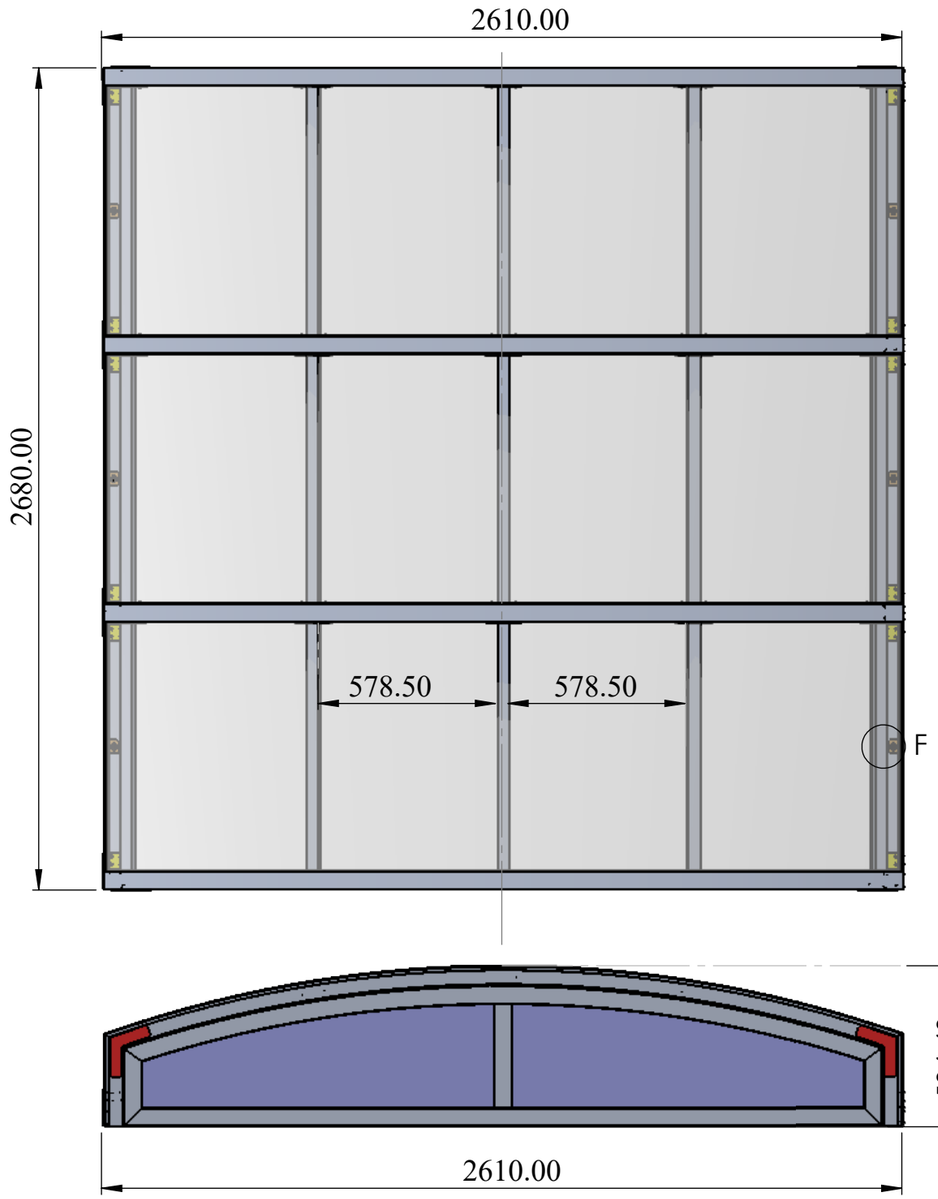


ITEM NO.	PART NAME	DESCRIPTION/ PART NUMBER	QTY.
1	PANEL NO 01 FIX PANEL		1
2	T PLATE ASM		8
3	L PLATE ASM		7
4	L ANGLE PLATE ASM		12
5	L ANGLE WELDING CORNER JOINING PLATE	AL JOINING PLATE	4
6	PANEL NO 01 FIX PANEL POLYCARBONET SHEET		3
7	PANEL NO 01 FIX PANEL ENCLOSER		1
8	SQ TUBE 40X40X2 MM THK 813.33 LONG ASM		15
9	ANCHOR FASTENING PLATE	MS - 45X32X4 MM THK	6
10	RR_ Anchor Bolt M10x100	STD	6

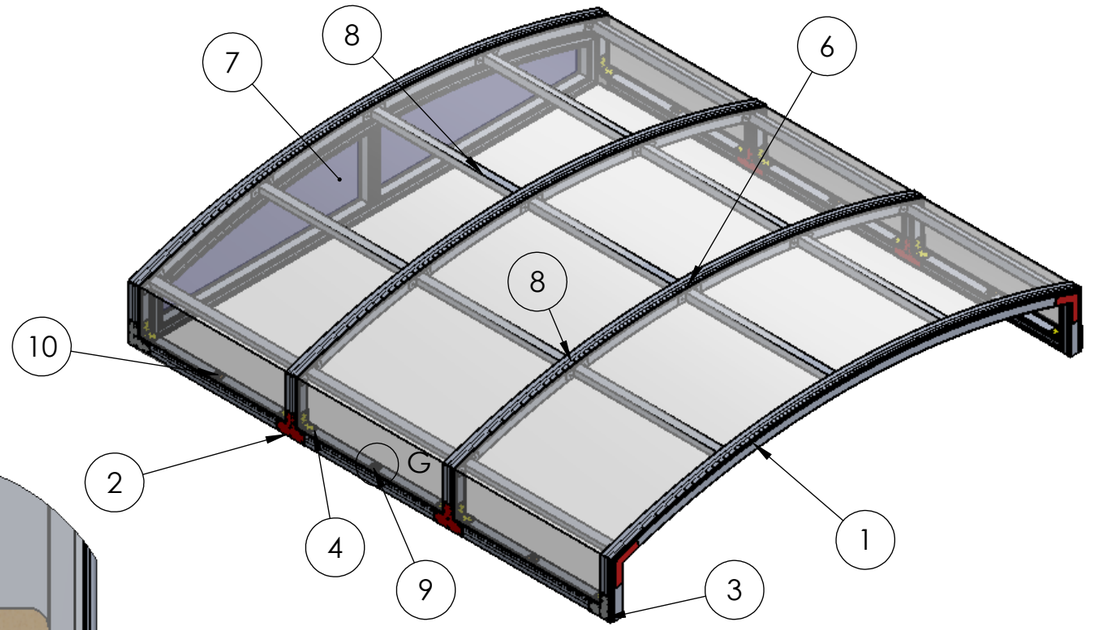

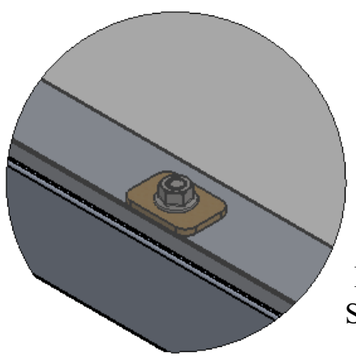

DETAIL G
SCALE 1 : 3


NOTE :
FIX PANEL ASSEMBLY

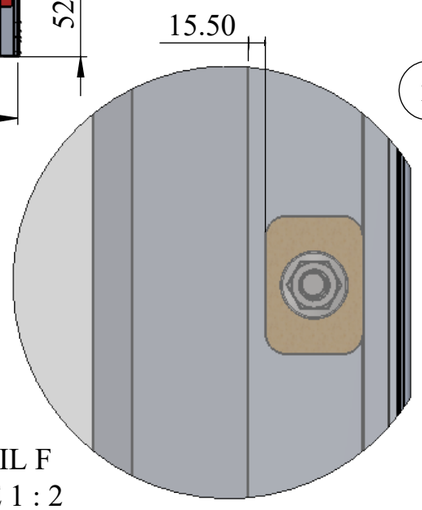


DETAIL F
SCALE 1 : 2


TITLE - ROOF AUTOMATION				NIHVA TECHNOLOGIES PVT.LTD.PUNE	
DWG NO - NTPL-283-PM-001-01-00-00				Website - www.nihva.com	
	NAME	SIGNATURE	DATE	PROJECT NO - NTPL-283-PM	
DRAWN	V.W		20-06-2025	PRODUCT - RETRACTABLE ROOF	WEIGHT - 233.442 KG
CHK'D	S.W.		24-06-2025	SITE LOCATION - LUCKNOW	REVISION - 01
APPV'D	V.T.		24-06-2025	MATRIAL SPECIFICATION-	QTY - 1
if any queries contact - supportautomation@nihva.com				PROJECTION METHOD:	SCALE :
ALL DIMENSION ARE IN mm			A3		SHEET 5 OF 25

``	PART NAME	DESCRIPTION / PART NUMBER	QTY.
1	PANEL NO 01 FIX PANEL		1

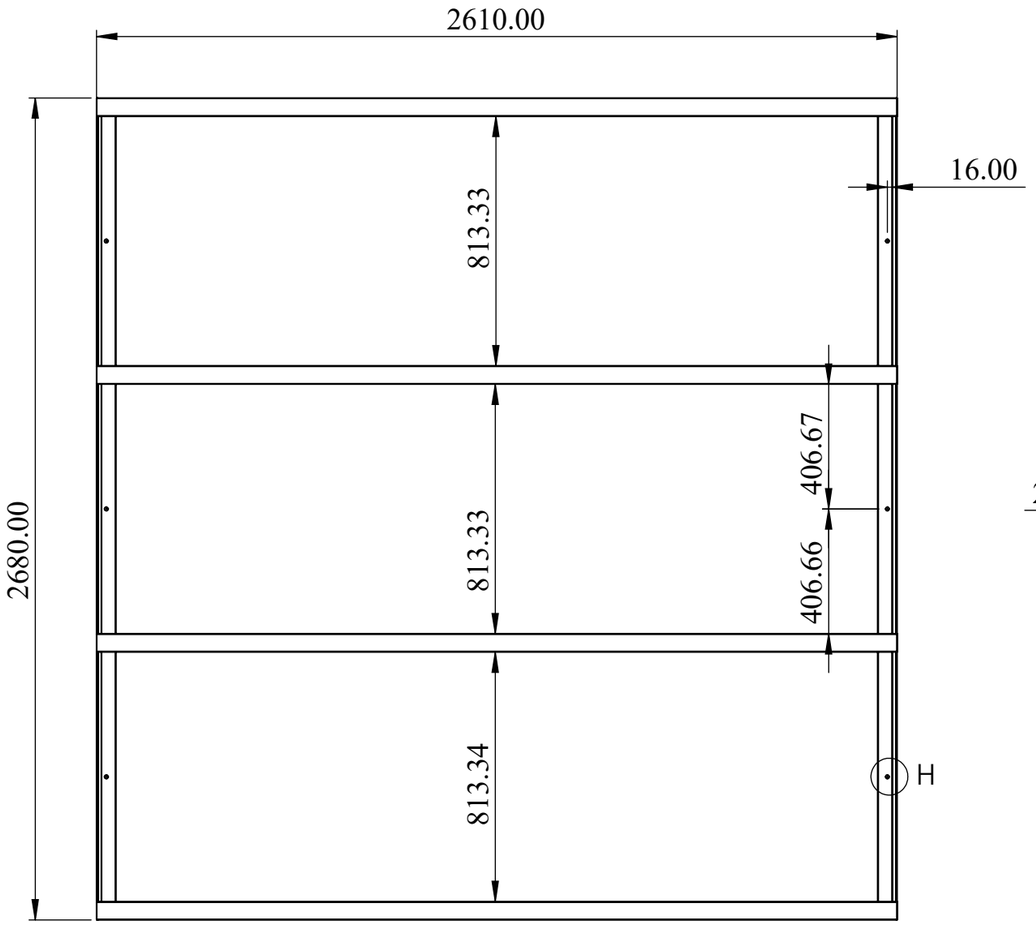


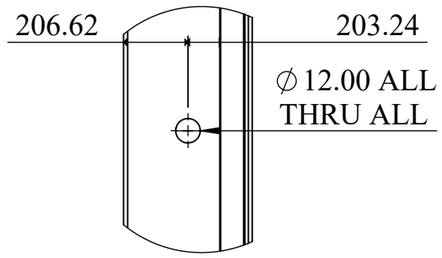


DETAIL H
SCALE 1 : 3

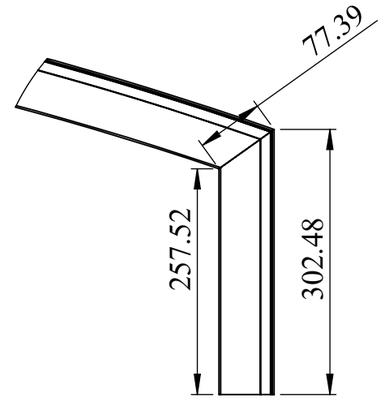

DETAIL I
SCALE 1 : 7

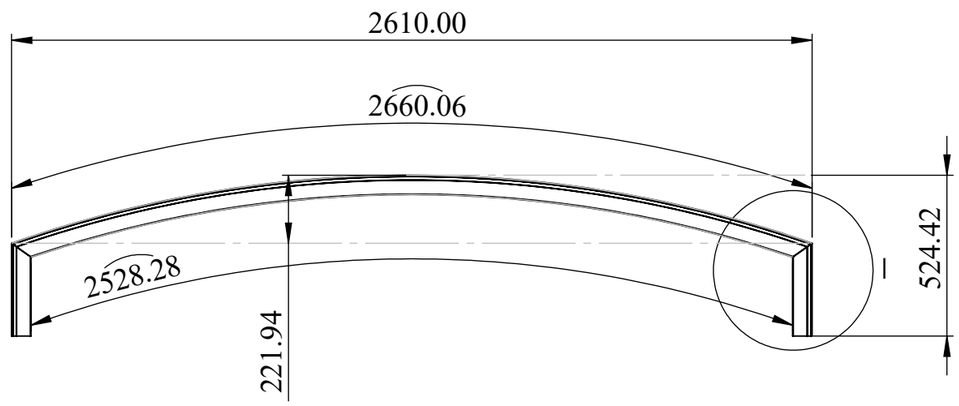


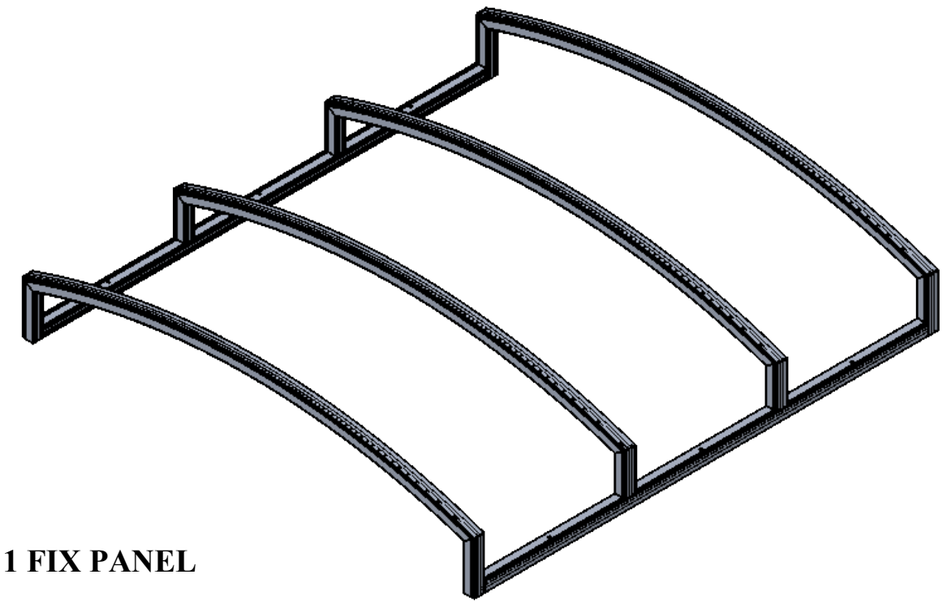


NOTE :
PANEL NO 1 FIX PANEL

TITLE - ROOF AUTOMATION				NIHVA TECHNOLOGIES PVT.LTD.PUNE Website - www.nihva.com	
DWG NO - NTPL-283-PM-001-01-01-01					
	NAME	SIGNATURE	DATE	PROJECT NO - NTPL-283-PM	
DRAWN	V.W		20-06-2025	PRODUCT - RETRACTABLE ROOF	WEIGHT - 43.05 KG
CHK'D	S.W.		24-06-2025	SITE LOCATION - LUCKNOW	REVISION -01
APPV'D	V.T.		24-06-2025	MATRIAL SPECIFICATION- AL 6063	QTY - 1
if any queries contact - supportautomation@nihva.com				PROJECTION METHOD:	SCALE :
ALL DIMENSION ARE IN mm			A3		SHEET 6 OF 25

ITEM NO.	PART NUMBER	DESCRIPTION	QTY.
1	T PLATE	SS304 -117.5X156X3 MM THK	8
2	VIJAY_Rivet_iso_15977_4_x_16_0	RIVET M4X16	80

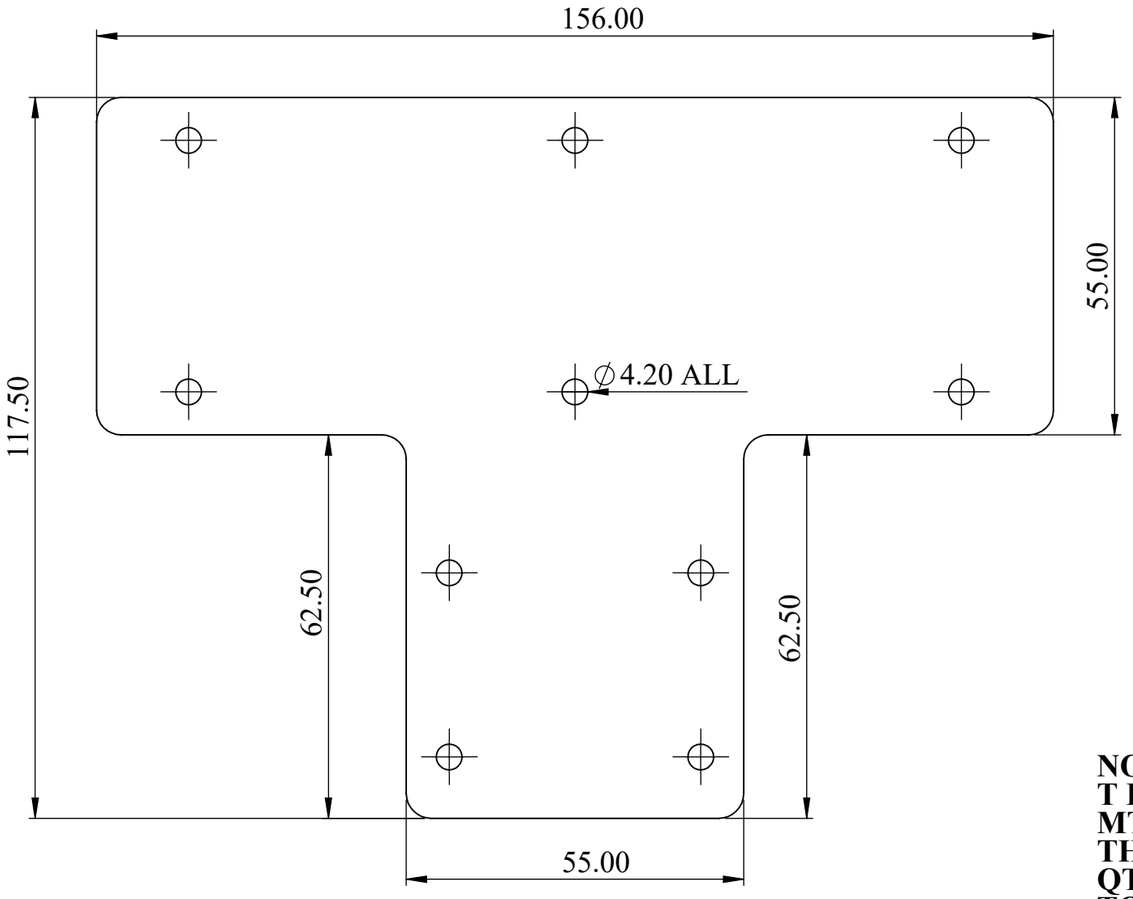


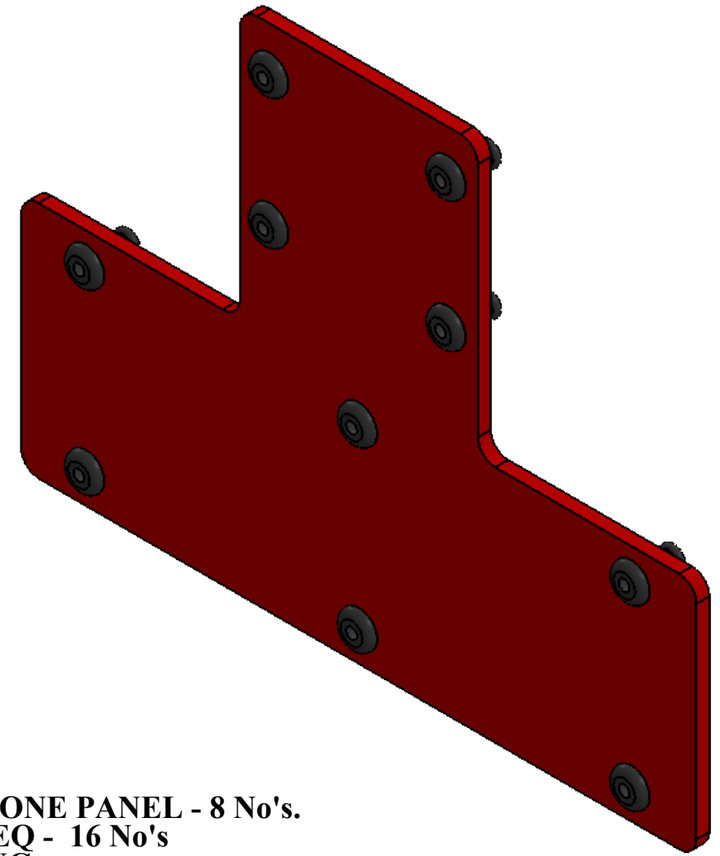


NOTE:
T PLATE
MTL - SS 304
THK - 3MM
QTY REQ FOR ONE PANEL - 8 No's.
TOTAL QTY REQ - 16 No's
LASER CUTTING.

TITLE - ROOF AUTOMATION				NIHVA TECHNOLOGIES PVT.LTD.PUNE	
DWG NO - NTPL-283-PM-001-01-02-02				Website - www.nihva.com	
	NAME	SIGNATURE	DATE	PROJECT NO - NTPL-283-PM	
DRAWN	V.W		20-06-2025	PRODUCT - RETRACTABLE ROOF	WEIGHT -
CHK'D	S.W.		24-06-2025	SITE LOCATION - LUCKNOW	REVISION - 01
APPV'D	V.T.		24-06-2025	MATRIAL SPECIFICATION- SS 304	QTY - 1
if any queries contact - supportautomation@nihva.com				PROJECTION METHOD:	SCALE :
ALL DIMENSION ARE IN mm			A3		SHEET 7 OF 25

ITEM NO.	PART NUMBER	DESCRIPTION	QTY.
1	L PLATE	SS304- 117.5X117.5X3 MM THK	1
2	VIJAY_Rivet_iso_15977_4_x_16_0	RIVET M4X16	10

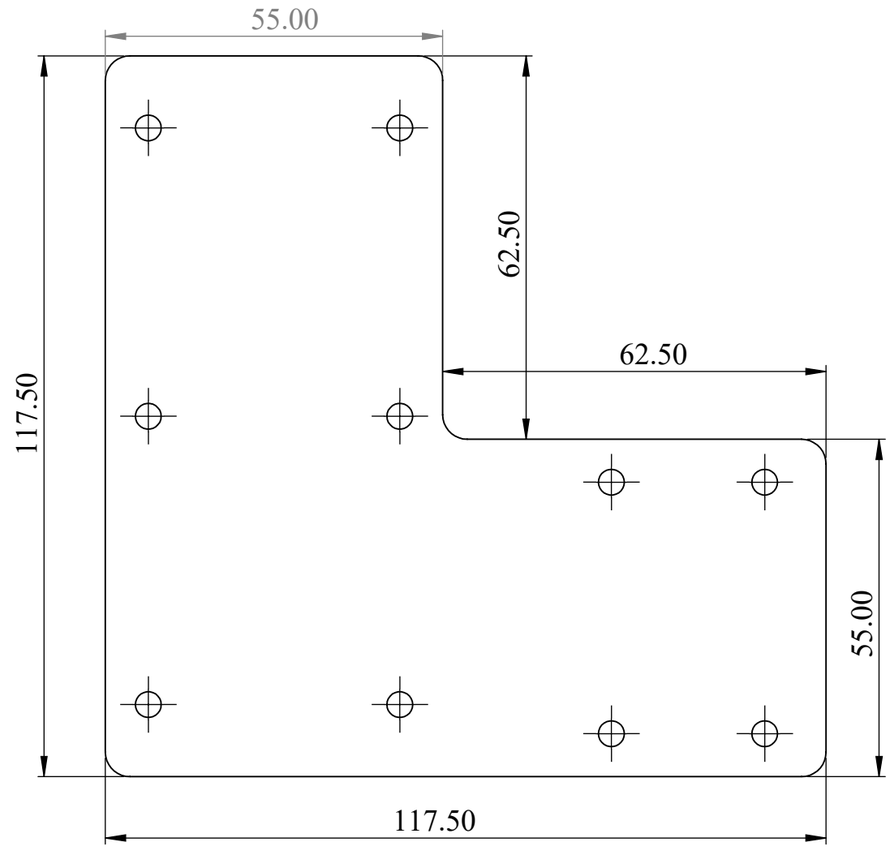


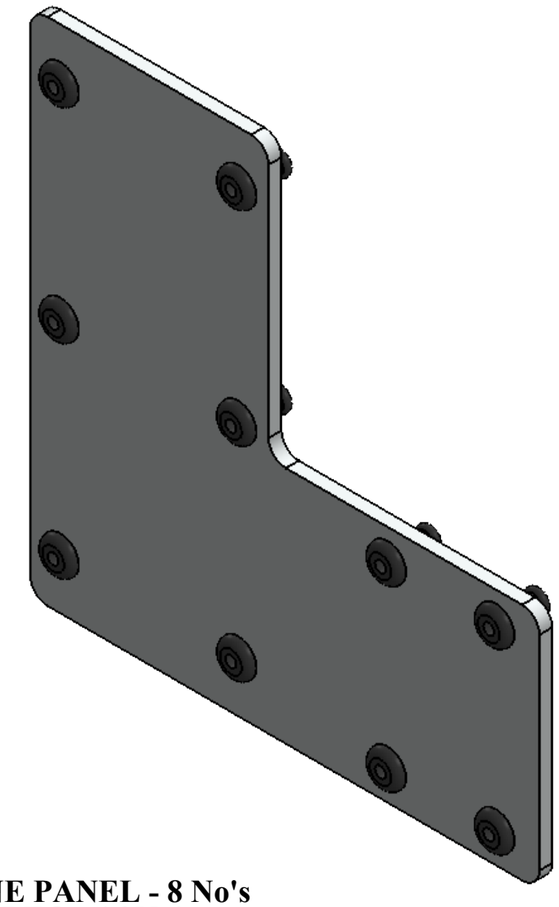


NOTE :
L PLATE
MTL - SS 304
THK - 3 MM
QTY REQ FOR ONE PANEL - 8 No's
TOTAL REQ QTY REQ - 16 No's
LASER CUTTING.

TITLE - ROOF AUTOMATION				NIHVA Technologies Pvt. Ltd.	NIHVA TECHNOLOGIES PVT.LTD.PUNE Website - www.nihva.com
DWG NO - NTPL-283-PM-001-01-03-03					
	NAME	SIGNATURE	DATE	PROJECT NO - NTPL-283-PM	
DRAWN	V.W		20-06-2025	PRODUCT - RETRACTABLE ROOF	WEIGHT -
CHK'D	S.W.		24-06-2025	SITE LOCATION - LUCKNOW	REVISION - 01
APPV'D	V.T.		24-06-2025	MATRIAL SPECIFICATION- SS 304	QTY - 1
if any queries contact - supportautomation@nihva.com				PROJECTION METHOD:	SCALE :
ALL DIMENSION ARE IN mm			A3		SHEET 8 OF 25

ITEM NO.	PART NUMBER	DESCRIPTION	QTY.
1	L ANGLE PLATE	SS304 - 60X60X3 MM	8
2	VIJAY_Rivet_iso_15977_4_x_16_0	RIVET M4X16	96

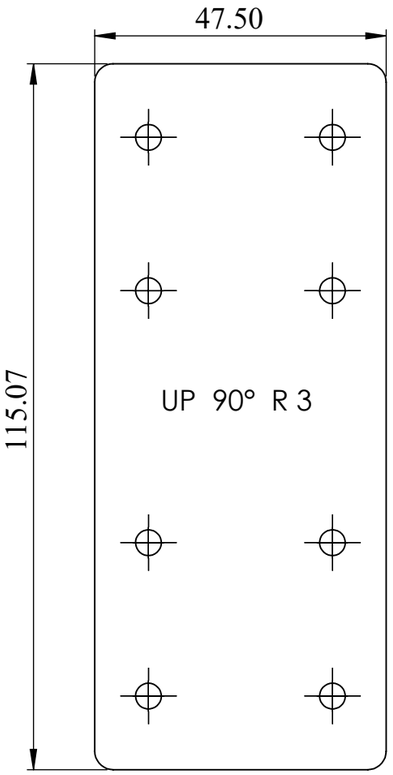


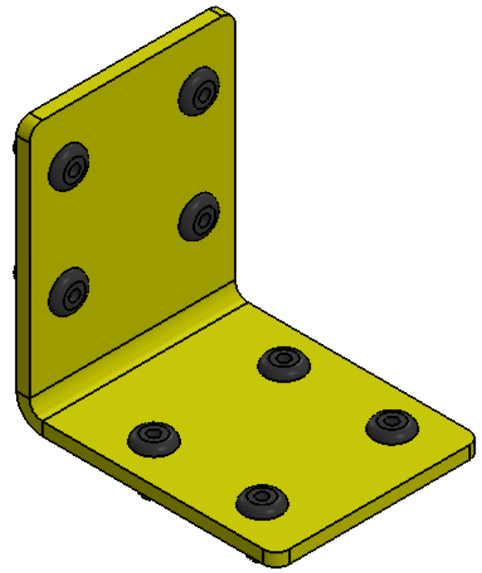


NOTE :
L ANGLE PLATE
MTL - SS 304
THK - 3 MM
QTY REQ FOR ONE PANEL - 12 No's
TOTAL QTY REQ - 24 No's
LASER CUTTING.

TITLE - ROOF AUTOMATION				NIHVA TECHNOLOGIES PVT.LTD.PUNE	
DWG NO - NTPL-283-PM-001-01-04-04				Website - www.nihva.com	
	NAME	SIGNATURE	DATE	PROJECT NO - NTPL-283-PM	
DRAWN	V.W		20-06-2025	PRODUCT - RETRACTABLE ROOF	WEIGHT -
CHK'D	S.W.		24-06-2025	SITE LOCATION - LUCKNOW	REVISION - 01
APPV'D	V.T.		24-06-2025	MATRIAL SPECIFICATION- SS 304	QTY - 1
if any queries contact - supportautomation@nihva.com				PROJECTION METHOD:	SCALE :
ALL DIMENSION ARE IN mm			A3		SHEET 9 OF 25

ITEM NO.	PART NUMBER	DESCRIPTION	QTY.
1	L ANGLE WELDING CORNER JOINING PLATE	AL JOINING PLATE	4

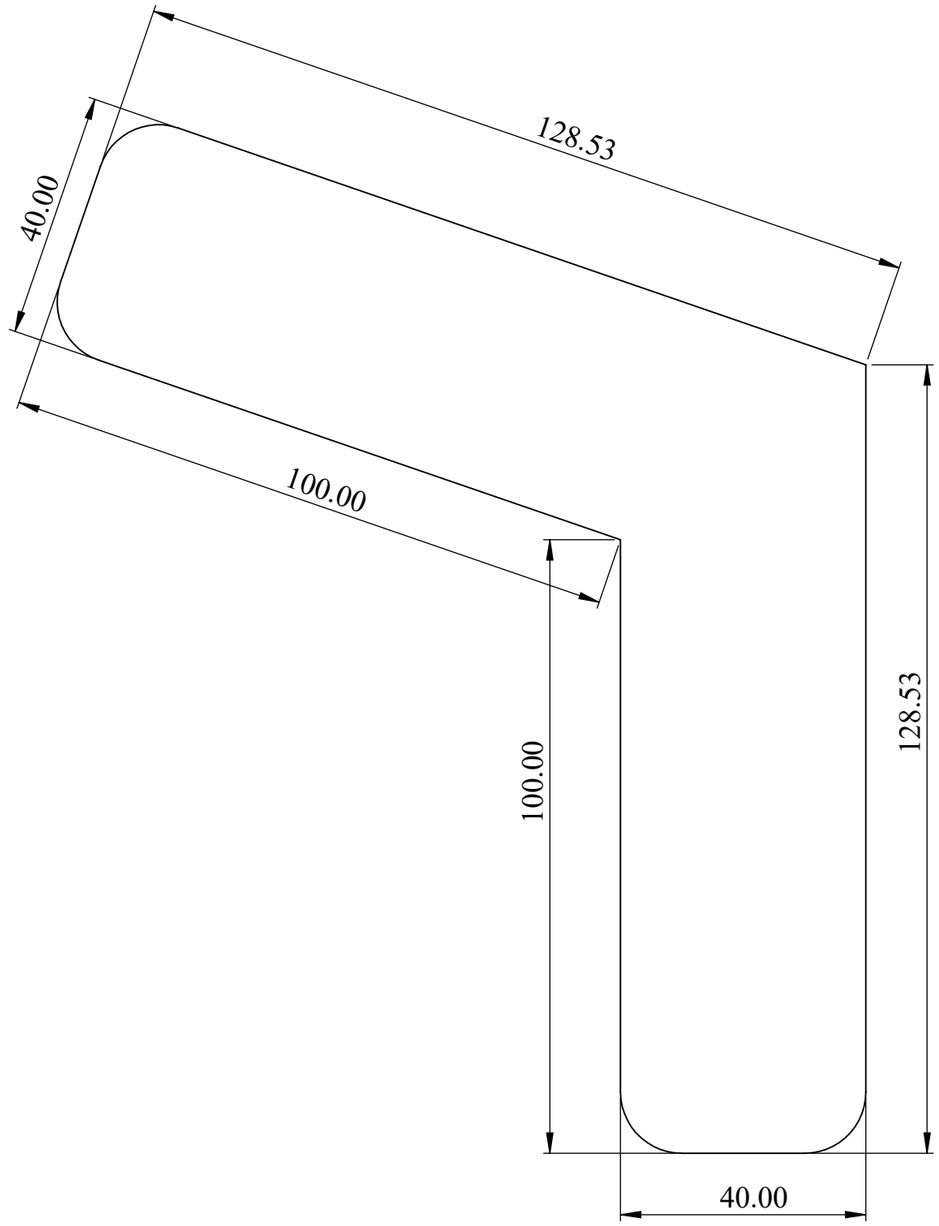


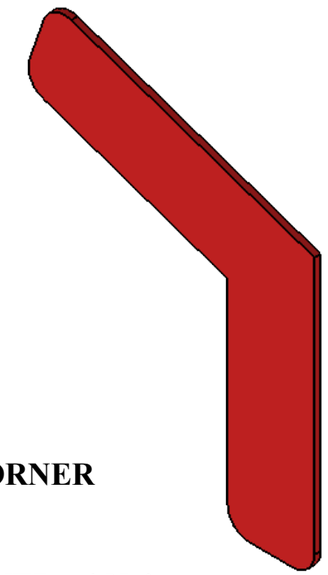


NOTE :
L ANGLE WELDING CORNER JOINING PLATE
MTL - AL
THK - 3MM
QTY REQ FOR ONE PANEL - 4 No's.
TOTAL QTY REQ - 8 No's
LASER CUTTING.


TITLE - ROOF AUTOMATION				NIHVA TECHNOLOGIES PVT.LTD.PUNE Website - www.nihva.com	
DWG NO - NTPL-283-PM-001-01-05-05					
	NAME	SIGNATURE	DATE	PROJECT NO - NTPL-283-PM	
DRAWN	V.W		20-06-2025	PRODUCT - RETRACTABLE ROOF	WEIGHT -
CHK'D	S.W.		24-06-2025	SITE LOCATION - LUCKNOW	REVISION - 01
APPV'D	V.T.		24-06-2025	MATRIAL SPECIFICATION- AL	QTY - 1
if any queries contact - supportautomation@nihva.com				PROJECTION METHOD:	SCALE :
ALL DIMENSION ARE IN mm			A3		SHEET 10 OF 25

ITEM NO.	PART NUMBER	DESCRIPTION	QTY.
1	PANEL NO 01 FIX PANEL ENCLOSER		1

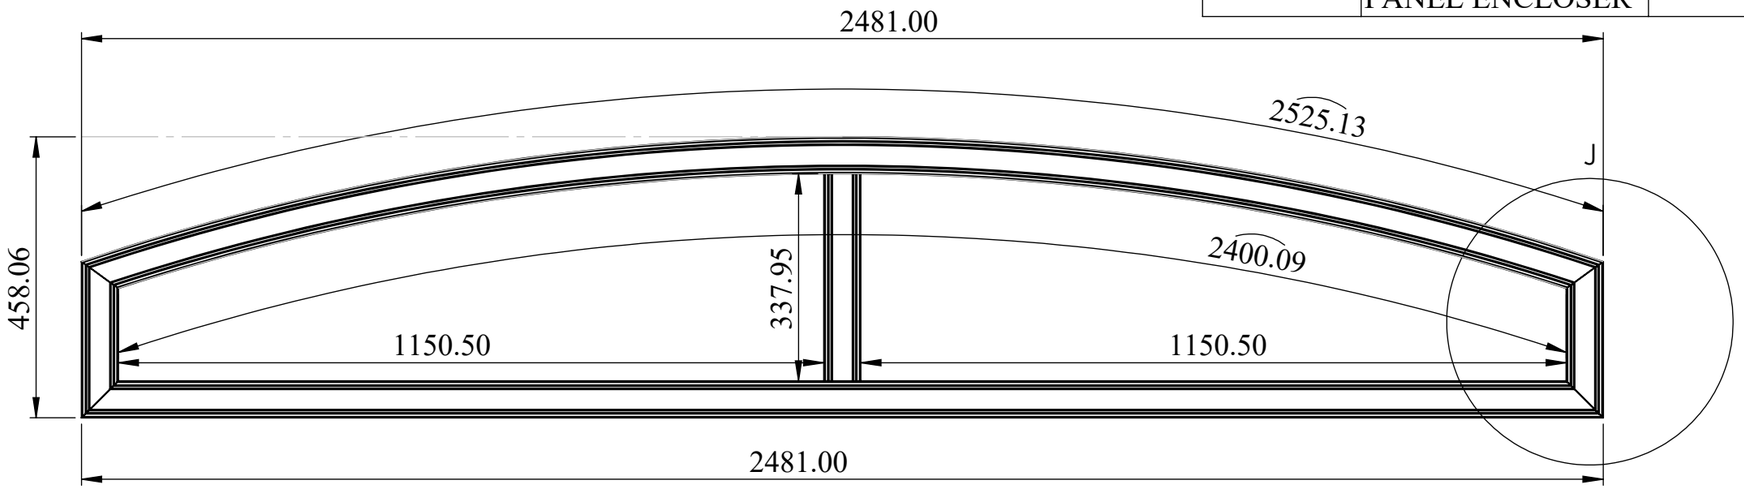

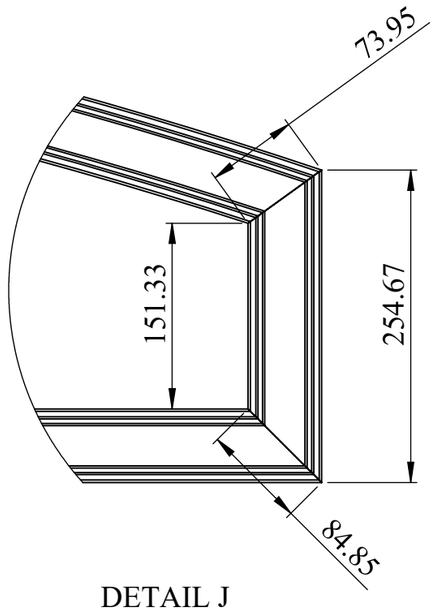


DETAIL J
SCALE 1 : 5

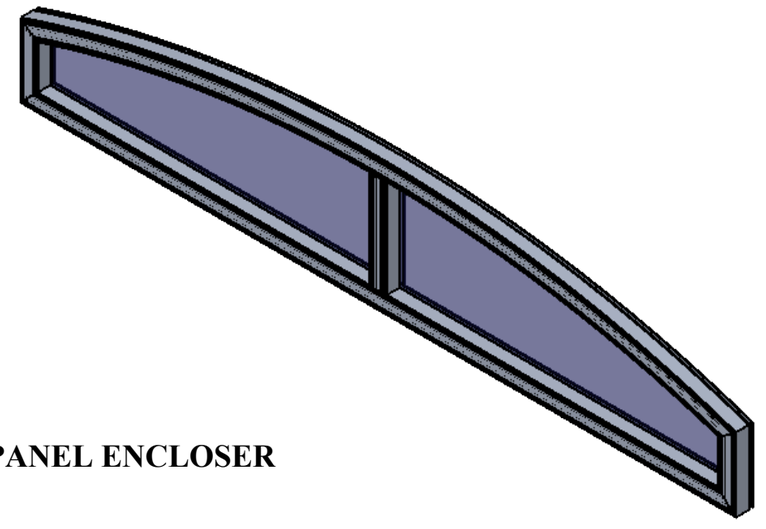


NOTE :
PANEL NO 1 FIX PANEL ENCLOSER
QTY - 01

TITLE - ROOF AUTOMATION				NIHVA TECHNOLOGIES PVT.LTD.PUNE	
DWG NO - NTPL-283-PM-001-01-07-07				Website - www.nihva.com	
	NAME	SIGNATURE	DATE	PROJECT NO - NTPL-283-PM	
DRAWN	V.W		20-06-2025	PRODUCT - RETRACTABLE ROOF	WEIGHT - 20.413 KG
CHK'D	S.W.		24-06-2025	SITE LOCATION - LUCKNOW	REVISION - 01
APPV'D	V.T.		24-06-2025	MATRIAL SPECIFICATION- AL 6063	QTY - 1
if any queries contact - supportautomation@nihva.com				PROJECTION METHOD:	SCALE :
ALL DIMENSION ARE IN mm			A3		SHEET 11 OF 25

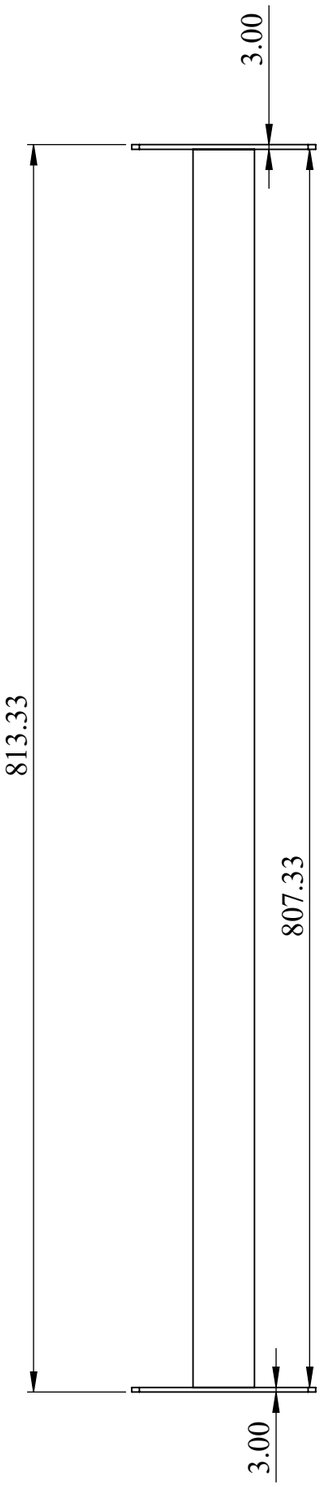


ITEM NO.	PART NUMBER	DESCRIPTION	QTY.
1	AL Support tube SQ TUBE 40X40X2 MM L-807.33 MM	AL INTERMEDIAT SUPPORT TUBE	15

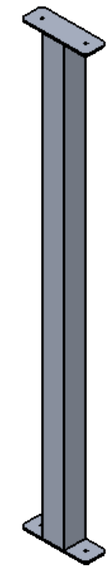



NOTE :
SQ INTERMEDIATE SUPPORT TUBE
MTL - AL
THK - 2MM
QTY REQ FOR ONE PANEL - 15 No's
TOTAL QTY REQ - 30 No's.

TITLE - ROOF AUTOMATION				NIHVA Technologies Pvt. Ltd.	NIHVA TECHNOLOGIES PVT.LTD.PUNE Website - www.nihva.com
DWG NO - NTPL-283-PM-001-01-08-08					
	NAME	SIGNATURE	DATE	PROJECT NO - NTPL-283-PM	
DRAWN	V.W		20-06-2025	PRODUCT - RETRACTABLE ROOF	WEIGHT - 0.579 KG
CHK'D	S.W.		24-06-2025	SITE LOCATION - LUCKNOW	REVISION - 01
APPV'D	V.T.		24-06-2025	MATRIAL SPECIFICATION- AL	QTY - 1
if any queries contact - supportautomation@nihva.com				PROJECTION METHOD:	SCALE :
ALL DIMENSION ARE IN mm			A3		SHEET 12 OF 25

ITEM NO.	PART NUMBER	DESCRIPTION	QTY.
1	ANCHOR FASTENING PLATE	MS - 45X32X4 MM THK	6

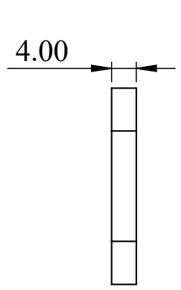

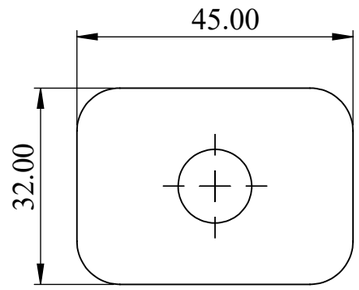

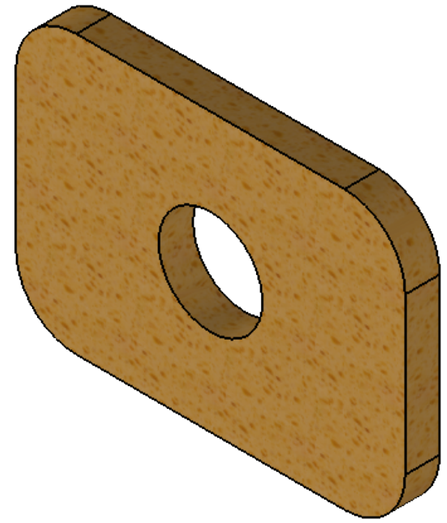


NOTE :
FASTENING PLATE
MTL - MS
THK - 4 MM
QTY - 06 No's
LASER CUTTING.

TITLE - ROOF AUTOMATION				NIHVA TECHNOLOGIES PVT.LTD.PUNE	
DWG NO - NTPL-283-PM-001-01-09-09				Website - www.nihva.com	
	NAME	SIGNATURE	DATE	PROJECT NO - NTPL-283-PM	
DRAWN	V.W		20-06-2025	PRODUCT - RETRACTABLE ROOF	WEIGHT -
CHK'D	S.W.		24-06-2025	SITE LOCATION - LUCKNOW	REVISION - 01
APPV'D	V.T.		24-06-2025	MATRIAL SPECIFICATION- MS	QTY - 1
if any queries contact - supportautomation@nihva.com				PROJECTION METHOD:	SCALE :
ALL DIMENSION ARE IN mm			A3		SHEET 13 OF 25

ITEM NO.	PART NUMBER	DESCRIPTION	QTY.
1	RR_ Anchor Bolt M10x100	STD	1



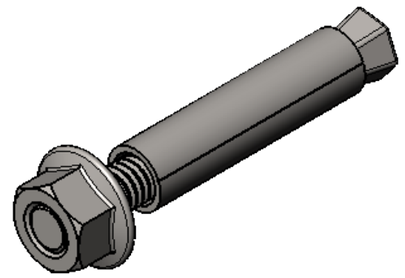


NOTE :


CHEMICAL ANCHOR BOLT M10 X 200
MTL - SS
QTY - 10 No's.
NOTE :


CHEMICAL ANCHOR BOLT M10 X 100
MTL - SS
QTY - 30 No's.

TITLE - ROOF AUTOMATION				NIHVA Technologies Pvt. Ltd.	NIHVA TECHNOLOGIES PVT.LTD.PUNE Website - www.nihva.com
DWG NO - NTPL-283-PM-001-01-10-10				PROJECT NO - NTPL-283-PM	
	NAME	SIGNATURE	DATE		
DRAWN	V.W		20-06-2025	PRODUCT - RETRACTABLE ROOF	WEIGHT -
CHK'D	S.W.		24-06-2025	SITE LOCATION - LUCKNOW	REVISION -
APPV'D	V.T.		24-06-2025	MATRIAL SPECIFICATION- SS	QTY - 1
if any queries contact - supportautomation@nihva.com				PROJECTION METHOD:	SCALE :
ALL DIMENSION ARE IN mm			A3		SHEET 14 OF 25


ITEM NO.	PART NUMBER	DESCRIPTION	QTY.
1	GNT001 TRACK 1		2

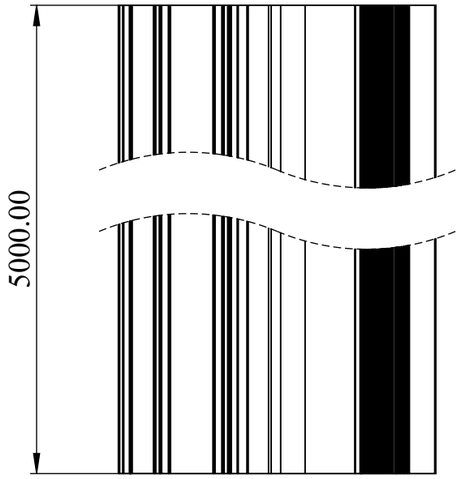

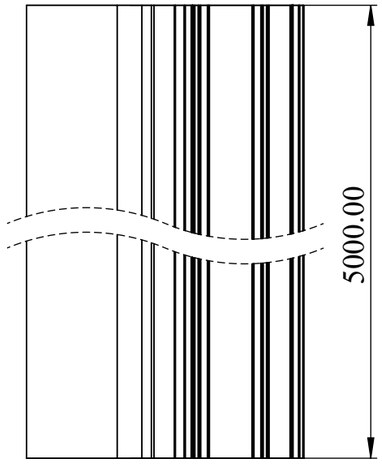

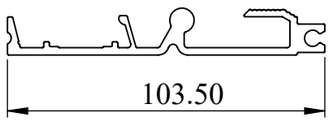


THIS TRACK MOUNT AT MOTOR SIDE

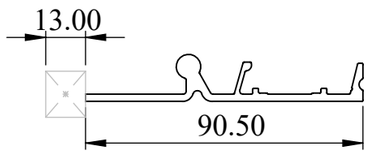


THIS CUT TRACK MOUNT AT WALL SIDE WHERE SPACE AVIALABLE 170 MM

NOTE :
TRACK - GNT001
ONE TRACK NEED TO BE BE CUT 13 MM


TITLE - ROOF AUTOMATION				NIHVA TECHNOLOGIES PVT.LTD.PUNE	
DWG NO - NTPL-283-PM-001-02-00-00				Website - www.nihva.com	
	NAME	SIGNATURE	DATE	PROJECT NO - NTPL-283-PM	
DRAWN	V.W		20-06-2025	PRODUCT - RETRACTABLE ROOF	WEIGHT -
CHK'D	S.W.		24-06-2025	SITE LOCATION - LUCKNOW	REVISION - 01
APPV'D	V.T.		24-06-2025	MATRIAL SPECIFICATION- MS	QTY - 02
if any queries contact - supportautomation@nihva.com				PROJECTION METHOD:	SCALE :
ALL DIMENSION ARE IN mm			A3		SHEET 15 OF 25

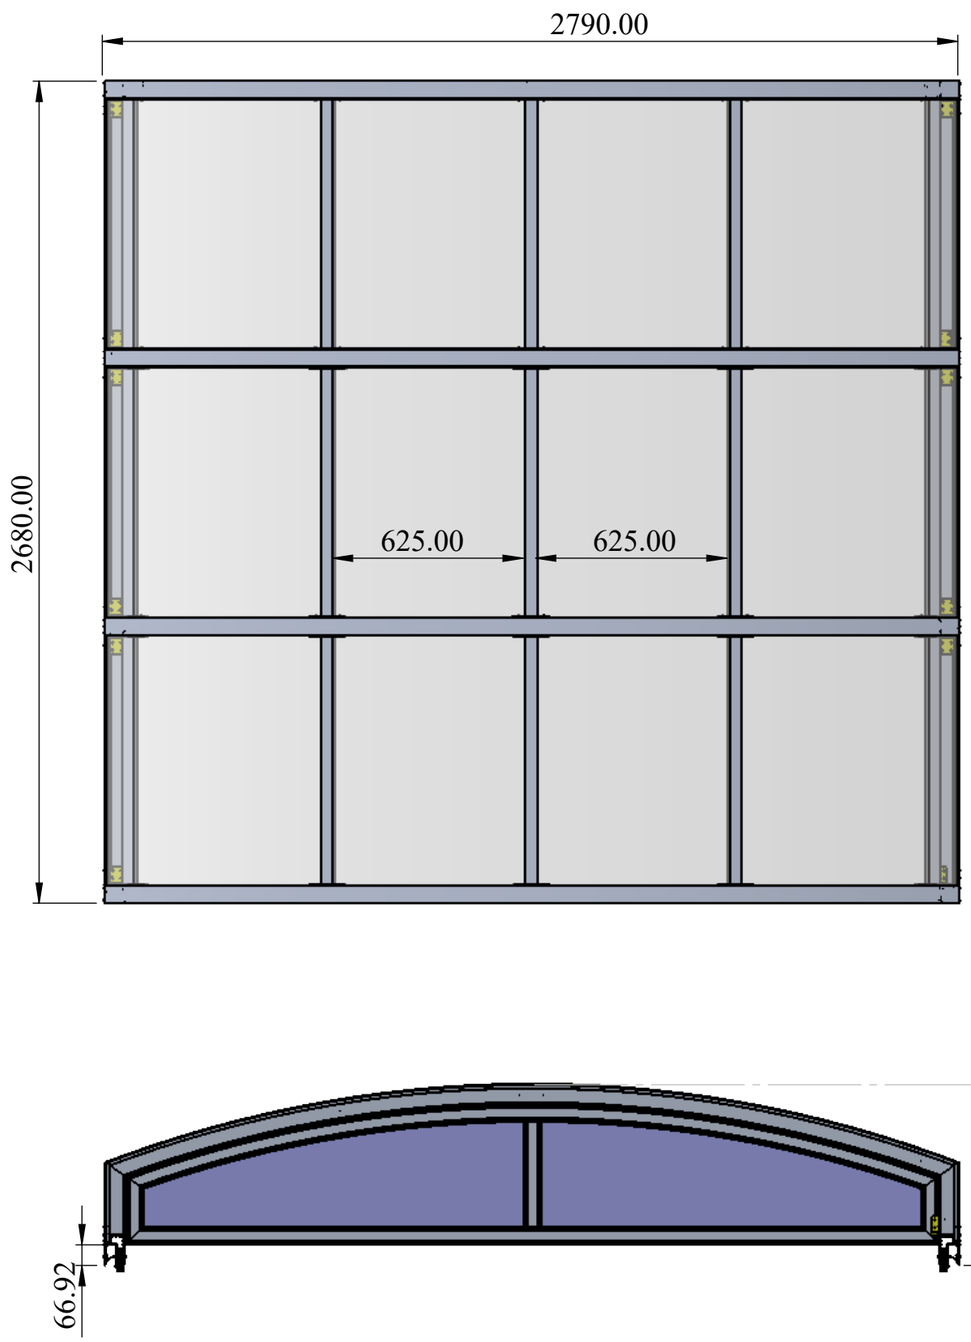


ITEM NO.	PART NUMBER	DESCRIPTION	QTY.
1	PANEL NO 2 MOVABLE PANEL		1
2	T PLATE ASM		8
3	L PLATE ASM		8
4	L ANGLE PLATE ASM		12
5	SQ TUBE 40X40X2 MM THK 813.33 LONG ASM		15
6	PANEL NO 2 MOVABLE PANEL POLYCARBONET SHEET		3
7	PANEL NO 02 ENCLOSER		1
8	NYLON WHEEL (1)	NYLON WHEEL ∅65X18	5

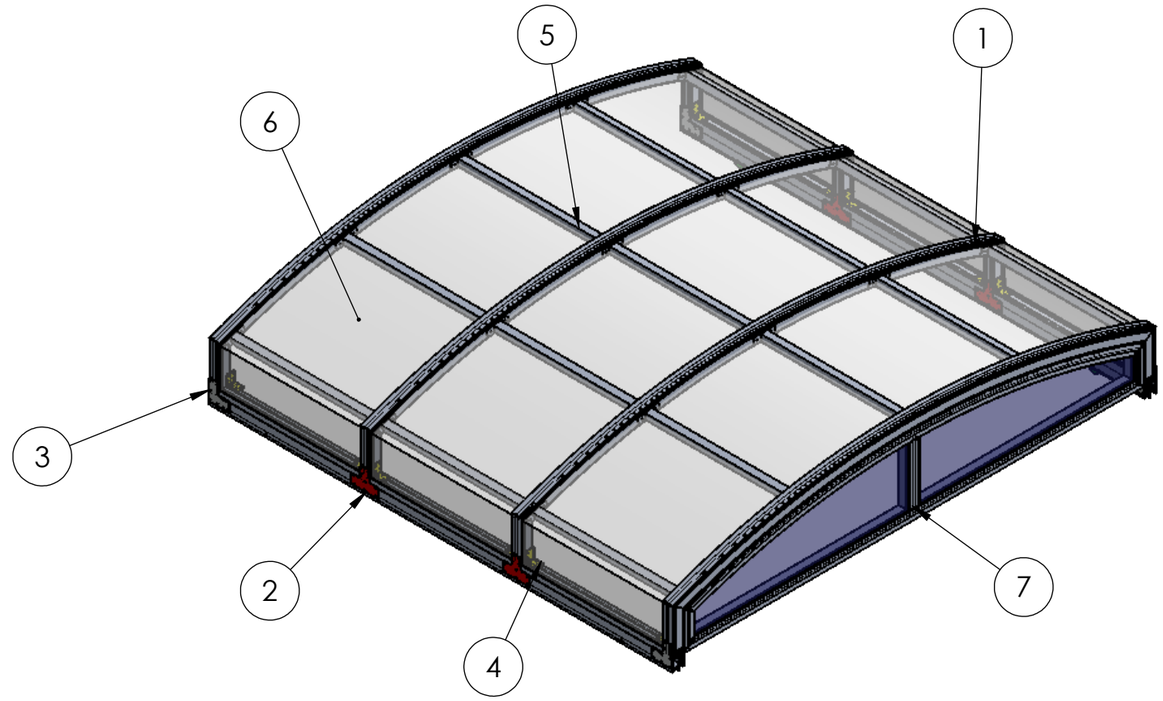


TITLE - ROOF AUTOMATION				NIHVA TECHNOLOGIES PVT.LTD.PUNE Website - www.nihva.com	
DWG NO - NTPL-283-PM-001-03-00-00					
	NAME	SIGNATURE	DATE	PROJECT NO - NTPL-283-PM	
DRAWN	V.W		20-06-2025	PRODUCT - RETRACTABLE ROOF	WEIGHT -
CHK'D	S.W.		24-06-2025	SITE LOCATION - LUCKNOW	REVISION - 01
APPV'D	V.T.		24-06-2025	MATRIAL SPECIFICATION-	QTY - 1
if any queries contact - supportautomation@nihva.com				PROJECTION METHOD:	SCALE :
ALL DIMENSION ARE IN mm			A3		SHEET 16 OF 25

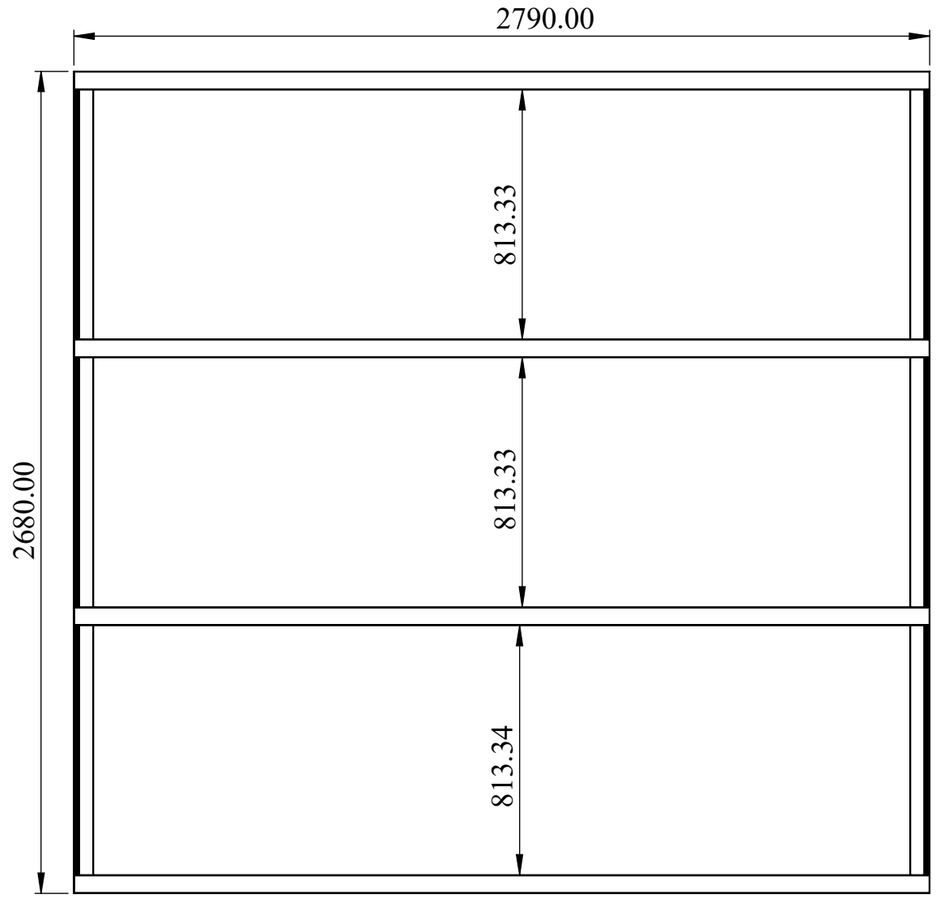


ITEM NO.	PART NUMBER	DESCRIPTION	QTY.
1	PANEL NO 2 MOVABLE PANEL		1

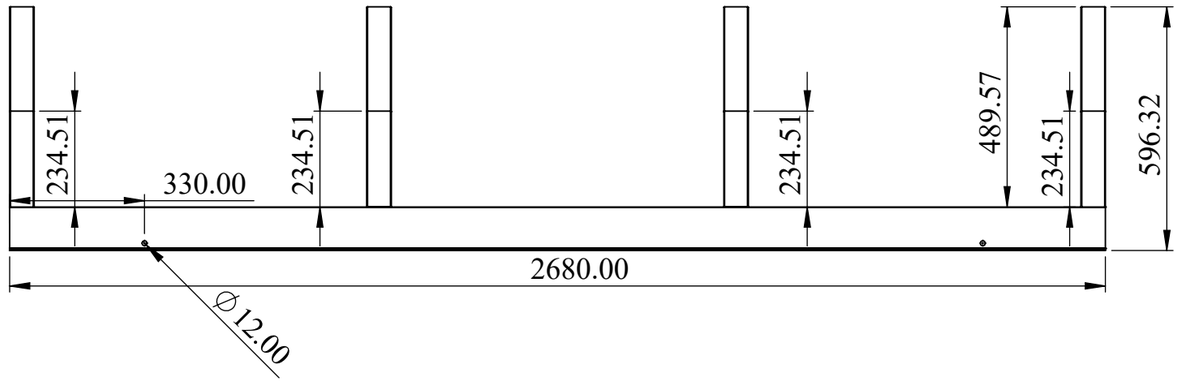

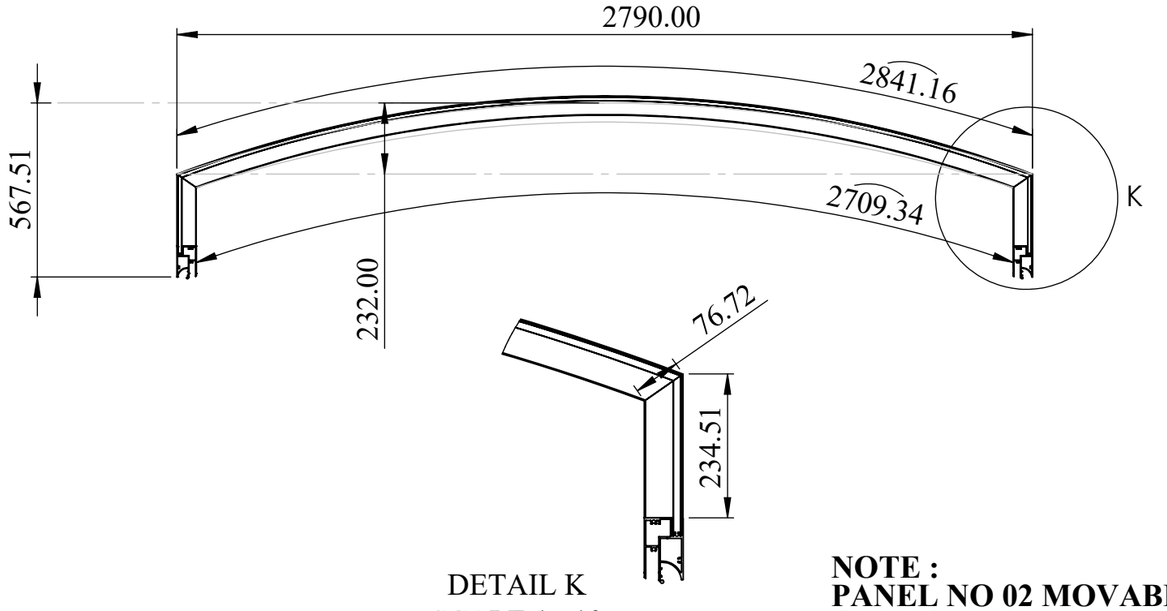


DETAIL K
SCALE 1 : 10


NOTE :
PANEL NO 02 MOVABLE PANEL
QTY - 01 No's.

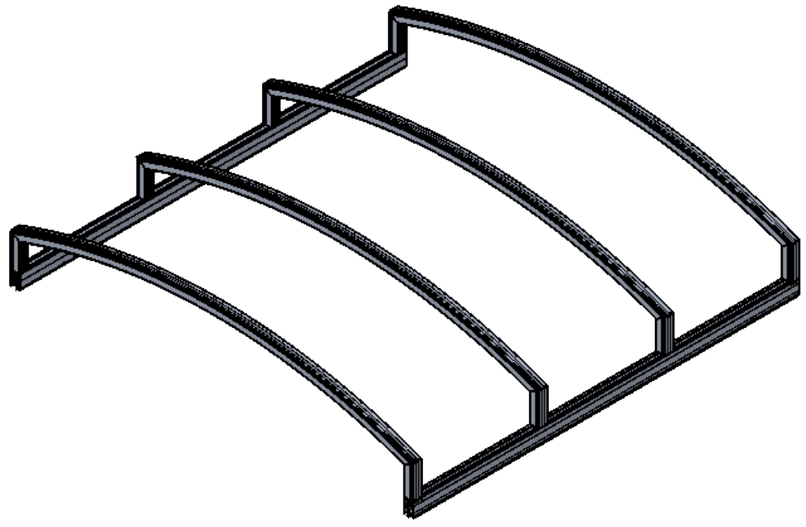

TITLE - ROOF AUTOMATION				NIHVA TECHNOLOGIES PVT.LTD.PUNE Website - www.nihva.com	
DWG NO - NTPL-283-PM-001-03-01-01					
	NAME	SIGNATURE	DATE	PROJECT NO - NTPL-283-PM	
DRAWN	V.W		20-06-2025	PRODUCT - RETRACTABLE ROOF	WEIGHT -
CHK'D	S.W.		24-06-2025	SITE LOCATION - LUCKNOW	REVISION - 01
APPV'D	V.T.		24-06-2025	MATRIAL SPECIFICATION- AL	QTY - 1
if any queries contact - supportautomation@nihva.com				PROJECTION METHOD:	SCALE :
ALL DIMENSION ARE IN mm			A3		SHEET 17 OF 25

ITEM NO.	PART NUMBER	DESCRIPTION	QTY.
1	NYLON WHEEL (1)	NYLON WHEEL ∅65X18	4

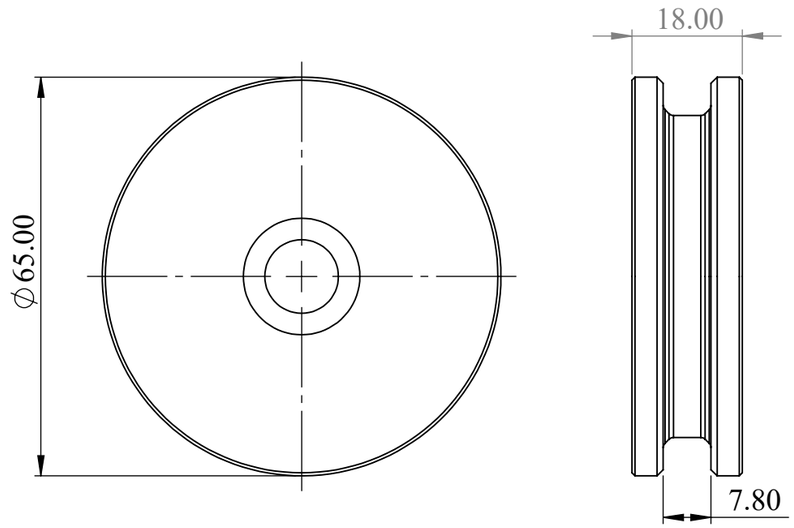


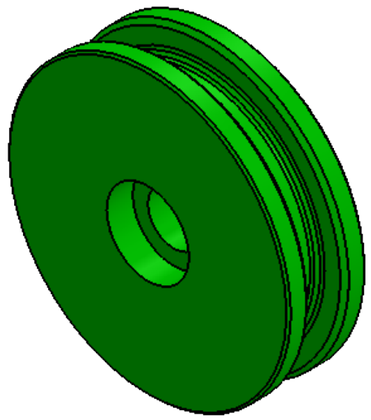


NOTE :
NYLON WHEEL
QTY - 04 No'S.


TITLE - ROOF AUTOMATION				NIHVA Technologies Pvt. Ltd.	NIHVA TECHNOLOGIES PVT.LTD.PUNE Website - www.nihva.com
DWG NO - NTPL-283-PM-001-03-02-02				PROJECT NO - NTPL-283-PM	
	NAME	SIGNATURE	DATE		
DRAWN	V.W		20-06-2025	PRODUCT - RETRACTABLE ROOF	WEIGHT - 0.95 KG
CHK'D	S.W.		24-06-2025	SITE LOCATION - LUCKNOW	REVISION - 01
APPV'D	V.T.		24-06-2025	MATRIAL SPECIFICATION- AL	QTY - 1
if any queries contact - supportautomation@nihva.com				PROJECTION METHOD:	SCALE :
ALL DIMENSION ARE IN mm			A3		SHEET 18 OF 25

ITEM NO.	PART NUMBER	DESCRIPTION	QTY.
1	PANEL NO 02 ENCLOSER		1

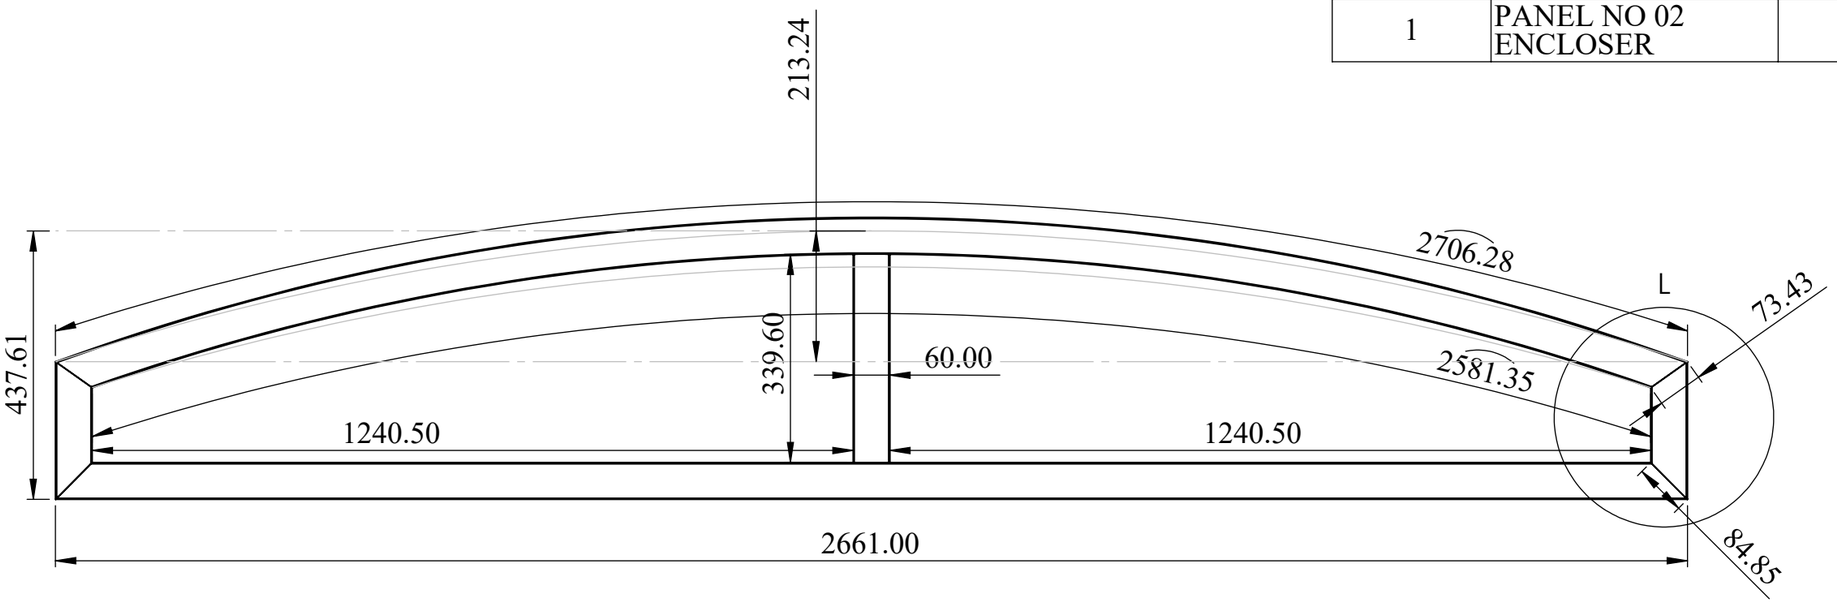

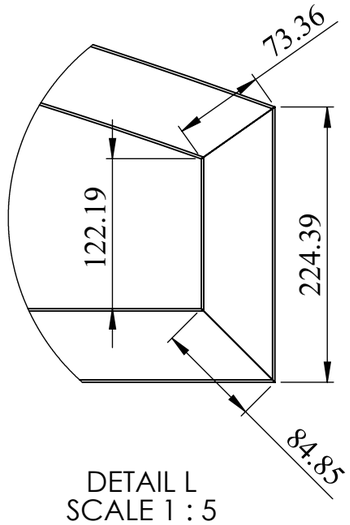



DETAIL L
SCALE 1 : 5

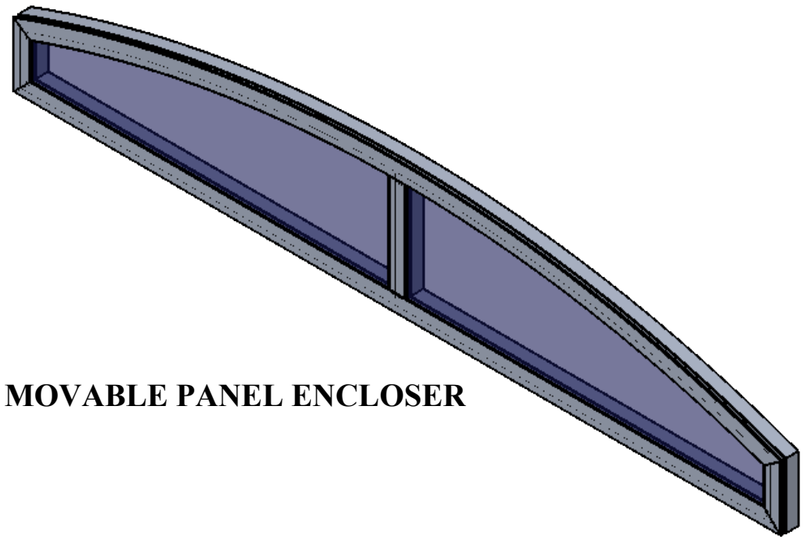


NOTE :
PANEL NO 02 MOVABLE PANEL ENCLOSER
QTY - 01

TITLE - ROOF AUTOMATION				NIHVA TECHNOLOGIES PVT.LTD.PUNE	
DWG NO - NTPL-283-PM-001-03-03-03				Website - www.nihva.com	
	NAME	SIGNATURE	DATE	PROJECT NO - NTPL-283-PM	
DRAWN	V.W		20-06-2025	PRODUCT - RETRACTABLE ROOF	WEIGHT - 21.533 KG
CHK'D	S.W.		24-06-2025	SITE LOCATION - LUCKNOW	REVISION - 01
APPV'D	V.T.		24-06-2025	MATRIAL SPECIFICATION- AL	QTY - 1
if any queries contact - supportautomation@nihva.com				PROJECTION METHOD:	SCALE :
ALL DIMENSION ARE IN mm			A3		SHEET 19 OF 25

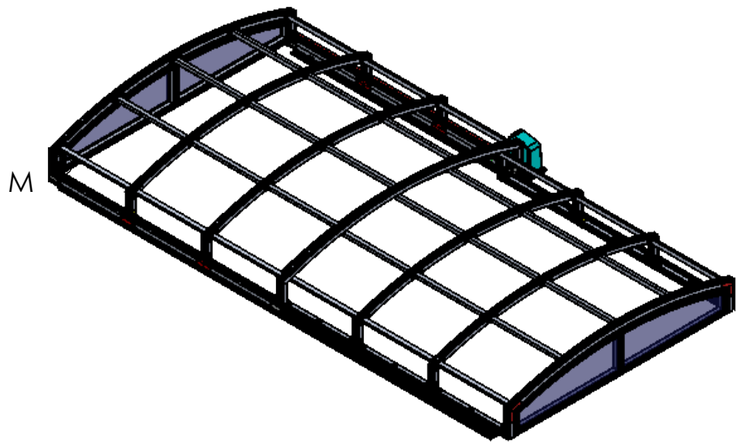

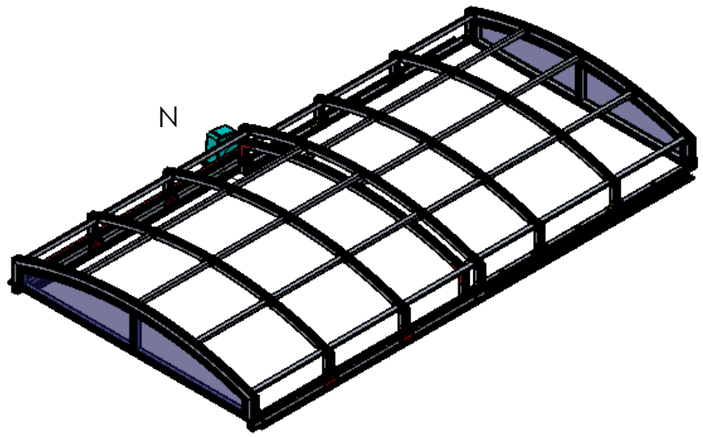

DETAIL M
SCALE 1 : 2

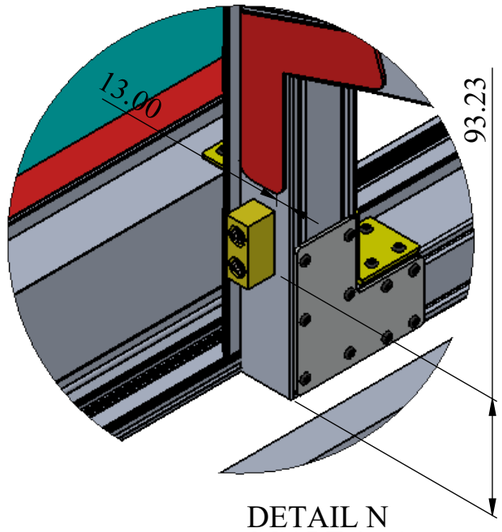

DETAIL N
SCALE 1 : 4


THIS NYLON STOPPER
ATTCHED TO THE MOVABLE PANEL
TO STACK THE MOVABLE PANEL TO THE FIX
PANEL.


NOTE :
SUB ASM - NYLON STOPPER ASM

THIS NYLON STOPPER IS ATTACED TO
FIX PANEL AT FRONT SIDE

TITLE - ROOF AUTOMATION				NIHVA Technologies Pvt. Ltd.	NIHVA TECHNOLOGIES PVT.LTD.PUNE Website - www.nihva.com
DWG NO - NTPL-283-PM-001-00-00-00				PROJECT NO - NTPL-283-PM	
	NAME	SIGNATURE	DATE		
DRAWN	V.W		20-06-2025	PRODUCT - RETRACTABLE ROOF	WEIGHT -
CHK'D	S.W.		24-06-2025	SITE LOCATION - LUCKNOW	REVISION - 01
APPV'D	V.T.		24-06-2025	MATRIAL SPECIFICATION-	QTY - 1
if any queries contact - supportautomation@nihva.com				PROJECTION METHOD:	SCALE :
ALL DIMENSION ARE IN mm			A3		SHEET 20 OF 25

ITEM NO.	PART NUMBER	DESCRIPTION	QTY.
1	NYLON STOPPER		4

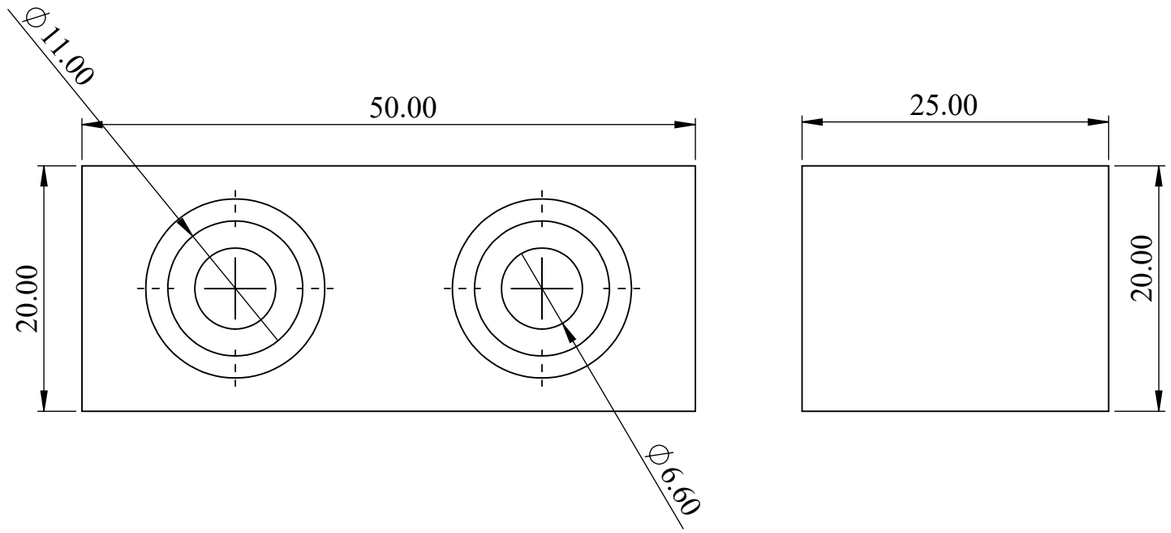


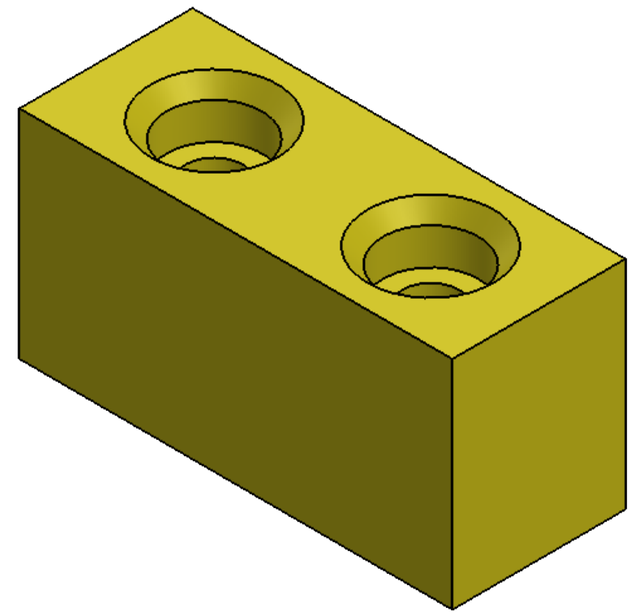


NOTE :
NYLON STOPPER
QTY - 04 No'S.

TITLE - ROOF AUTOMATION				NIHVA Technologies Pvt. Ltd.	NIHVA TECHNOLOGIES PVT.LTD.PUNE Website - www.nihva.com
DWG NO - NTPL-283-PM-001-04-00-00				PROJECT NO - NTPL-283-PM	
	NAME	SIGNATURE	DATE		
DRAWN	V.W		20-06-2025	PRODUCT - RETRACTABLE ROOF	WEIGHT -
CHK'D	S.W.		24-06-2025	SITE LOCATION - LUCKNOW	REVISION - 01
APPV'D	V.T.		24-06-2025	MATRIAL SPECIFICATION - NYLON	QTY - 1
if any queries contact - supportautomation@nihva.com				PROJECTION METHOD:	SCALE :
ALL DIMENSION ARE IN mm			A3		SHEET 21 OF 25

ITEM NO.	PART NUMBER	DESCRIPTION	QTY.
1	IS 2269 - M6 x 40-N	SS	8

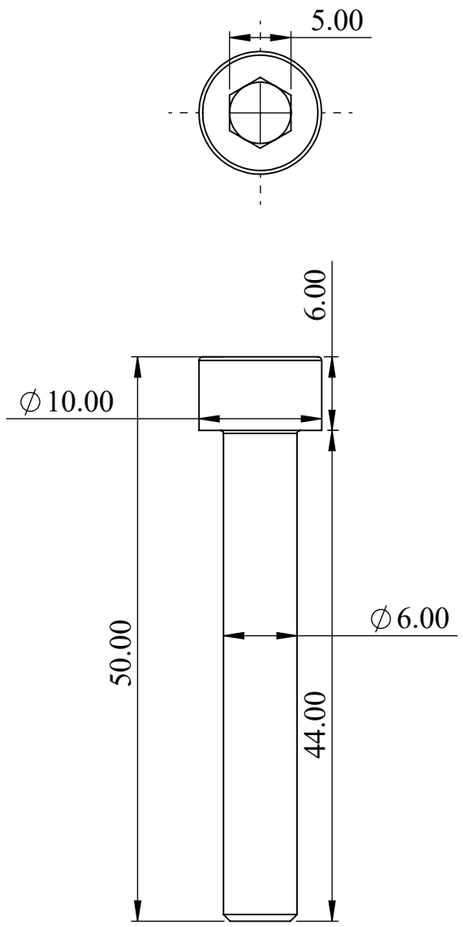


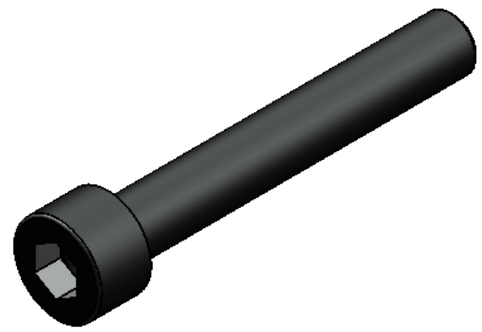



NOTE :
ALLEN BOLT M6 X 50 MM L
QTY - 8No's.

TITLE - ROOF AUTOMATION				NIHVA TECHNOLOGIES PVT.LTD.PUNE	
DWG NO - NTPL-283-PM-001-05-00-00				Website - www.nihva.com	
	NAME	SIGNATURE	DATE	PROJECT NO - NTPL-283-PM	
DRAWN	V.W		20-06-2025	PRODUCT - RETRACTABLE ROOF	WEIGHT -
CHK'D	S.W.		24-06-2025	SITE LOCATION - LUCKNOW	REVISION - 01
APPV'D	V.T.		24-06-2025	MATRIAL SPECIFICATION-	QTY - 1
if any queries contact - supportautomation@nihva.com				PROJECTION METHOD:	SCALE :
ALL DIMENSION ARE IN mm			A3		SHEET 22 OF 25

ITEM NO.	PART NUMBER	DESCRIPTION	QTY.
1	RR_NICE RB 600		1

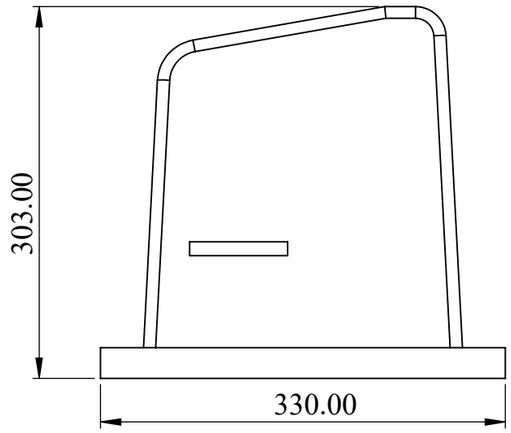

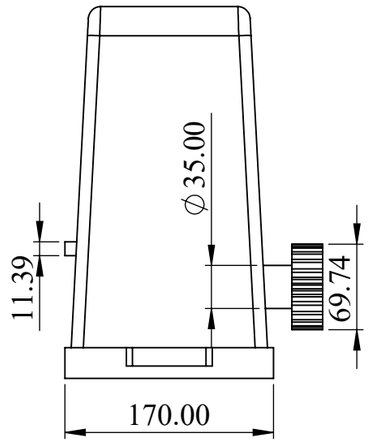


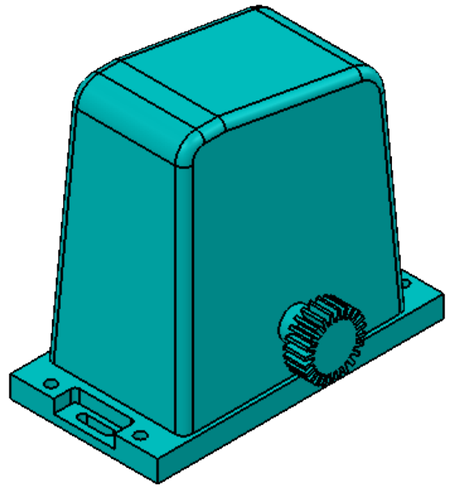



NOTE :
RB NICE 600
QTY - 01 No's.

TITLE - ROOF AUTOMATION				NIHVA Technologies Pvt. Ltd.	NIHVA TECHNOLOGIES PVT.LTD.PUNE Website - www.nihva.com
DWG NO - NTPL-283-PM-001-07-00-00					
	NAME	SIGNATURE	DATE	PROJECT NO - NTPL-283-PM	
DRAWN	V.W		20-06-2025	PRODUCT - RETRACTABLE ROOF	WEIGHT -
CHK'D	S.W.		24-06-2025	SITE LOCATION - LUCKNOW	REVISION - 01
APPV'D	V.T.		24-06-2025	MATRIAL SPECIFICATION-	QTY - 1
if any queries contact - supportautomation@nihva.com				PROJECTION METHOD:	SCALE :
ALL DIMENSION ARE IN mm			A3		SHEET 23 OF 25

ITEM NO.	PART NUMBER	DESCRIPTION	QTY.
1	RR_RACK	STD (M4 RACK, 30x8x1000 mm, ZINC COATED WITH SPACERS AND SCREWS.)	3

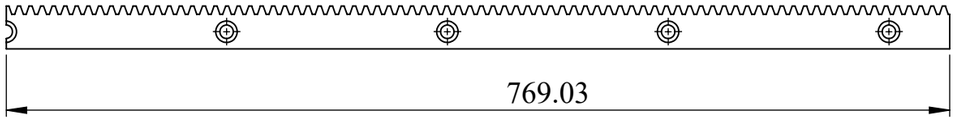

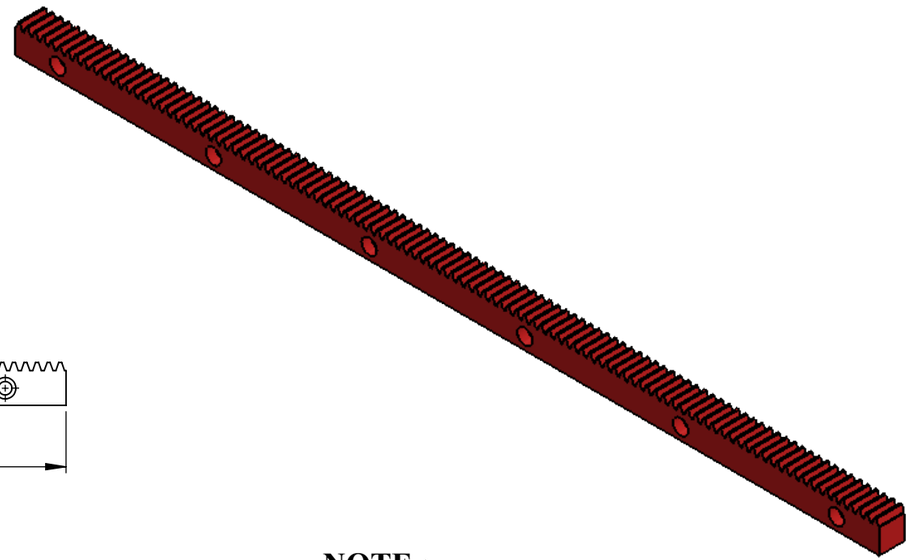


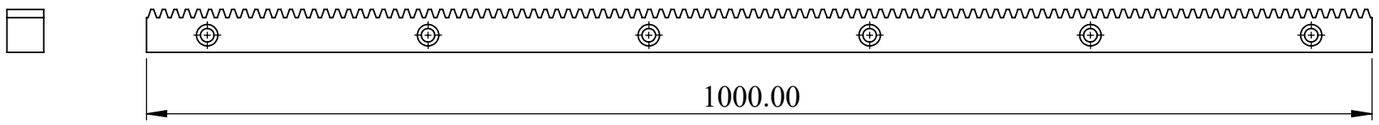


NOTE :
RACK
QTY - 03 No's
ONE TRACK NEED TO BE CUT

TITLE - ROOF AUTOMATION				NIHVA TECHNOLOGIES PVT.LTD.PUNE Website - www.nihva.com	
DWG NO - NTPL-283-PM-001-09-00-00					
	NAME	SIGNATURE	DATE	PROJECT NO - NTPL-283-PM	
DRAWN	V.W		20-06-2025	PRODUCT - RETRACTABLE ROOF	WEIGHT -
CHK'D	S.W.		2406-2025	SITE LOCATION - LUCKNOW	REVISION - 01
APPV'D	V.T.		24-06-2025	MATRIAL SPECIFICATION-	QTY - 1
if any queries contact - supportautomation@nihva.com				PROJECTION METHOD:	SCALE :
ALL DIMENSION ARE IN mm			A3		SHEET 24 OF 25

ITEM NO.	PART NUMBER	DESCRIPTION	QTY.
1	MOTOR BRACKET PLATE MS 308X300X6MM THK	MS	1

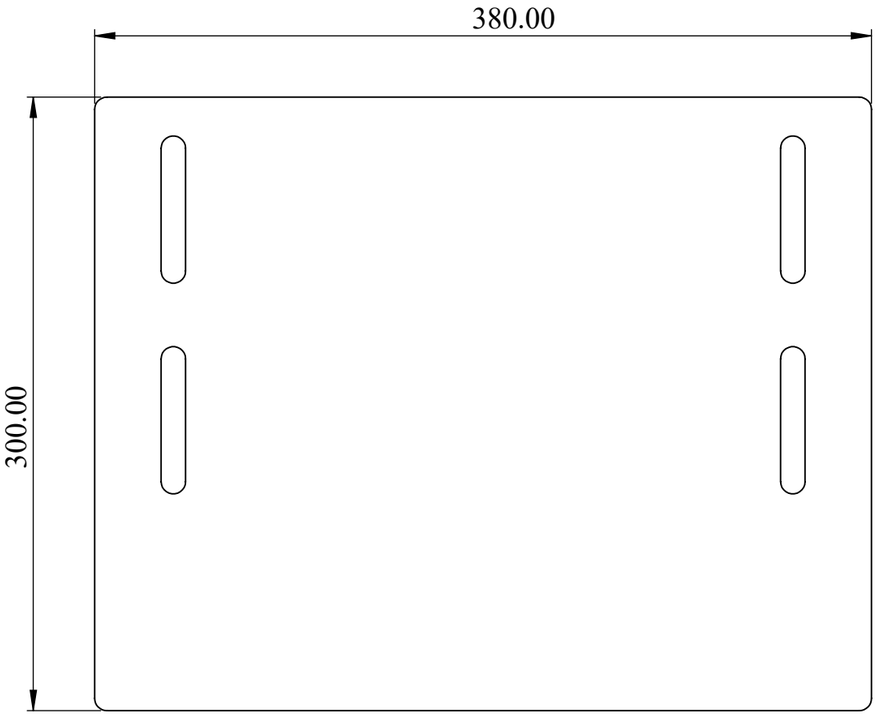

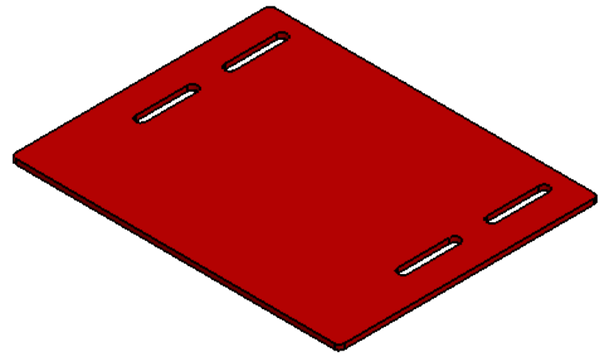

NOTE :
MOTOR BRACKET PALTE FOR MOTOR MOUNTING
MTL - MS
THK - 6MM

TITLE - ROOF AUTOMATION				NIHVA TECHNOLOGIES PVT.LTD.PUNE	
DWG NO - NTPL-283-PM-001-00-00-00				Website - www.nihva.com	
	NAME	SIGNATURE	DATE	PROJECT NO - NTPL-283-PM	
DRAWN	V.W		17-06-2025	PRODUCT - RETRACTABLE ROOF	WEIGHT -
CHK'D	S.W.		17-06-2025	SITE LOCATION - LUCKNOW	REVISION -
APPV'D	V.T.		17-06-2025	MATRIAL SPECIFICATION-	QTY - 1
if any queries contact - supportautomation@nihva.com				PROJECTION METHOD:	SCALE :
ALL DIMENSION ARE IN mm			A3		SHEET 25 OF 25