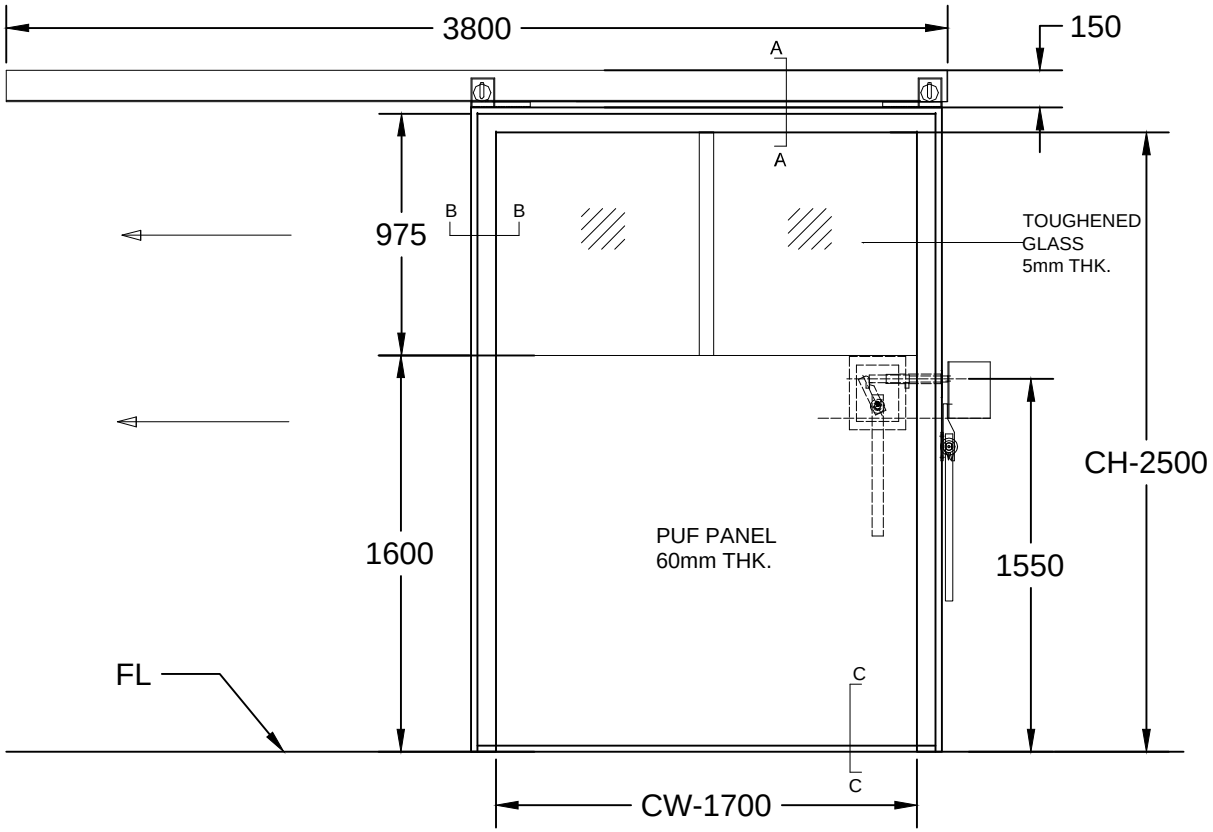

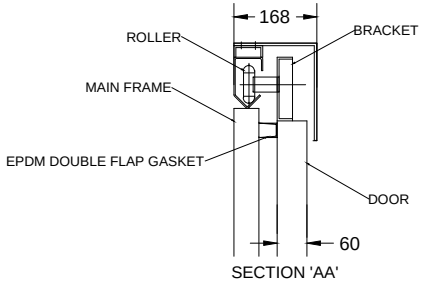

SECTION 'AA'

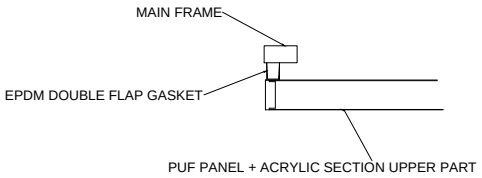

SECTION 'BB'

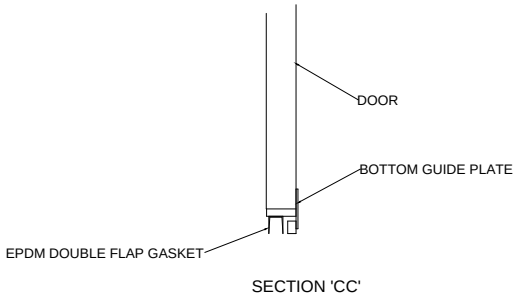

SECTION 'CC'

CLEAR WIDTH	CLEAR HEIGHT	QUANTITY	LOCATION
1700	2500	01	

DOOR TYPE- L.H.S

COLOR OF DOOR - RAL 9002(GREY WHITE)

This drawing & design is the property of NIHVA TECHNOLOGIES. Not to be sold or copied to any other concern.

TITLE: SLIDING DOOR 2

	SIGN	DATE
DRAWN	OMKAR	09/10/17
CHECK	SHEKHAR	09/10/17
REV.		
APPROVAL	SHEKHAR	09/10/17

If any queries contact : projects@nihva.com

ALL DIMENSION ARE IN mm

NIHVA TECHNOLOGIES PVT. LTD. PUNE
Tel : 020 66304033
Email:- info@nihva.com
Website:- www.nihva.com

CLIENT -

PROJECT -

SITE -

DWG. NO. : NIHVA/17-18/VDR/0135

SCALE: NTS | WT: | SHEET: 01 OF 01