1.THREE LEAF TELESCOPIC
GATE (6X2.1m) TRACK

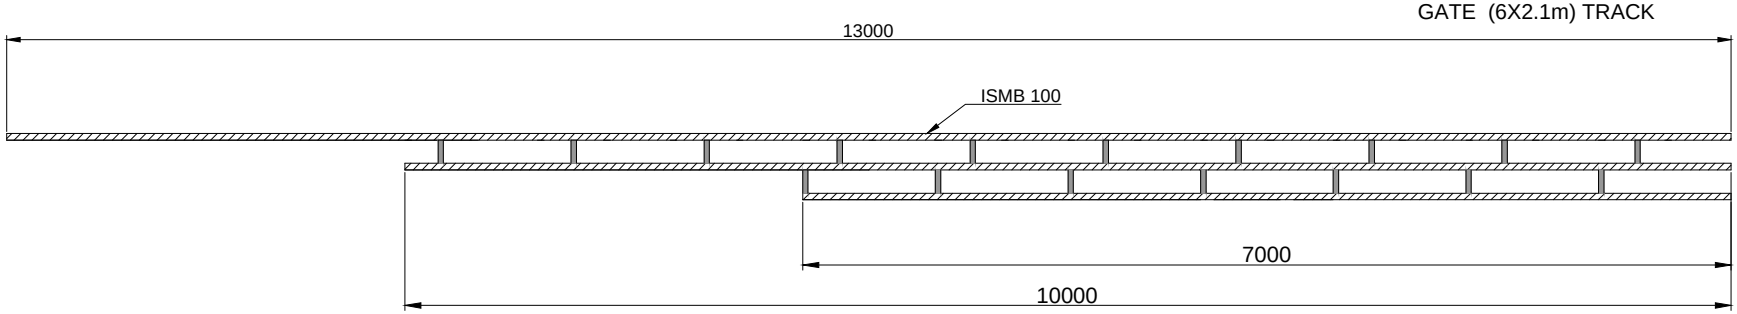

2.THREE LEAF TELESCOPIC
GATE (6X2.1m) TRACK

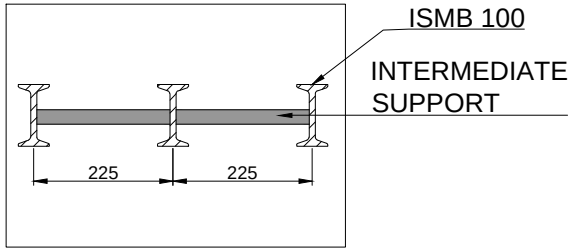

THREE LEAF TELESCOPIC
GATE TRACK

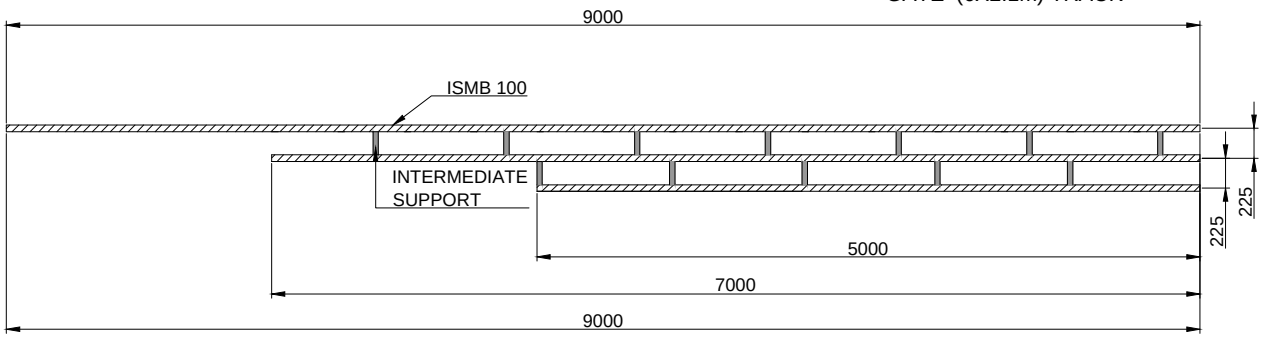

3.TWO LEAF TELESCOPIC
GATE (4X1.8m) TRACK

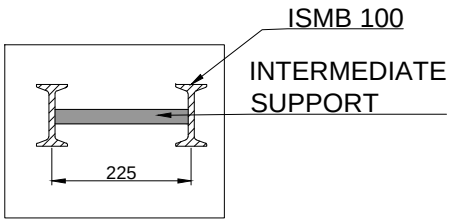

TWO LEAF TELESCOPIC
GATE TRACK

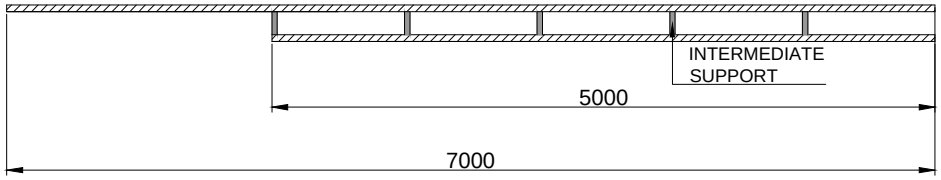

This drawing & design is the property of NIHVA TECHNOLOGIES. Not to be sold or copied to any other concern.

TITLE: TELESCOPIC GATE TRACK		
	NAME	DATE
DRAWN	OMKAR	26/10/17
CHECK	SHEKHAR	26/10/17
REV.		
APPROVAL	SHEKHAR	26/10/17
If any queries contact : projects@nihva.com		
ALL DIMENSION ARE IN mm		

NIHVA TECHNOLOGIES PVT. LTD.
NIHVA TECHNOLOGIES PVT. LTD. PUNE
Tel : 020 66304033
Email:- info@nihva.com
Website:- www.nihva.com

CLIENT - LUPIN LIMITED		
PROJECT -		
SITE LOCATION - MIHAN, NAGPUR		
DWG. NO. : NIHVA/17-18/0264		REV -0
SCALE: NTS	WT:	SHEET: 01 OF 01