


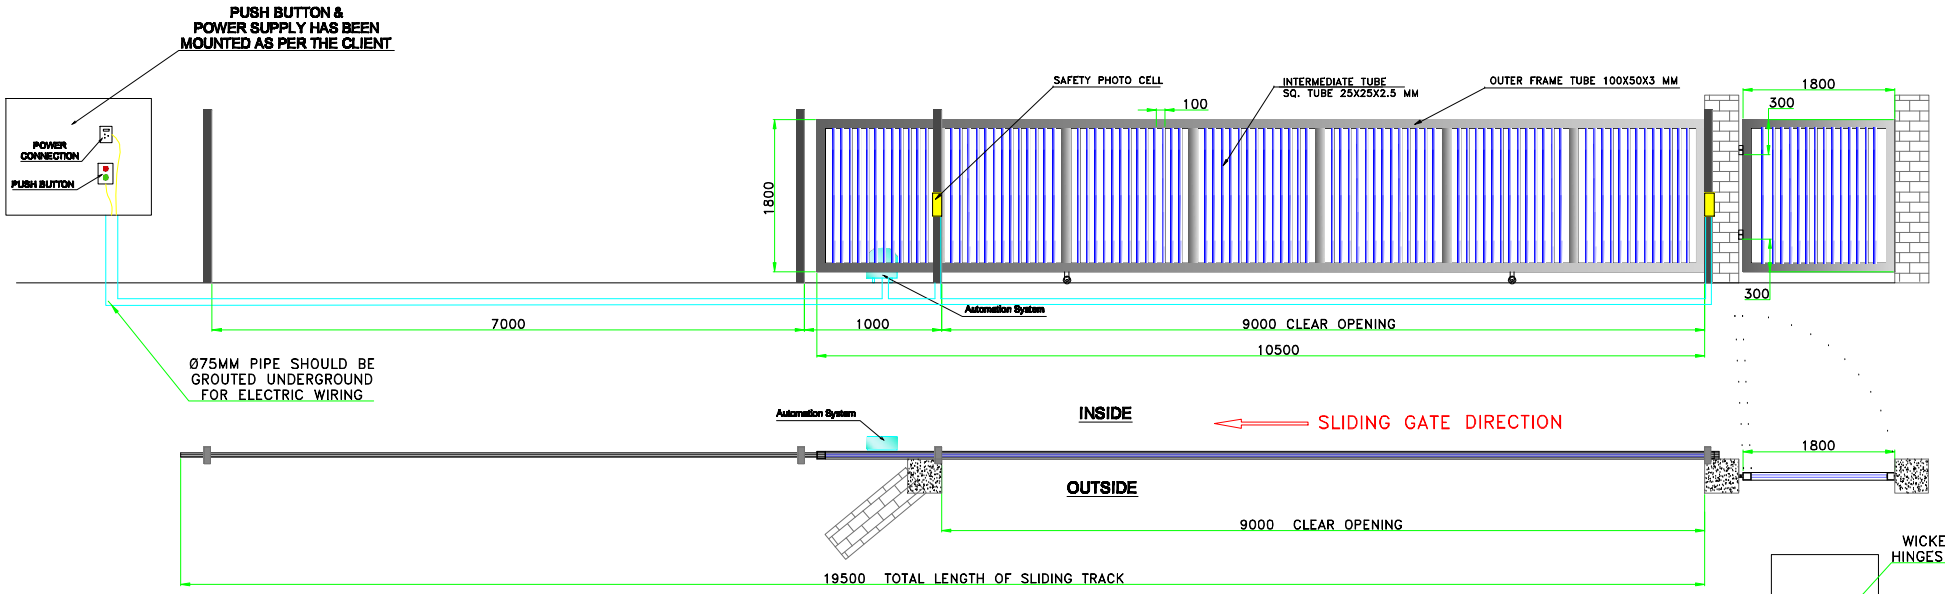


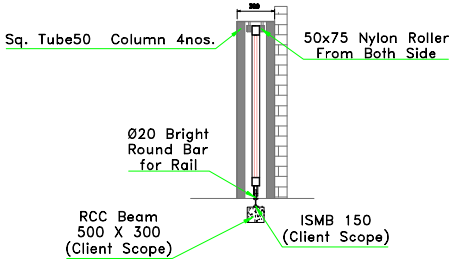


DETAIL 'A'

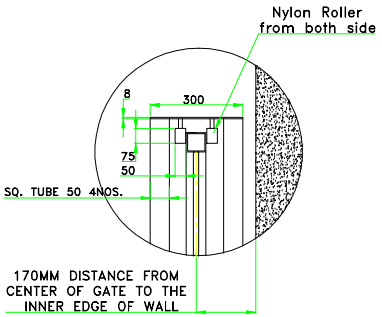

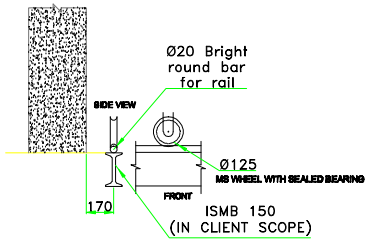

DETAIL 'B'

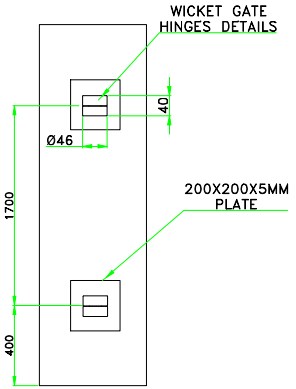

SLIDING GATE SIZE = 10500 (W) X 1800 (H), QTY = 1NOS.
CLEAR OPENING = 9,000 (W) X 1800 (H)
WICKET GATE SIZE = 1800(W) X 1800 (H), QTY = 1NOS.
OUTER FRAME = 100 X 50 X 3 mm
INNER FRAME = 25 X 25 X 2.5 mm
GAP B/W FRAME = 100 c/c
C'COLUMN(V) SUPPORT= 4 NOS.
Total weight of sliding gate= 625 kg (APPORX).

This drawing & designing is the property of NIHVA TECHNOLOGIES. Not be sold or copy to any other concern.

TITLE

SLIDING GATE

CLIENT APPROVAL

ALL DIMENSION ARE IN mm

	SIGN	DATE
DRAWN	ABHIJIT	22/01/15
CHECK	ANIL	22/01/15
REV.	05	
APPRD.		
MFG		
Ref. No.		

NIHVA TECHNOLOGY
PVT. LTD. PUNE
Tel : 020 66304033
Email:- info@nihva.com
Website:- www.nihva.com

CLIENT - REWARD CONSTRUCTION

PROJECT -INGRERSOLL RAND

SITE -NARODA , GUJRAT

DWG. NO. - NVA/REWARD/D1/R3

SCALE: 01 | WT: | SHEET: 01

If any queries contact : projects@nihva.com