
ASSA ABLOY

GENERAL DRAWING RR3000ISO

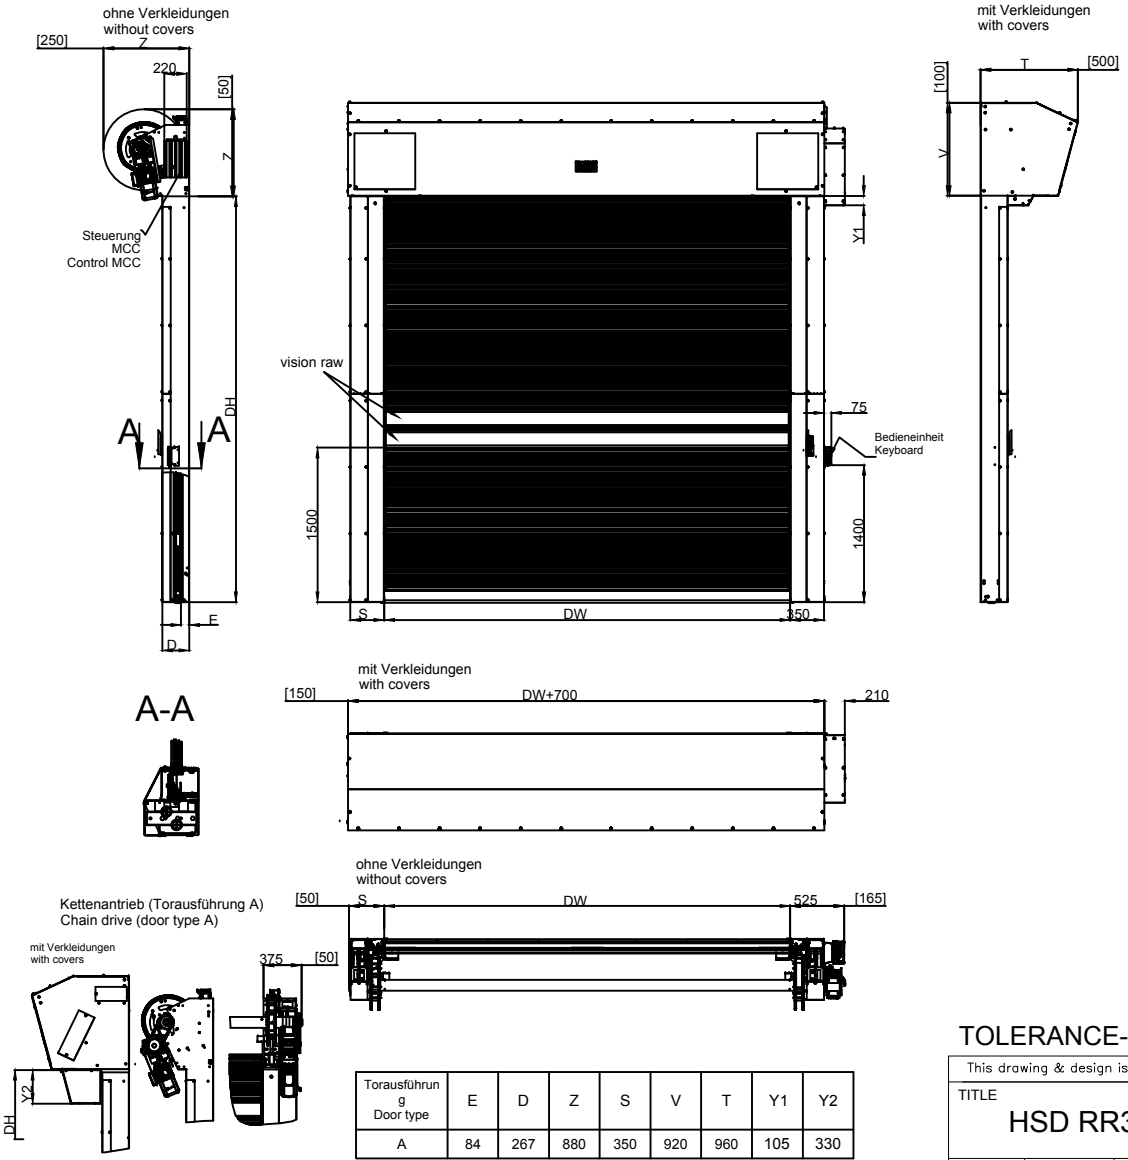

Torausführung Door type	E	D	Z	S	V	T	Y1	Y2
A	84	267	880	350	920	960	105	330

DOOR DIMENSION

SR NO	DOOR WIDTH (DW)	DOOR HEIGHT (DH)	QTY	REMARK
1	3000	3500	1 NO	SOUTH SIDE
2	3885	4500	1 NO	EAST SIDE
3	4500	4500	1 NO	EAST SIDE
4	3990	4000	1 NO	WEST SIDE
5	4000	4450	1 NO	WEST SIDE
6	4000	5000	1 NO	WEST SIDE
7	4000	4500	2 NOS	NORTH SIDE
8	6000	5990	1 NO	NORTH SIDE

TOLERANCE- ±5mm

REV NO	DATE	DRAWN	REMARK
R03	19.05.2020	P.A	REMARK ADDED DOOR DIMENSION CHANGE
R02	18.05.2020	P.A	VISION ROWS ADDED
R01	11.05.2020	P.A	DOOR DIMENSION CHANGE

This drawing & design is the property of NIHVA TECHNOLOGIES. Not to be sold or copied to any other concern.

TITLE: HSD RR3000ISO

	NAME	SIGN	DATE
DRAWN	P.A		09.05.2020
CHECK	G.J		09.05.2020
APPRD.			

NIHVA TECHNOLOGIES PVT. LTD.
NIHVA TECHNOLOGIES PVT. LTD. PUNE
Tel : 020 66304033
Email:- info@nihva.com
Website:- www.nihva.com

CLIENT - SCON

PROJECT - JOHN DEERE

SITE LOCATION - PUNE

If any queries contact : design@nihva.com

DWG. NO. : NIHVA/20-21/0005/R03

REV- R03

ALL DIMENSION ARE IN mm

SCALE: NTS

WT:

SHEET: 01 OF 01