
MMC DOOR TECH SERVICES PVT LTD
#4,3rd Lane,Habibullah Road,
T-Nagar,Chennai-600 017.
Ph :044-42122770,71,72 Fax :42122774
E-mail :mmc@mmcgroup.in

Project :PYRAMID SKYLIGHT	***Sales Executive : Mr. Murugan***	***Dwg.Ref.No :MQ 20-158***
Glass Tck : 15.52mm LAMI T/G	***Architect Name***	***Date :24-10-24***
Prepared By M.Vadivel	***Checked by***	***Approved by***

SKYLIGH- OPTION-1

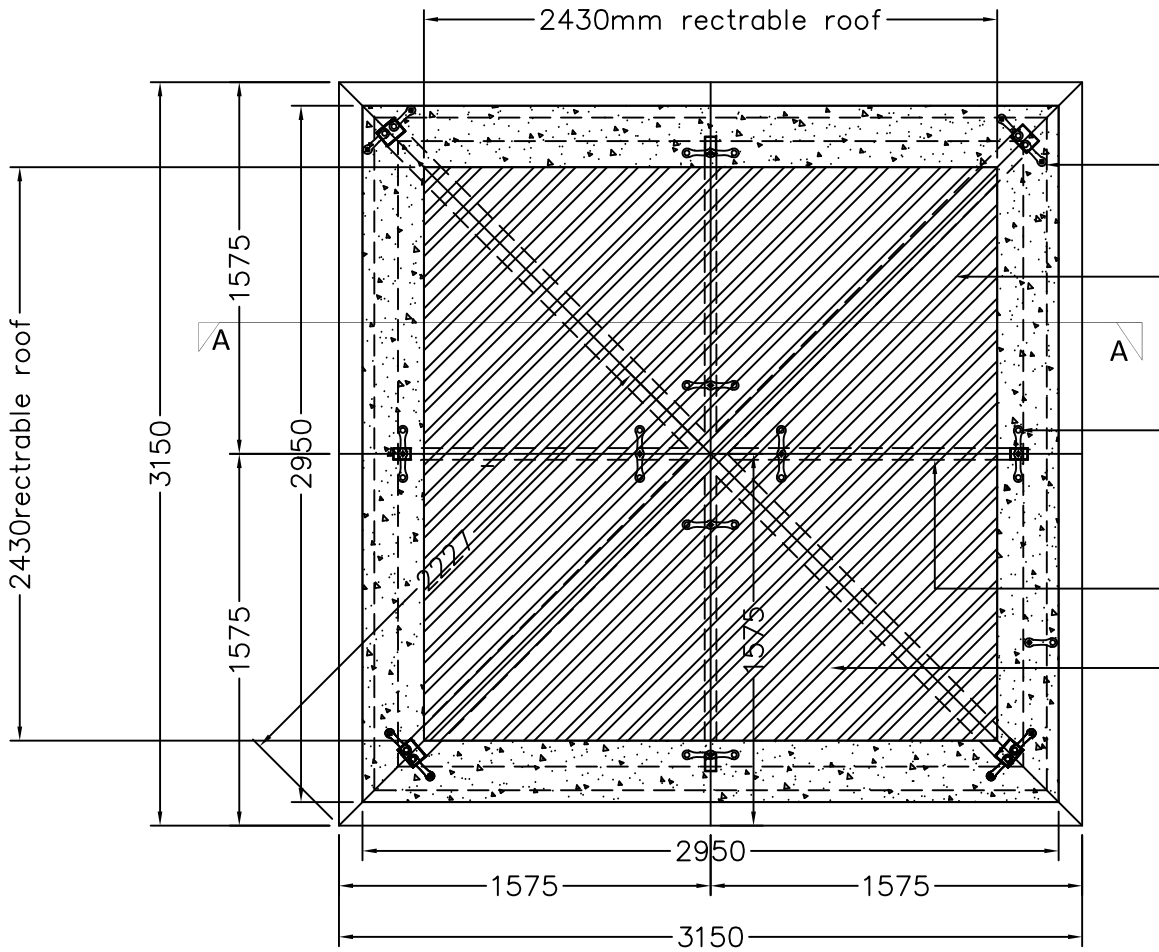

SKYLIGHT-PLAN

SINGLE ARM TRUSS SPIDER


15.52mm thk laminated glass

TWO ARM TRUSS SPIDER

STEEL STRUCTURE

this one area auto sliding roof area



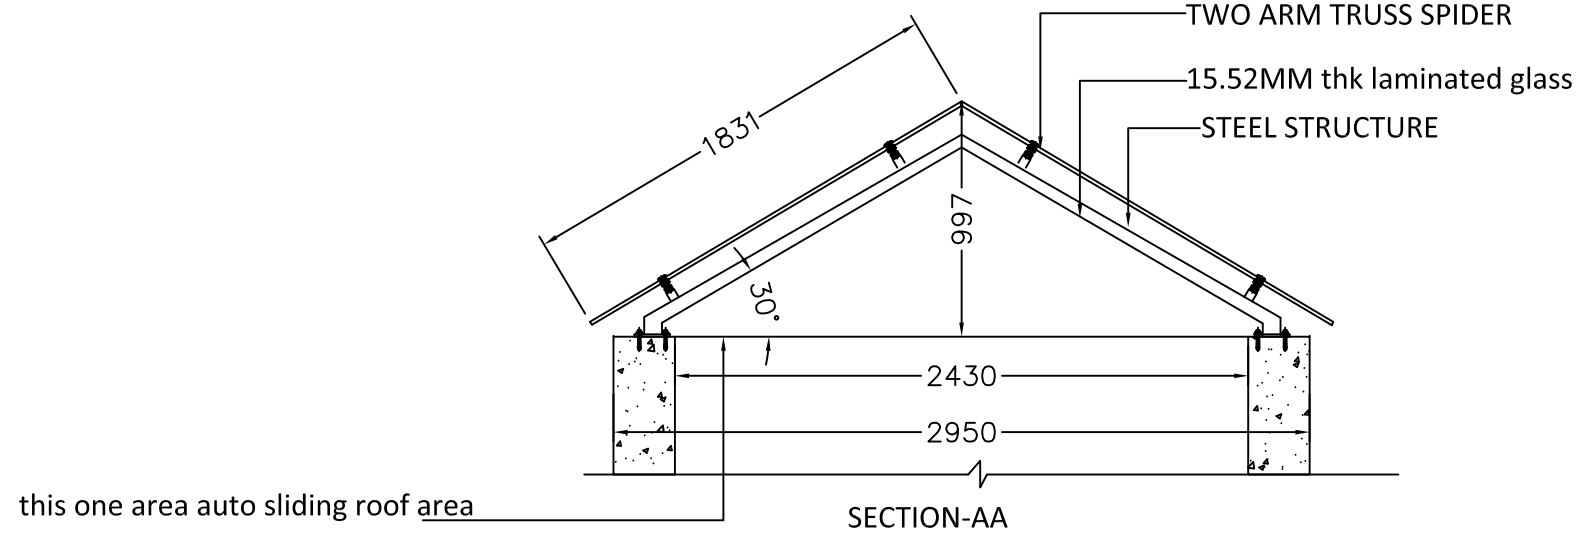

SECTION-AA

All Dimensions are in 'mm'