

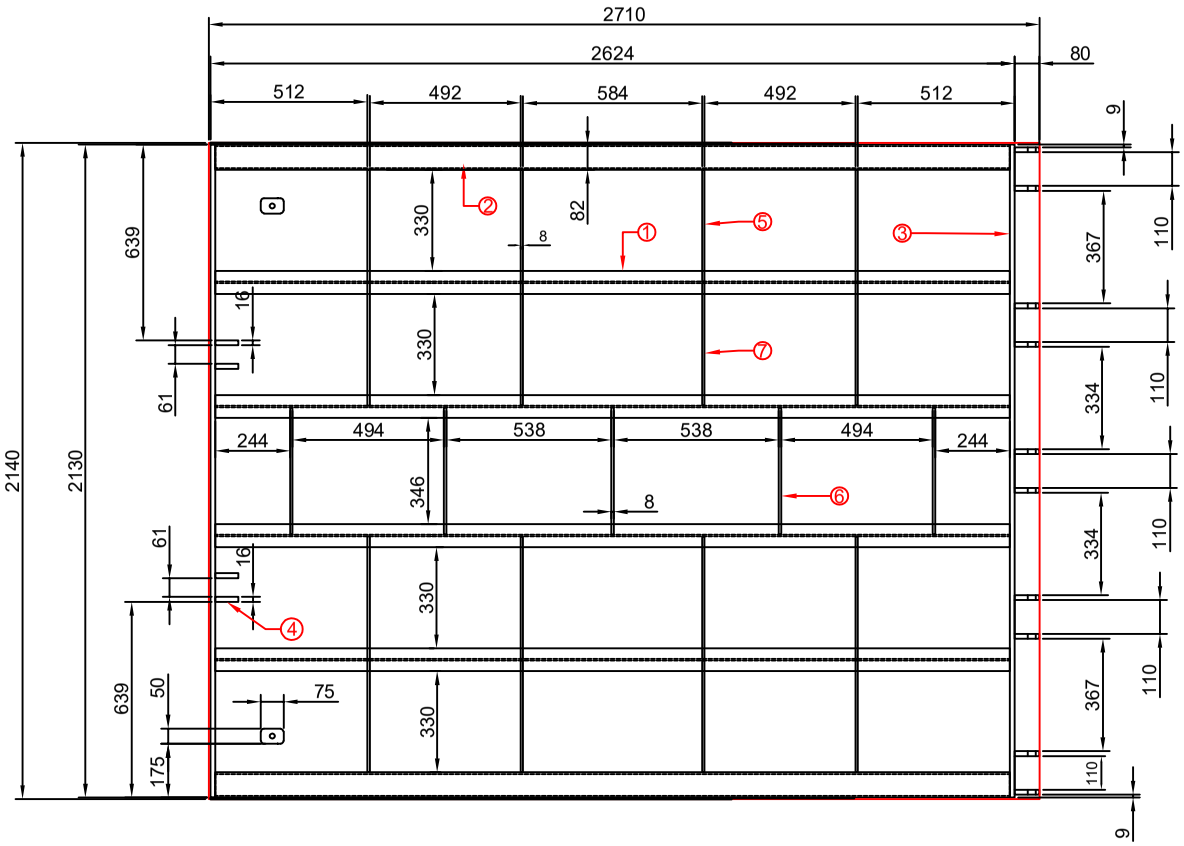


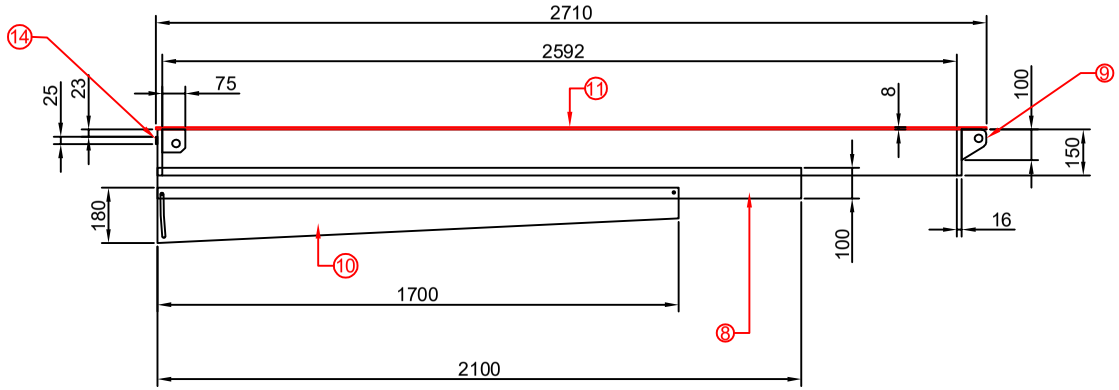

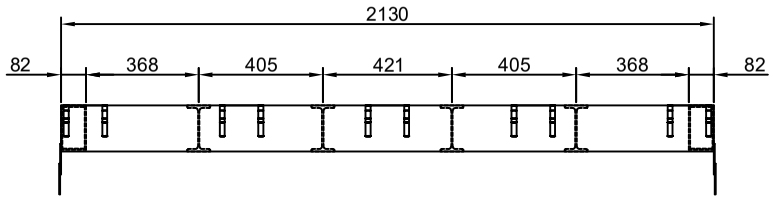

BOM			
SL NO.	DESCRIPTION	SPECIFICATION	QTY
1	ISMB	150X75X2592L	4NOS
2	MS RECT.TUBE	145X82X2592X5.4THK	2NOS
3	MS FLAT	150X16X2130L	2NOS
4	CYLINDER MTG BKT	75X75X16THK	4NOS
5	MS FLAT	150X8X365L	8NOS
6	MS FLAT	150X8X416L	5NOS
7	MS FLAT	150X8X400	8NOS
8	L BEND	100X2100X3THK	2NOS
9	HOLDING BKT	100X80X16THK	10NOS
10	SIDE COVER	180X1700X3THK	2NOS
11	CHEQ.SHEET	2140X2710X8	1NO
12	EYE BOLT	M16XSTD WITH NUT	3NOS
13	EYE BOLT MTNG BKT	50X75X16	3NOS
14	MS FLAT	25X5X100	20

This drawing & design is the property of NIHVA TECHNOLOGIES. Not to be sold or copied to any other concern.

TITLE: DECK FRAME

NIHVA
NIHVA TECHNOLOGIES PVT. LTD.

NIHVA TECHNOLOGIES PVT. LTD. PUNE
Tel : 020 66304033
Email:- info@nihva.com
Website:- www.nihva.com

	NAME	DATE	SIGN
DRAWN	SUJATA	30/12/2021	
CHECK	G.PATIL	30/12/2021	
APPRD.	A.K	30/12/2021	

CLIENT -
LOCATION -
PRODUCT -
If any queries contact : design@nihva.com
DWG NO:-NIHVA/21-22/MFG/008
REV- 0
ALL DIMENSION ARE IN mm
SCALE: NTS
SCALE:-- 1:1
SHEET: 01 OF 01

Rev No.	Revision	Date	Revised By