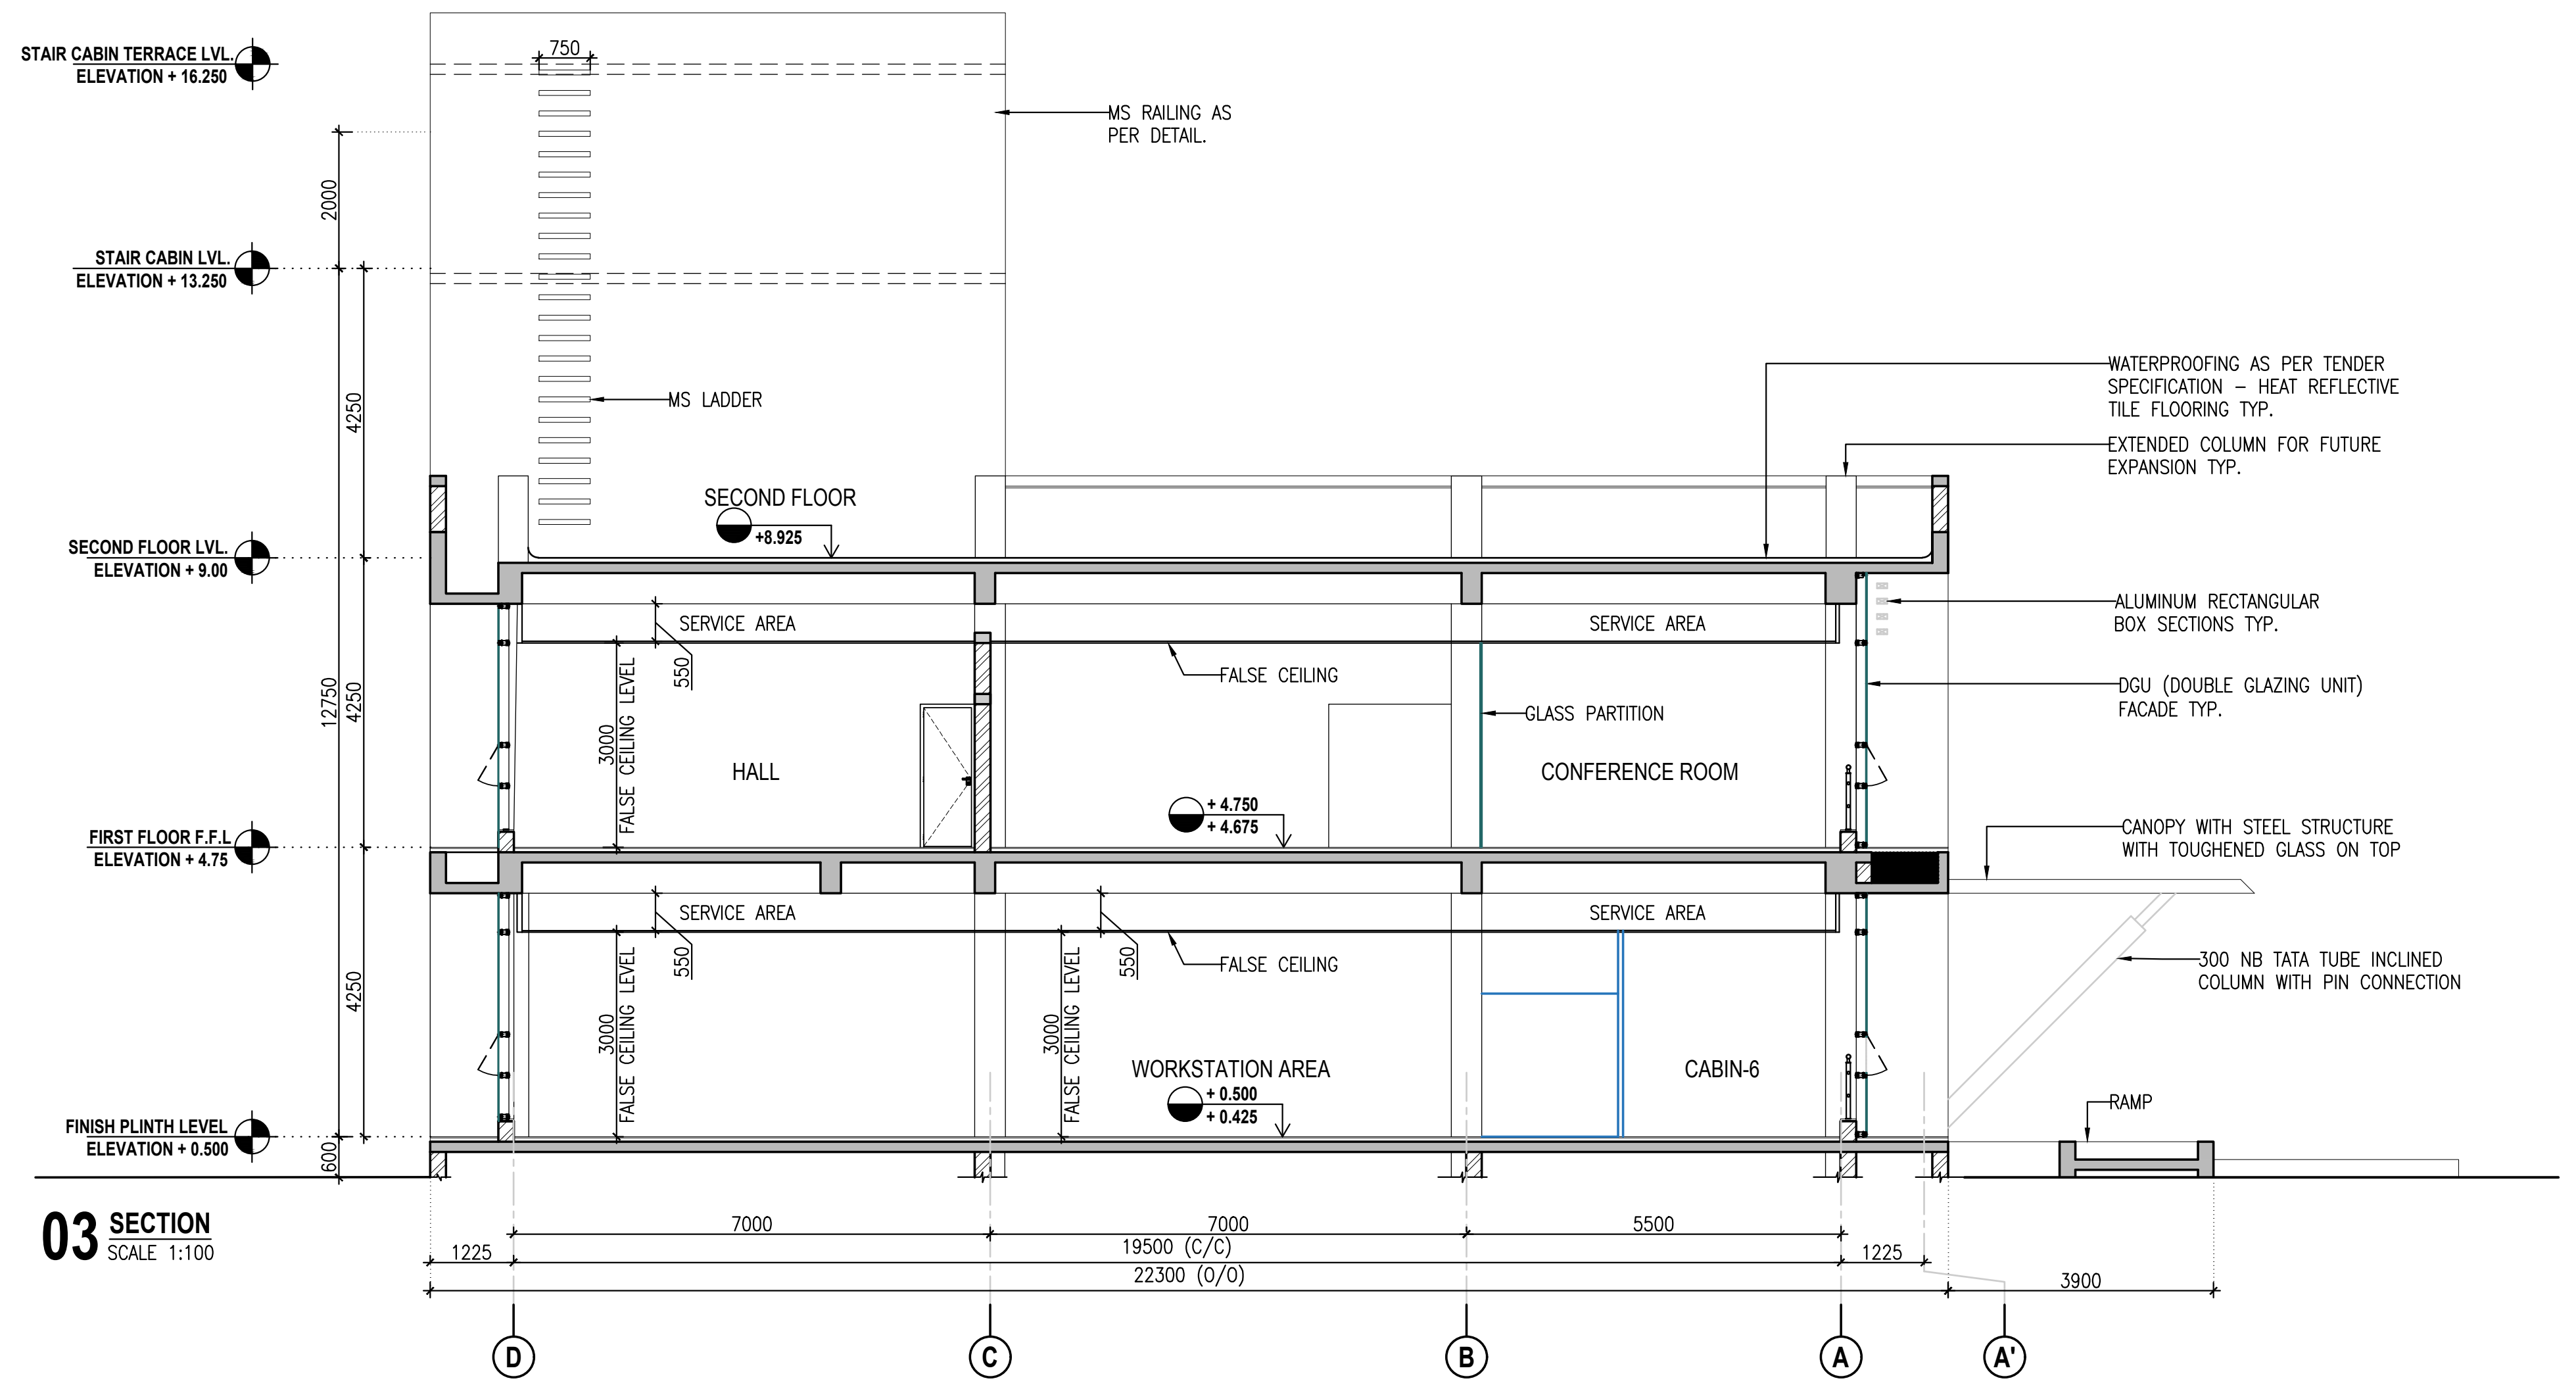
STAIR CABIN TERRACE LVL.
ELEVATION + 16.250
STAIR CABIN LVL.
ELEVATION + 13.250
SECOND FLOOR LVL.
ELEVATION + 9.00
FIRST FLOOR F.F.L
ELEVATION + 4.75
FINISH PLINTH LEVEL
ELEVATION + 0.500
750
MS RAILING AS PER DETAIL.
MS LADDER
2000
4250
12750
600
SECOND FLOOR
+8.925
WATERPROOFING AS PER TENDER SPECIFICATION – HEAT REFLECTIVE TILE FLOORING TYP.
EXTENDED COLUMN FOR FUTURE EXPANSION TYP.
ALUMINUM RECTANGULAR BOX SECTIONS TYP.
DGU (DOUBLE GLAZING UNIT) FACADE TYP.
CANOPY WITH STEEL STRUCTURE WITH TOUGHENED GLASS ON TOP
300 NB TATA TUBE INCLINED COLUMN WITH PIN CONNECTION
RAMP
SERVICE AREA
FALSE CEILING
GLASS PARTITION
550
3000
FALSE CEILING LEVEL
HALL
CONFERENCE ROOM
+ 4.750
+ 4.675
WORKSTATION AREA
CABIN-6
+ 0.500
+ 0.425
7000
7000
5500
1225
19500 (C/C)
1225
22300 (O/O)
3900
D
C
B
A
A'

03 SECTION
SCALE 1:100

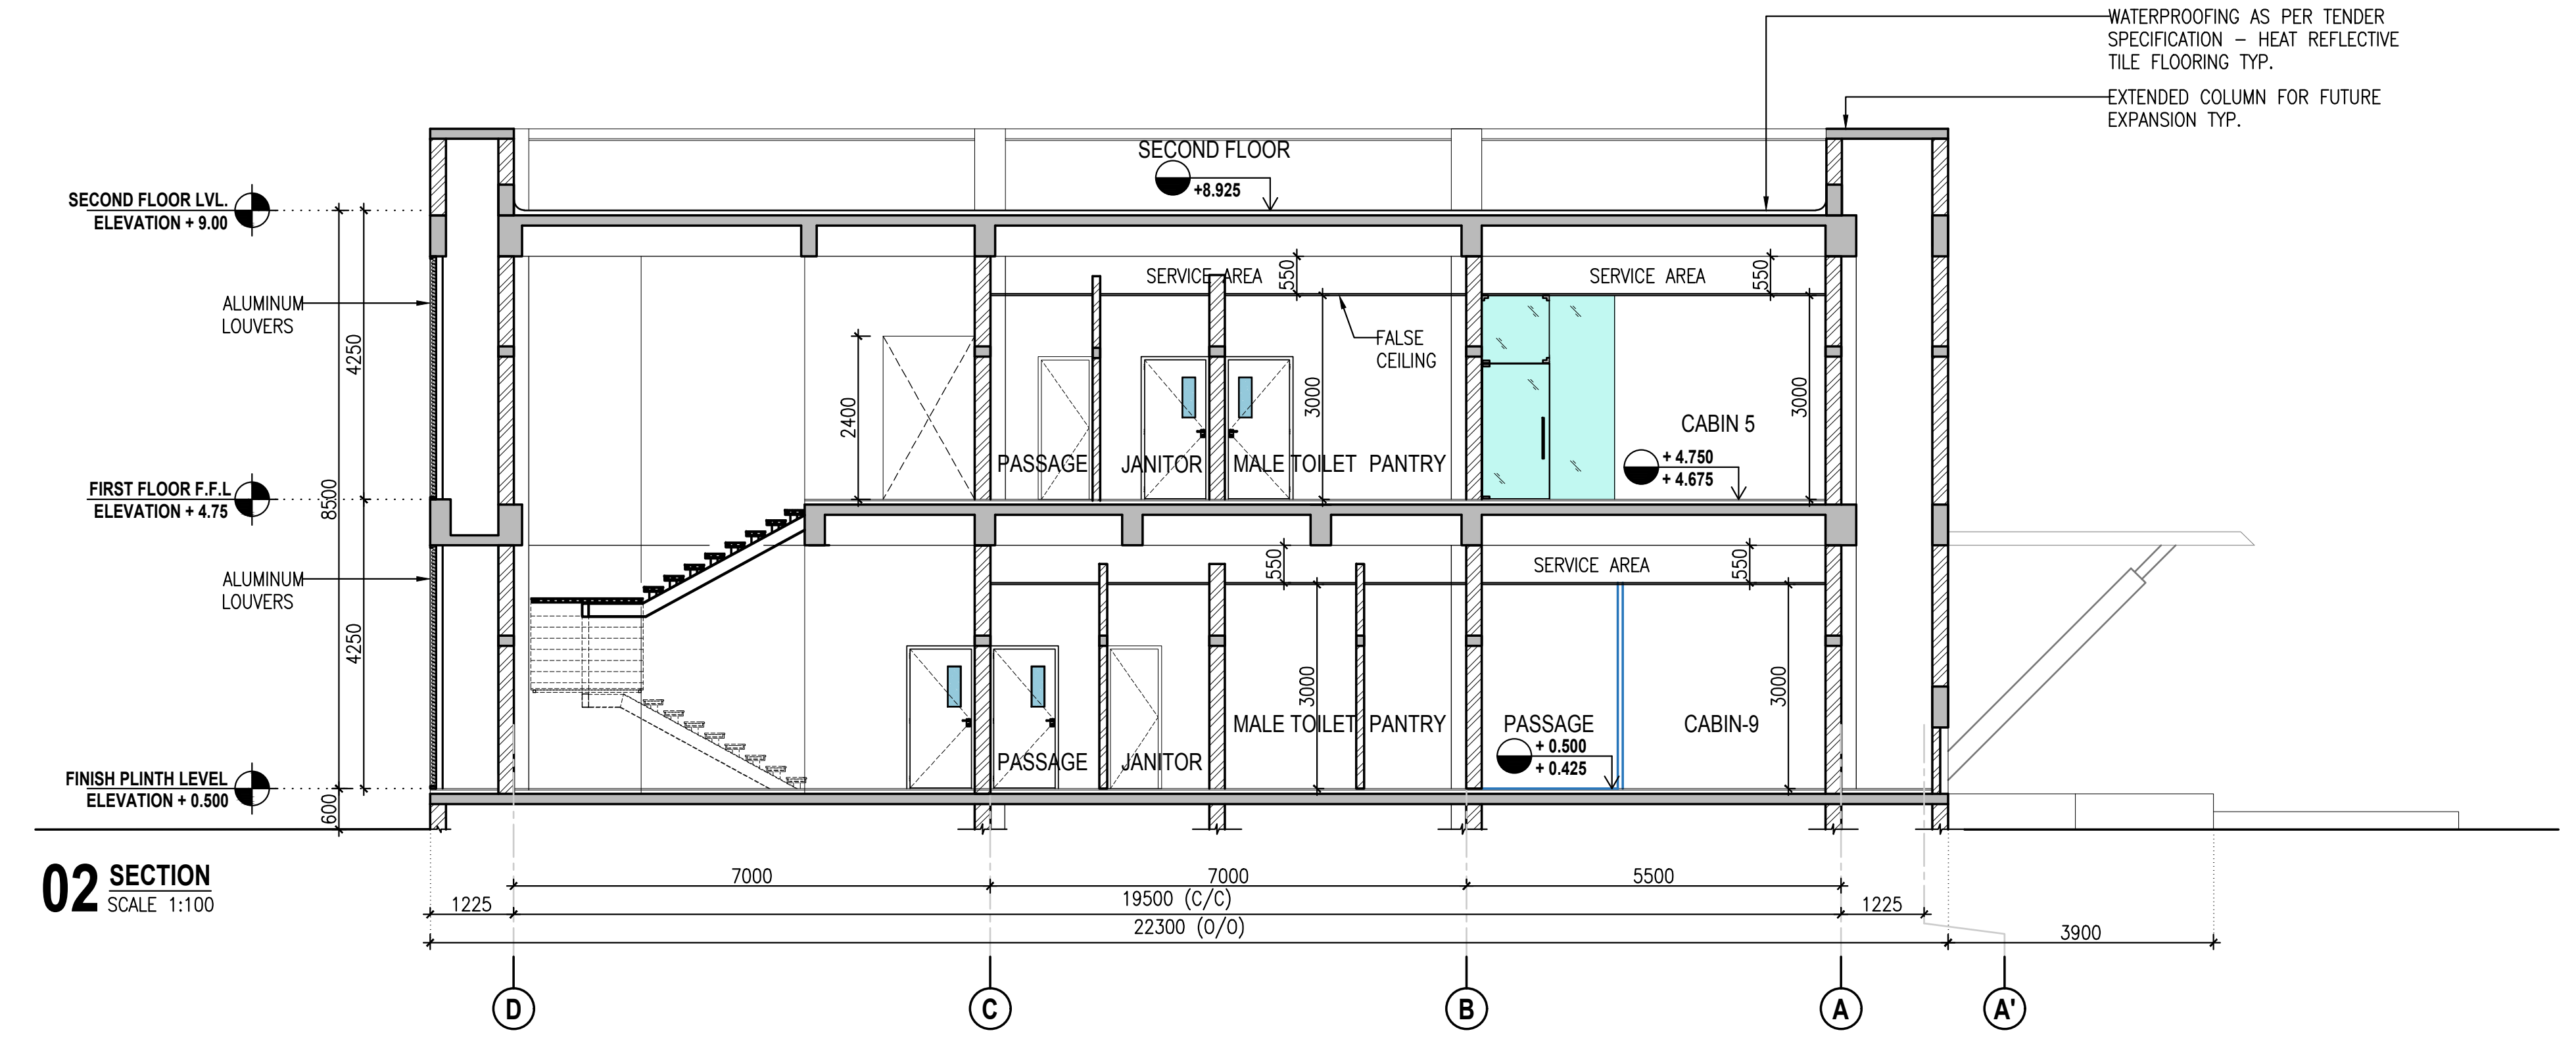
SECOND FLOOR LVL.
ELEVATION + 9.00
FIRST FLOOR F.F.L
ELEVATION + 4.75
FINISH PLINTH LEVEL
ELEVATION + 0.500
ALUMINUM LOUVERS
ALUMINUM LOUVERS
4250
8500
600
2400
WATERPROOFING AS PER TENDER SPECIFICATION – HEAT REFLECTIVE TILE FLOORING TYP.
EXTENDED COLUMN FOR FUTURE EXPANSION TYP.
SECOND FLOOR
+8.925
SERVICE AREA
FALSE CEILING
550
3000
PASSAGE
JANITOR
MALE TOILET
PANTRY
CABIN 5
+ 4.750
+ 4.675
PASSAGE
JANITOR
MALE TOILET
PANTRY
PASSAGE
CABIN-9
+ 0.500
+ 0.425
7000
7000
5500
1225
19500 (C/C)
1225
22300 (O/O)
3900
D
C
B
A
A'

02 SECTION
SCALE 1:100

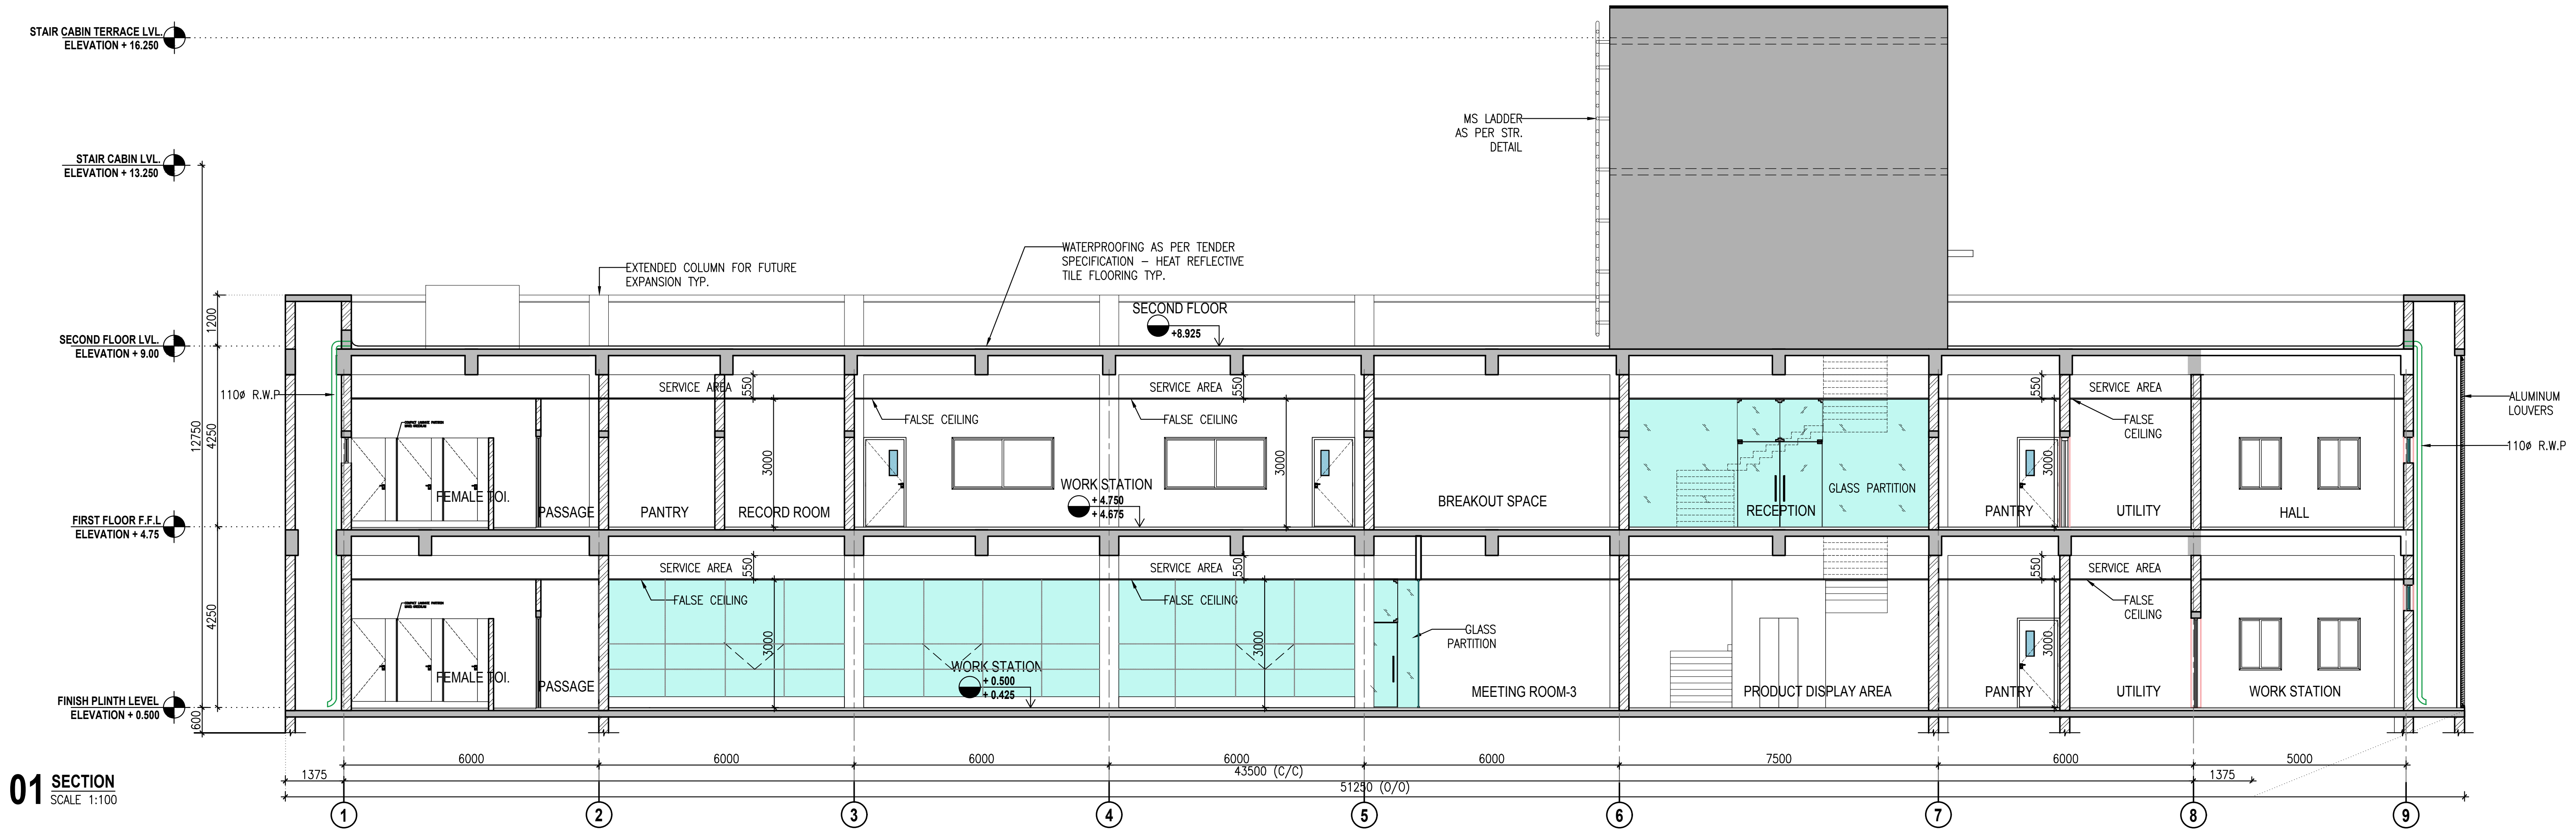
STAIR CABIN TERRACE LVL.
ELEVATION + 16.250
STAIR CABIN LVL.
ELEVATION + 13.250
SECOND FLOOR LVL.
ELEVATION + 9.00
FIRST FLOOR F.F.L
ELEVATION + 4.75
FINISH PLINTH LEVEL
ELEVATION + 0.500
1200
12750
4250
600
110ø R.W.P
EXTENDED COLUMN FOR FUTURE EXPANSION TYP.
WATERPROOFING AS PER TENDER SPECIFICATION – HEAT REFLECTIVE TILE FLOORING TYP.
MS LADDER AS PER STR. DETAIL
SECOND FLOOR
+8.925
SERVICE AREA
FALSE CEILING
550
3000
FEMALE TOI.
PASSAGE
PANTRY
RECORD ROOM
WORK STATION
+ 4.750
+ 4.675
BREAKOUT SPACE
RECEPTION
GLASS PARTITION
PANTRY
UTILITY
HALL
FEMALE TOI.
PASSAGE
WORK STATION
+ 0.500
+ 0.425
GLASS PARTITION
MEETING ROOM-3
PRODUCT DISPLAY AREA
PANTRY
UTILITY
WORK STATION
ALUMINUM LOUVERS
110ø R.W.P
1375
6000
6000
6000
6000
6000
7500
6000
5000
1375
43500 (C/C)
51250 (O/O)
1
2
3
4
5
6
7
8
9

01 SECTION
SCALE 1:100

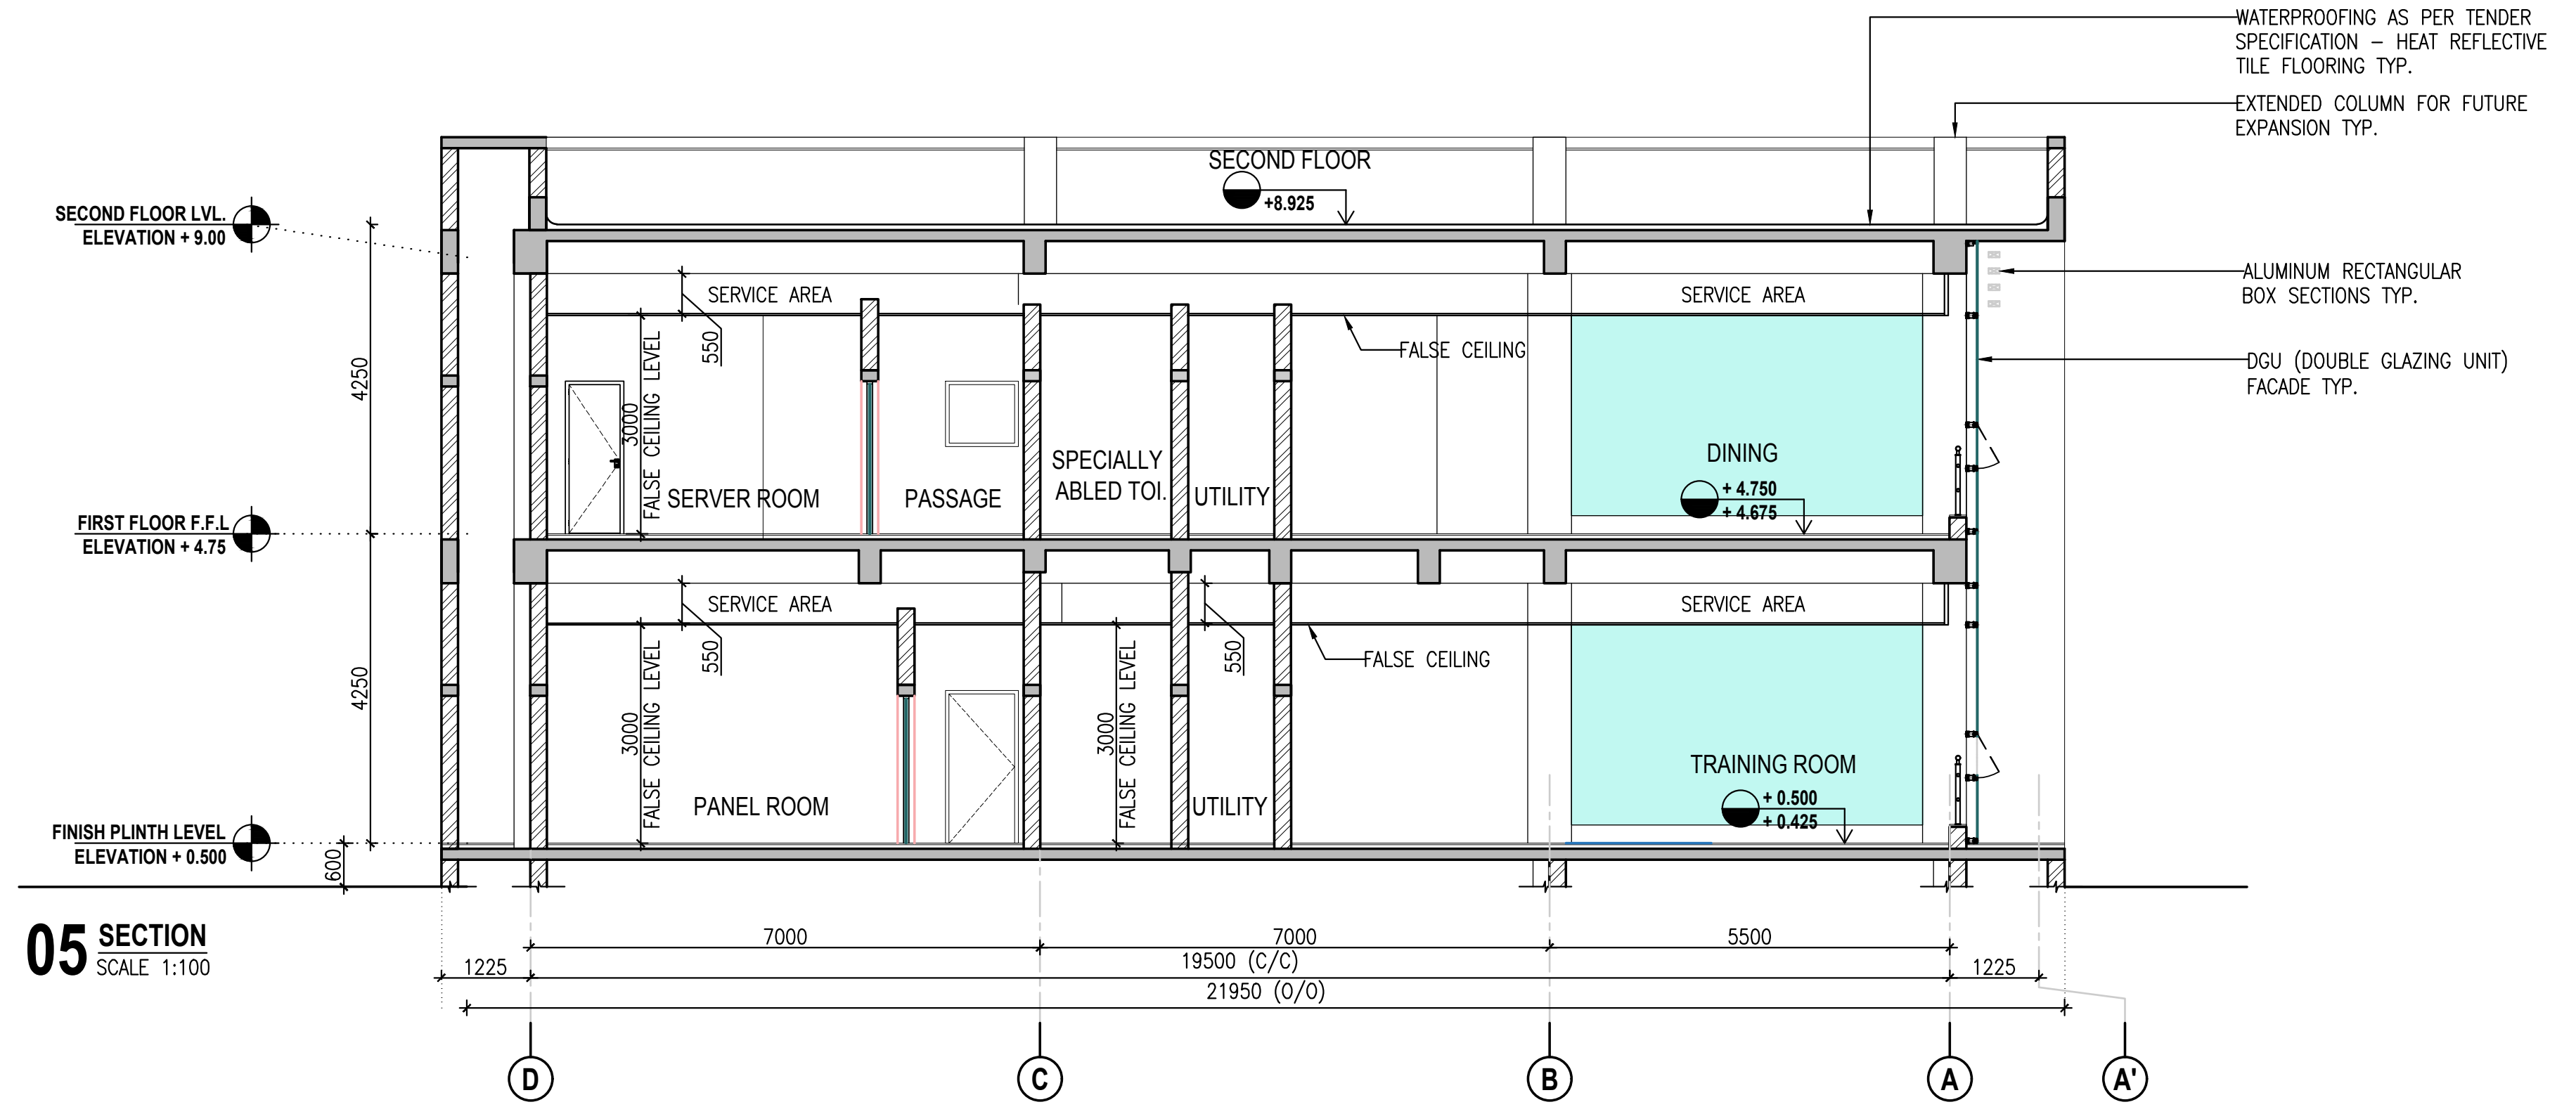
SECOND FLOOR LVL.
ELEVATION + 9.00
FIRST FLOOR F.F.L
ELEVATION + 4.75
FINISH PLINTH LEVEL
ELEVATION + 0.500
4250
4250
600
WATERPROOFING AS PER TENDER SPECIFICATION – HEAT REFLECTIVE TILE FLOORING TYP.
EXTENDED COLUMN FOR FUTURE EXPANSION TYP.
ALUMINUM RECTANGULAR BOX SECTIONS TYP.
DGU (DOUBLE GLAZING UNIT) FACADE TYP.
SECOND FLOOR
+8.925
SERVICE AREA
FALSE CEILING
550
3000
FALSE CEILING LEVEL
SERVER ROOM
PASSAGE
SPECIALLY ABLED TOI.
UTILITY
DINING
+ 4.750
+ 4.675
PANEL ROOM
UTILITY
TRAINING ROOM
+ 0.500
+ 0.425
7000
7000
5500
1225
19500 (C/C)
1225
21950 (O/O)
D
C
B
A
A'

05 SECTION
SCALE 1:100

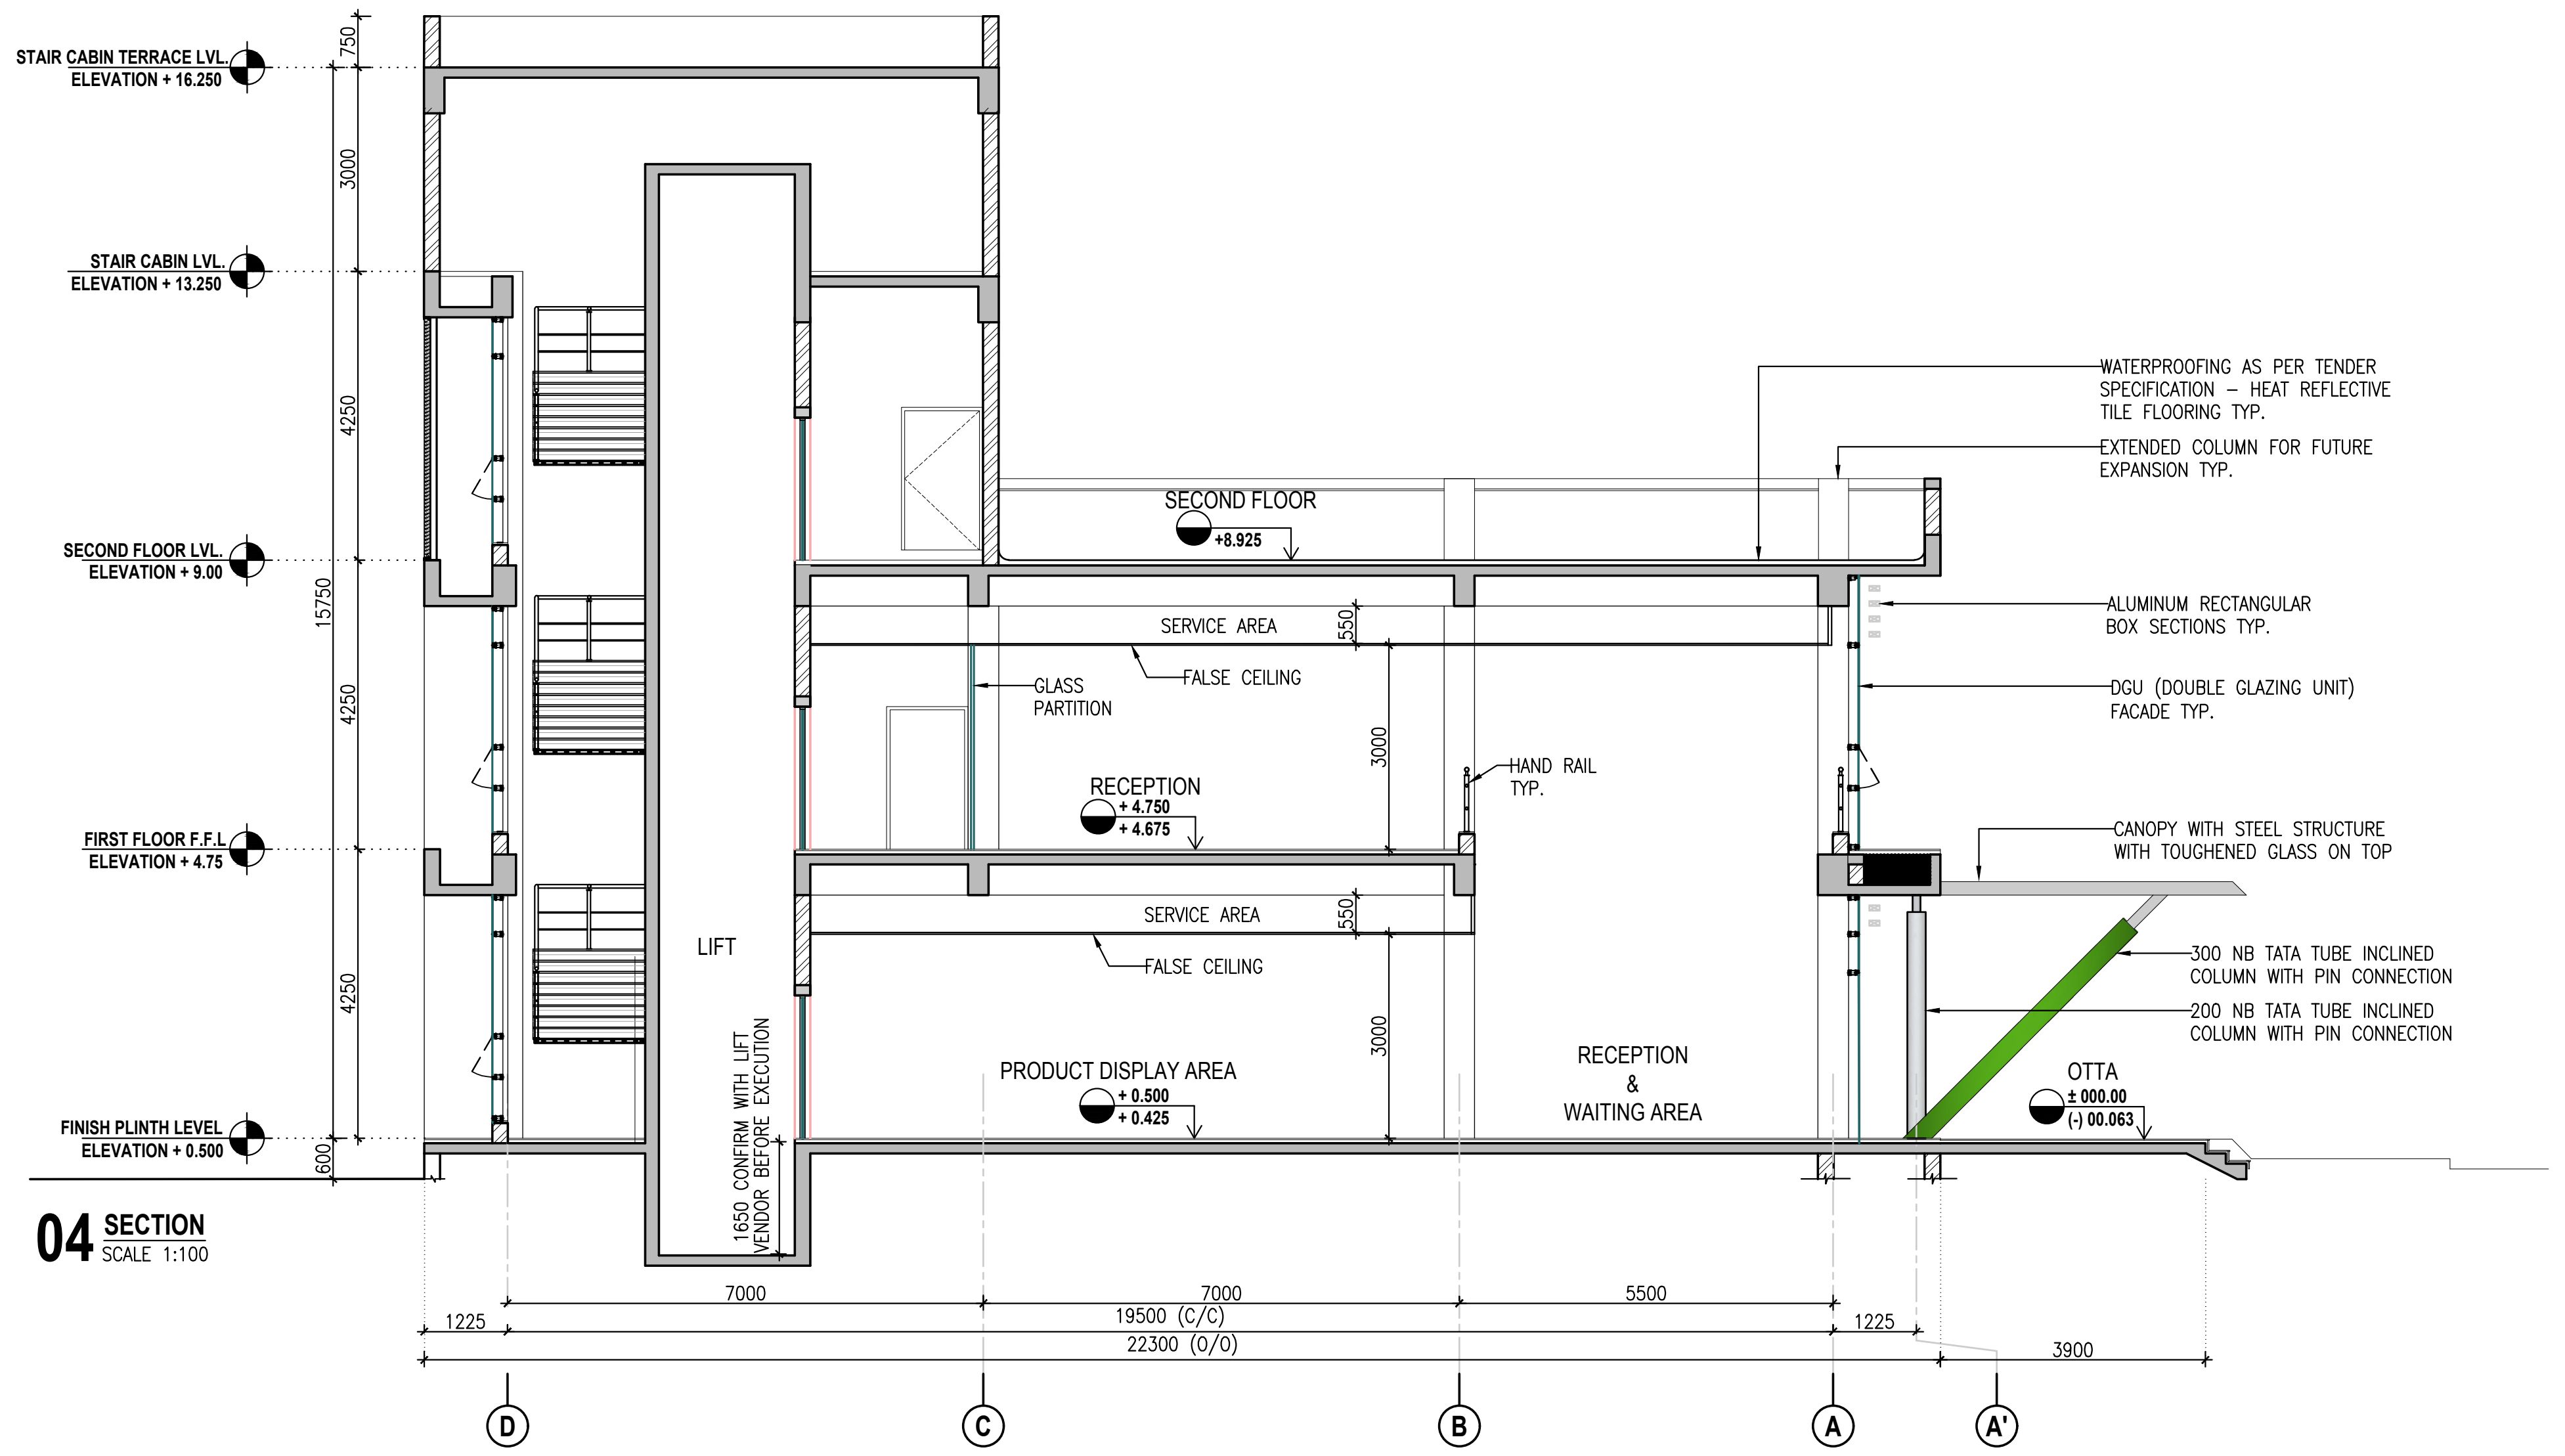
STAIR CABIN TERRACE LVL.
ELEVATION + 16.250
STAIR CABIN LVL.
ELEVATION + 13.250
SECOND FLOOR LVL.
ELEVATION + 9.00
FIRST FLOOR F.F.L
ELEVATION + 4.75
FINISH PLINTH LEVEL
ELEVATION + 0.500
750
3000
4250
15750
4250
4250
600
WATERPROOFING AS PER TENDER SPECIFICATION – HEAT REFLECTIVE TILE FLOORING TYP.
EXTENDED COLUMN FOR FUTURE EXPANSION TYP.
ALUMINUM RECTANGULAR BOX SECTIONS TYP.
DGU (DOUBLE GLAZING UNIT) FACADE TYP.
SECOND FLOOR
+8.925
SERVICE AREA
FALSE CEILING
GLASS PARTITION
550
3000
RECEPTION
+ 4.750
+ 4.675
HAND RAIL TYP.
CANOPY WITH STEEL STRUCTURE WITH TOUGHENED GLASS ON TOP
300 NB TATA TUBE INCLINED COLUMN WITH PIN CONNECTION
200 NB TATA TUBE INCLINED COLUMN WITH PIN CONNECTION
LIFT
1650 CONFIRM WITH LIFT VENDOR BEFORE EXECUTION
PRODUCT DISPLAY AREA
+ 0.500
+ 0.425
RECEPTION & WAITING AREA
OTTA
± 000.00
(-) 00.063
7000
7000
5500
1225
19500 (C/C)
1225
22300 (O/O)
3900
D
C
B
A
A'

04 SECTION
SCALE 1:100

IMPORTANT NOTE :

1. ± 0.000 LEVEL CORRESPONDS TO + 365.50 LEVEL

THIS DRAWING & DESIGN IS THE SOLE PROPERTY OF VMS & SHALL NOT BE COPIED, TRACED OR REPRODUCED BY ANY MEANS WITHOUT PRIOR WRITTEN CONSENT OF THE FIRM.

GENERAL NOTES :

1. ALL THE DIMENSIONS ARE UNFINISHED DIMENSIONS.
2. ALL DIMENSIONS ARE IN MM AND LEVELS ARE IN MT, UNLESS OTHERWISE MENTIONED.
3. ALL THE DIMENSIONS SHALL BE READ & NOT TO BE MEASURED.
4. IN CASE OF ANY DISCREPANCY, BRING IT TO THE NOTICE OF THE ARCHITECT IMMEDIATELY.
5. DETAIL DRAWING PRECEDES THE GENERAL DRAWING

STANDARD DRAWING SYMBOLS:

+ FINISHED LEVEL
+ UNFINISHED LEVEL

01 SECTION SYMBOL
UPPER HALF INDICATES DIAGRAM NO. (NUMERICAL VALUE) IN DRAWING SHEET & LOWER HALF INDICATES DRAWING NO.

04 ELEVATION SYMBOL
UPPER HALF INDICATES DIAGRAM NO. IN DRAWING SHEET & LOWER HALF INDICATES DRAWING NO.

W100 A000 WINDOW SYMBOL
UPPER HALF INDICATES WINDOW NO. & LOWER HALF INDICATES DRAWING NO.

D100 A000 DOOR SYMBOL
UPPER HALF INDICATES DOOR NO. & LOWER HALF INDICATES DRAWING NO.

GRAPHIC LEGEND :

▨	230THK. FLY ASH BRICK WALL 3MT. HT.	—	PUFF PANEL PARTITION
■	RCC COLUMN CUT IN PLAN.	▩	115THK. FLY ASH BRICK WALL 2.1MT. HT.

NOTE : FOR CIVIL CONTRACTORS

1. CIVIL CONTRACTOR–VENDOR NEEDS TO SUBMIT DETAILED SHOP DRAWINGS WITH NECESSARY JUNCTION & FIXING DETAILS FOR GLAZING, EXTERIOR CLADDING, GRILL–LOUVERS, PARTITIONS, FALSE CEILING, DOOR–WINDOWS, ETC. TO CLIENTS/ CONSULTANTS & GET IT APPROVED PRIOR TO THE EXECUTION.
2. BASED ON SCHEMATIC DRAWING PROVIDED BY CONSULTANT, CIVIL CONTRACTOR–VENDOR NEEDS TO PROVIDE DETAILED SHOP DRAWINGS OR ANY SPECIFIC SHOP DRAWINGS & SAMPLES ASK BY CLIENT/CONSULTANTS & GET IT APPROVED PRIOR TO THE EXECUTION.
3. NEED TO CONSIDER SUPPORTING PRIMARY & SECONDARY STRUCTURE FOR ABOVE MENTION ITEMS.

IMPORTANT NOTE

1. FUTURE EXPANSION IS CONSIDERED FOR GRID B TO D, 1 TO 8.

FOR TENDER

NO.	DATE	DESCRIPTION	DRAWN BY	CHECKED BY
R1	03-12-22	REVISED AS MARKED & GENERALLY REVISED	V.CHAUHAN	DD.

REVISION HISTORY

KEY PLAN
SCALE : N.T.S.

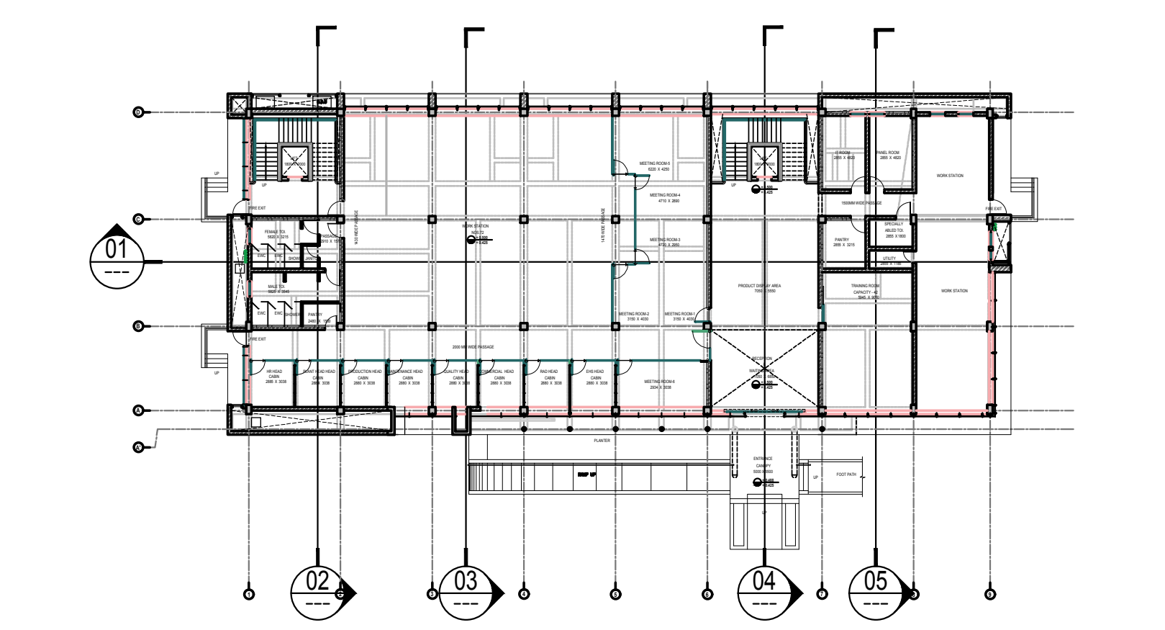
01
02
03
04
05

REFERENCE DRAWINGS :

01. ARCHITECTURAL : A.5.101, A.5.202, A.5.301
02. STRUCTURAL :
03. HVAC : -
04. ELECTRICAL : -
05. UTILITIES : -

SECTIONS
ADMIN BUILDING
AGRAWAL METAL WORKS(P) LTD.

PROJECT NO.	SCALE :	DRAWN :	NAMRATA
3824	AS NOTED	CHECKED:	DARSH
	DATE :	APPROVED:	DARSH
	02-12-2024	COORDINATION CHECKED:	DARSH

VMS ENGINEERING & DESIGN SERVICES (P) LTD.
CHITRAKOOT FLATS, B/H TIMES OF INDIA, OFF ASHRAM ROAD,
AHMEDABAD-380 009. PHONE: +91 (079) 2658-8829, 4023-6236
WWW.VMSCONSULTANTS.COM
ENGINEERING + ARCHITECTURE

SHEET SIZE	DRAWING NO.	TENDER	REVISION:
600x 1200	T.A.5.201	T	R0