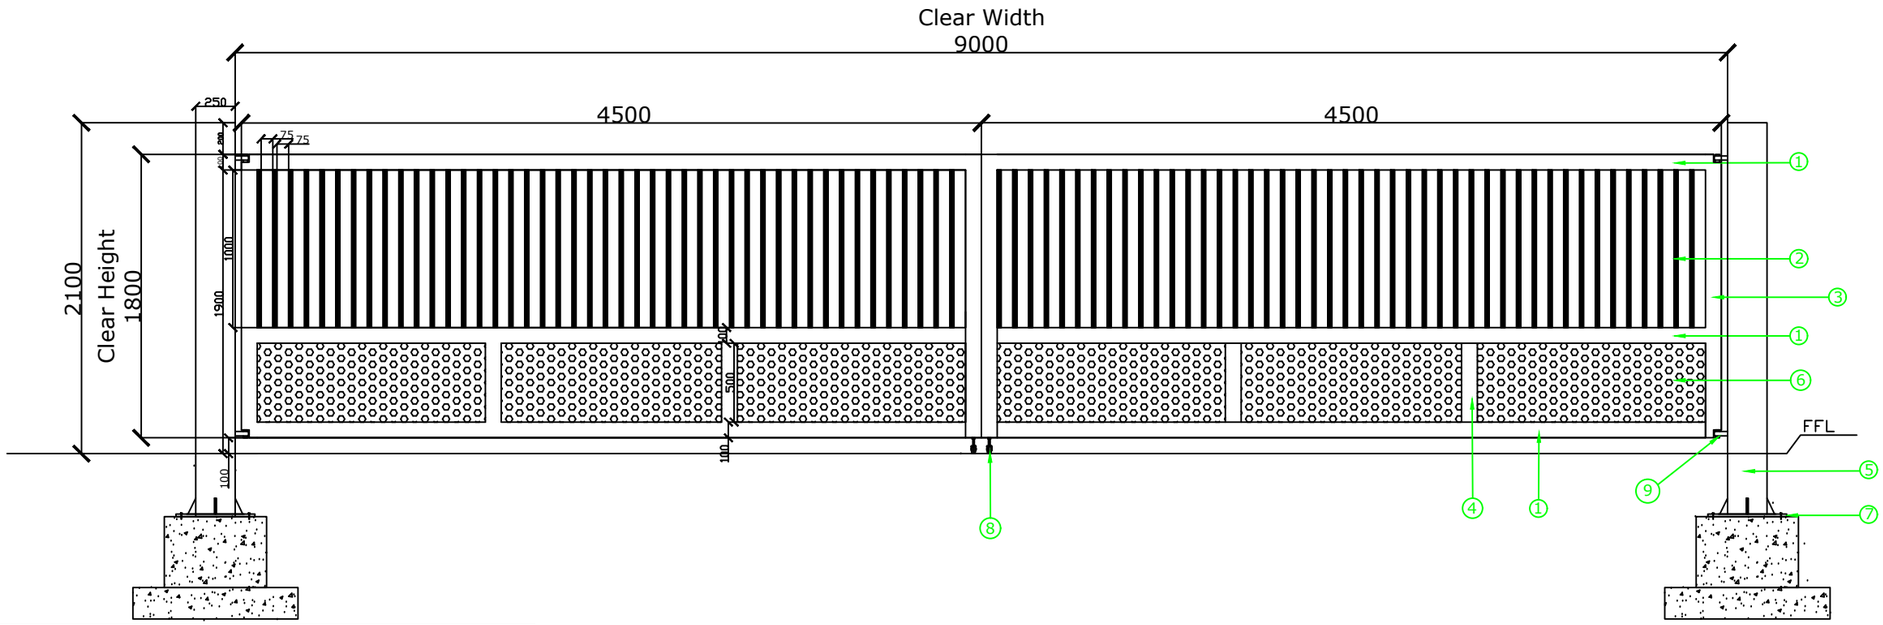


SR.NO	DESCRIPTION	LENGTH (M)	QTY
1	MS.RQ. TUBE 100X50X2.5 THK	4.5	06
2	MS.RQ. TUBE 100X50X2.5 THK	1.8	04
3	MS.RQ. TUBE 100X50X2.5 THK	0.5	04
4	MS.SQ. TUBE 25X25X2.0 THK	1.0	88
5	MS.SQ. TUBE 250X250X6.3 THK	2.5	02
6	PERFORATED SHEET 1466X500X2.0MM THK		05
7	MS PLATE 500X500X16mm		02
8	BOTTOM SLIDING WHEEL		02
9	HINGES		02

GATE SIZES :-

SR.	CLEAR WIDTH	CLEAR HEIGHT	QTY.
01	10000 mm	1800 mm	01

This drawing & designing is the property of NIHVA TECHNOLOGIES. Not to be sold or copied to any other concern.

TITLE :- GATE MANUFACTURING LEAF DRAWING

NIHVA TECHNOLOGIES PVT. LTD. PUNE
Tel : 020 66304033
Email:- info@nihva.com
Website:- www.nihva.com

	NAME	DATE
DRAWN	S.J.	18/11/2024
CHECK	K.T.	18/11/2024
APPROVAL	V.T.	18/11/2024

CLIENT - REWARD CON.
PROJECT - GATE LEAF
FORMAT NO - NIHVA-DD-F-03
DWG. NO. : NIHVA/24-25/XX00 | REV-00
SCALE: NTS | WT: | SHEET: 01 OF 01
ALL DIMENSION ARE IN mm
If any queries contact : design@nihva.com