

DOOR DIMENSION


CW: 24380 MM	CH: 4880 MM	QTY:01 NO

WEIGHT -
> TOTAL WEIGHT OF THE DOOR - 4800 KG APPROX.
> MOVING WEIGHT OF THE DOOR - 4300 KG APPROX.
> EACH PANEL WEIGHT - 720 KG APPROX.

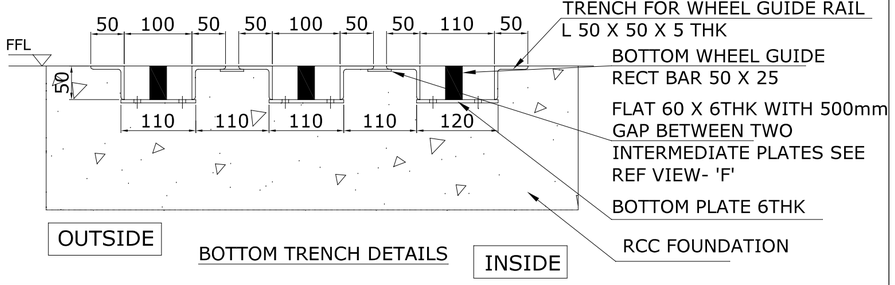



BOTTOM TRENCH DETAILS

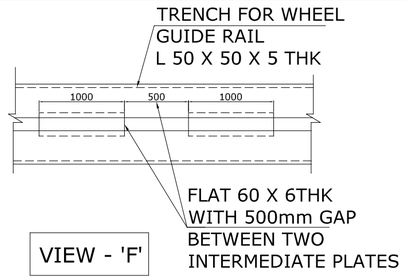

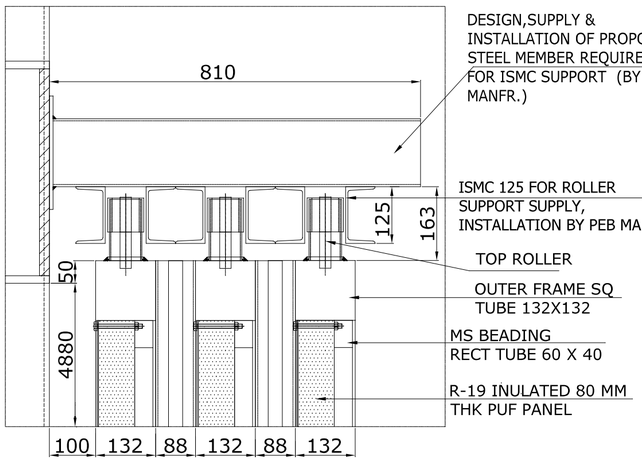


DETAIL 'A'

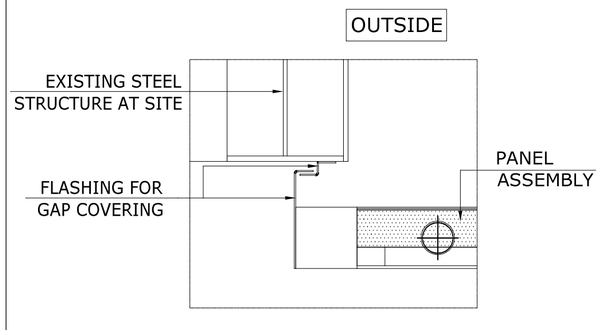


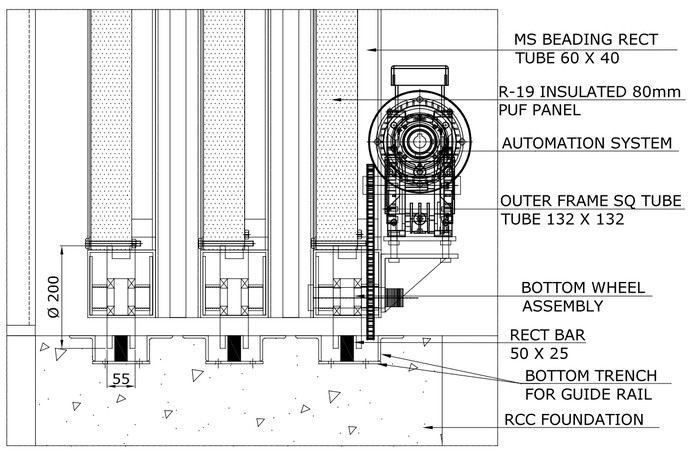

DETAIL 'B'

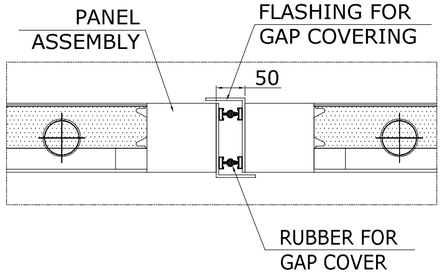

DETAIL 'E'

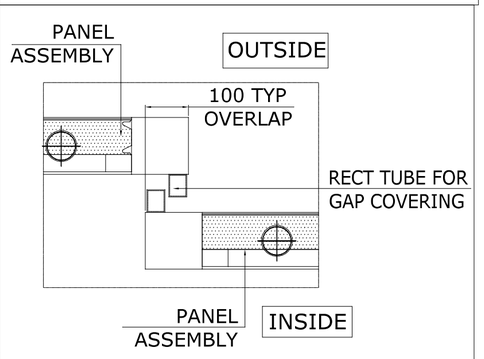

DETAIL 'D'

TECHNICAL DATA

COMPONENTS	MATERIAL	SPECIFICATION
GATE FRAME	MS	IS 4923:2017 SQ TUBE 132 X 132 X 3.0 THK MAKE - APPOLO/JSW/EQV. TENSILE STRENGTH (Mpa) - 300 Mpa
INTERMEDIATE SECTION	MS	IS 4923:2017 RECT TUBE 60 X 40 X 2.0 THK MAKE - APPOLO/JSW/EQV. TENSILE STRENGTH (Mpa) - 300 Mpa
	-	R-19 FRIGOWALL TYPE INSULATED 80 MM PUF PANEL MAKE - METECNO
	AL	FLAT 25 X 3THK
TOP TRACK ROLLER	-	PU ROLLER WITH GUIDER
BOTTOM ROLLERS	MS	IS 2062:2011 HEAVY DUTY WHEEL WITH RECTANGLE BAR
TOP TRACK	-	IS 2062:2011 ISMC 125 X 65
AUTOMATION SYSTEM	-	THREE PHASE ,415V,50HZ, MOTOR SPEED -1400RPM, POWER -1.5KW, TORQUE - 326NM
		CONTROL PANEL AVIANS MAKE
STANDARD FINISH	-	PU PAINT RAL 1001

IMPORTANT NOTES :-
1) ALL DIMENSION ARE IN MM.
2) THREE PHASE , POWER SUPPLY REQUIRE (CLIENTS SCOPE)
3) INPUT SUPPLY 3Ø, 3P,20A,415V(R.Y.B.N & E) IN CLIENT SCOPE
4) WIND SPEED - CLASS-4 (180KM/hr)

GENERAL NOTES & REMARKS :

THIS IS A COPYRIGHT DOCUMENT AND MUST NOT BE REPORDUCED WITHOUT WRITTEN PERMISSION.
THE BUILDER IS TO WORK ACCORDING TO FIGURED DIMENSIONS, AND MUST NOT SCALE THE DRAWING.
ALL DIMENSIONS ARE TO BE CHECKED ON SITE, ANY DISCREPANCIES TO BE REPORTED TO THE ENGINEER BEFORE ANY WORK IS CARRIED OUT.
ALL DIMENSIONS IN MILLIMETERS, UNLESS OTHER WISE STATED.
MEASUREMENTS ARE TO THE CLOSEST SITE DIMENSION.
VERIFY ALL DIMENSIONS ON SITE.

KEY PLAN :

REVISION :

NO.	DATE	DESCRIPTION	ACTION
R-0	14.10.20	DOOR SPECIFICATION & CLIENT COMMENTS ADDED	-

ACTION CODE :

A - APPROVED
B - APPROVED AS NOTED
C - NOT APPROVED
D - RETURNED WITH COMMENTS
E - FOR INFORMATION

CLIENT :
ALI AL SALEM AIR BASE
ALI AL SALEM AIR BASE, KUWAIT

PROJECT :
SEMI PERMANENT SMALL AIRCRAFT WEATHER SHELTER C-12

MAIN CONTRACTOR :

SUB CONTRACTOR:
AVIANS INNOVATIONS TECHNOLOGY PVT. LTD.
615 / 25, Pradhikaran, Nigdi, Pune-411044
Tel : 020 65112222, Fax : +91 20 27490570
www. avians.co.in sales@avians.co.in

VENDOR DESIGNER:

DRAWING TITLE :
MOTORIZED TELESCOPIC HANGER DOOR

REFERENCE DRAWING DETAILS :

DATE :	-	REVISION NO. :	-
DRAWING NO. :	- AIT/19-20/8027-1/MTSD-01/R1		
DRAWING DETAILS :	GENERAL ARRANGEMENT DRAWING		

DRAWN BY :	DESIGN BY :	CHECKED BY :	APPROVED BY :
CAK	CAK	MCP	MCP
DATE :	SCALE :	PAPER SIZE :	REVISION NO. :
30.09.2020	AS NOTED	A3	0
DRAWING NO. :			

SHEET 2 OF 2