
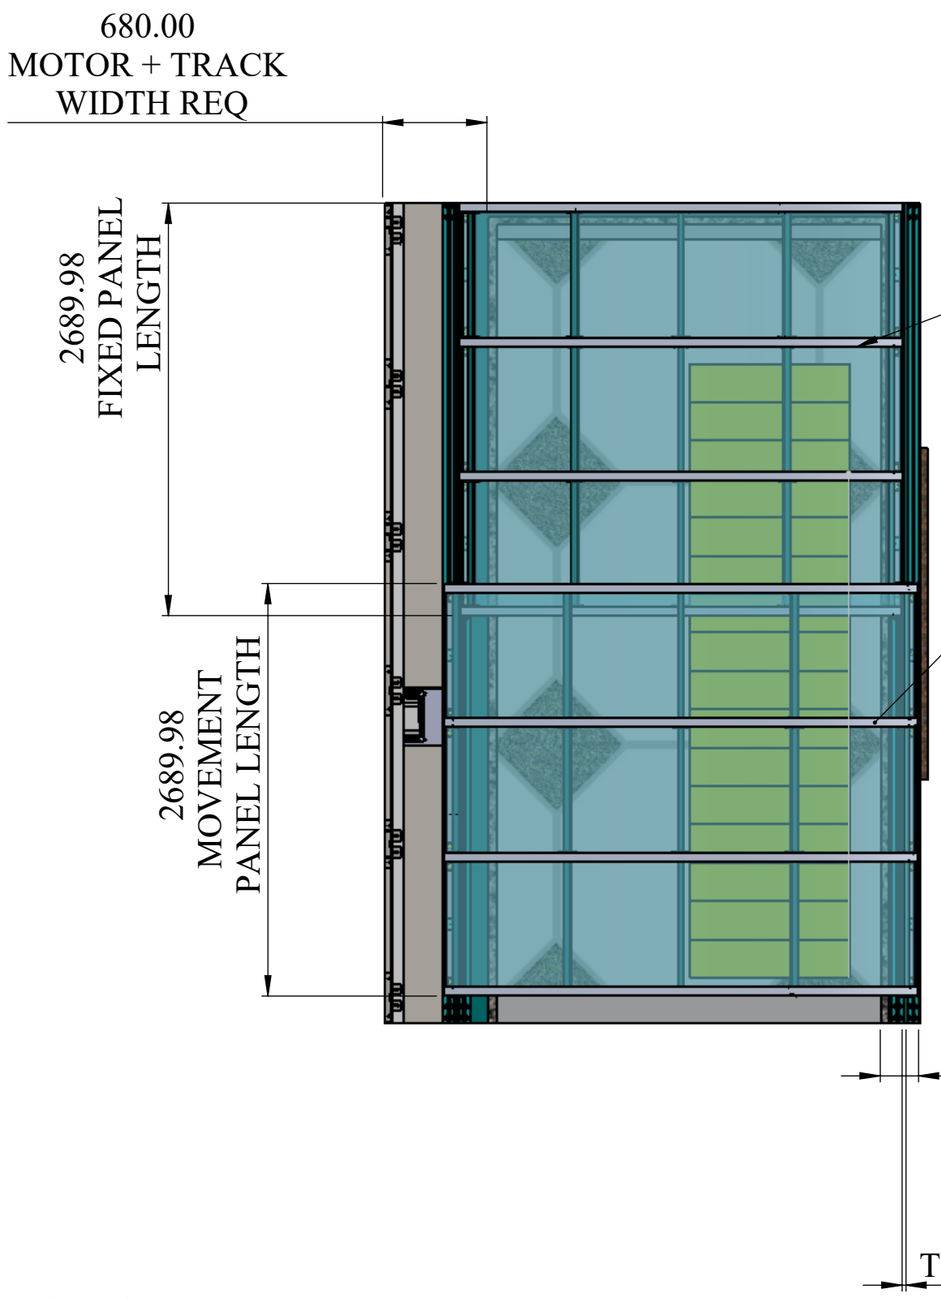
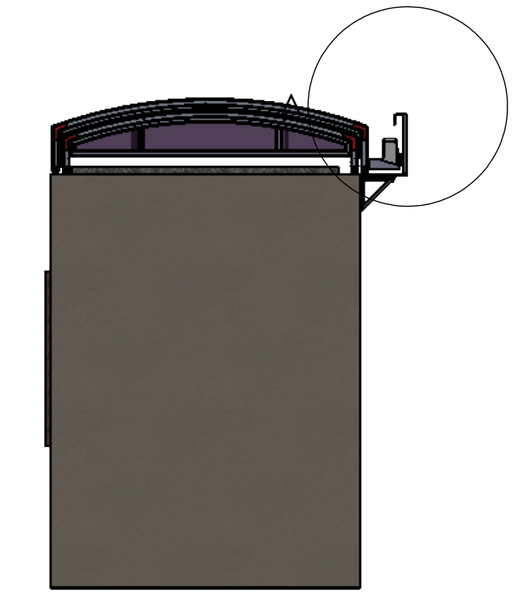


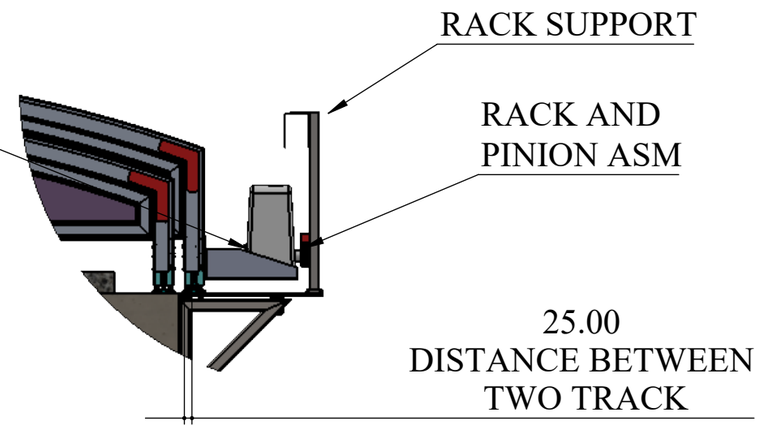


DETAIL A
SCALE 1 : 20


**NOTE 01**:-


1) IF YOU DO CIVIL WORK FOR TRACK THEN REQUIRED THICKNESS OF CONCERT 200 MM


**NOTE 02:-**

2) IF YOU DO FABRICATION WORK FOR MOTOR AND TRACK MOUNTING THEN MS PLATE IS REQUIRED,THICKNESS OF PLATE 12 MM IS REQUIRED AT CLIENT SCOPE

| | | | | |
|---|---|---|---|---|
| TITLE - ROOF AUTOMATION | | | | NIHVA TECHNOLOGIES PVT.LTD.PUNE |
| DWG NO - NTPL | | | QTY - 1 | Website - www.nihva.com |
| | NAME | SIGNATURE | DATE | PROJECT NO - NTPL |
| DRAWN | V.B. | | 28-05-2025 | PRODUCT - RETRACTABLE ROOF |
| CHK'D | S.W. | | 28-05-2025 | SITE LOCATION - LUCKNOW |
| APPV'D | V.T. | | 28-05-2025 | |
| if any queries contact - supportautomation@nihva.com | | | | REVISION - |
| ALL DIMENSION ARE IN mm | | | A3 | SCALE - SHEET 1 OF 2 |

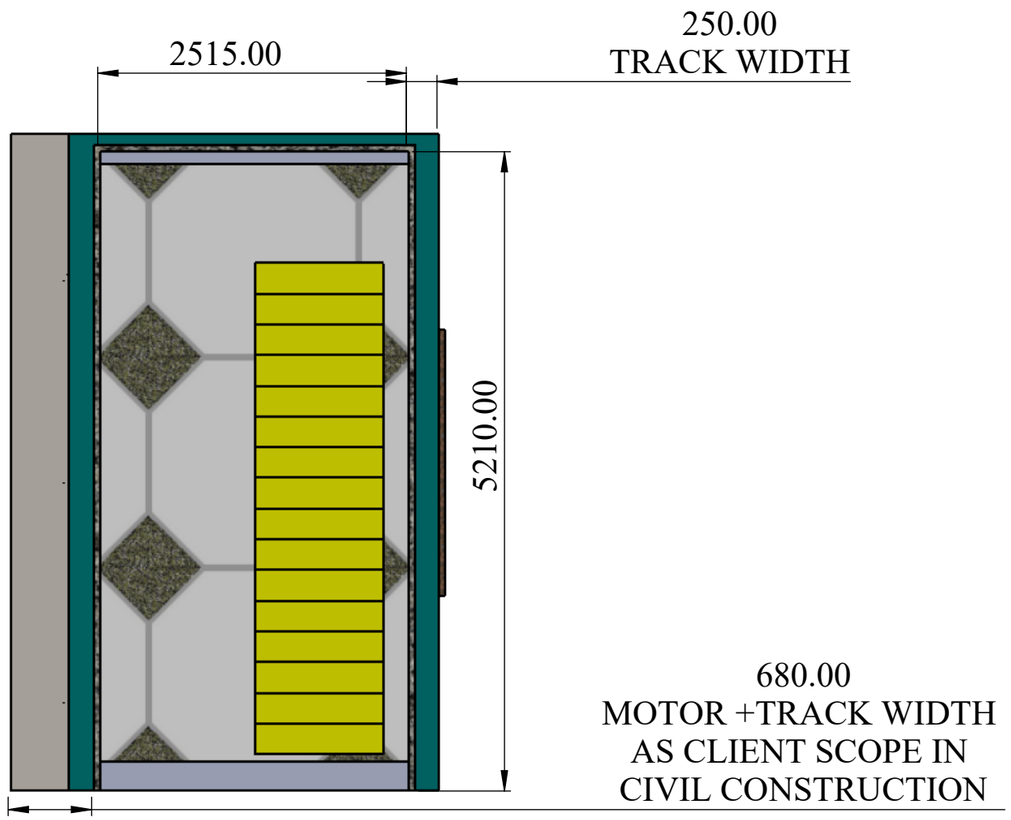

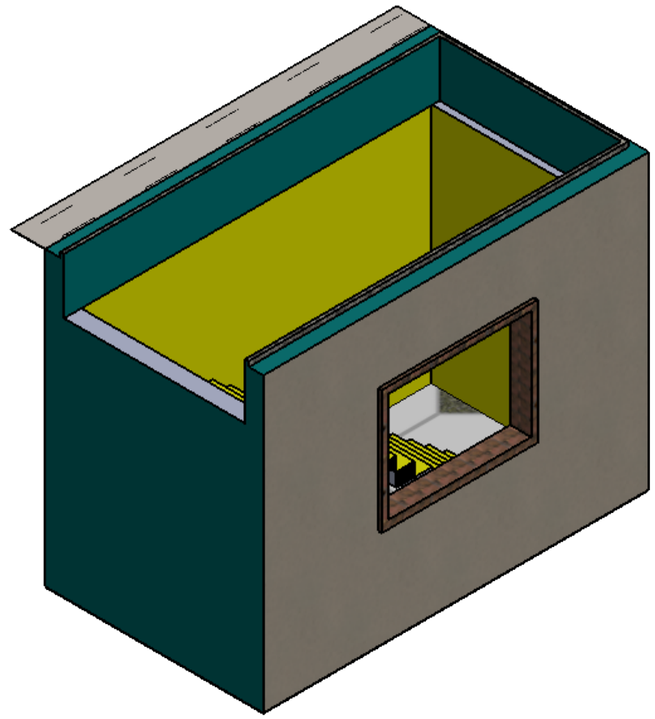

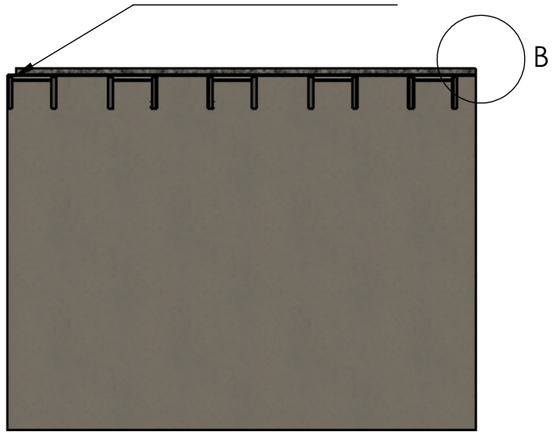
**NOTE:-**

THE PRESENT WALL WIDTH IS 155MM AND PRESENT COLOUMN SIZE IS FRONT COLOUMN SIDE SIZE 540X250MM AND COLOUMN BACK SIDE SIZE 460X250 MM

I NEED 250 MM WALL WIDTH FOR PROPER PANEL MOUNTING AND ITS MOVEMENT SO ITS NEED TO INCREASE A WALL WIDTH 155 MM TO SAME AS COLOUMN WIDTH 250MM




DETAIL B
SCALE 1 : 10

| | | | | |
|---|---|---|---|---|
| TITLE - ROOF AUTOMATION | | | | NIHVA TECHNOLOGIES PVT.LTD.PUNE<br>Website - www.nihva.com |
| DWG NO - NTPL | | | QTY - 1 | |
| | NAME | SIGNATURE | DATE | PROJECT NO - NTPL268 |
| DRAWN | V.B. | | 28-05-2025 | PRODUCT - RETRACTABLE ROOF |
| CHK'D | S.W. | | 28-05-2025 | SITE LOCATION - LUCKNOW |
| APPV'D | V.T. | | 28-05-2025 | |
| if any queries contact - supportautomation@nihva.com | | | | REVISION - |
| ALL DIMENSION ARE IN mm | | | A3 | SCALE - SHEET 2 OF 2 |