



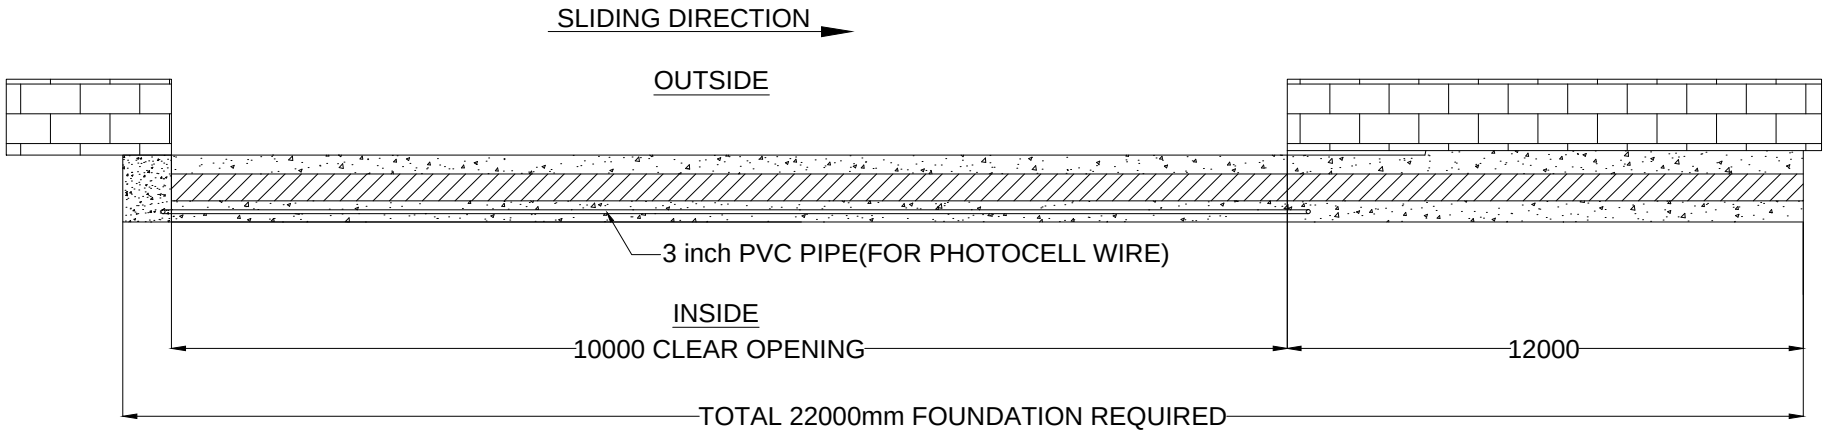

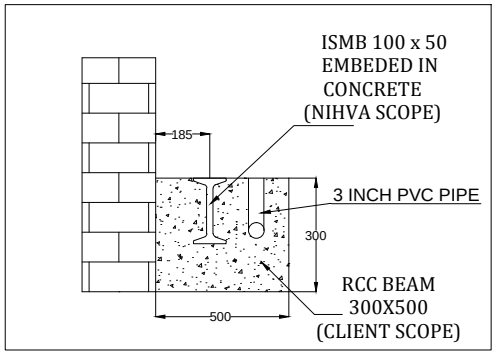

This drawing & designing is the property of NIHVA TECHNOLOGIES. Not to be sold or copied to any other concern.

TITLE: SLIDING GATE FOUNDATION DRAWING			NIHVA TECHNOLOGIES PVT. LTD.
	Name	SIGN	DATE
DRAWN	SURAJ		13/11/18
CHECK	PRADEEP		13/11/18
APPROVAL	R.D		13/11/18
If any queries contact : design@nihva.com			
ALL DIMENSION ARE IN mm			

NIHVA TECHNOLOGIES PVT. LTD. PUNE
Tel : 020 66304033
Email:- info@nihva.com
Website:- www.nihva.com

CLIENT - INOX		
PROJECT -		
SITE LOCATION -BARJORA,WEST BENGAL		
DWG. NO. : NIHVA/18-19/0170		REV.:- 0
SCALE: NTS	WT:	SHEET: 01 OF 01