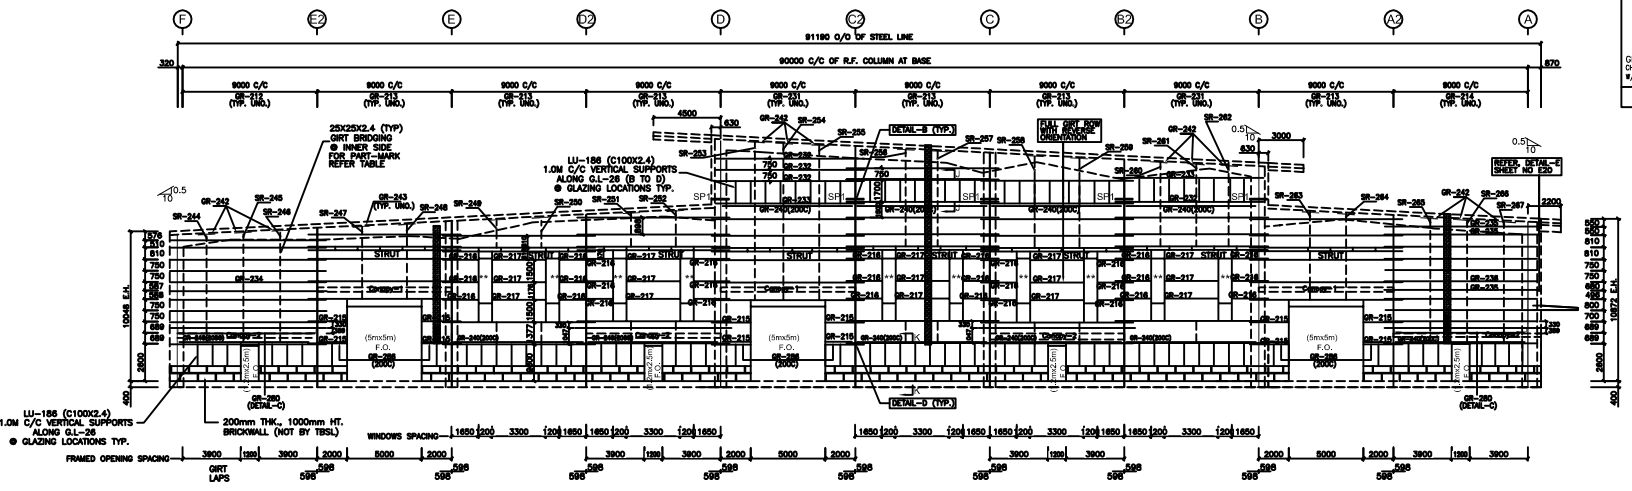



ENDWALL FRAMING @ G.L. - 26

:- DENOTES INSULATION – ROCK WOOL, 50MM THICK 48KG/M3 WITH FSK FACING.
FOR CONNECTION DETAILS REFER DWG NO –: A30
FOR CANOPY DETAILS REFER DWG NO–A07
** :- DENOTES 1.2MX3.0M OPENING TYP. SILL LVL–5.2m FROM FFL.
FOR SHEETING REF, E29A
FOR GABLE EXTENSION DETAILS, REFER E29D


SP1-M24X100 HSB 8 NOS W/25mm THK. PLATES

GIRT BRIDGING TABLE

GIRT SPACING	GIRT BRACE PART MARK (@ INNER SIDE)	GIRT BRACE LENGTH
1377	PA–237	1425
689	PA–268	737
359	PA–269	407
330	PA–270	378
750	PA–271	798
587/588	PA–272	636
810	PA–273	858
510	PA–274	558
1175	PA–275	1223
1500	PA–276	1548
570	PA–277	618
898	PA–278	946
700	PA–279	748
496	PA–281	544
680	PA–282	728
550	PA–283	598
1047	PA–301	1095
800	PA–302	848

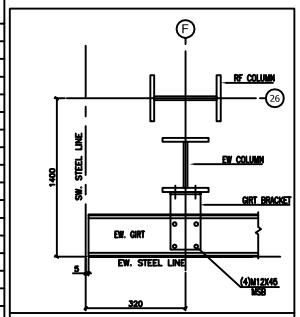


GIRT CONNECTION DETAIL @ CORNER

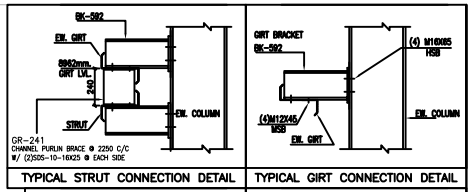


TYPICAL STRUT CONNECTION DETAIL

TYPICAL GIRT CONNECTION DETAIL

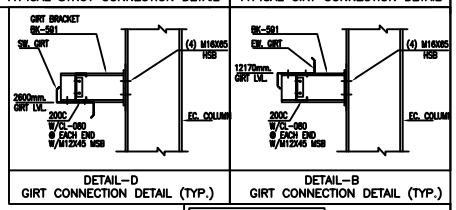


DETAIL–D GIRT CONNECTION DETAIL (TYP.)


DETAIL–B GIRT CONNECTION DETAIL (TYP.)

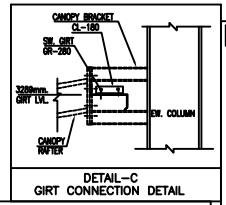


DETAIL–C GIRT CONNECTION DETAIL

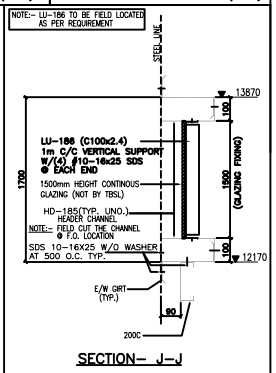


SECTION– J–J

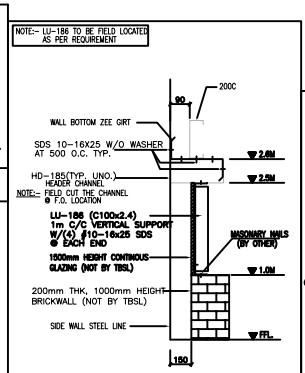


SECTION K–K

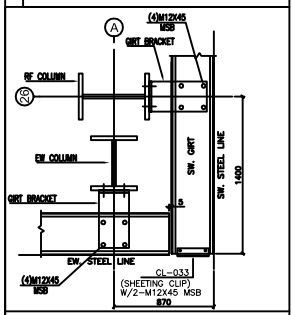

GIRT CONNECTION DETAIL @ CORNER

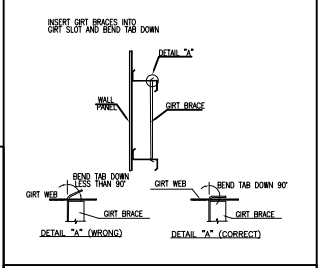


SINGLE BRACE BETWEEN INTERIOR GIRT

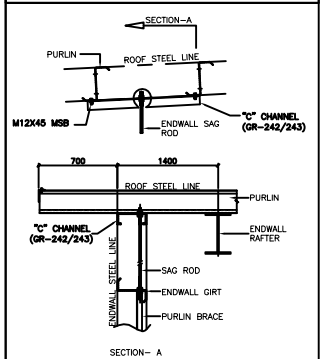


SECTION– A


SAGROD I/S FIXING DETAIL @ BYPASS EW

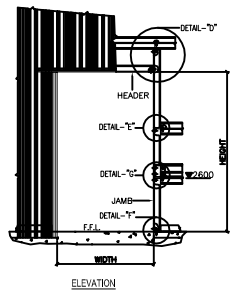

ELEVATION

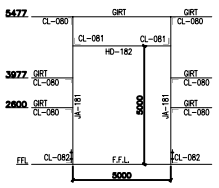


5m x 5m FRAMED OPENING DETAIL

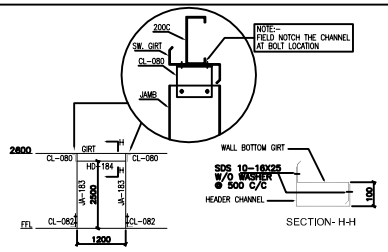


1.2m x 2.5m FRAMED OPENING DETAIL


SECTION- H-H

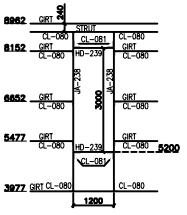


1.2m x 3m FRAMED OPENING DETAIL

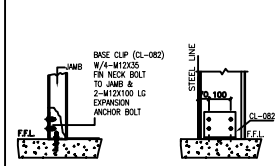


DETAIL-F

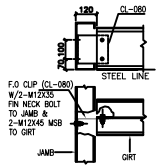

DETAIL-E

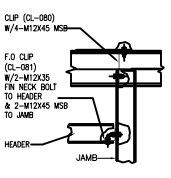

DETAIL-D

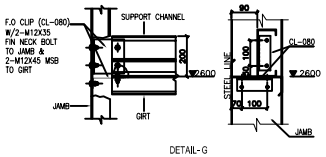

DETAIL-G

NOTE:- THIS DRAWING NEED TO SUBMITTED FOR FM APPROVAL

ALL DIMENSIONS ARE IN MM

NO.	DATE	DESCRIPTION	DRN	CHK	DSN
00	04.07.13	ISSUED FOR CONSTRUCTION	PKM	GHR	SSD/RAP

Tata BlueScope Steel Limited
Survey No. 247 & 250,
Hinjewadi, Taluka Mulshi,
Pune - 411057, India.
Telephone : +91 20 6674 2000
Facsmile : +91 20 6674 2001
www.tatabluescopesteel.com

JOB NO.	: FM1-1384	BUILDING NO. :	01 (F.L. 15 TO 26)
PROJECT NAME	: GE INDIA INDUSTRIAL PVT. LTD		
CUSTOMER	: GE INDIA INDUSTRIAL PVT. LTD		
JOBSITE LOCATION	: CHAKAN, PUNE		
DRAWING TITLE	: ENDWALL FRAMING & SHEETING @ G.L-26	DRAWING NO.	E29