
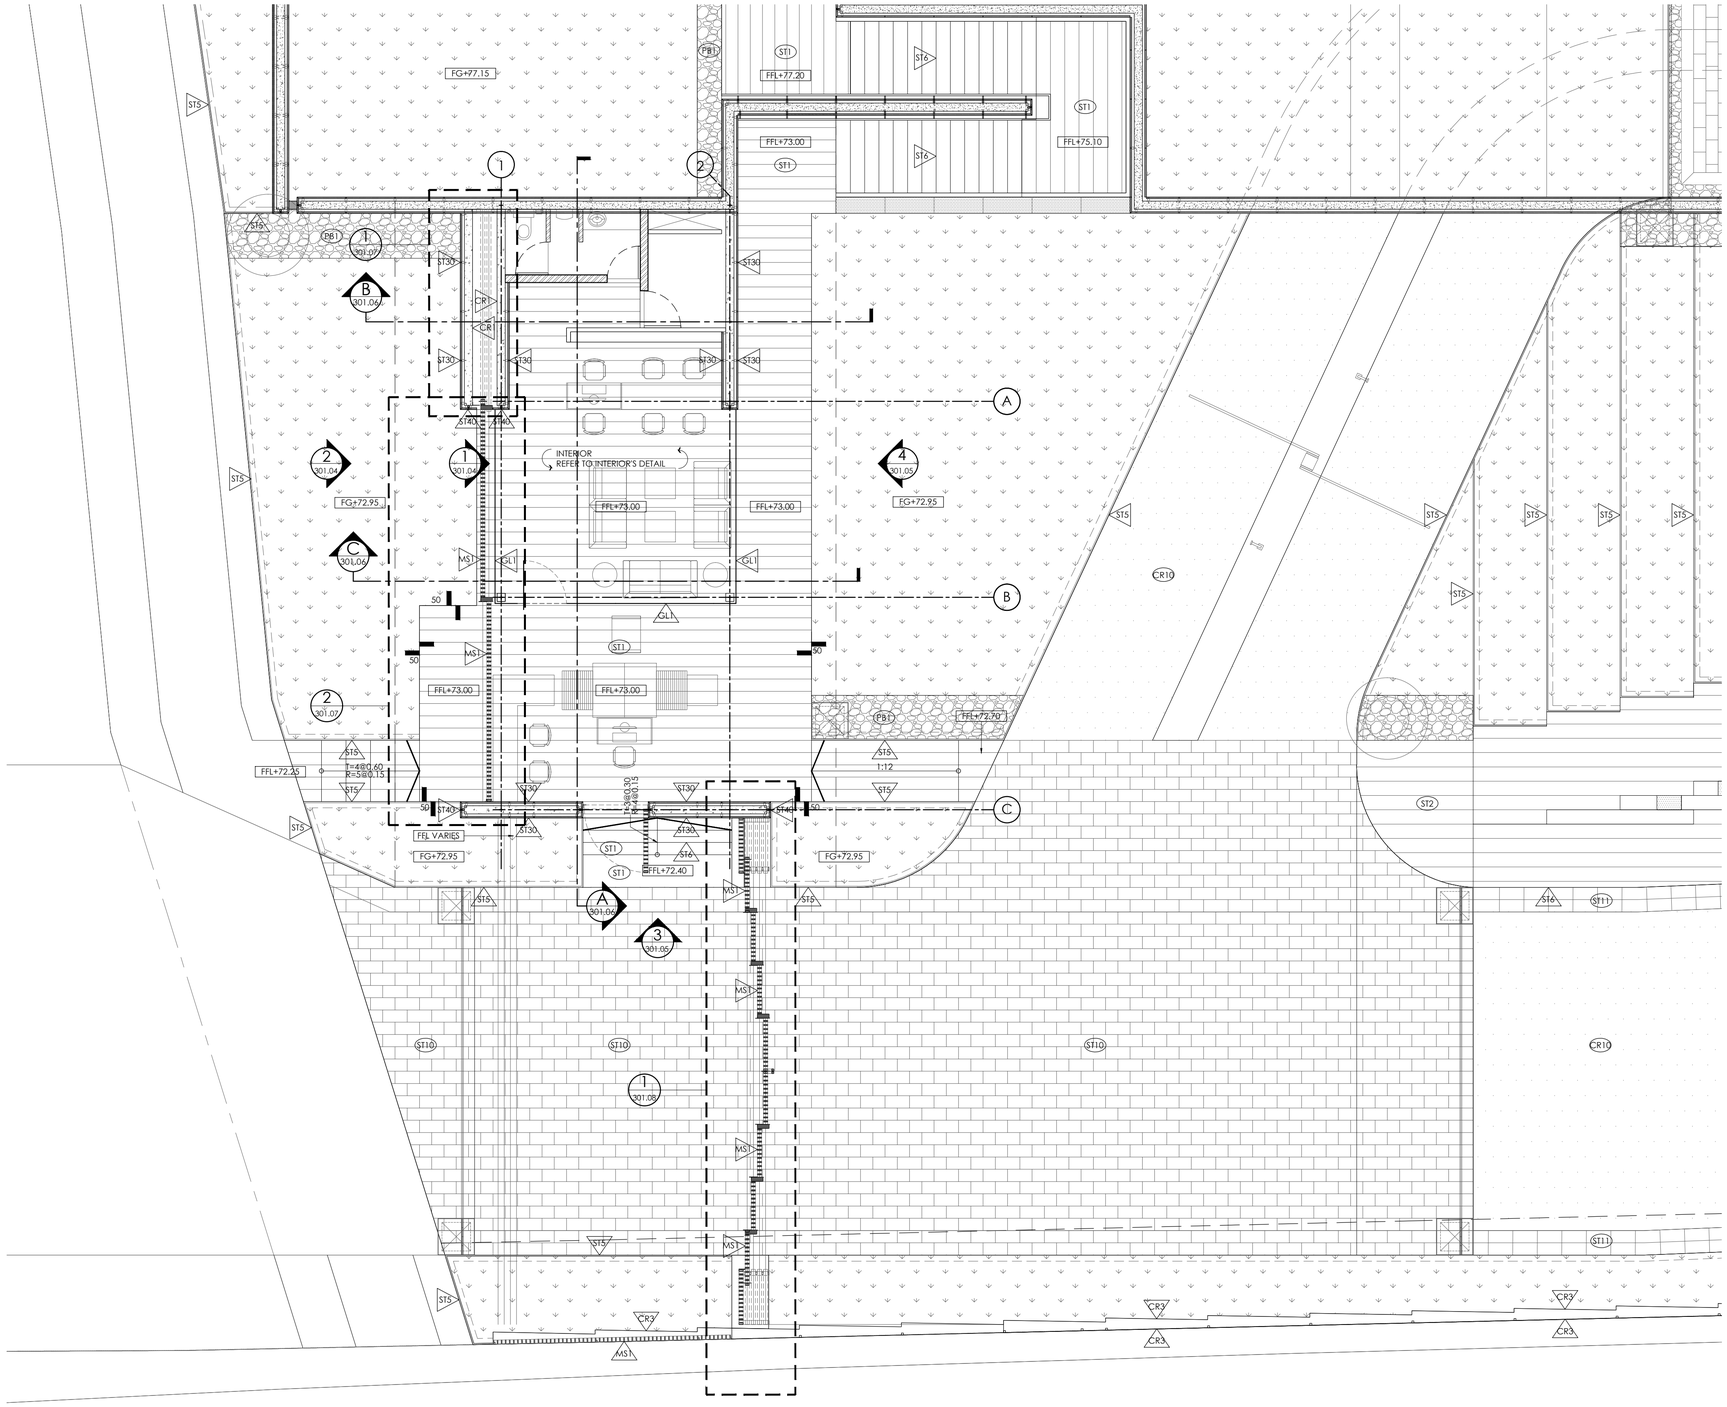


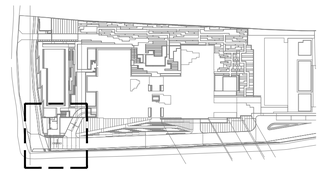


0 KEY PLAN

1 / 111.01 BLOW-UP 01 : GUARD HOUSE DETAIL PLAN
1:75


NOTES	LANDSCAPE ARCHITECT	CLIENT / OWNER	ARCHITECT
1. Shma Co., Ltd. All rights reserved. No copy is allowed without written permission from Shma. 2. All dimensions are to be carefully checked by the contractor. All adjustments must be made before commencement of works or frabrication of fittings.	Shma Co., Ltd. 93/2 Ekkamai 3 Sukhumvit 63 Rd. Klongton Nuer Vadhana Bangkok Thailand 10110 TEL:662 390 1977 Fax:662 390 1974 Email: admin@shmadesigns.com	**LUPIN LIMITED** MUMBAI	**Venkataramanan Associates** ARCHITECTURE - URBAN DESIGN 10/2 , O'SHAUGHNESSY ROAD, LANGFORD GARDENS, BANGALORE– 560 025

PROJECT TITLE : LUPIN RESEARCH PARK, PUNE, INDIA

JOB NO.	315	DATE	17.08.15	PROJECT LA	DRAWING NAME	DRAWING NO.	ISSUED FOR	STAGE	REV	DESCRIPTION	NORTH
SCALE	A0 -	CHECKED BY	PRAPAN	PRAPAN NAPAWONGDEE	*BLOW-UP 01*	*301.01*	CONSTRUCTION	GFC			
	A1 *1:75*	DRAWN BY	KATAVET	KATAVET SITTIKIT	*GUARD HOUSE*						
	A3 -			KRITTAYA and PAT	*DETAILPLAN*						

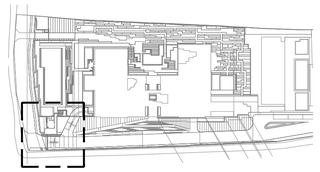

0 KEY PLAN

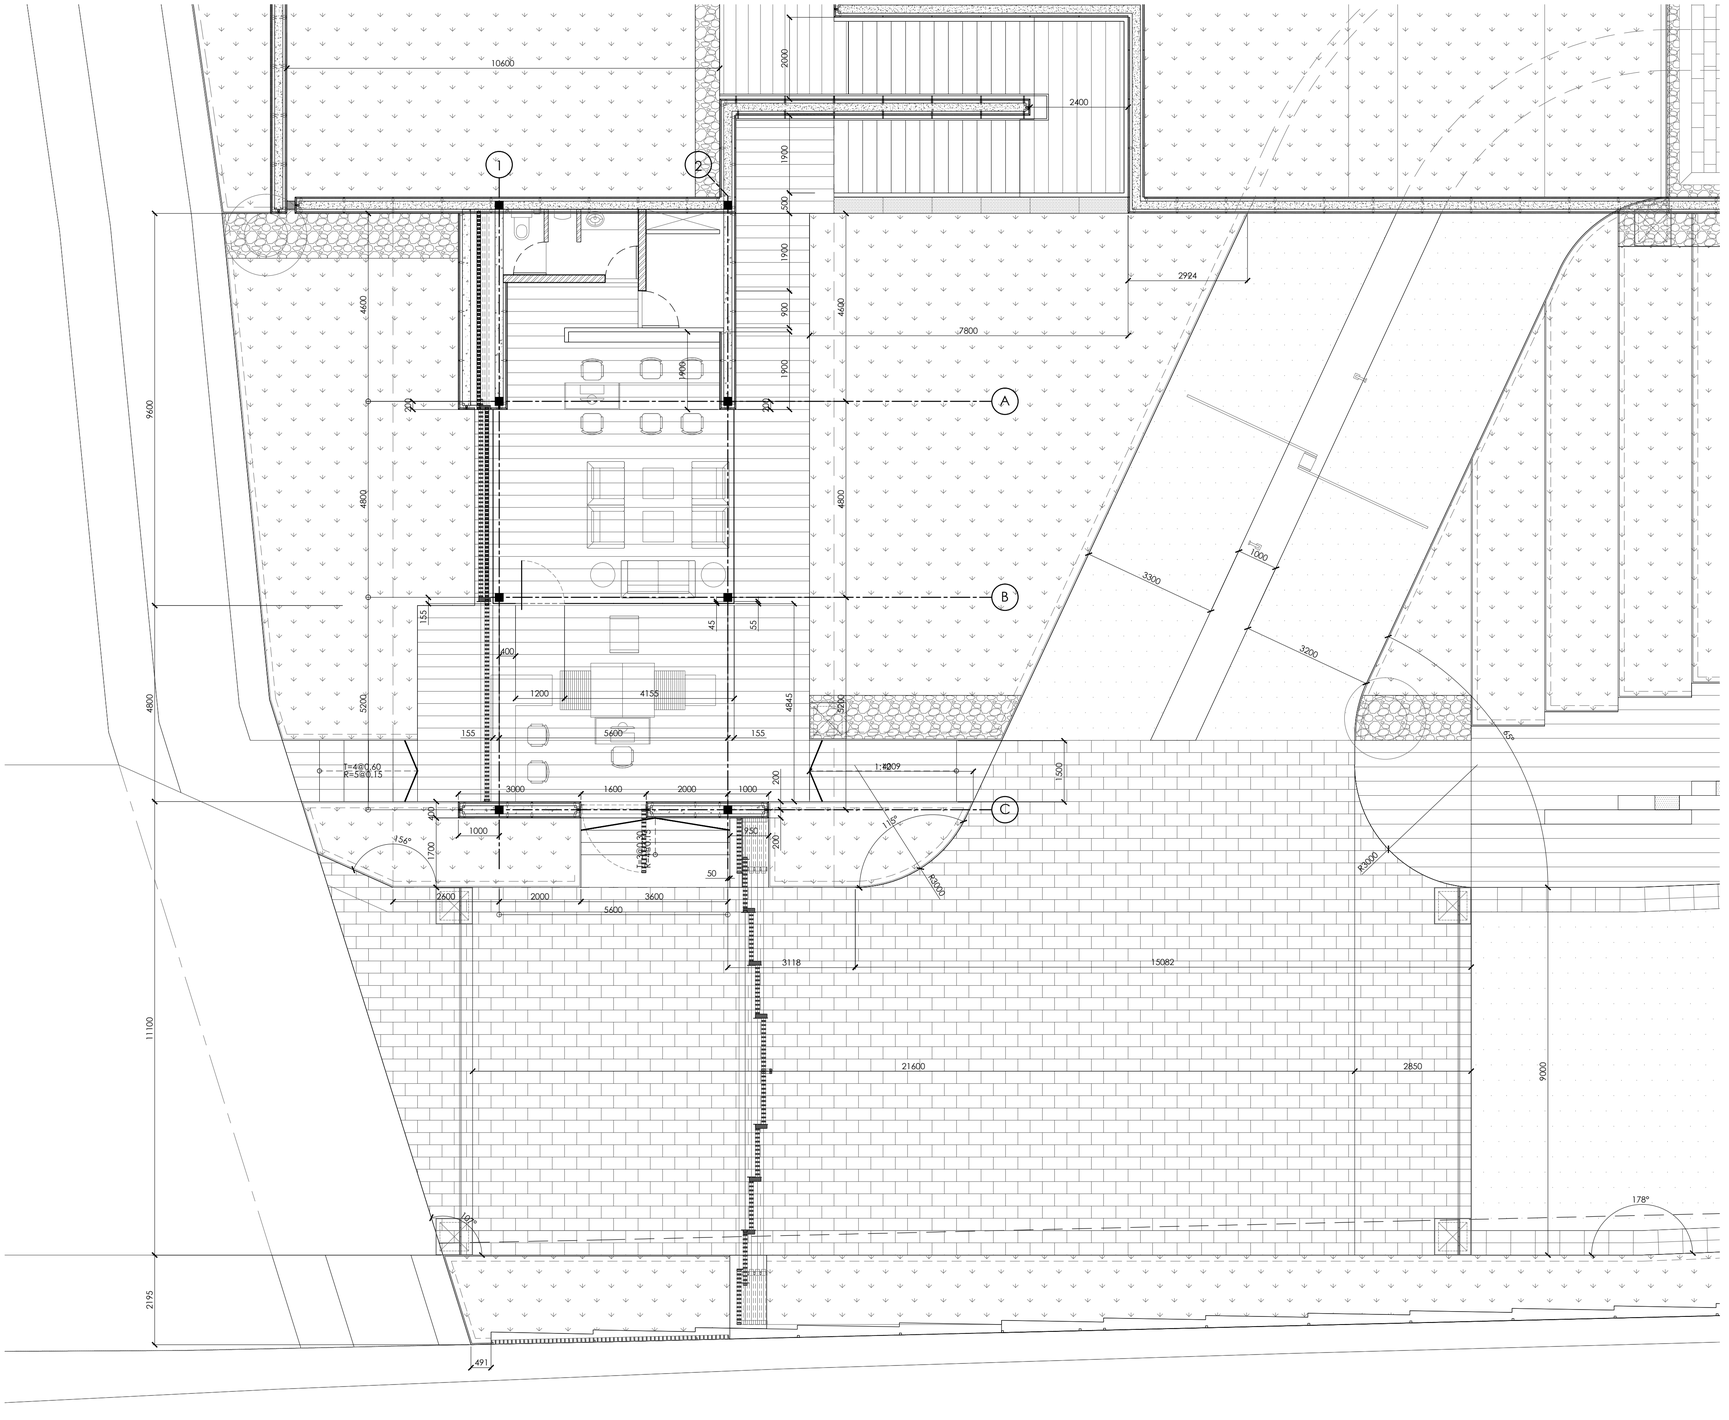

1 (111.01) BLOW-UP 01 : GUARD HOUSE SETTING-OUT PLAN
1:75

NOTES

1. Shma Co., Ltd. All rights reserved.
   No copy is allowed without written permission from Shma.
2. All dimensions are to be carefully checked by the contractor.
   All adjustments must be made before commencement of works or frabrication of fittings.

LANDSCAPE ARCHITECT

shma

Shma Co., Ltd.
93/2 Ekkamai 3 Sukhumvit 63 Rd.
Klongton Nuer Vadhana
Bangkok Thailand 10110
TEL:662 390 1977 Fax:662 390 1974
Email: admin@shmadesigns.com

CLIENT / OWNER


LUPIN LIMITED
MUMBAI

ARCHITECT


Venkataramanan Associates
ARCHITECTURE - URBAN DESIGN
10/2 , D'SHAUGHNESSY ROAD, LANGFORD GARDENS, BANGALORE– 560 025

PROJECT TITLE : LUPIN RESEARCH PARK, PUNE, INDIA

JOB NO.	315	**DATE**	17.08.15	**PROJECT LA**	PRAPAN NAPAWONGDEE	**DRAWING NAME**	**DRAWING NO.**	**ISSUED FOR**	**STAGE**	**REV**	**DESCRIPTION**	**NORTH**
SCALE	**A0** -	**CHECKED BY**	PRAPAN	KATAVET SITTIKIT		*BLOW-UP 01*	*301.02*	CONSTRUCTION	GFC			
	A1 *1:75*	**DRAWN BY**	KATAVET	KRITTAYA and PAT		*GUARD HOUSE SETTING-OUT PLAN*						
	A3 -											

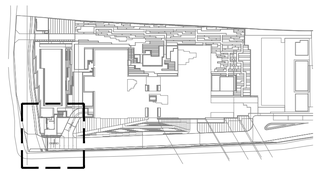

0 KEY PLAN

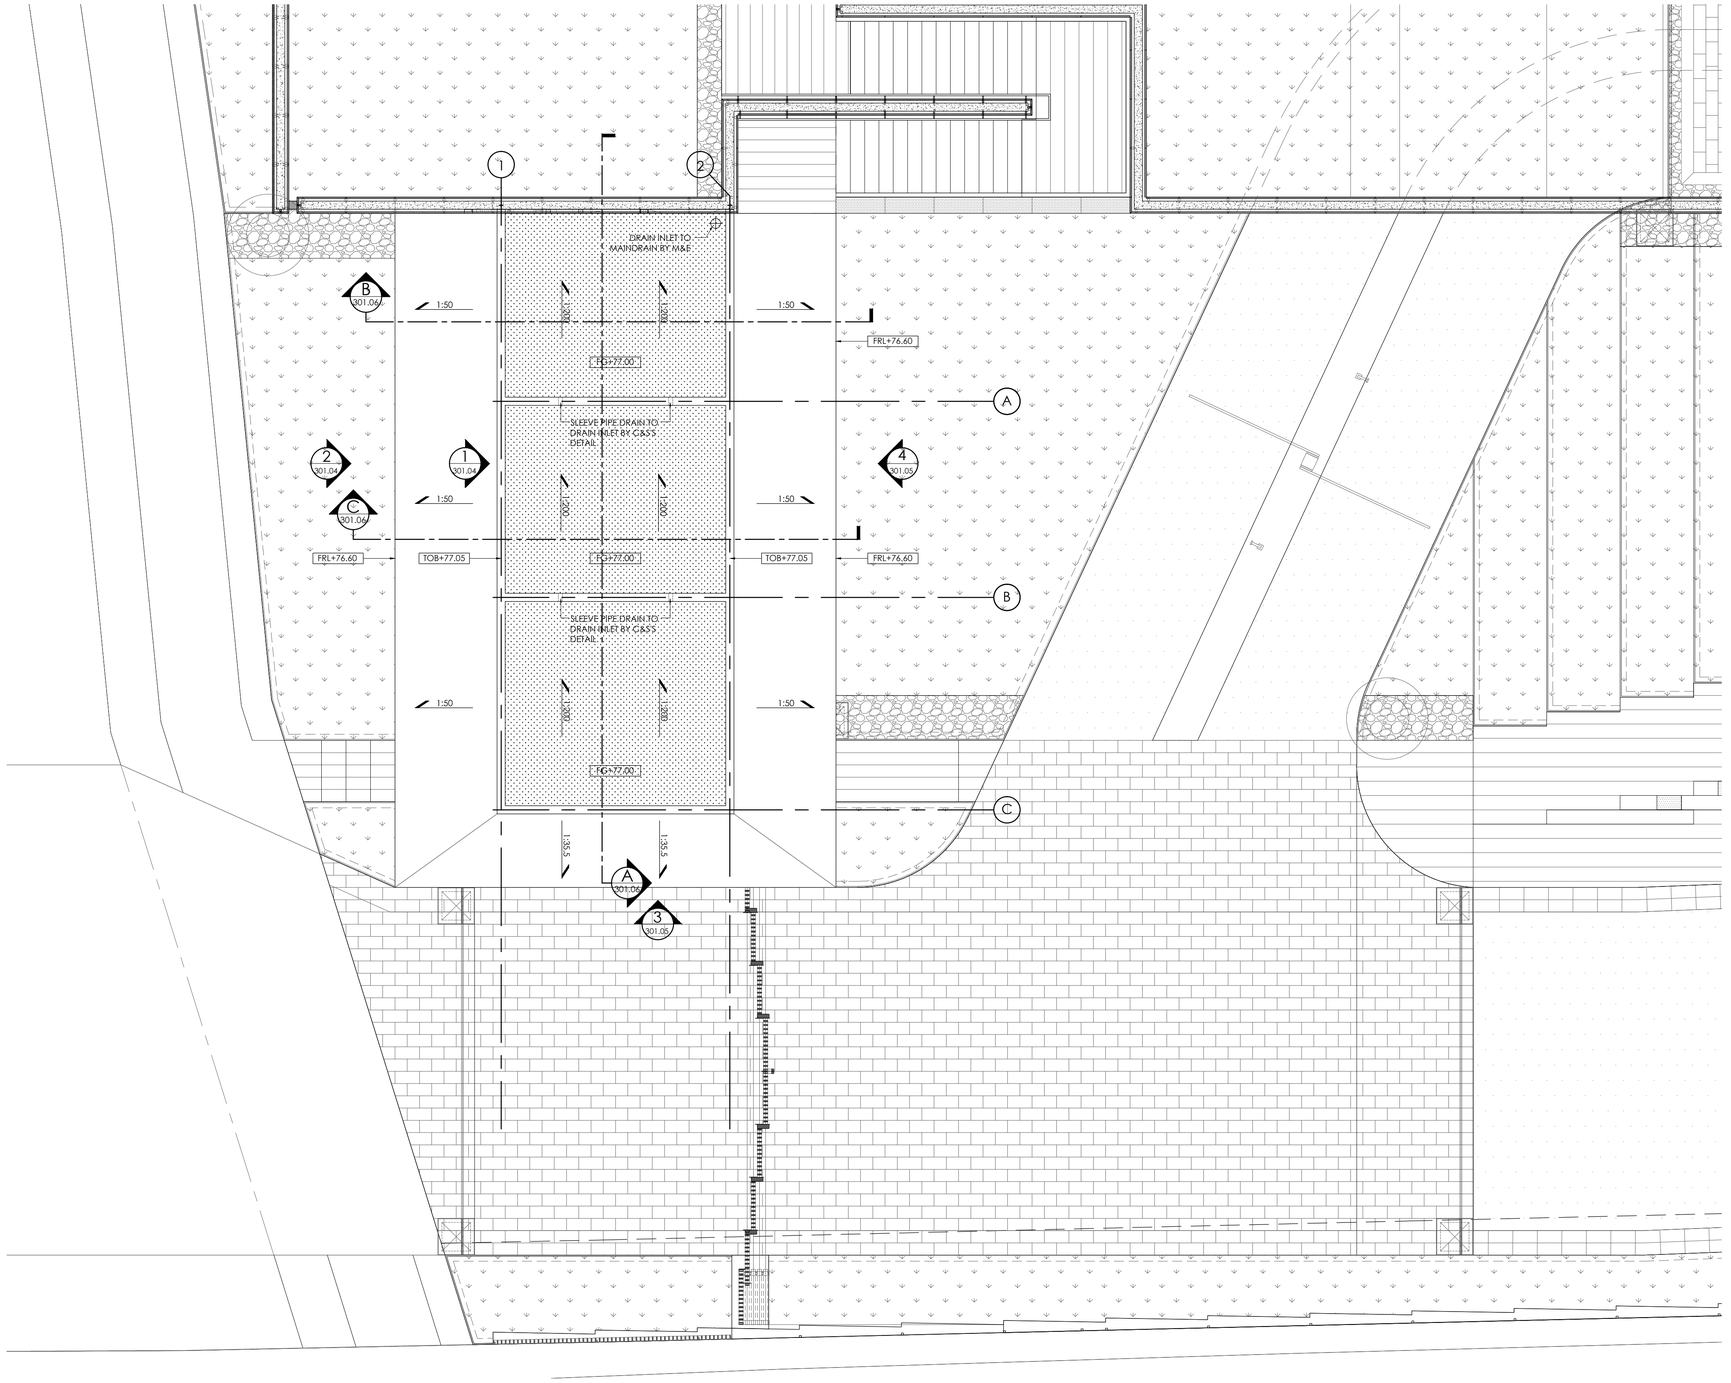

1 111.01 BLOW-UP 01 : GUARD HOUSE ROOF PLAN
1:75

NOTES

1. Shma Co., Ltd. All rights reserved.
   No copy is allowed without written permission from Shma.
2. All dimensions are to be carefully checked by the contractor.
   All adjustments must be made before
   commencement of works or frabrication of fittings.

LANDSCAPE ARCHITECT

shma

Shma Co., Ltd.
93/2 Ekkamai 3 Sukhumvit 63 Rd.
Klongton Nuer Vadhana
Bangkok Thailand 10110
TEL:662 390 1977 Fax:662 390 1974
Email: admin@shmadesigns.com

CLIENT / OWNER


LUPIN LIMITED
MUMBAI

ARCHITECT


Venkataramanan Associates
ARCHITECTURE - URBAN DESIGN
10/2 , O'SHAUGHNESSY ROAD, LANGFORD GARDENS, BANGALORE– 560 025

PROJECT TITLE : LUPIN RESEARCH PARK, PUNE, INDIA

JOB NO.	315	**DATE**	17.08.15	**PROJECT LA**	PRAPAN NAPAWONGDEE	**DRAWING NAME**	*BLOW-UP 01*	**DRAWING NO.**	**ISSUED FOR**	**STAGE**	**REV**	**DESCRIPTION**	**NORTH**
SCALE	**A0** -	**CHECKED BY**	PRAPAN	KATAVET SITTIKIT		*GUARD HOUSE*	*301.03*	CONSTRUCTION	GFC			
	A1 *1:75*	**DRAWN BY**	KATAVET	KRITTAYA and PAT		*ROOF PLAN*						
	A3 -											

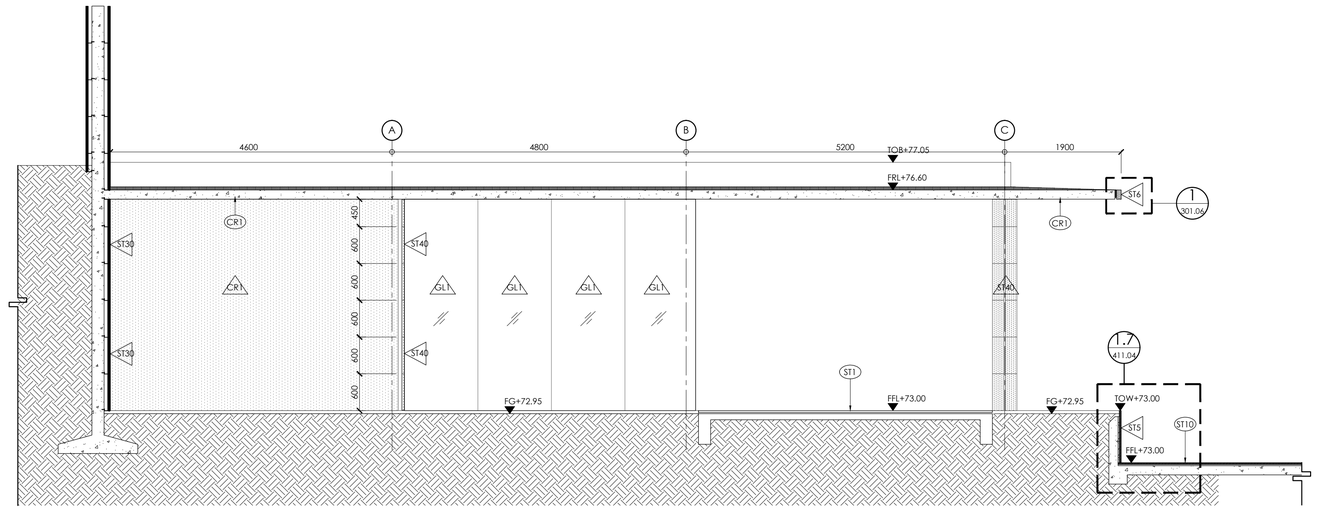

1 / 301.01 BLOW-UP 01 : GUARD HOUSE ELEVATION 1
1:50

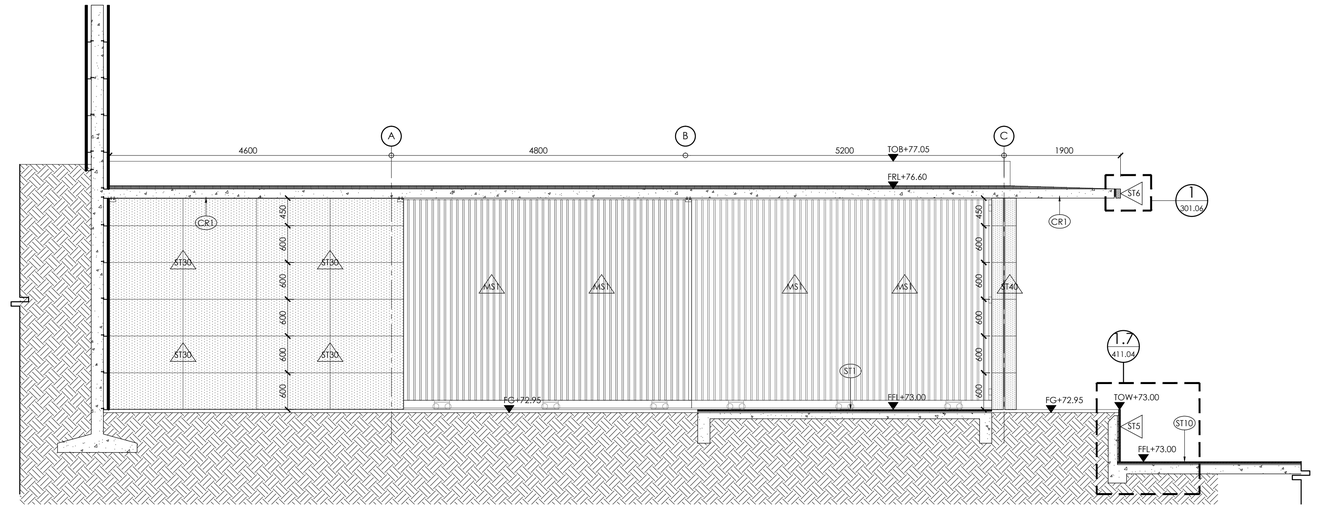

2 / 301.01 BLOW-UP 01 : GUARD HOUSE ELEVATION 2
1:50

NOTES

1. Shma Co., Ltd. All rights reserved. No copy is allowed without written permission from Shma.
2. All dimensions are to be carefully checked by the contractor. All adjustments must be made before commencement of works or frabrication of fittings.

LANDSCAPE ARCHITECT

Shma Co., Ltd.
93/2 Ekkamai 3 Sukhumvit 63 Rd.
Klongton Nuer Vadhana
Bangkok Thailand 10110
TEL:662 390 1977 Fax:662 390 1974
Email: admin@shmadesigns.com

CLIENT / OWNER


LUPIN LIMITED
MUMBAI

ARCHITECT

Venkataramanan Associates
ARCHITECTURE - URBAN DESIGN
10/2 , O'SHAUGHNESSY ROAD, LANGFORD GARDENS, BANGALORE- 560 025


PROJECT TITLE : LUPIN RESEARCH PARK, PUNE, INDIA

JOB NO.	315	**DATE**	17.08.15	**PROJECT LA**	**DRAWING NAME**	**DRAWING NO.**	**ISSUED FOR**	**STAGE**	**REV**	**DESCRIPTION**	**NORTH**
SCALE	**A0** -	**CHECKED BY**	PRAPAN	PRAPAN NAPAWONGDEE	*BLOW-UP 01*						
	A1 *1:50*	**DRAWN BY**	KATAVET	KATAVET SITTIKIT	*GUARD HOUSE*	*301.04*	CONSTRUCTION	GFC			
	A3 -			KRITTAYA and PAT	*ELEVATION 1&2*						

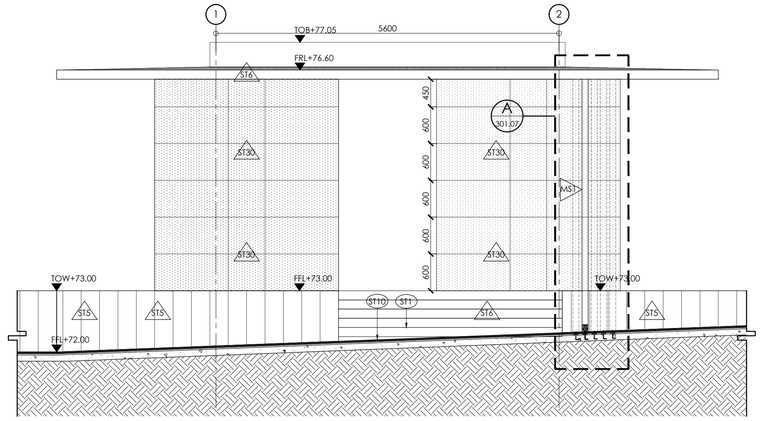

3 301.01 BLOW-UP 01 : GUARD HOUSE ELEVATION 3

1:50

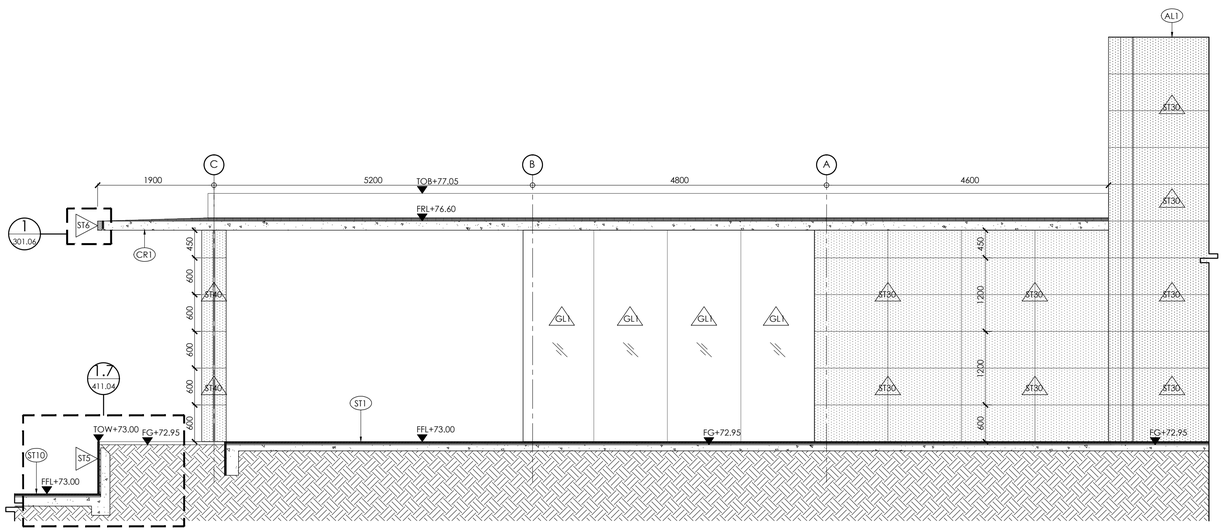

4 301.01 BLOW-UP 01 : GUARD HOUSE ELEVATION 4

1:50

NOTES

1. Shma Co., Ltd. All rights reserved.
   No copy is allowed without written permission from Shma.
2. All dimensions are to be carefully checked by the contractor.
   All adjustments must be made before
   commencement of works or frabrication of fittings.

LANDSCAPE ARCHITECT

Shma Co., Ltd.
93/2 Ekkamai 3 Sukhumvit 63 Rd.
Klongton Nuer Vadhana
Bangkok Thailand 10110
TEL:662 390 1977 Fax:662 390 1974
Email: admin@shmadesigns.com

CLIENT / OWNER


LUPIN LIMITED
MUMBAI

ARCHITECT


Venkataramanan Associates
ARCHITECTURE - URBAN DESIGN
10/2 , O'SHAUGHNESSY ROAD, LANGFORD GARDENS, BANGALORE– 560 025

PROJECT TITLE : LUPIN RESEARCH PARK, PUNE, INDIA


JOB NO.	315	**DATE**	17.08.15	**PROJECT LA**	**DRAWING NAME**	**DRAWING NO.**	**ISSUED FOR**	**STAGE**	**REV**	**DESCRIPTION**	**NORTH**
SCALE	**A0** -	**CHECKED BY**	PRAPAN	PRAPAN NAPAWONGDEE	*BLOW-UP 01*	*301.05*	CONSTRUCTION	GFC			
	A1 *1:50*	**DRAWN BY**	KATAVET	KATAVET SITTIKIT	*GUARD HOUSE*						
	A3 -			KRITTAYA and PAT	*ELEVATION 3&4*						

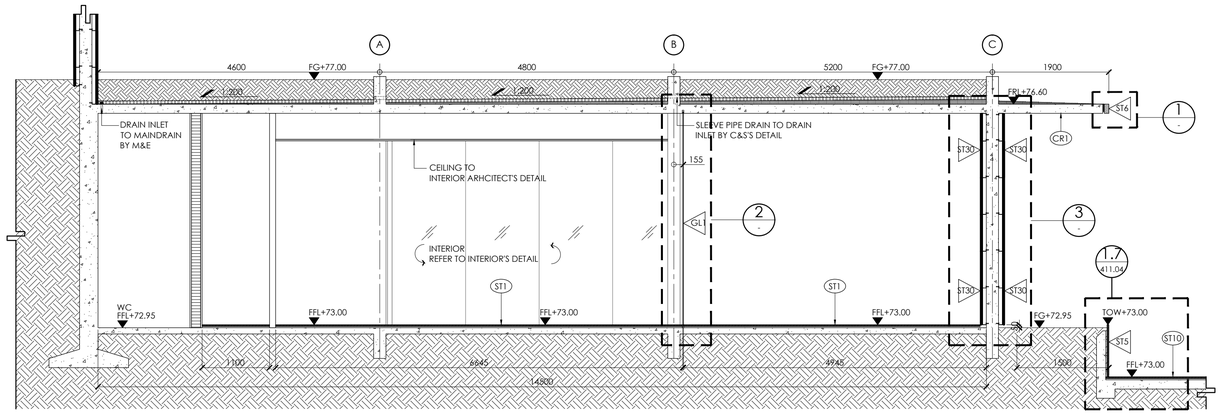


A 301.01 BLOW-UP 01 : GUARD HOUSE SECTION A
1:50

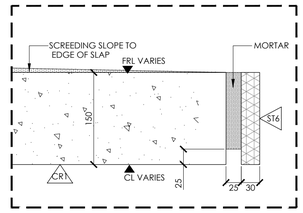


1 - ROOF EDGE TYPICAL DETAIL
1:5

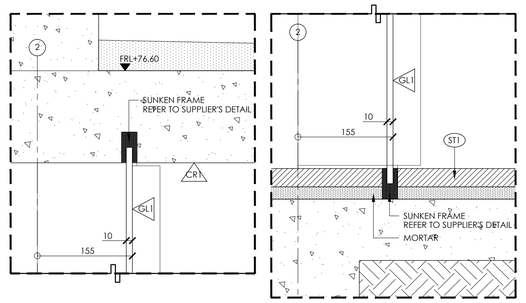


2 - GLASS TYPICAL DETAIL
1:5

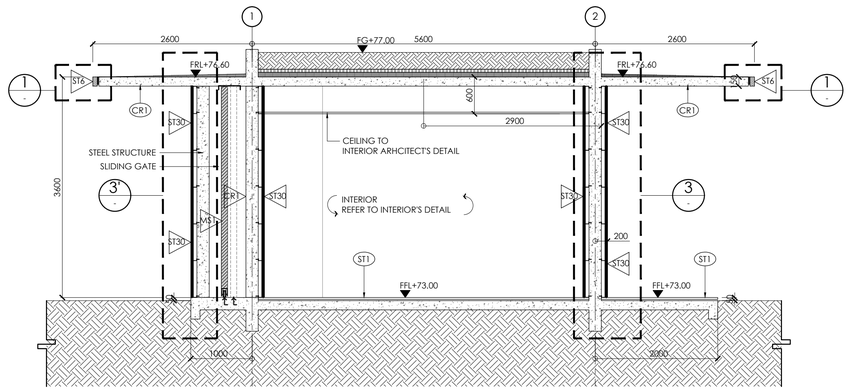


B 301.01 BLOW-UP 01 : GUARD HOUSE SECTION B
1:50

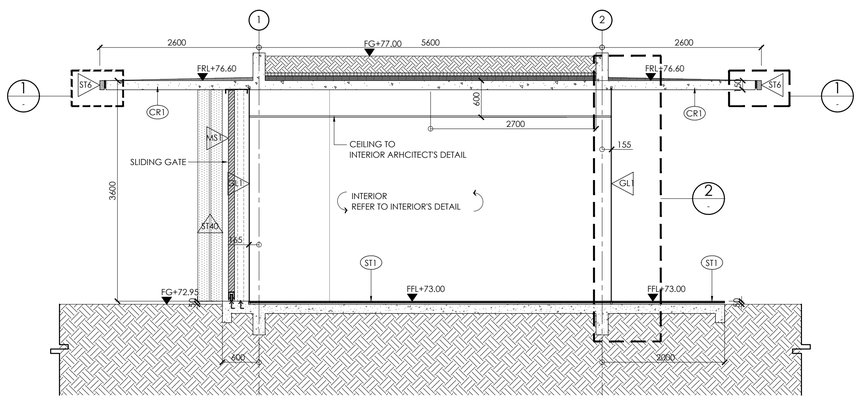

C 301.01 BLOW-UP 01 : GUARD HOUSE SECTION C
1:50

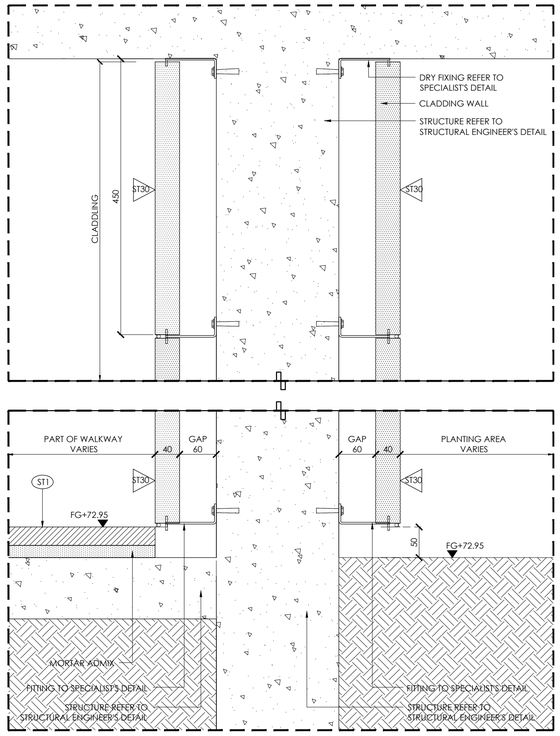

3 - CLADDING WALL TYPICAL DETAIL TYPE 1
1:5

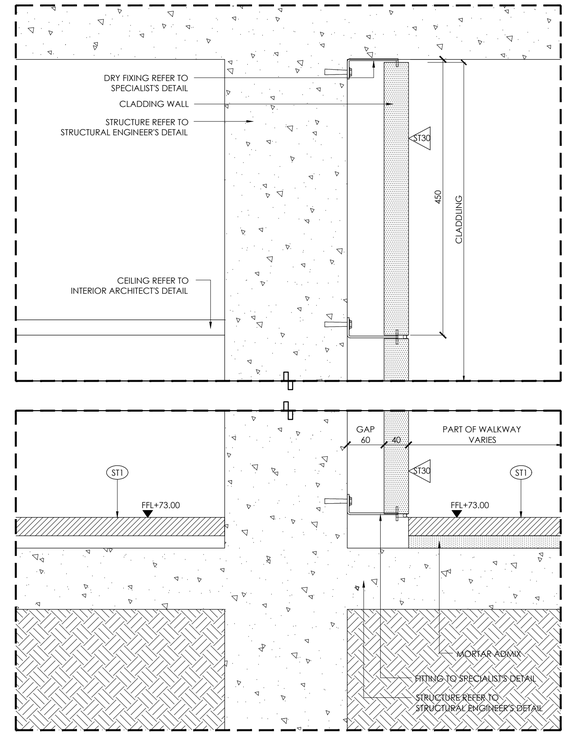

4 - CLADDING WALL TYPICAL DETAIL TYPE 2
1:5

NOTES

1. Shma Co., Ltd. All rights reserved.
   No copy is allowed without written permission from Shma.
2. All dimensions are to be carefully checked by the contractor.
   All adjustments must be made before
   commencement of works or frabrication of fittings.

LANDSCAPE ARCHITECT

Shma Co., Ltd.
93/2 Ekkamai 3 Sukhumvit 63 Rd.
Klongton Nuer Vadhana
Bangkok Thailand 10110
TEL:662 390 1977 Fax:662 390 1974
Email: admin@shmadesigns.com

CLIENT / OWNER


LUPIN LIMITED
MUMBAI

ARCHITECT


Venkataramanan Associates
ARCHITECTURE - URBAN DESIGN
10/2 , O'SHAUGHNESSY ROAD, LANGFORD GARDENS, BANGALORE– 560 025

PROJECT TITLE : LUPIN RESEARCH PARK, PUNE, INDIA


JOB NO.	315	DATE	17.08.15	PROJECT LA	DRAWING NAME	DRAWING NO.	ISSUED FOR	STAGE	REV	DESCRIPTION	NORTH
SCALE	A0 -	CHECKED BY	PRAPAN	PRAPAN NAPAWONGDEE	*BLOW-UP 01*						
	A1 *AS SHOWN*	DRAWN BY	KATAVET	KATAVET SITTIKIT	*GUARD HOUSE*	*301.06*	CONSTRUCTION	GFC			
	A3 -			KRITTAYA and PAT	*SECTION A,B,C AND DETAIL*						

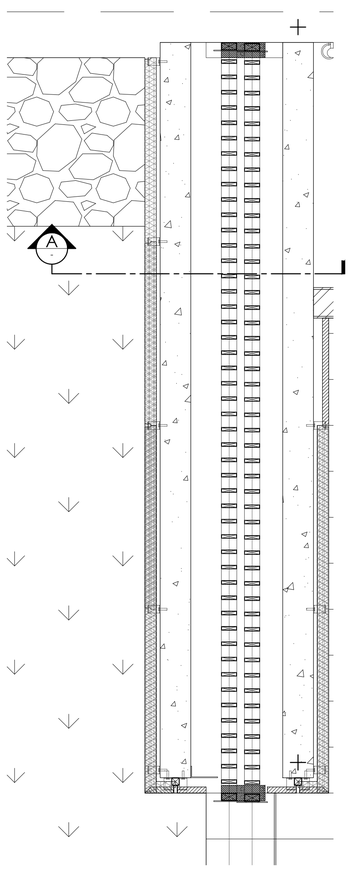


1 301.01 SLIDING DOOR PLAN (OPEN) 1:20

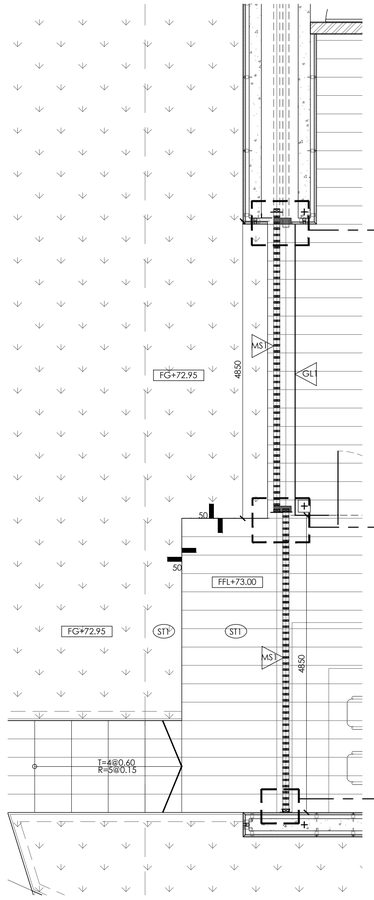


2 301.01 SLIDING DOOR PLAN (CLOSE) 1:50

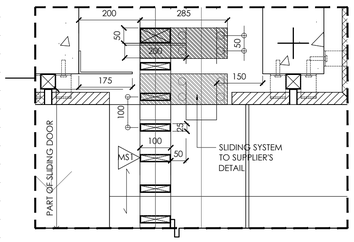


3.1 TYPICAL DETAIL 1:10

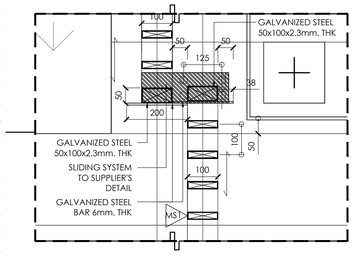


3.2 TYPICAL DETAIL 1:10

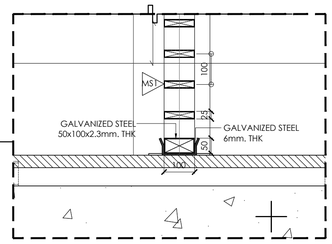

3.3 TYPICAL DETAIL 1:10

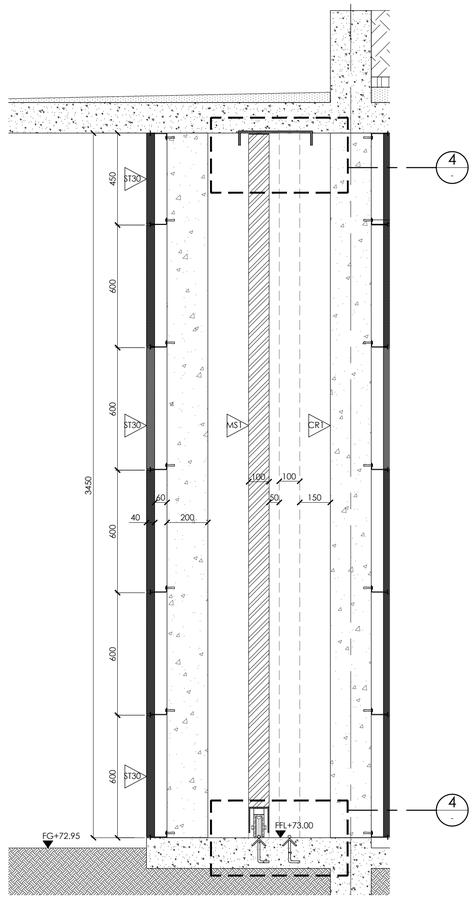

A - SECTION A 1:15

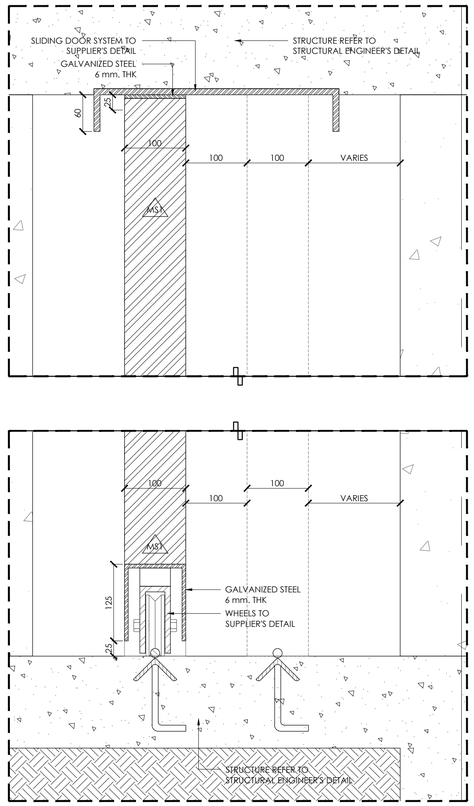


4 - TYPICAL DETAIL 1:5


NOTES	LANDSCAPE ARCHITECT	CLIENT / OWNER	ARCHITECT
1. Shma Co., Ltd. All rights reserved. No copy is allowed without written permission from Shma. 2. All dimensions are to be carefully checked by the contractor. All adjustments must be made before commencement of works or frabrication of fittings.	Shma Co., Ltd. 93/2 Ekkamai 3 Sukhumvit 63 Rd. Klongton Nuer Vadhana Bangkok Thailand 10110 TEL:662 390 1977 Fax:662 390 1974 Email: admin@shmadesigns.com	**LUPIN LIMITED** MUMBAI	**Venkataramanan Associates** ARCHITECTURE - URBAN DESIGN 10/2 , O'SHAUGHNESSY ROAD, LANGFORD GARDENS, BANGALORE– 560 025

PROJECT TITLE : LUPIN RESEARCH PARK, PUNE, INDIA


JOB NO.	315	DATE	17.08.15	PROJECT LA	PRAPAN NAPAWONGDEE	DRAWING NAME	DRAWING NO.	ISSUED FOR	STAGE	REV	DESCRIPTION	NORTH
SCALE	A0 -	CHECKED BY	PRAPAN	PRAPAN NAPAWONGDEE		*BLOW-UP 01*						
	A1 *AS SHOWN*	DRAWN BY	KATAVET	KATAVET SITTIKIT		*MAIN ENTRANCE*	*301.07*	CONSTRUCTION	GFC			
	A3 -			KRITTAYA and PAT		*SLIDING DOOR DETAIL*						

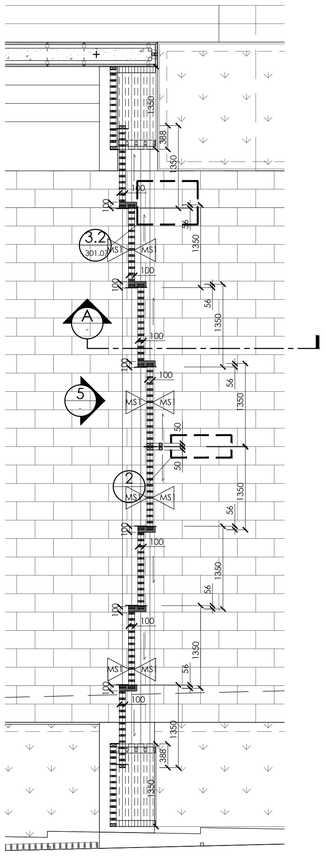


1 301.01 SLIDING GATE PLAN @MAIN ENTRANCE (CLOSE)
1:50

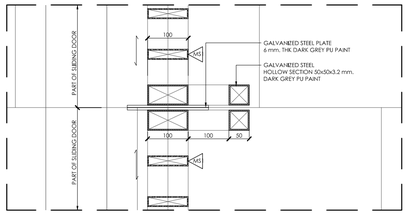


2 - SLIDING GATE TYPICAL DETAIL
1:5

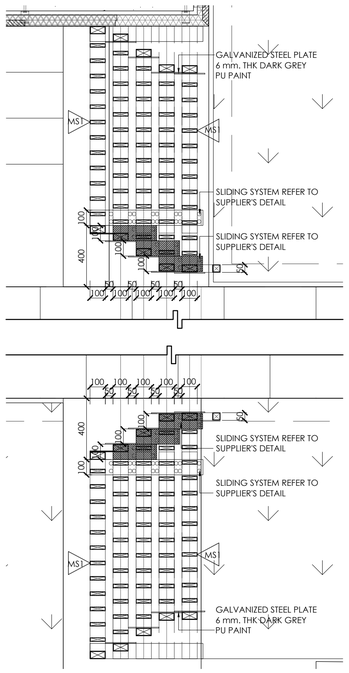


3 - SLIDING GATE PLAN @MAIN ENTRANCE (OPEN)
1:20

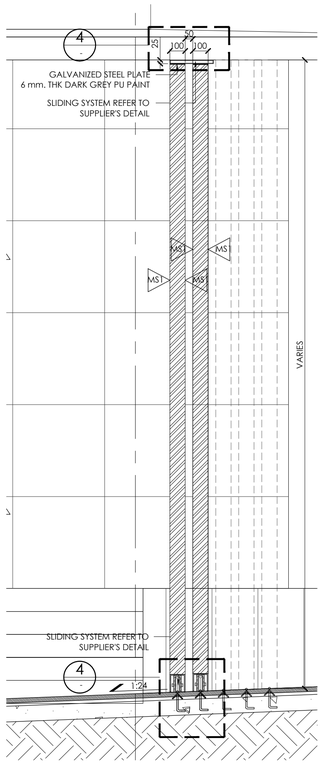

A - SECTION A
1:20

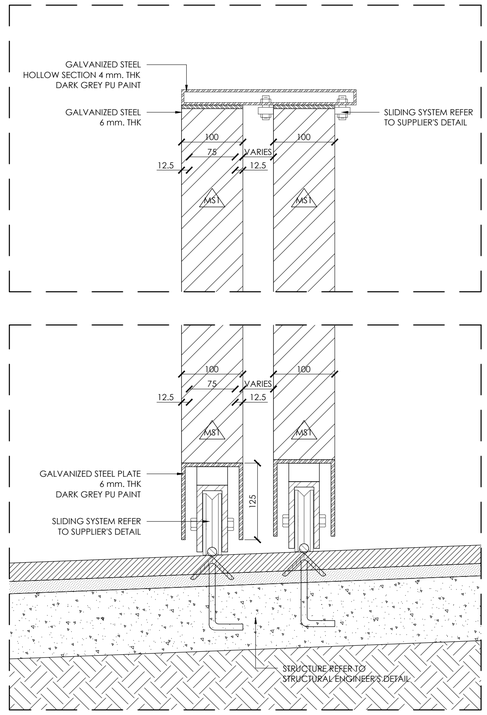

4 - TYPICAL DETAIL
1:5

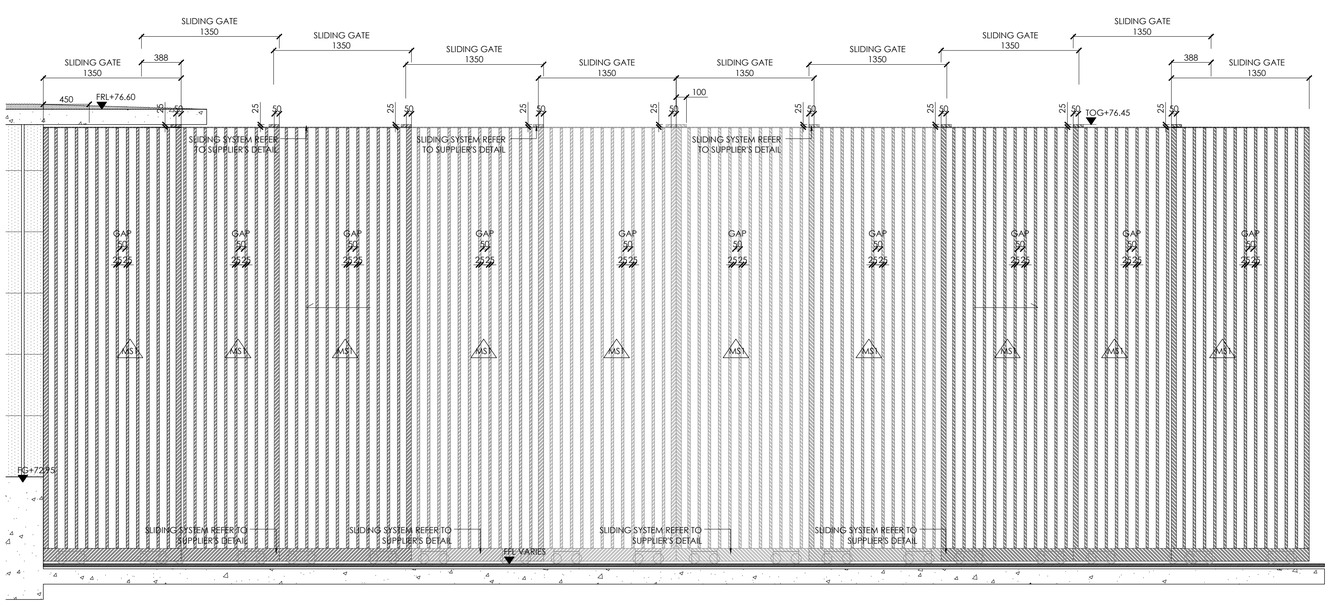

5 - SLIDING GATE ELEVATION
1:30

NOTES

1. Shma Co., Ltd. All rights reserved.
   No copy is allowed without written permission from Shma.
2. All dimensions are to be carefully checked by the contractor.
   All adjustments must be made before commencement of works or frabrication of fittings.

LANDSCAPE ARCHITECT

Shma Co., Ltd.
93/2 Ekkamai 3 Sukhumvit 63 Rd.
Klongton Nuer Vadhana
Bangkok Thailand 10110
TEL:662 390 1977 Fax:662 390 1974
Email: admin@shmadesigns.com

CLIENT / OWNER

LUPIN LIMITED
MUMBAI

ARCHITECT

Venkataramanan Associates
ARCHITECTURE - URBAN DESIGN
10/2 , D'SHAUGHNESSY ROAD, LANGFORD GARDENS, BANGALORE– 560 025

PROJECT TITLE : LUPIN RESEARCH PARK, PUNE, INDIA

JOB NO.	315	**DATE**	17.08.15	**PROJECT LA**	PRAPAN NAPAWONGDEE	**DRAWING NAME**	**DRAWING NO.**	**ISSUED FOR**	**STAGE**	**REV**	**DESCRIPTION**	**NORTH**
SCALE	**A0** -	**CHECKED BY**	PRAPAN			*BLOW-UP 01*						
	A1 *AS SHOWN*	**DRAWN BY**	KATAVET	KATAVET SITTIKIT		*MAIN ENTRANCE*	*301.08*	CONSTRUCTION	GFC			
	A3 -			KRITTAYA and PAT		*SLIDING GATE DETAIL*						