CAPACITY	15 TON
PLATFORM SIZE	2500(L) X 2000(W)
POWER PACK	15 HP, 3 PH
SHUT HEIGHT	1000 MM
LIFT HEIGHT	1200 MM
OPEN HEIGHT	2200 MM
RAILING	1000 MM HEIGHT

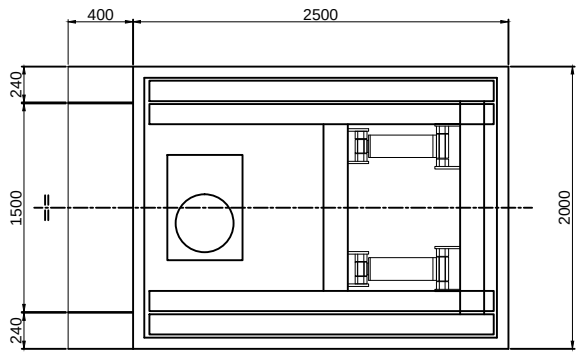

PLAN VIEW

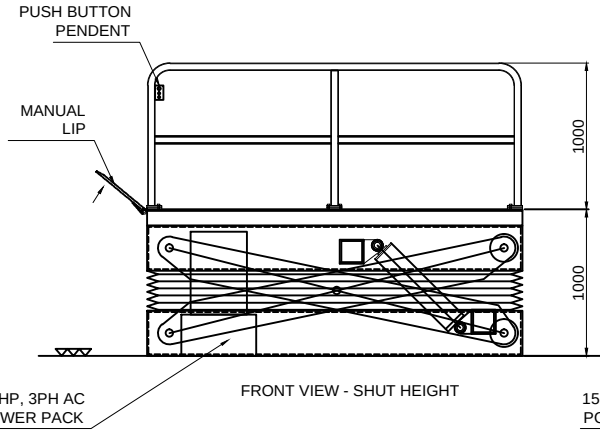

FRONT VIEW - SHUT HEIGHT

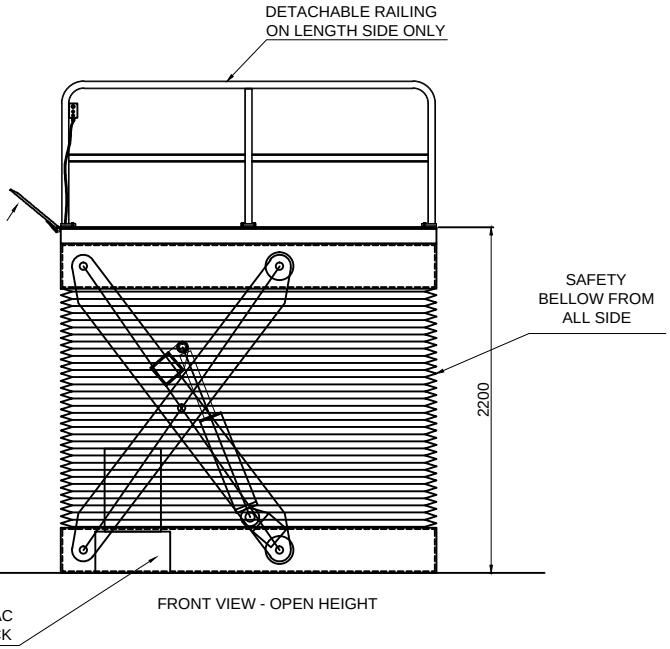

FRONT VIEW - OPEN HEIGHT

NOTE :
1. CONTROL PANEL MOUNTING WILL BE 5 MTR AWAY FROM PIT LOCATION.
2. ALL REQ. TECHNICAL CIVIL WORK WILL BE IN CLIENT SCOPE.

REV NO	DATE	DRAWN	REMARK
R01	11.09.20	P.A	1. POWER PACK LOCATION CHANGE

This drawing & designing is the property of NIHVA TECHNOLOGIES. Not to be sold or copied to any other concern.

TITLE: ELECTRO HYDRAULIC SCISSOR LIFT

NIHVA TECHNOLOGIES PVT. LTD.
NIHVA TECHNOLOGIES PVT. LTD. PUNE
Tel : 020 66304033
Email:- info@nihva.com
Website:- www.nihva.com

	NAME	SIGN	DATE
DRAWN	P.A		27.02.20
CHECK	G.J		27.02.20
APPROVAL			

CLIENT - Endress + Hauser Flowtec (India) Pvt. Ltd.
PROJECT - Endress + Hauser Flowtec (India) Pvt. Ltd.
SITE LOCATION - AURANGABAD
If any queries contact : design@nihva.com
DWG. NO. : NIHVA/19-20/0225/R01 | REV- R01
ALL DIMENSION ARE IN mm
SCALE: NTS | WT: | SHEET: 01 OF 01