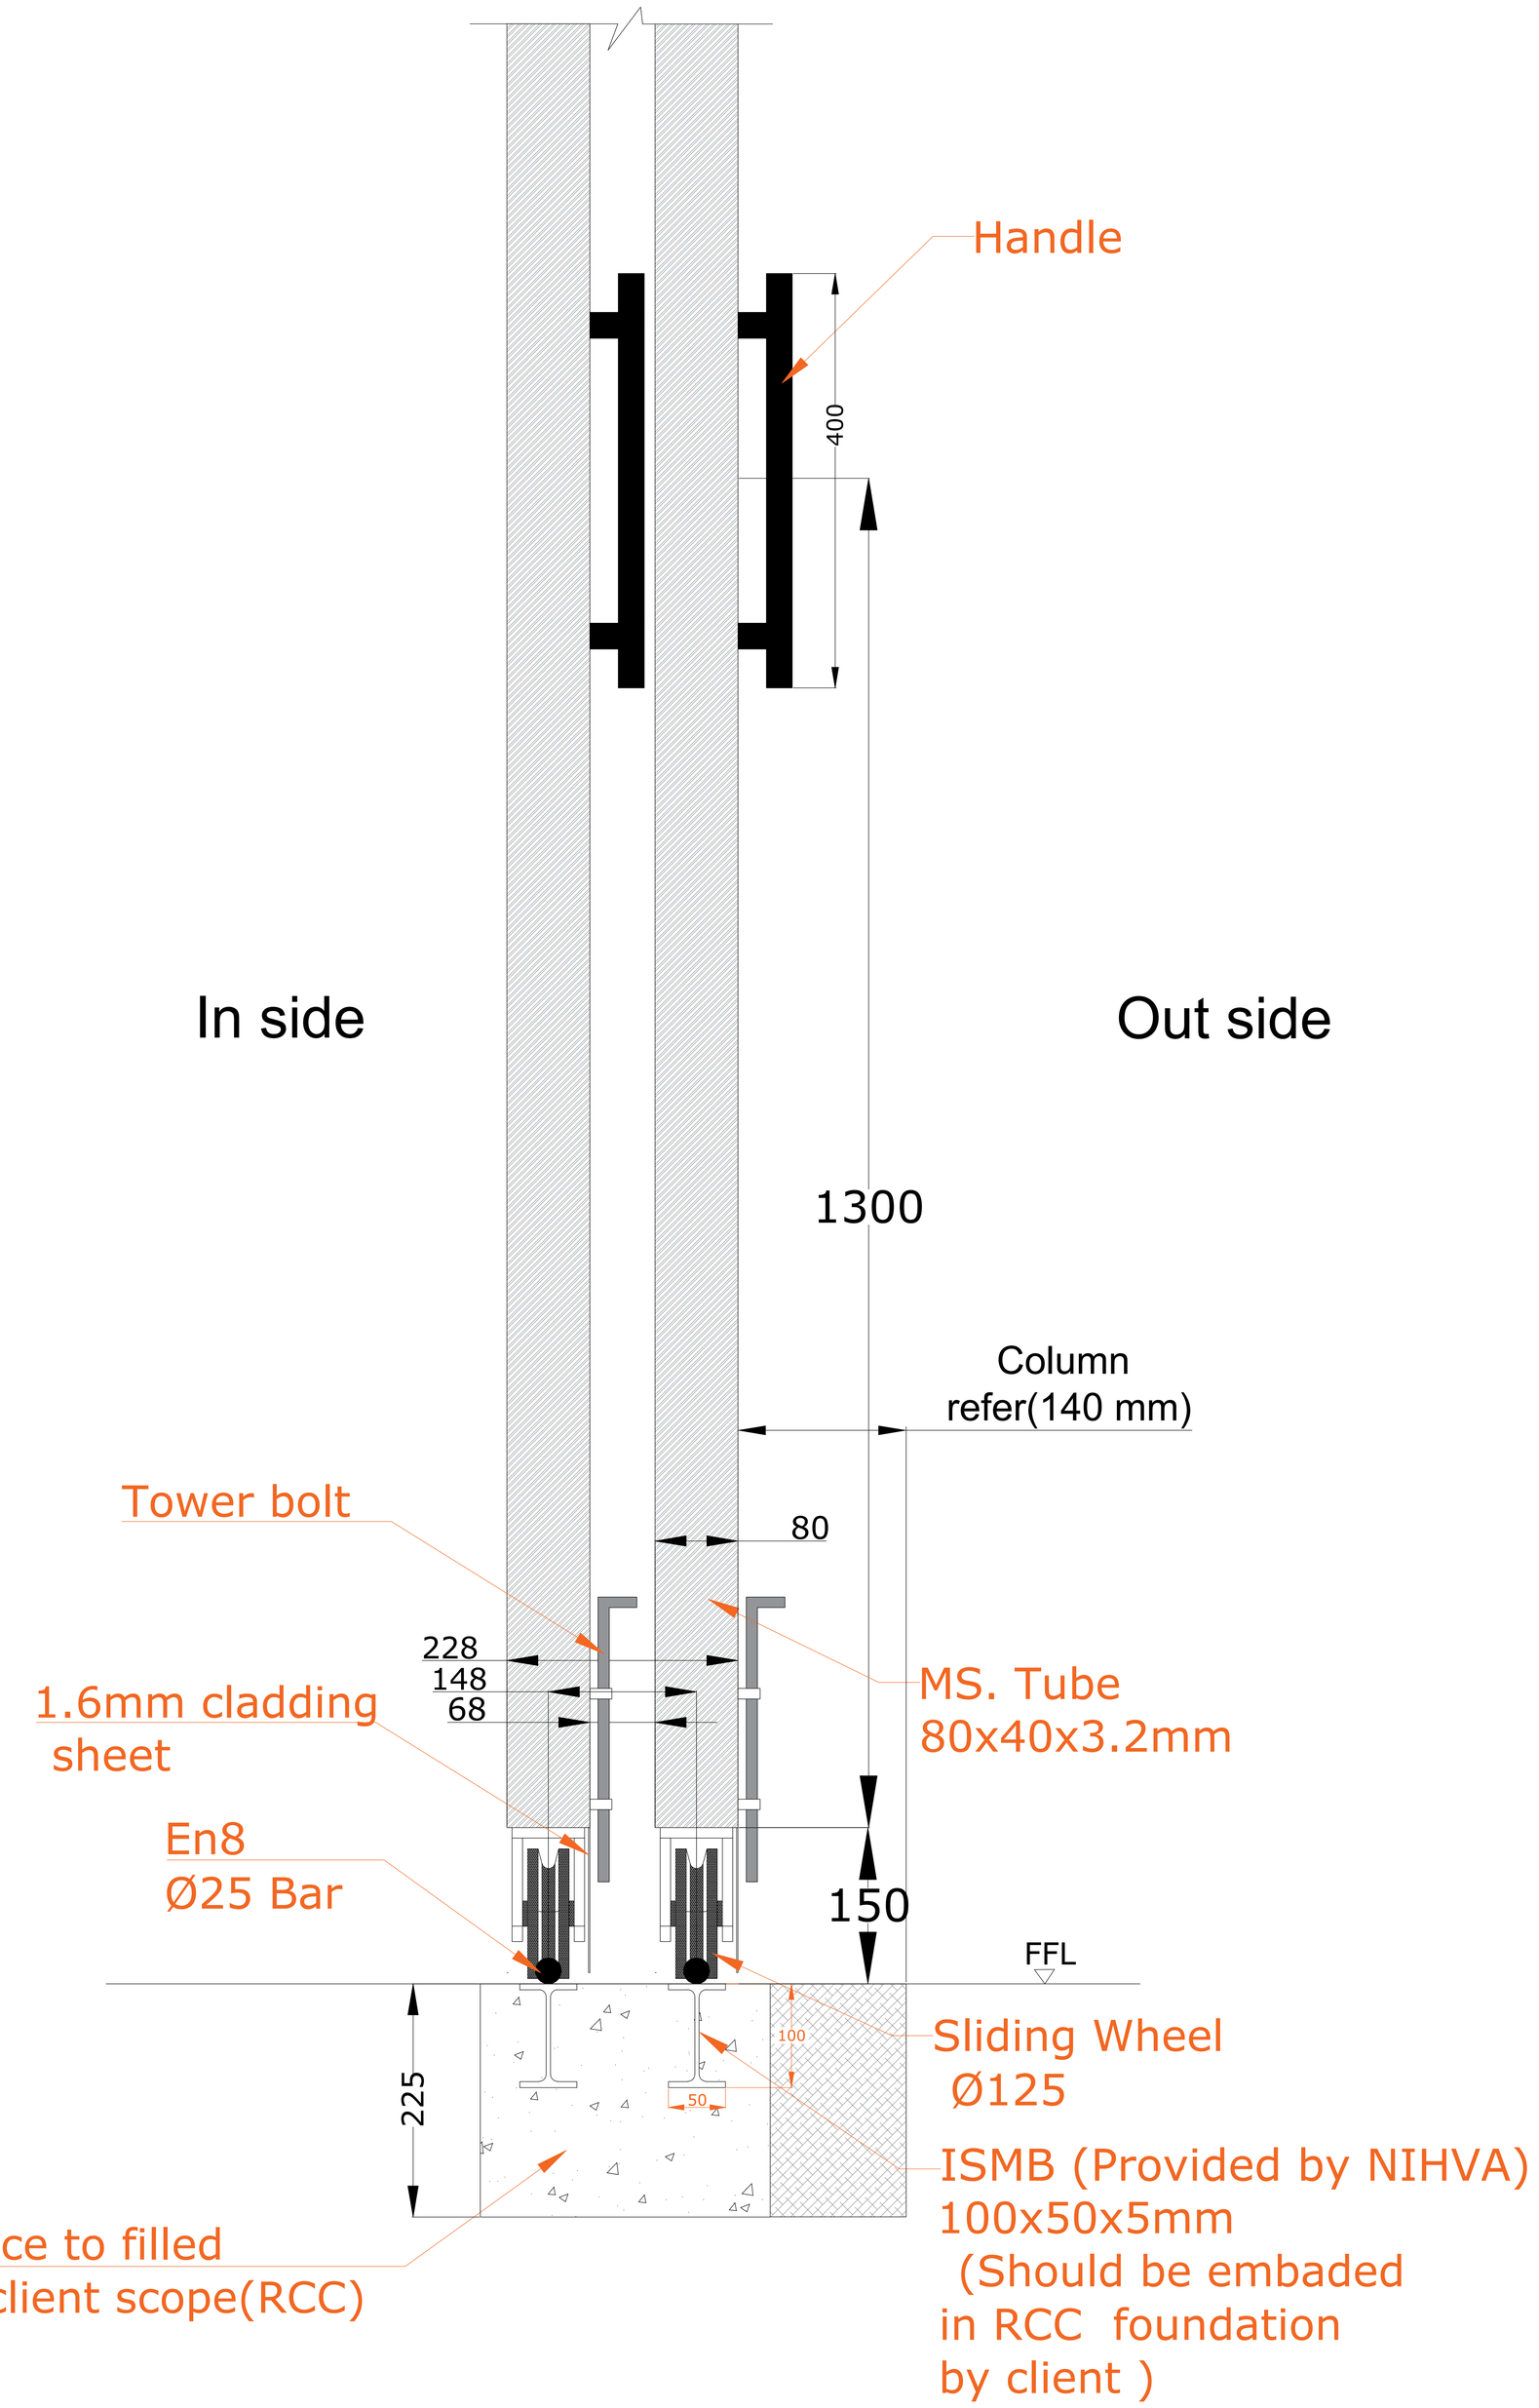


This drawing & designing is the property of NIHVA TECHNOLOGIES. Not to be sold or copied to any other concern.

TITLE :- Manual sliding gate bottom foundation			NIHVA TECHNOLOGIES PVT. LTD. PUNE NIHVA TECHNOLOGIES PVT. LTD. Tel : 020 66304033 Email:- info@nihva.com Website:- www.nihva.com
	NAME	DATE	CLIENT - Panchashil
DRAWN	S.J	26/08/2024	PROJECT - Manual Sliding Gate
CHECK	B.B.	26/08/2024	FORMAT NO :-NIHVA-DD-F-03
APPROVAL	V.T.	26/08/2024	DWG. NO. : NIHVA/23-24/XX REV-03
			SCALE: NTS WT: SHEET: 01 OF 01
ALL DIMENSION ARE IN mm			If any queries contact : design@nihva.com