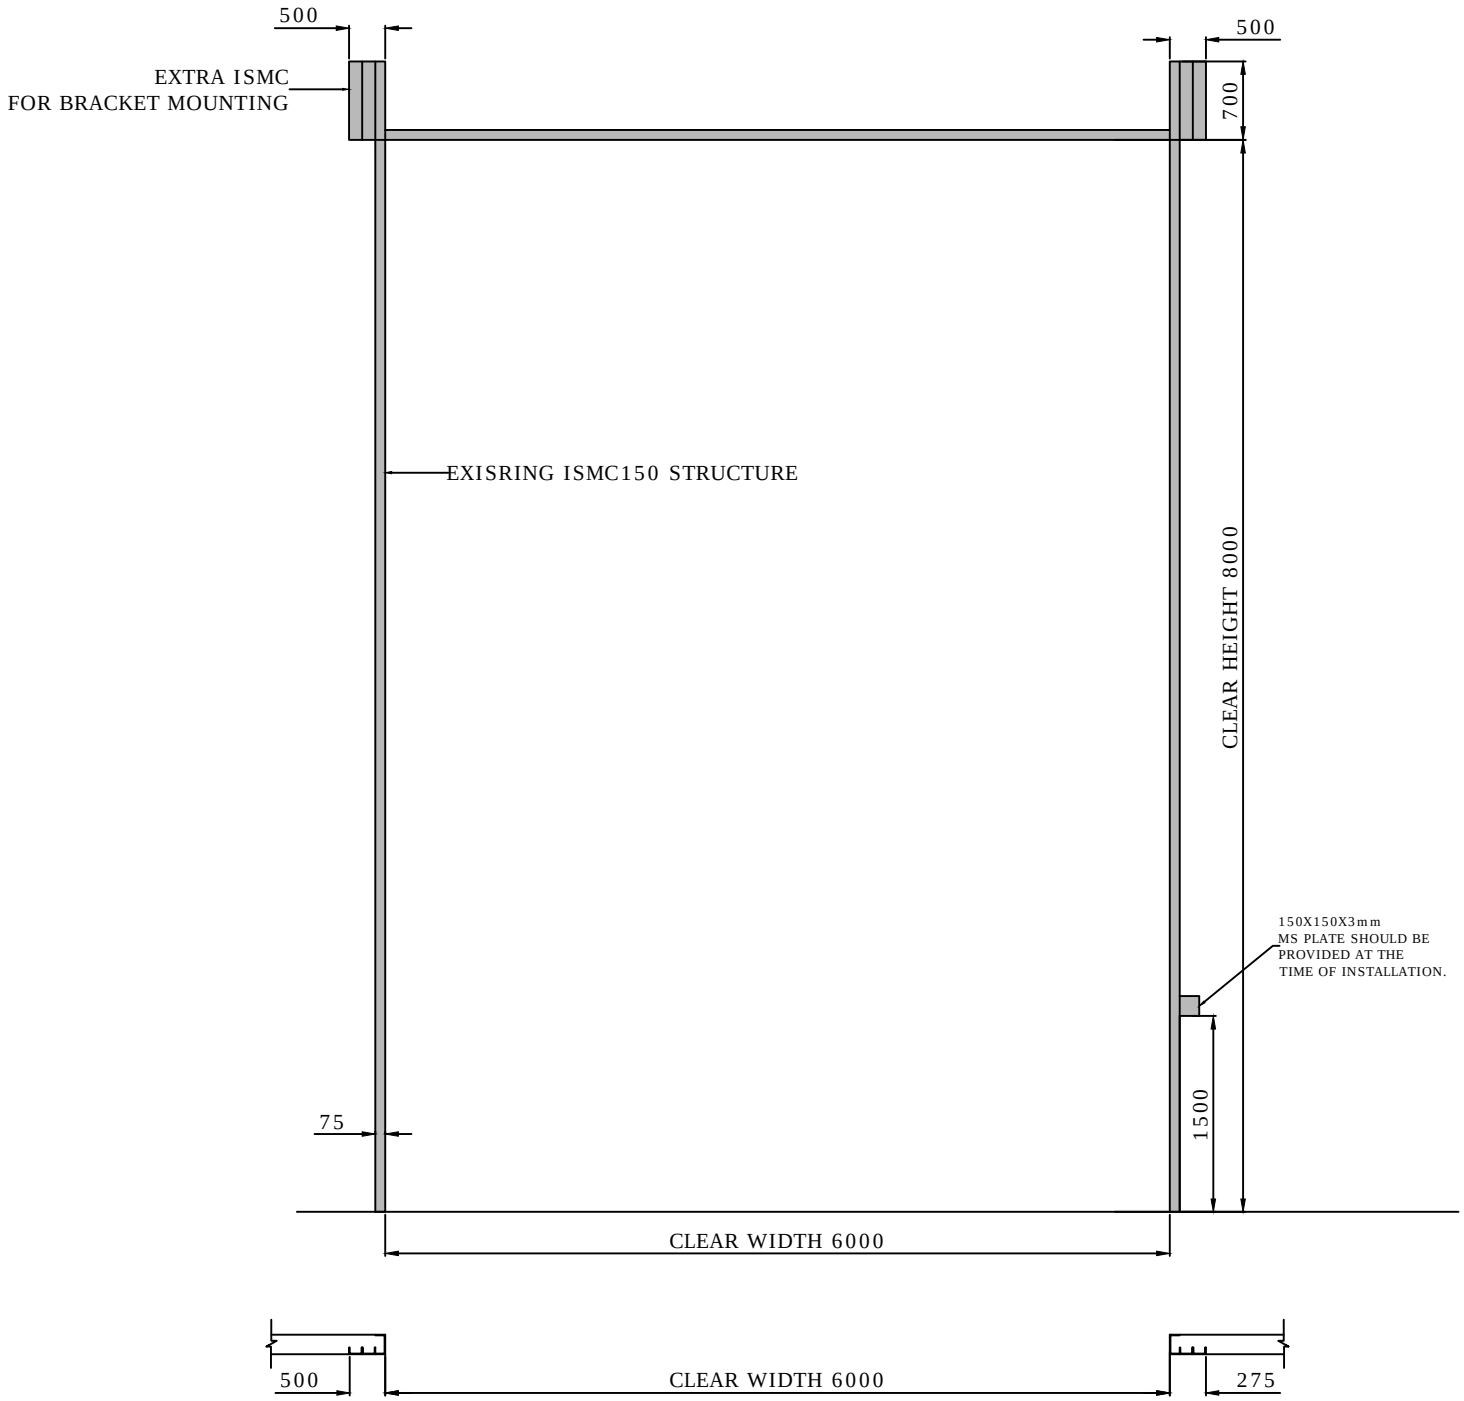


DIMENSION :

| CLEAR WIDTH | CLEAR HEIGHT | QUANTITY |
|---|---|---|
| 6000 mm | 8000 mm | 02 NOS. |

MATERIAL :

THICKNESS :

NIHVA TECHNOLOGIES PVT. LTD.

NIHVA TECHNOLOGY
PVT. LTD. PUNE
Email:- info@nihva.com
Website:- www.nihva.com

TITLE:

STRUCTURE FOR
MOTORIZED ROLLING SHUTTER
6X8m

CLIENT'S APPROVAL :

CLIENT - SURAJ BUILDCON PVT. LTD

PROJECT - KSB

SITE LOCATION - SHIRWAL MIDC

DWG. NO. : NIHVA/16-17/115

| SCALE: NTS | WT: | SHEET:1 OF 1 |
|---|---|---|

| DRAWN BY: OMKAR | DATE: 20-12-2016 |
|---|---|
| CHECK : SAGAR P. | DATE: 20-12-2016 |

If any queries contact : projects@nihva.com

NOTE: ALL DIMENSION ARE IN mm

THIS DRAWING & DESIGNING IS THE PROPERTY OF NIHVA TECHNOLOGIES. NOT BE SOLD OR COPY TO ANY OTHER CONCERN.