
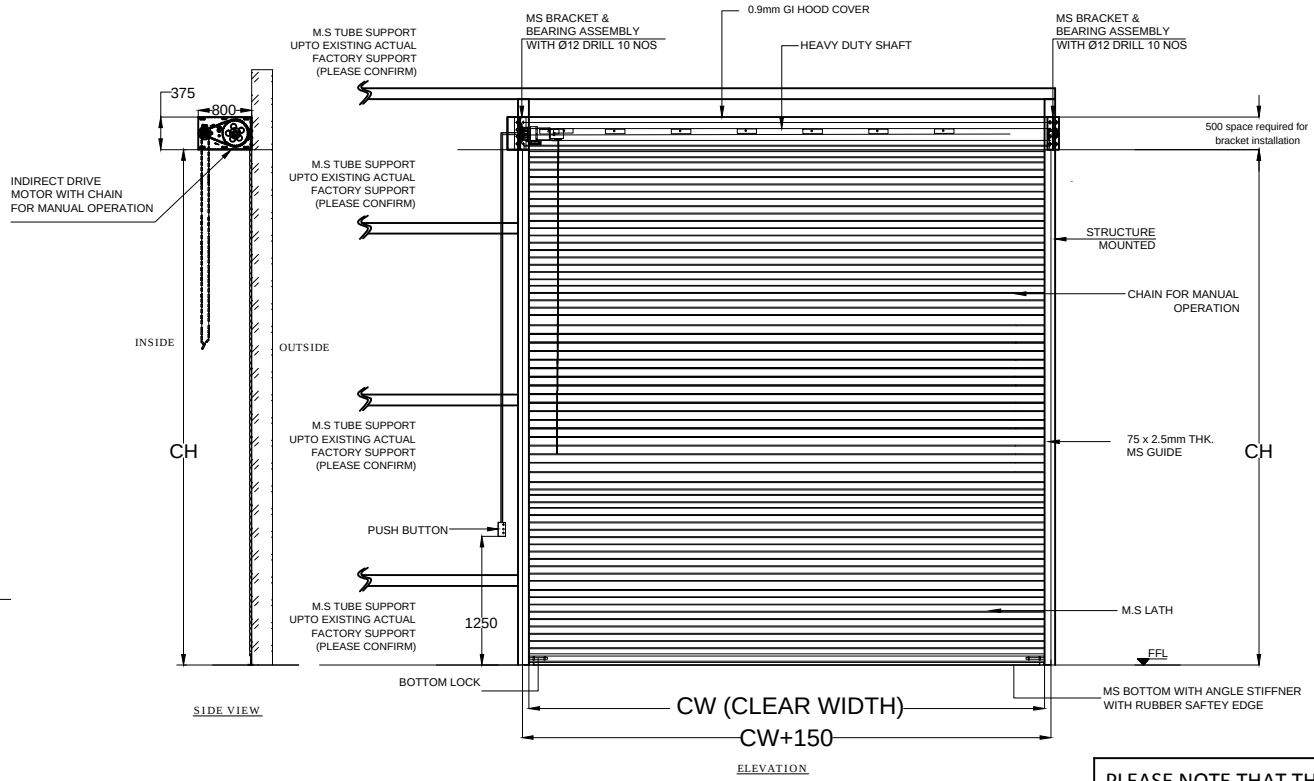
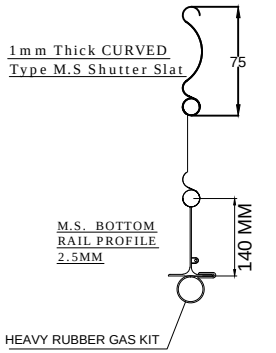
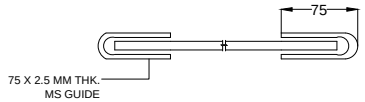



PLEASE NOTE THAT THE OPENING HEIGHT STRICTLY 2400 MM BELOW BOTTOM.

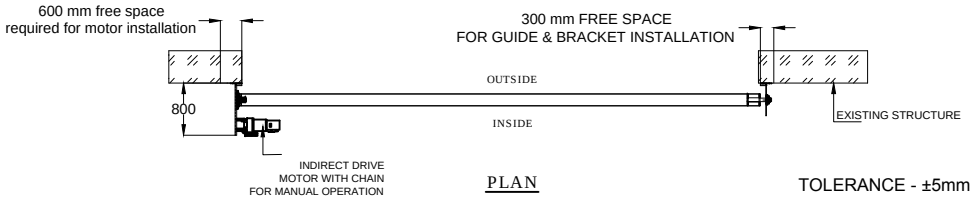


TOLERANCE - ±5mm

NOTE-
1. ALL CIVIL WORK & M.S STRUCTURE WILL BE CLIENT'S SCOPE.

| S.NO | RAL CODE | COLOR | CLEAR WIDTH | CLEAR HEIGHT | QTY. | MOUNTING |
|---|---|---|---|---|---|---|
| 01 | RAL 5002 | UM BLUE | 2500mm | 2500mm | 1 NO | STRUCTURE |

This drawing & design is the property of NIHVA TECHNOLOGIES. Not to be sold or copied to any other concern.

| TITLE | MOTORISED ROLLING SHUTTER | | |
|---|---|---|---|
| | NAME | SIGN | DATE |
| DRAWN | P.A | | 17.03.2020 |
| CHECK | G.J | | 17.03.2020 |
| APPRD. | | | |

NIHVA TECHNOLOGIES PVT. LTD.
Website:- www.nihva.com
NIHVA TECHNOLOGIES PVT. LTD. PUNE
Tel : 020 66304033
Email:- info@nihva.com

CLIENT -
PROJECT -
SITE LOCATION -
If any queries contact : design@nihva.com
DWG. NO. : NIHVA/19-20/VDR/373
REV- R00
ALL DIMENSION ARE IN mm
SCALE: NTS
WT:
SHEET: 01 OF 01