
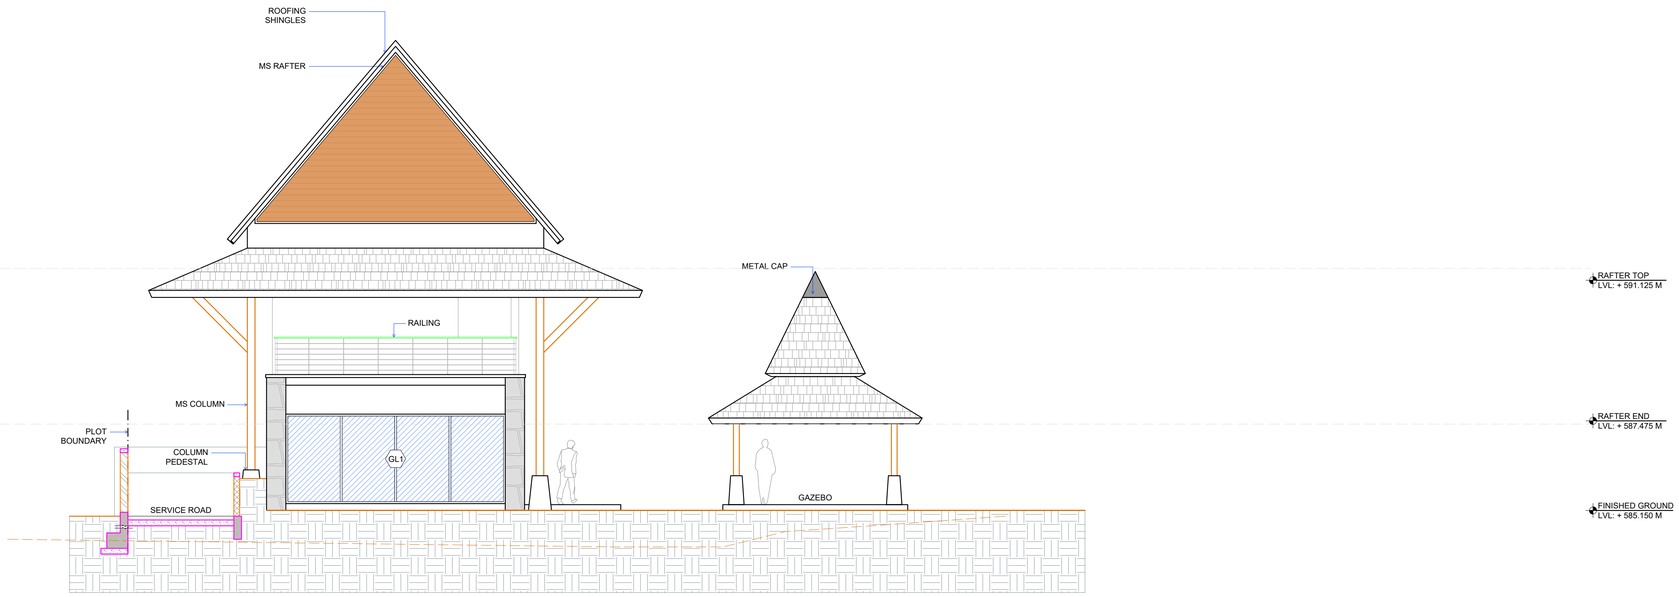


ELEVATION 01

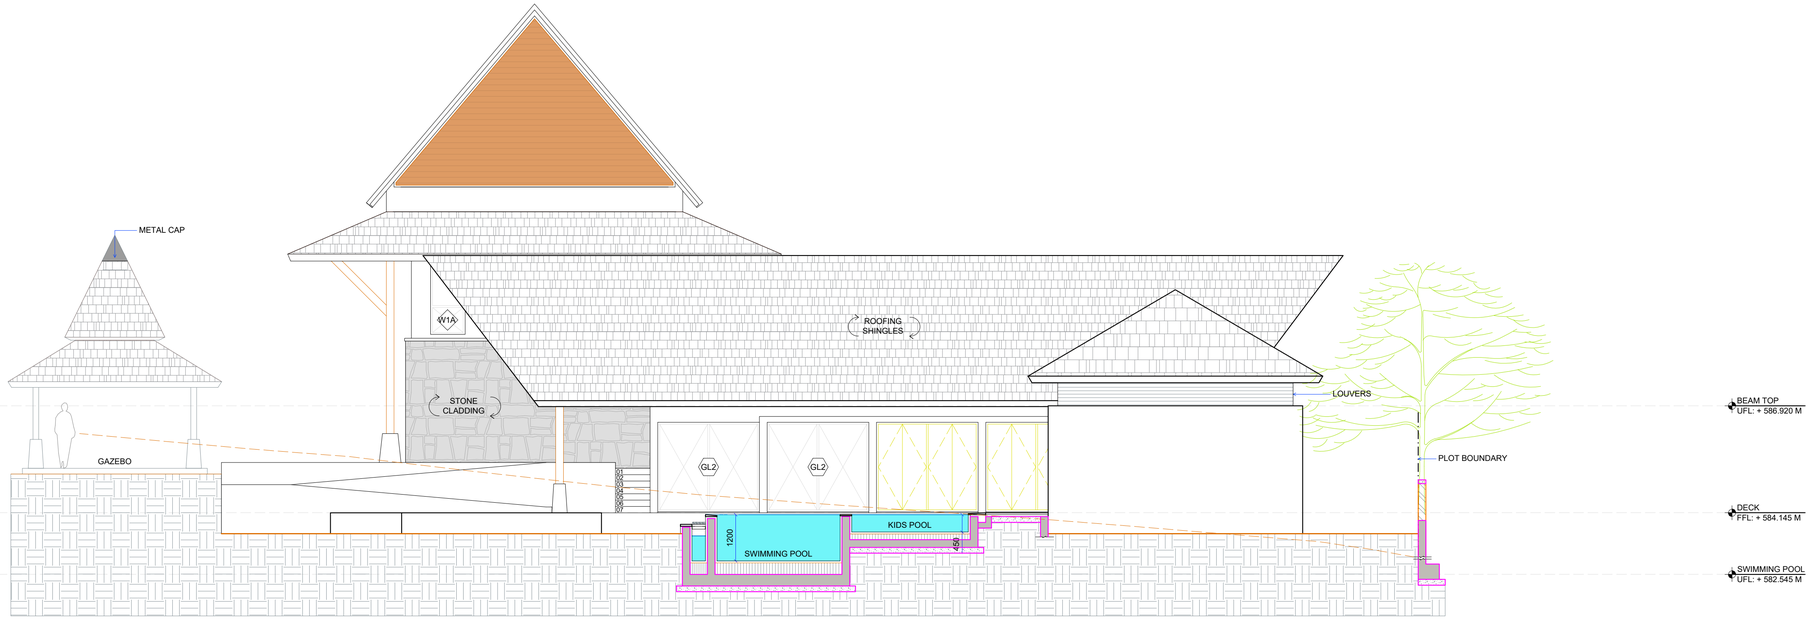

ELEVATION 03

PANCHSHIL REALTY
Pune: Tech Park One, Tower "E", 191 Yerwada, Pune 411 006

ISSUES

SITE	RCC	LANDSCAPE	INTERIOR	SERVICES	

REVISIONS

REV. NO.	DATE	DESCRIPTION	DRN BY	CHKD BY

REVISIONS

REV. NO.	DATE	DESCRIPTION	DRN BY	CHKD BY

NOTES

1. ONLY WRITTEN DIMENSIONS TO BE FOLLOWED.
2. ALL DIMENSIONS ARE IN MILLIMETERS AND LEVELS IN METERS UNLESS OTHERWISE SPECIFIED.
3. ALL LEVELS/ DIMENSIONS ARE FROM UNFINISHED ARCHITECTURAL SURFACES.
4. FOR STRUCTURAL, SERVICES, LANDSCAPE & INTERIOR DETAILS REFER RELEVANT CONSULTANTS DRAWINGS.
5. DISCREPANCIES IF ANY TO BE BROUGHT TO THE NOTICE OF THE ARCHITECTS BEFORE EXECUTION.

DATE : 19-03-25

DEALT : PD

DRAWN BY : SB

SCALE : 1:75

PROJECT : BOUGAIN VILLA, LOHEGAON, PUNE

DRAWING TITLE : CLUBHOUSE - ELEVATIONS 01 & 03

JOB NO. PAN - 2332

DRAWING NO. XXXX

REVISION NO. XXXX