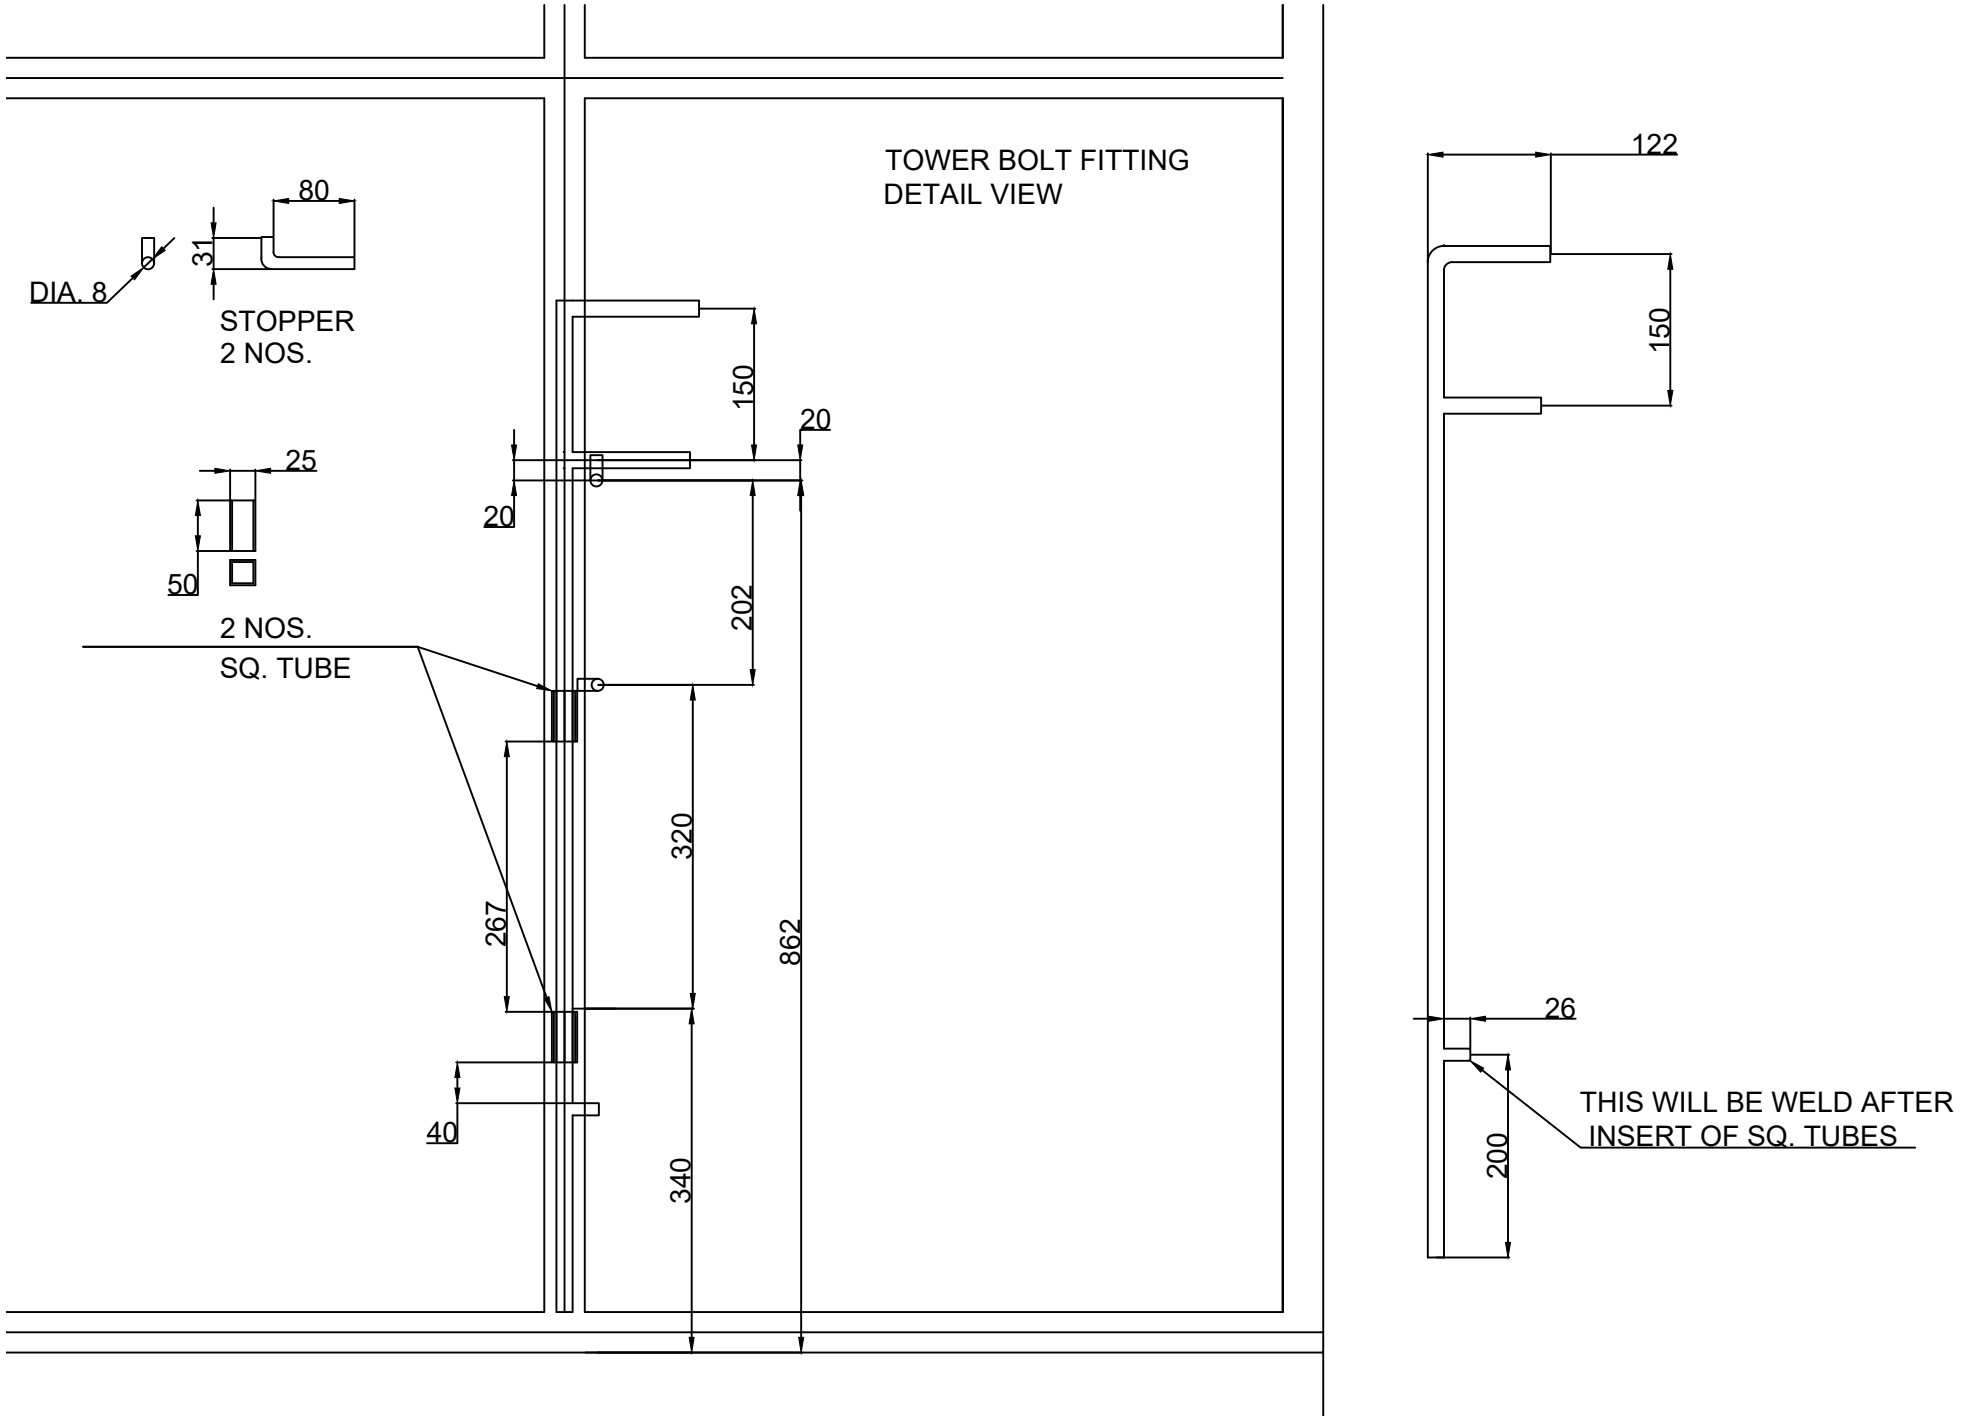

TOWER BOLT FITTING
DETAIL VIEW
80
31
DIA. 8
STOPPER
2 NOS.
25
50
2 NOS.
SQ. TUBE
150
20
20
202
320
267
862
40
340
122
150
26
THIS WILL BE WELD AFTER
INSERT OF SQ. TUBES
200