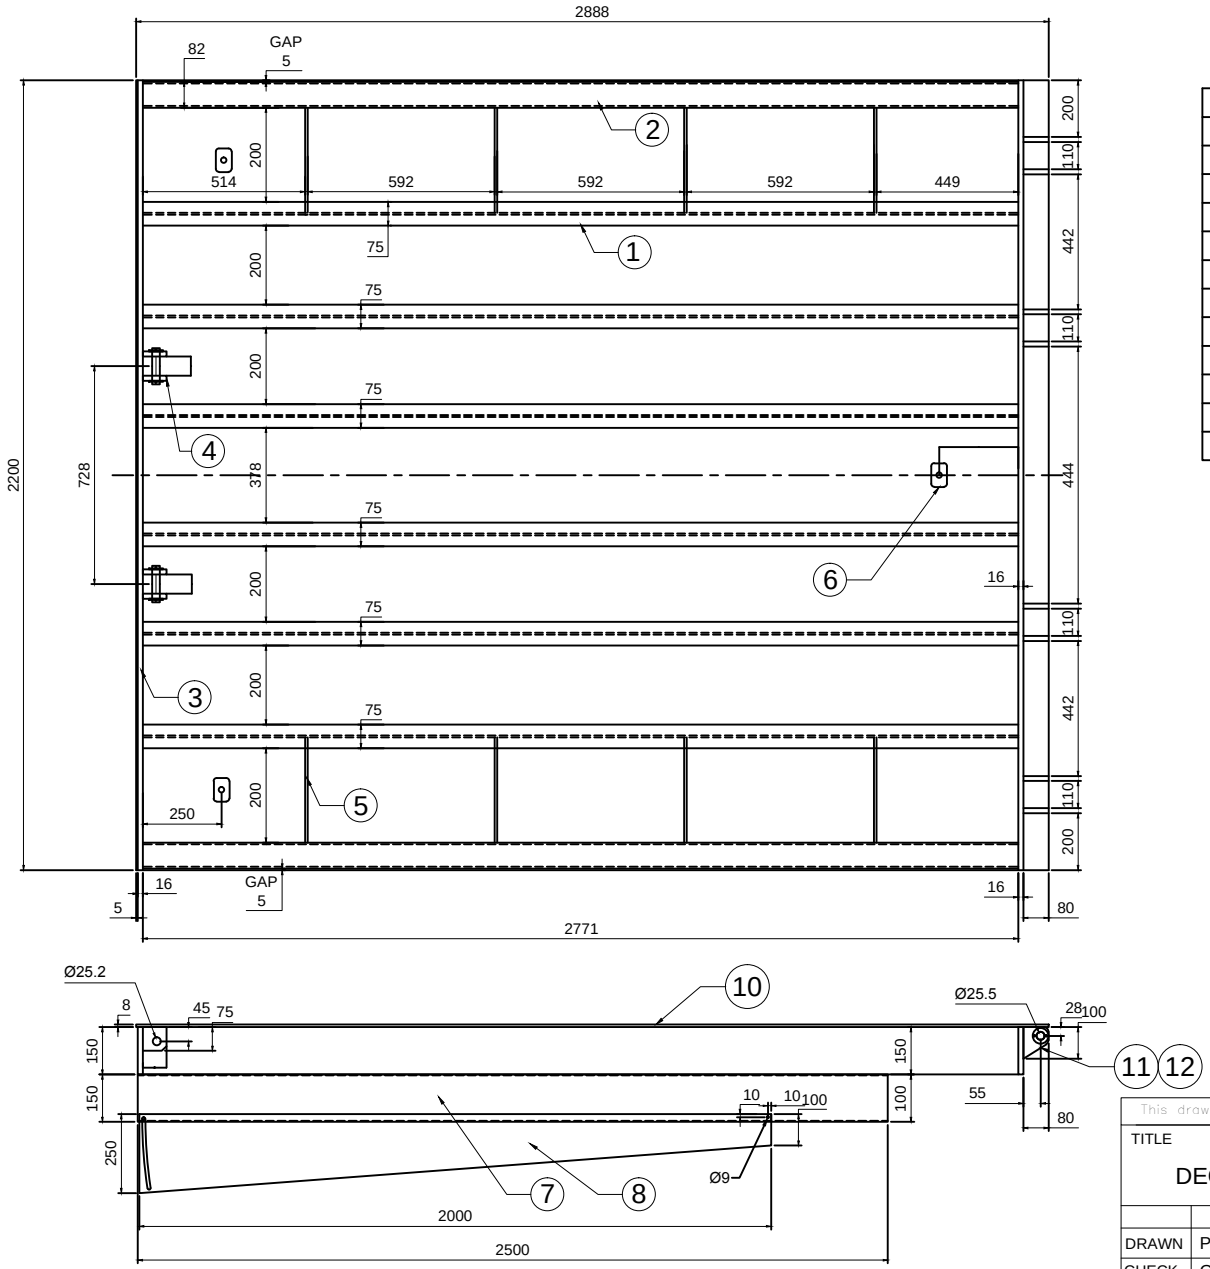


NOTE:~ MTL : MS

PART NO.	PART NAME	DESCRIPTION	QTY
1.	ISMB	150 X 75 X 2770L	6 NOS
2.	R.TUBE	145 X 82 X 4.8THK X 2770L	2 NOS
3.	FLAT	150 X 16 X 2200L	2 NOS
4.	FLAT	75 X 16 X 75L	4 NOS
5.	FLAT	150 X 8 X 234L	8 NOS
6.	FLAT	50 X 16 X 75L	3 NOS
7.	BEND	100 X 3THK X 2500L	2 NOS
8.	SIDE COVER	USE STD IN STOCK	2 NOS
9.	LIP STOPER	Ø25 X 53L	4 NOS
10.	CHEQ.SHEET	2200 X 8 THK X 2888L	1 NO
11.	PROFILE	80 X 16 THK X 100L	10 NOS
12.	PROFILE	50 X 5 THK	2 NOS

This drawing & design is the property of NIHVA TECHNOLOGIES. Not to be sold or copied to any other concern.

TITLE

DECK ASSLY

	NAME	SIGN	DATE
DRAWN	P.A		04.11.19
CHECK	G.J		04.11.19
APPRD.			

NIHVA TECHNOLOGIES PVT. LTD.
NIHVA TECHNOLOGIES PVT. LTD. PUNE
Tel : 020 66304033
Email:- info@nihva.com
Website:- www.nihva.com

CLIENT -

PROJECT -

SITE LOCATION -

If any queries contact : design@nihva.com

DWG. NO. : NIHVA/19-20/VDR/198

ALL DIMENSION ARE IN mm

SCALE: NTS | WT: | REV- 00