

THIS PRINT IS THE PROPERTY OF NIHVA IT IS TO BE USED ONLY FOR THE PURPOSE FOR WHICH IT WAS LENT AND MUST NOT BE USED IN ANY WAY DERTIMENTAL TO THE INTEREST OF THIS COMPANY AND IS SUBJECT TO RETURN ON DEMAND.

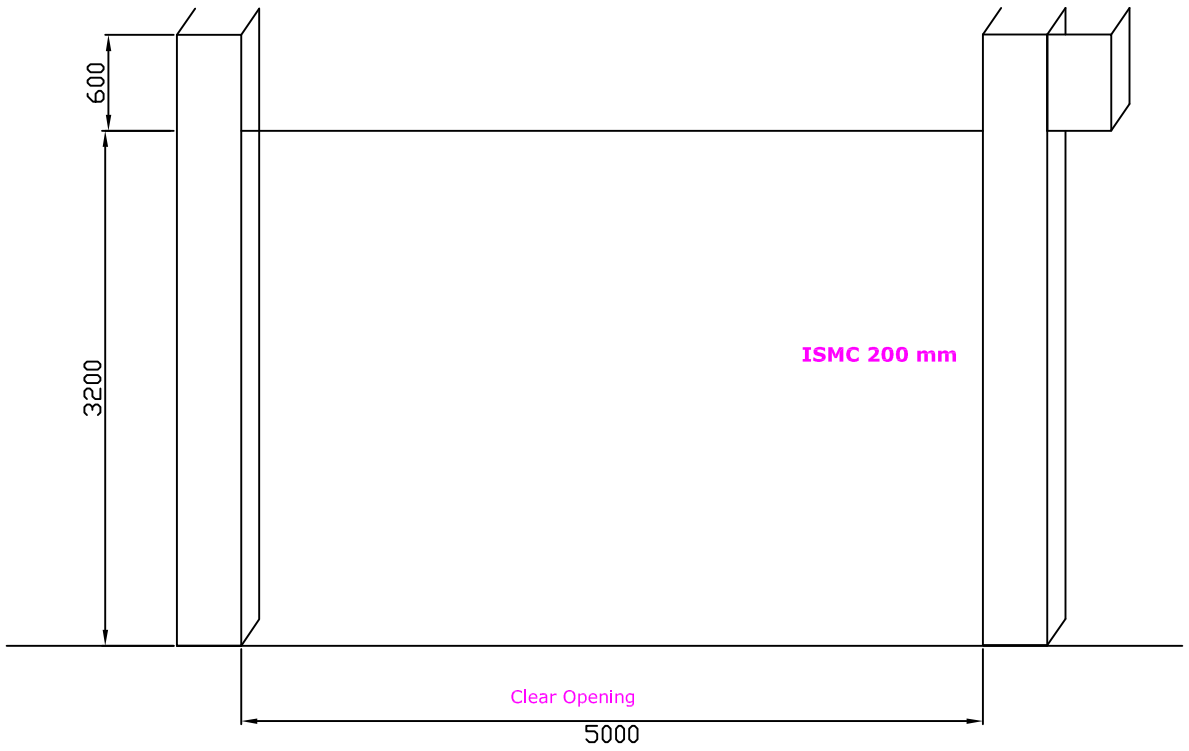

FRONT VIEW FROM INSIDE BUILDING

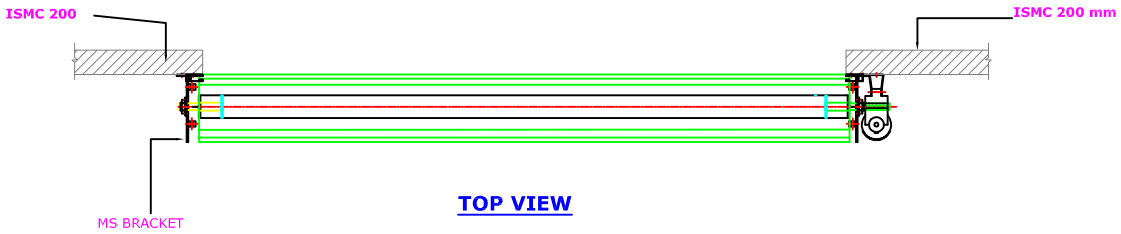

TOP VIEW

SIZE :- (W)5.0M X (H)3.2M

QTY :- 02 NOS

TITLE: MOTORISED DOUBLE WALL ROLLING SHUTTER	DO NOT SCALE DRAWING		NIHVA TECHNOLOGIES PVT. LTD. Pune-411044 Tel : 020 66304033 , Email:-info@nihva.com
		SIGN / DATE	
CLIENTS APPROVEL:–	DRAWN	ANIL	CLIENT: TATA MOTORS
	CHECK		PROJECT / SITE: PIMPRI
	ENG		PRODUCT NAME: MOTORISED DOUBLE WALL ROLLING SHUTTER
	APPRD.		
ALL DIMENSION ARE IN M.M.	PROD		
	MFG		DWG. NO.:– NVA / TATA MOTORS/ 0R1
If any queries CONTACT: projects@nihva.com	Ref. No.		SCALE: NTS SHEET: 1 OF 1