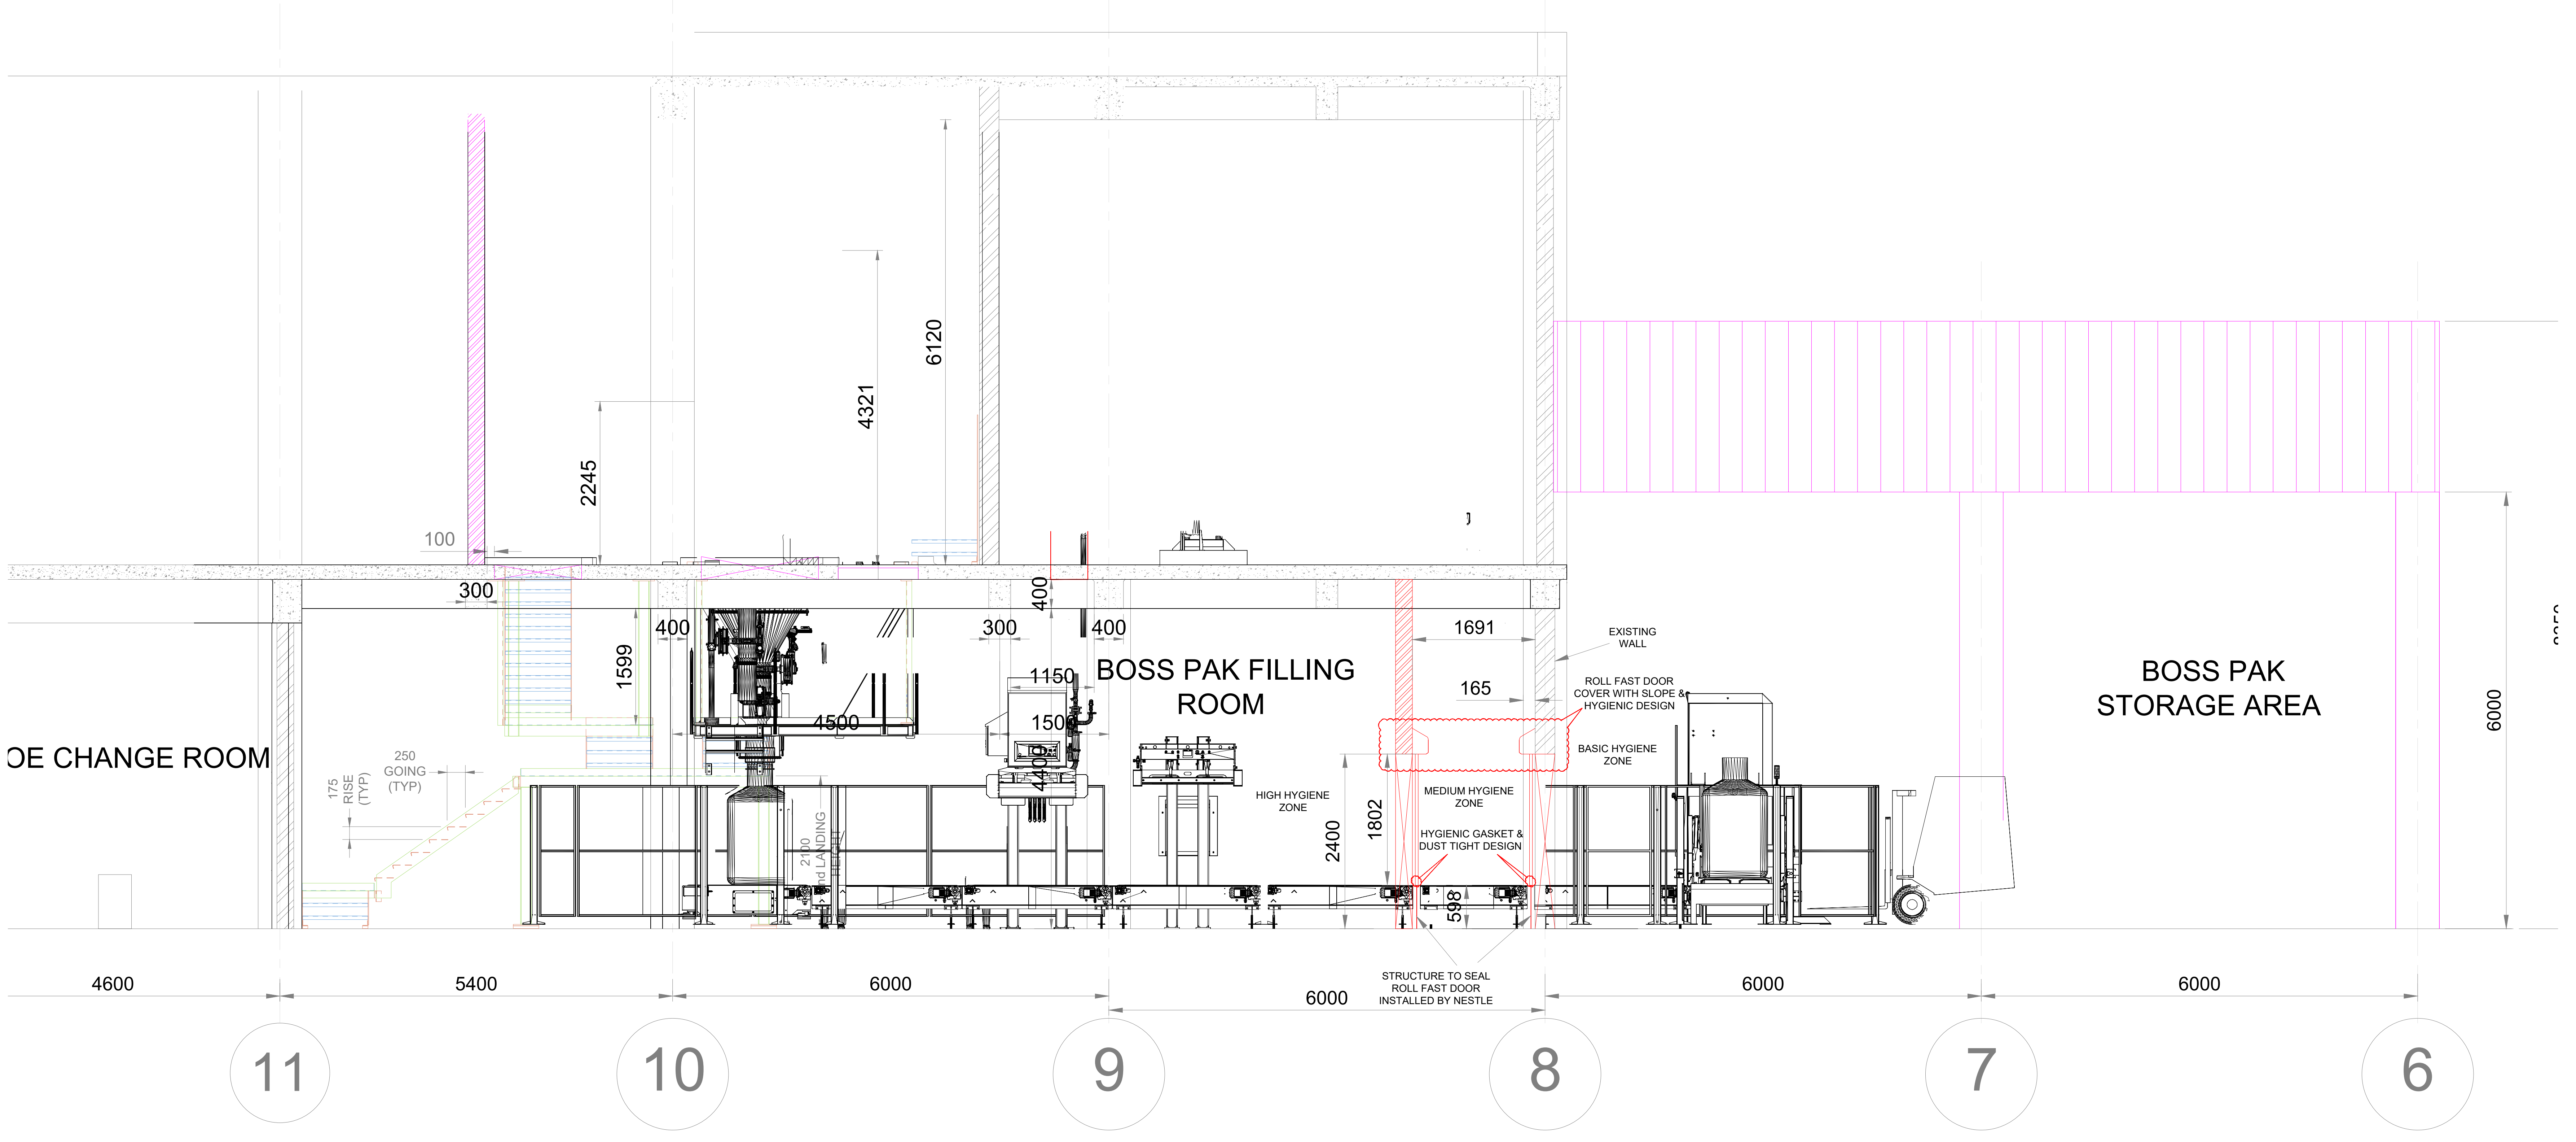

1599
1691
1500
BOSS PAK FILLING ROOM
EXISTING WALL
ROLL FAST DOOR COVER WITH SLOPE & HYGIENIC DESIGN
BASIC HYGIENE ZONE
HIGH HYGIENE ZONE
MEDIUM HYGIENE ZONE
HYGIENIC GASKET & DUST TIGHT DESIGN
1802
OE CHANGE ROOM
250 GOING (TYP)
175 RISE (TYP)
2nd LANDING
BOSS PAK STORAGE AREA
STRUCTURE TO SEAL ROLL FAST DOOR INSTALLED BY NESTLE

SECTION B-B

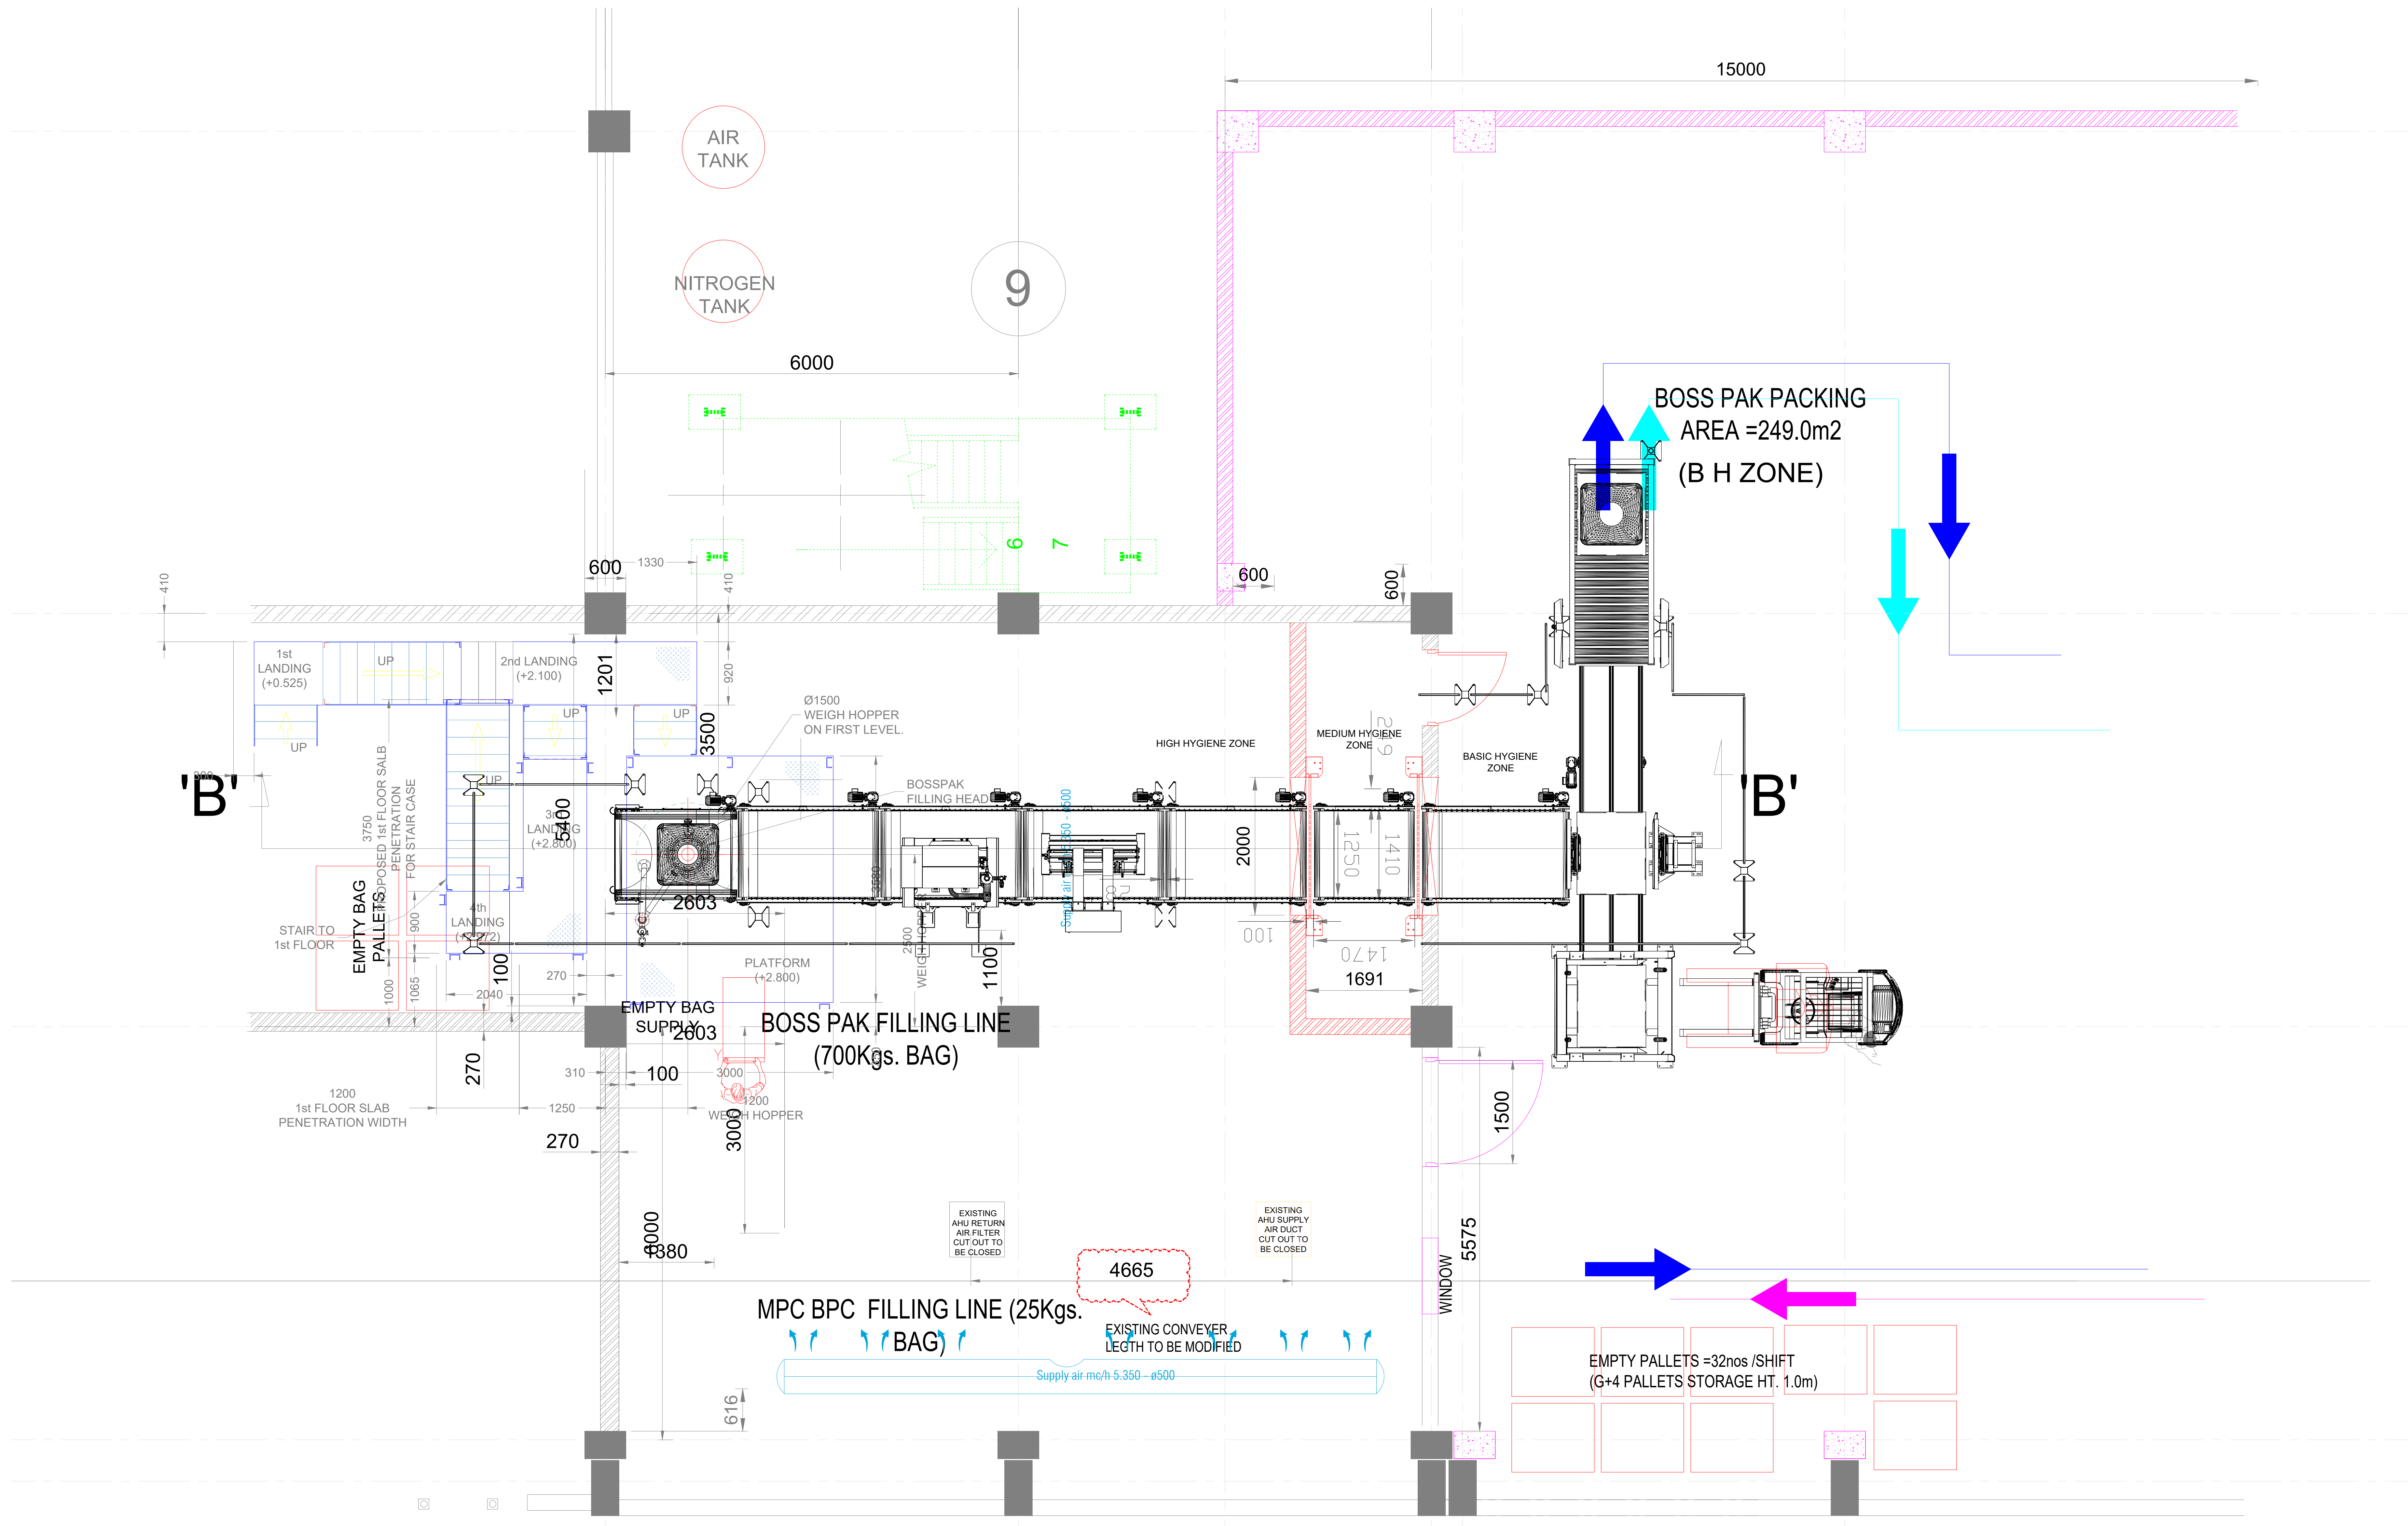

AIR TANK
NITROGEN TANK
9
15000
6000
BOSS PAK PACKING AREA =249.0m2
(B H ZONE)
410
600
1330
410
600
600
1st LANDING (+0.525)
UP
2nd LANDING (+2.100)
1201
920
UP
UP
UP
3500
Ø1500 WEIGH HOPPER ON FIRST LEVEL
HIGH HYGIENE ZONE
MEDIUM HYGIENE ZONE
BASIC HYGIENE ZONE
'B'
'B'
3750 PROPOSED 1st FLOOR SALB PENETRATION FOR STAIR CASE
5400
3rd LANDING (+2.800)
BOSSPAK FILLING HEAD
2000
1250
1410
2603
STAIR TO 1st FLOOR
EMPTY BAG PALLETS
900
4th LANDING (+3.372)
1000
1065
100
270
2040
PLATFORM (+2.800)
1100
100
1470
1691
EMPTY BAG SUPPLY
2603
BOSS PAK FILLING LINE (700Kgs. BAG)
270
310
100
3000
1200
WEIGH HOPPER
1250
1200 1st FLOOR SLAB PENETRATION WIDTH
270
3000
1500
4000
4880
EXISTING AHU RETURN AIR FILTER CUT OUT TO BE CLOSED
EXISTING AHU SUPPLY AIR DUCT CUT OUT TO BE CLOSED
4665
5575
WINDOW
MPC BPC FILLING LINE (25Kgs. BAG)
EXISTING CONVEYER LEGTH TO BE MODIFIED
Supply air mc/h 5.350 - ø500
616
EMPTY PALLETS =32nos /SHIFT
(G+4 PALLETS STORAGE HT. 1.0m)