


Elevation

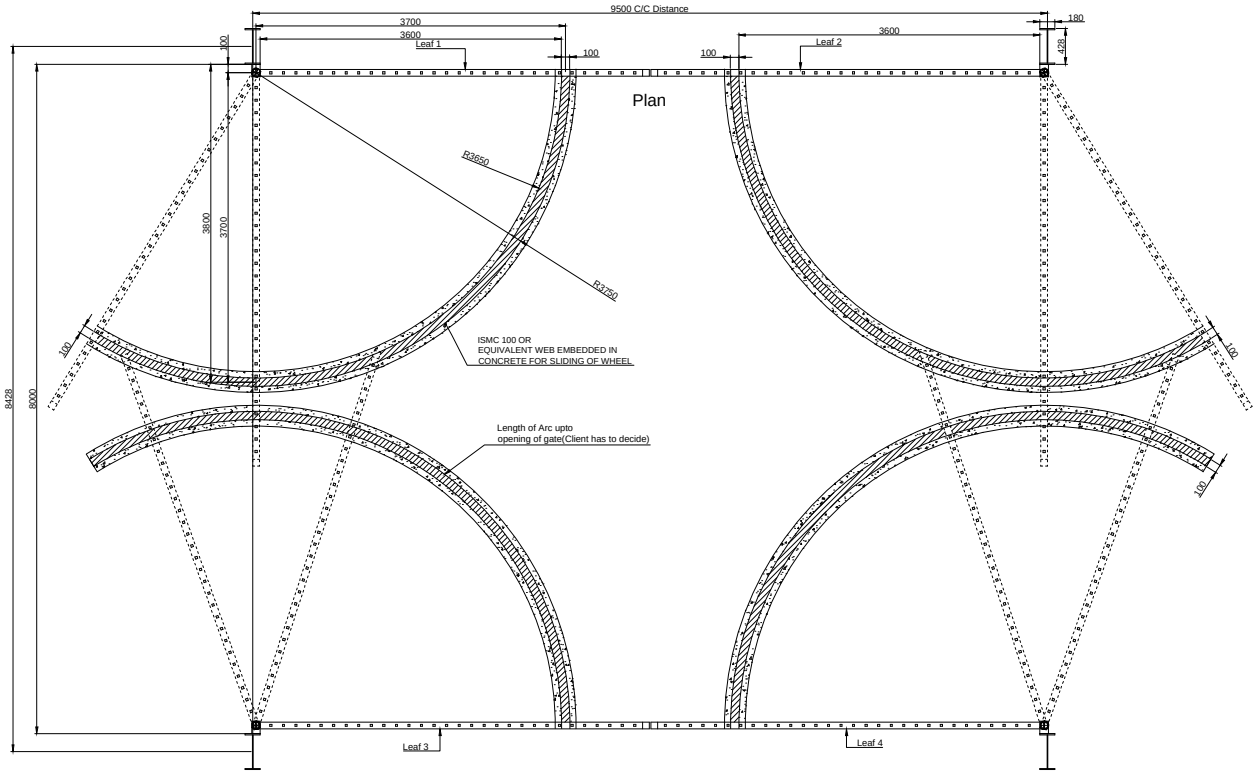

Color- 1. For Outer Boundry Golden Yellow RAL 1004
2. For Inner Tubes Marine blue RAL 5002

Color Shade are as per previously approved gates. Client has to confirm the same.

NOTE-
1. ALL REQUIRED CIVIL WORK WILL BE IN CLIENTS SCOPE.
2. ONE COAT OF RED OXIDE & TWO COAT OF APPROVED RAL SHADE WILL BE GIVEN TO THE GATE.

SR NO	TUBE SPECIFICATION	
01	MS 80X80X3.2mm	OUTER FRAME
02	MS 25X25X2mm	INNER PATTERN

This drawing & design is the property of NIHVA TECHNOLOGIES. Not to be sold or copied to any other concern.

TITLE

Gate 1(Boom gate)

ALL DIMENSION ARE IN mm

NIHVA TECHNOLOGIES PVT. LTD.
NIHVA TECHNOLOGIES PVT. LTD. PUNE
Tel : 020 66304033
Email:- info@nihva.com
Website:- www.nihva.com

	SIGN	DATE
DRAWN	OMKAR	12/01/18
CHECK	SHEKHAR	12/01/18
REV.		
APPRD.	SHEKHAR	12/01/18
MFG		
Ref. No.		

CLIENT APPROVAL

CLIENT - Tata Projects

PROJECT - Alstom

SITE - Madhepura, Bihar

DWG. NO. -NIHVA/17-18/0335 Rev- 0

SCALE: NTS WT: SHEET: 01 OF 01

If any queries contact : design@nihva.com