
Tolerance ±3 mm (for all dimensions)
Dimensions in [10] ==> clearance for installation

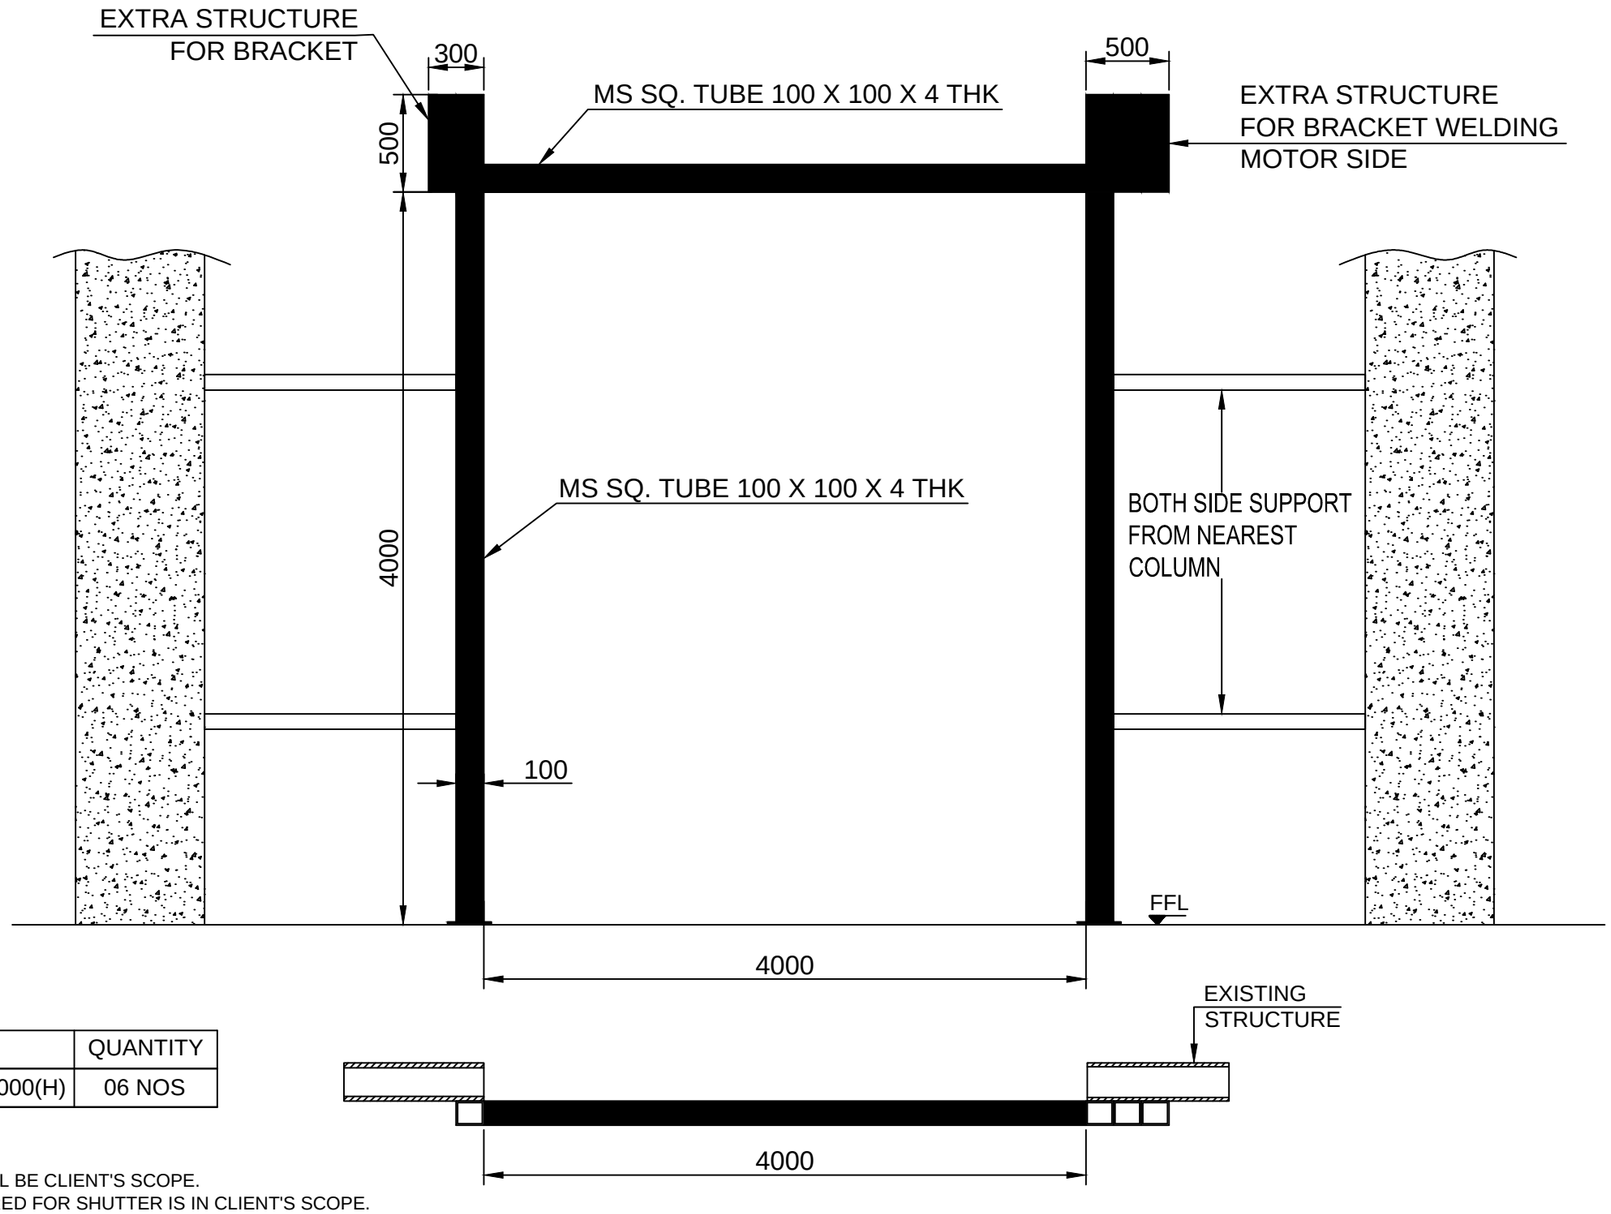

S.N.	SIZE	QUANTITY
1	4000(W) X 4000(H)	06 NOS

NOTE-
1. ALL CIVIL WORK WILL BE CLIENT'S SCOPE.
2.STRUCTURE REQUIRED FOR SHUTTER IS IN CLIENT'S SCOPE.

NOTES:

REVISIONS

REV	DESCRIPTION	DATE
R0	ISSUED FOR REVEW	23.01.19

KEY PLAN

SUBMITTED	REVIEWED	APPROVED

DESIGN BUILD

Shapoorji Pallonji ENGINEERING & CONSTRUCTION

SHAPOORJI PALLONJI & CO. PVT. LTD.
DESIGN & BUILD DIVISION
Contractor Building, 1st Floor,
Ramjibhai Kamani Marg, Ballard Estate
Mumbai - 400 038.
Tel/Fax: +91-22-66233500/533

THIS DRAWING IS THE PROPERTY OF SHAPOORJI PALLONJI & CO. PVT. LTD. (DESIGN & BUILD) IT SHALL NOT BE COPIED, REPRODUCED OR TRANSFERED IN ANY MANNER EITHER IN PART OR FULL WHAT SO EVER & SHALL BE USED ONLY FOR THE JOB ISSUED FOR.

DESIGN ASSOCIATE (ROLLING SHUTTER)

NIHVA TECHNOLOGIES PVT. LTD.
PUNE
Tel : 020 66304033
Email:- info@nihva.com
Website:- www.nihva.com

DESIGN ASSOCIATE (STRUCTURAL)

PRECISION PRECAST SOLUTION PVT.LTD.
FIRST FLOOR, SERVICE BUILDING, BAIF BHAVAN,
DR.MANIBHAI DESAI NAGAR WARJE,PUNE
PIN :411058

CLIENT

BRIDGESTONE INDIA PVT. LTD.
PLOT NO.A-43,CHAKAN INDUSTRIAL AREA,
PHASE 2,TEH:KHED,DIST:PUNE

DESIGN ASSOCIATE (ARCHITECTURE)

DESIGN CENTER
SHAPOORJI PALLONJI ENGINEERING
& CONSTRUCTION

PROJECT

BRIDGESTONE INDIA PVT. LTD.
11.5 K EXPANSION
THE EXPANSION OF THE EXISTING TYRE MANUFACTURING FACILITIES AT CHAKAN, PUNE, MAHARASHTRA.

BUILDING TYPE

DRAWING TITLE
RR300 PLUS ALU HSD

SIGNATURE	NORTH
	N

DWG. NO.	REV. NO.
NIHVA/18-19/0255	R0

SCALE	DATE	PROJECT NO.
NTS	23.01.2019	PUNE-1431
APPROVED	**CHECKED BY**	**DRAWN BY**
R.D.	P.A.	A.K.