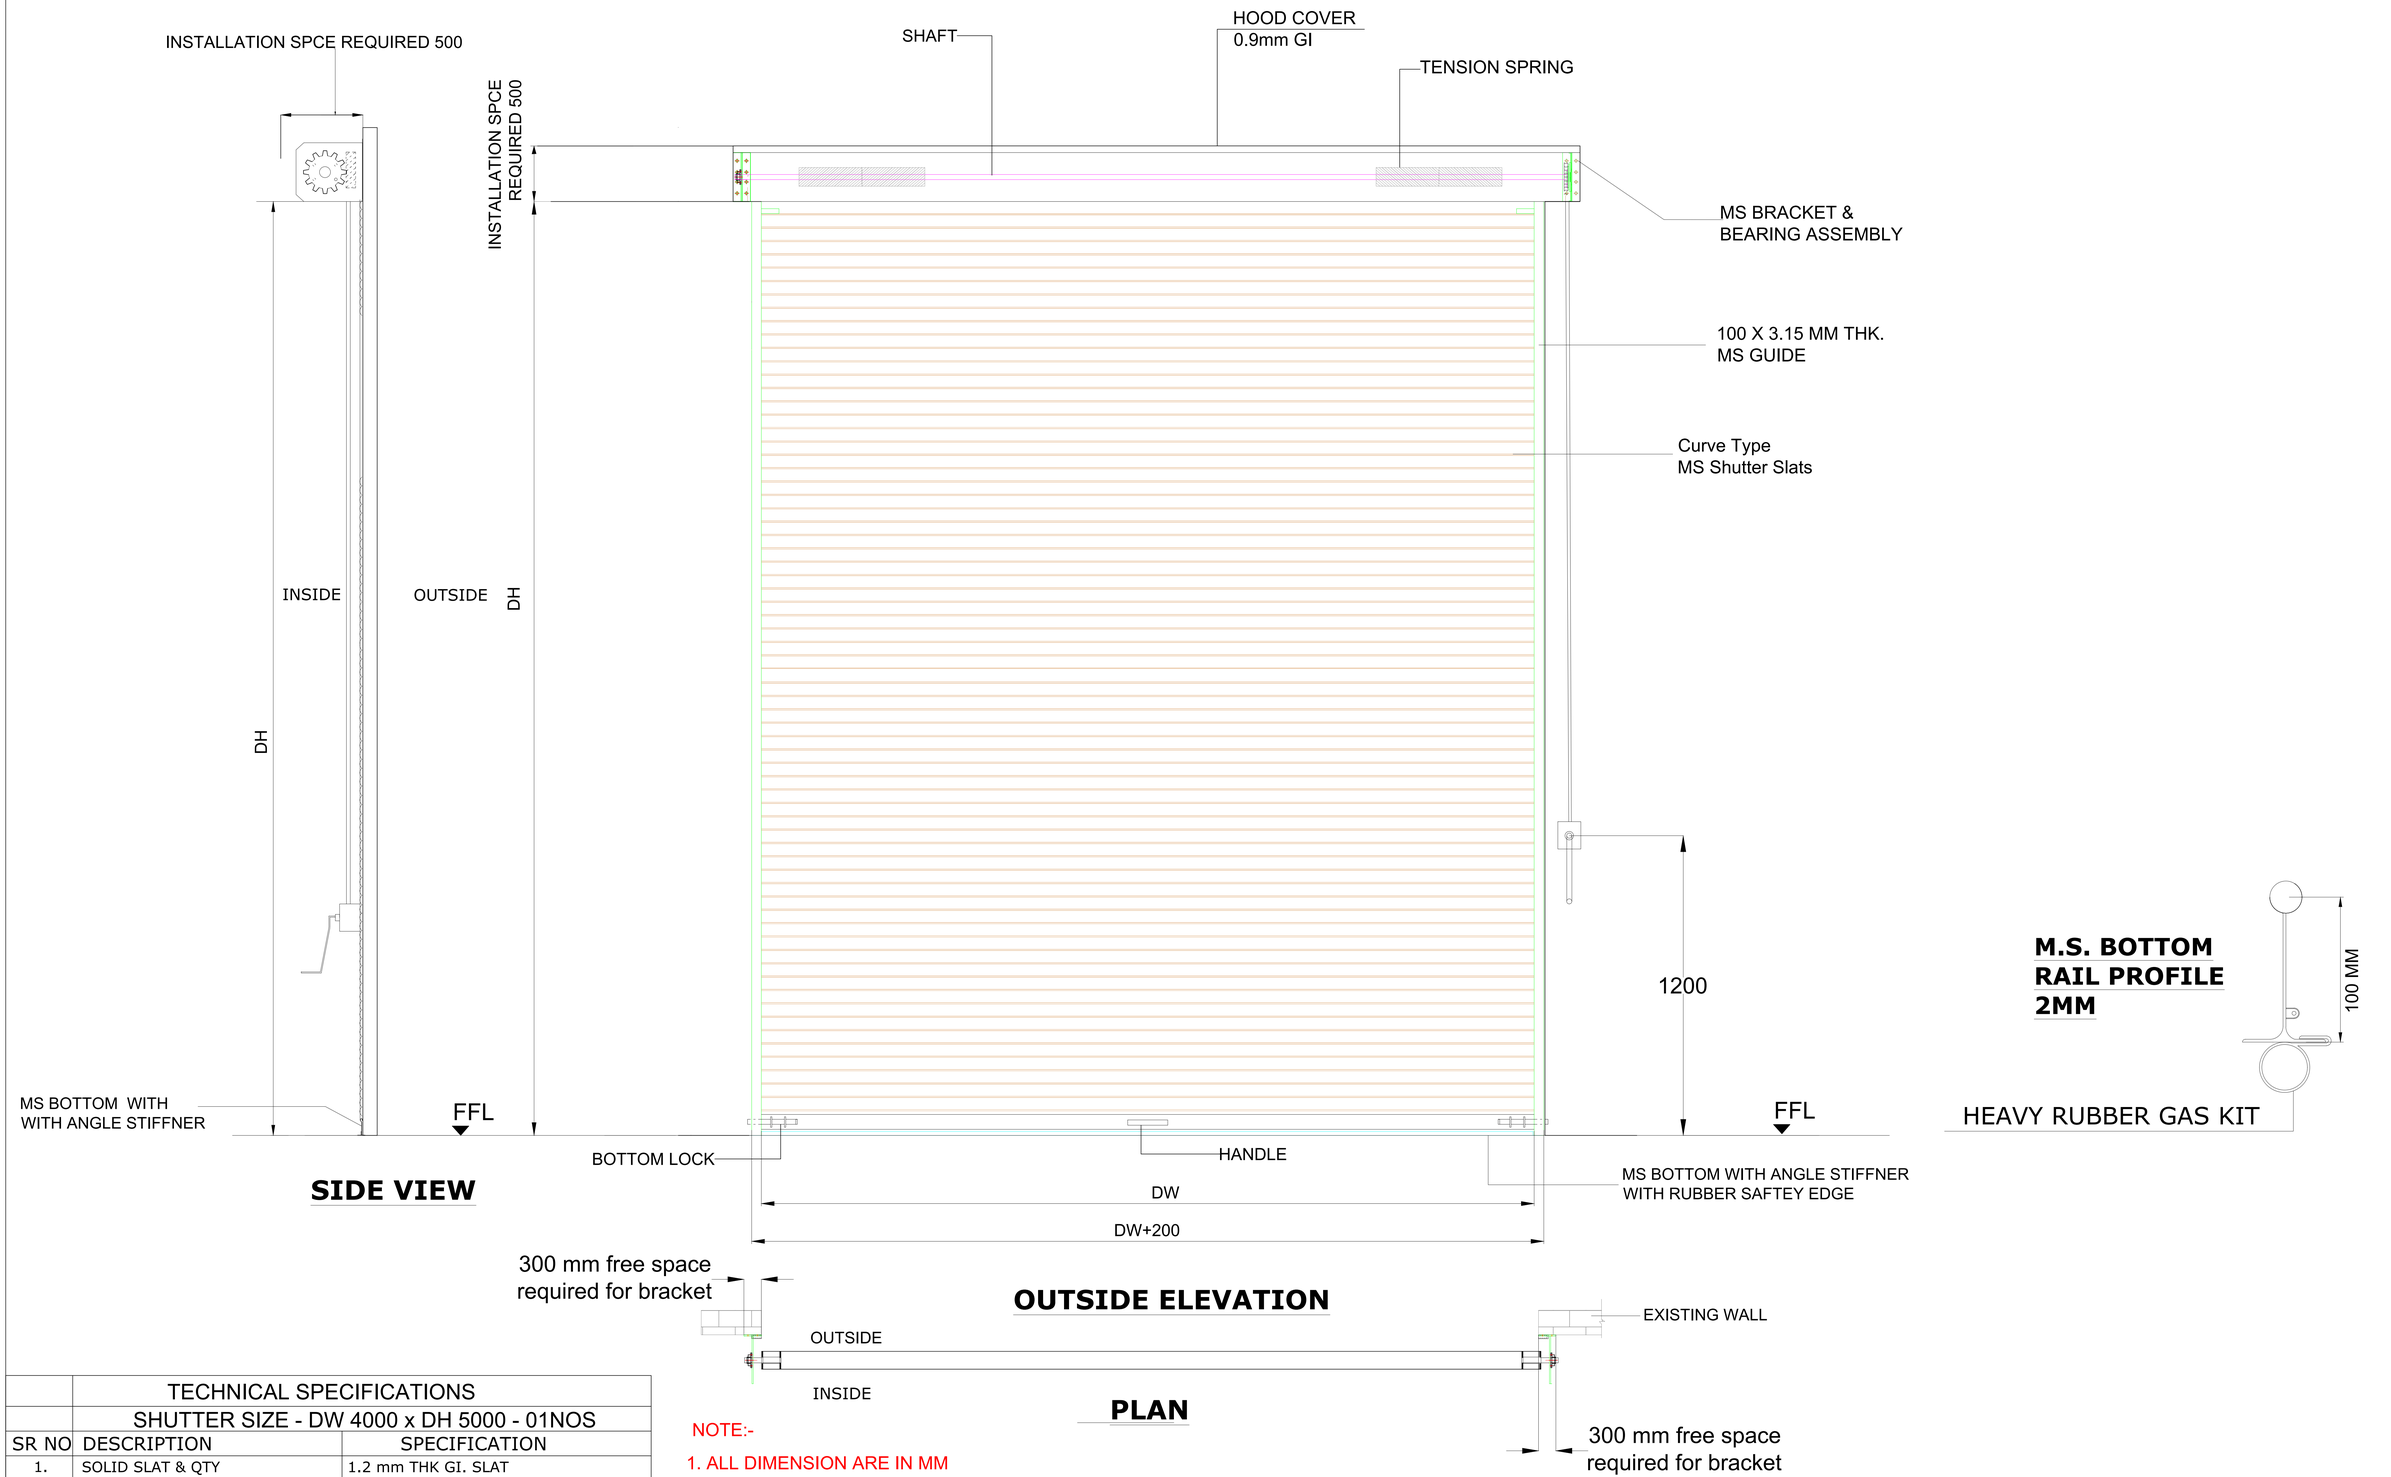


	TECHNICAL SPECIFICATIONS	
	SHUTTER SIZE - DW 4000 x DH 5000 - 01NOS	
SR NO	DESCRIPTION	SPECIFICATION
1.	SOLID SLAT & QTY	1.2 mm THK GI. SLAT
2.	M.S.GUIDE TYPE & SIZE	T GUIDE OF 100X2 THK
3.	HOOD COVER 0.9 mm GI	1/SHUTTER
4.	BOTTOM	MS BOTTOM 2 mm THK WITH ANGLE STIFFNER WITH RUBBER SAFTEY EDGE
5.	WIND LOCK	NOT CONSIDERED
6.	SAFETY BREAK	NOT APPLICABLE
7.	HAND CRANK	CONSIDERED
8.	CHAIN	NOT APPLICABLE
9.	HAND CRANK	RH SIDE
10.	SHUTTER MTG LOCATION	INSIDE
11.	SHUTTER MOUNTING BASE	MS STRUCTURE (IN CLIENT SCOPE)
12.	APPROVED RAL SHADE	AS CLIENT APPROVED RAL

NOTE:-

1. ALL DIMENSION ARE IN MM
2. ALL CIVIL WORK WILL BE IN S.P.F.S SCOPE.
3. MOUNTING: MS STRUCTURE MOUNTING WILL BE IN S.P.F.S SCOPE
4. SURFACE FINISH: POWDER COATING OF APPROVED RAL CODE -RAL 9001
5. SLATS QTY FOR SINGLE SHUTTER WILL BE 65NOS
6. SLAT GALVANIZATION SHALL BE MIN.230g/sqm
7. ROLLING SHUTTER SHALL BE WITHSTAND A BASIC WIND SPEED OF 50M/S

TOLERANCE - ±10mm

REV.NO	REVISION	DATE	REVISED BY

CLEAR WIDTH (DW)	CLEAR HEIGHT (DH)	QTY
4000	5000	1NOS

This drawing & designing is the property of NIHVA TECHNOLOGIES. Not to be sold or copied to any other concern.

TITLE :-
GEAR OPERATED ROLLING SHUTTER

NIHVA
NIHVA TECHNOLOGIES PVT. LTD.

	NAME	DATE
DRAWN	S.J	06/12/2023
CHECK		
APPROVAL		

CLIENT - SHREE PRE FAB STEEL PVT LTD
PROJECT -
SITE -HYDERABAD
DWG. NO. : NIHVA/NTPL/191 REV-01

If any queries contact : design1@nihva.com

SCALE: NTS WT: SHEET: 01 OF 01

ALL DIMENSION ARE IN mm