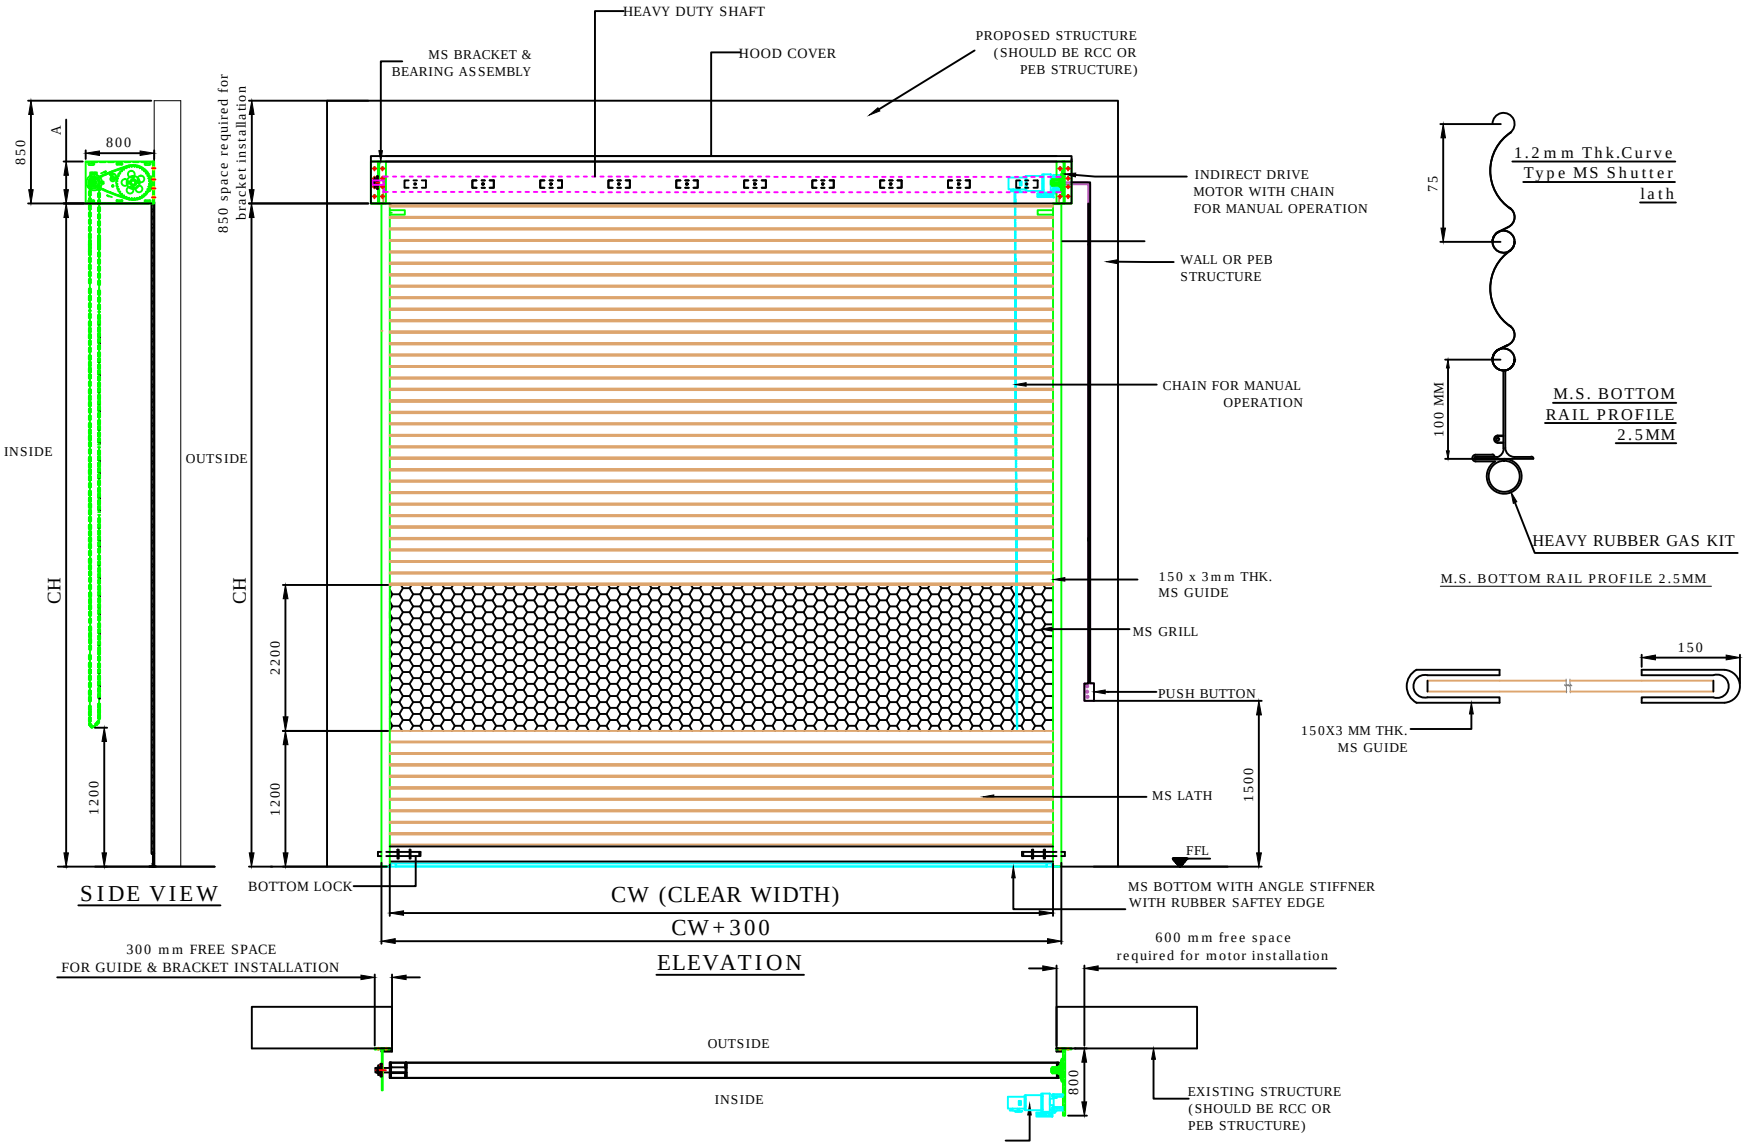


CLEAR WIDTH (CW)	CLEAR HEIGHT (CH)	GUIDE SIZE	BRACKET SIZE A	SHAFT SIZE (O.D)	SHUTTER QUANTITY
8000	6000	150X3mm	500X500	219mm	12
8000	8000	150X3mm	550X550	245mm	3

TECHNICAL DATA

COMPONENTS	MATERIAL	SPECIFICATION
SLATS	MS	1.2mm CURVED TYPE MS SLAT WITH PARTLY GRILLED.
SIDE GUIDE	MS	150X3 mm
BOTTOM PROFILE WITH ANGLE STIFFNER	MS	125X2.5mm BOTTOM PROFILE with 50mm MS ANGLE.
BRACKET PLATES	MS	—
ROLLER SHAFT	MS	—
HOOD COVER	GI	0.9mm THK.
AUTOMATION SYSTEM	—	JIELONG MAKE INDIRECT DRIVE MOTOR (MADE IN CHINA)
PRIMER	—	A COAT OF RED OXIDE ZINC CHROMATE WILL BE GIVEN.
STANDARD FINISH	—	FINAL COLOR SHADE WILL BE IN CLIENT'S SCOPE.

NOTE:
1.REQUIRED STRUCTURE FOR SHUTTER SHALL BE IN CLIENT SCOPE.
2.THREE PHASE POWER SUPPLY REQUIRE.
3.FOR POWER SUPPLY 4 CORE 2.5 SQ.mm CABLE REQUIRE

LOCATION OF SHUTTER

CLEAR WIDTH	CLEAR WIDTH	QUANTITY	LOCATION
8000mm	6000mm	12	PLANT 02
8000mm	8000mm	3	PLANT 02

CLIENT:
& BOYCE MFG. CO. LTD.
CONSULTANCY SERVICES FOR DETAILED ENGINEERING OF INDUSTRIAL EXPANSION PROJECT

PROJECT:
GODREJ & BOYCE MFG. CO. LTD.
PROPOSED INDUSTRIAL EXPANSION AT VILLAGE VADVAL AND TAMBATI. TAL. KHALAPUR, DIST. RAIGAD.

ARCHITECT/CONSULTANT:
TATA CONSULTING ENGINEERS LIMITED
MUMBAI

PMC:
CUSHMAN & WAKEFIELD
Cushman wakefield India Pvt. Ltd.
Onyx 11th Floor, North Main Road, Next to Westin Hotel, Koregaon Park, Pune 411001, India.

CONTRACTOR:
RATILAL BHAGWANDAS CONSTRUCTION COMPANY PVT. LTD. PUNE.

NIHVA TECHNOLOGIES PVT. LTD.
NIHVA TECHNOLOGY PVT. LTD. PUNE
Email:- info@nihva.com
Website:- www.nihva.com

DWG TITLE:
MOTORIZED ROLLING SHUTTER

SO Ref. No- SO/16-17/0073

DRN BY:	SCALE:	DWG NO:	REV NO:
OMKAR	NTS	NIHVA/16-17/0085/R01	1
CHKD BY: SAGAR P	DATE: 15-11-2016		

If any queries contact : projects@nihva.com

NOTE: ALL DIMENSION ARE IN mm

THIS DRAWING & DESIGNING IS THE PROPERTY OF NIHVA TECHNOLOGIES. NOT BE SOLD OR COPY TO ANY OTHER CONCERN.