


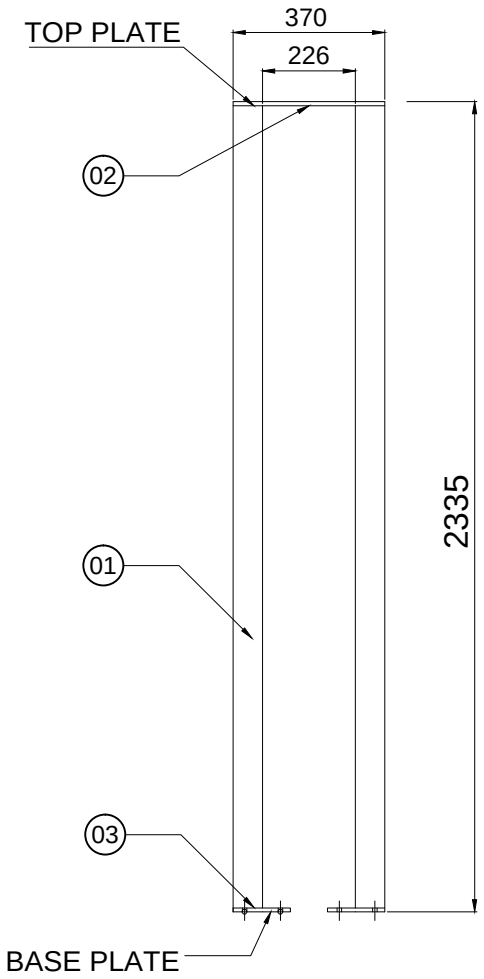


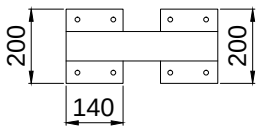

POST

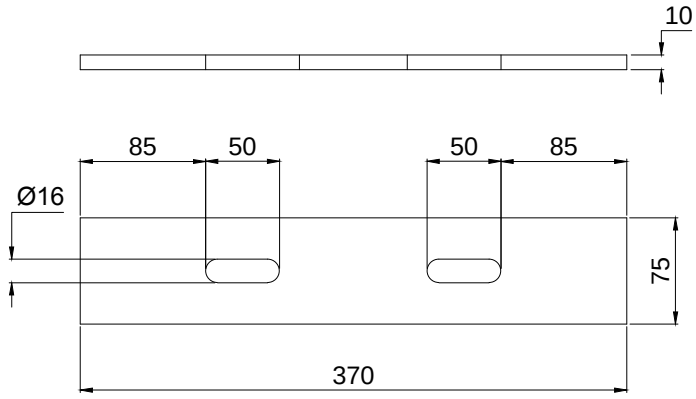

02 TOP PLATE

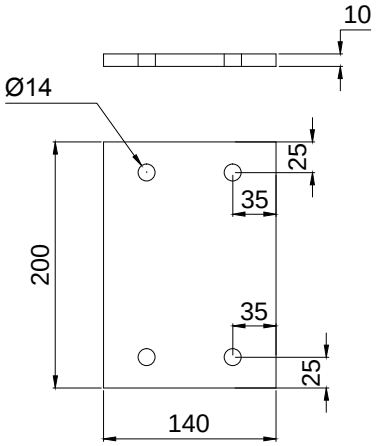

BASE PLATE

SR NO	DESCRIPTION	SPECIFICATION	QTY
05	GUIDE WHEEL	Ø50 X 75L	10 NOS
04	ANCHOR BOLT	M12 X 150L	40 NOS
03	FLAT	140 X 10 THK X 200L	10 NOS
02	FLAT	75 X 10 THK X 370L	5 NOS
01	SQ. TUBE	72 x 72 x 2.5 THK X 2325L	10 NOS

This drawing & designing is the property of NIHVA TECHNOLOGIES. Not to be sold or copied to any other concern.

TITLE: SLIDING GATE POST DRAWING

NIHVA TECHNOLOGIES PVT. LTD.
NIHVA TECHNOLOGIES PVT. LTD. PUNE
Tel : 020 66304033
Website:- www.nihva.com
Email:- info@nihva.com

	Name	SIGN	DATE
DRAWN	P.V.A		27.02.19
CHECK	V.M.T		27.02.19
APPROVAL			

CLIENT -
PROJECT -
SITE LOCATION -
If any queries contact : design@nihva.com
DWG. NO. : NIHVA/18-19/VDR/387 REV.:- 0
ALL DIMENSION ARE IN mm
SCALE: NTS WT: SHEET: 01 OF 01