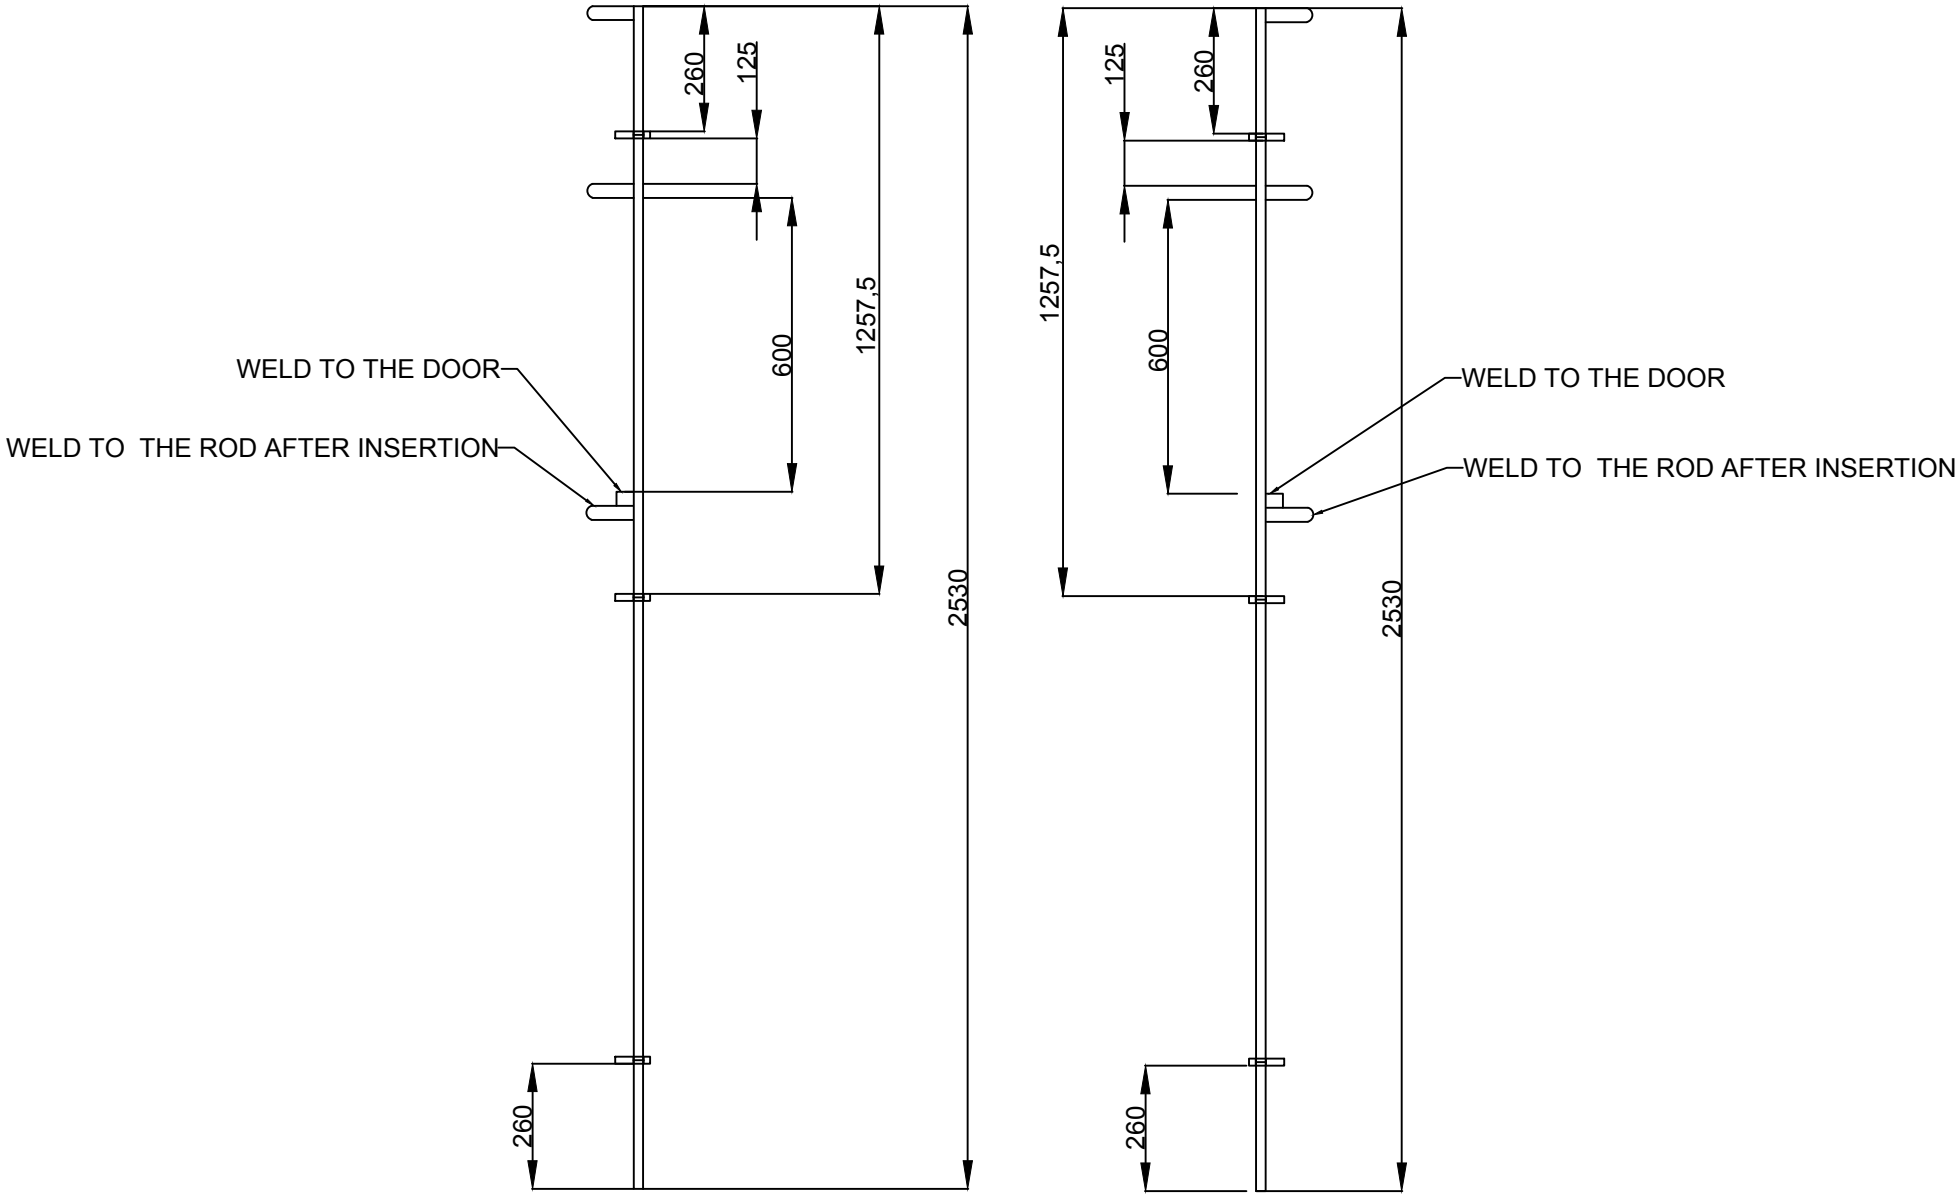


Date	Revised By

TITLE:- TOWER BOLT				NIHVA TECHNOLOGIES PVT. LTD. PUNE Tel : 020 66304033 Email:- info@nihva.com Website:- www.nihva.com	
	NAME	DATE	SIGN		
DRAWN	KISHAN	16/06/2022		CLIENT - NIHVA TECHNOLOGIES PVT.LTD	
CHECK	M. SUTAR	16/06/2022		LOCATION -	
APPRD.	V. TARAK			PRODUCT - SWING DOOR	
If any queries contact : design@nihva.com				DWG NO:-NIHVA/22-23/MFG/0024	REV- 0
ALL DIMENSION ARE IN mm				SCALE: NTS	SCALE:-- 1:1 | SHEET: 01 OF 01