

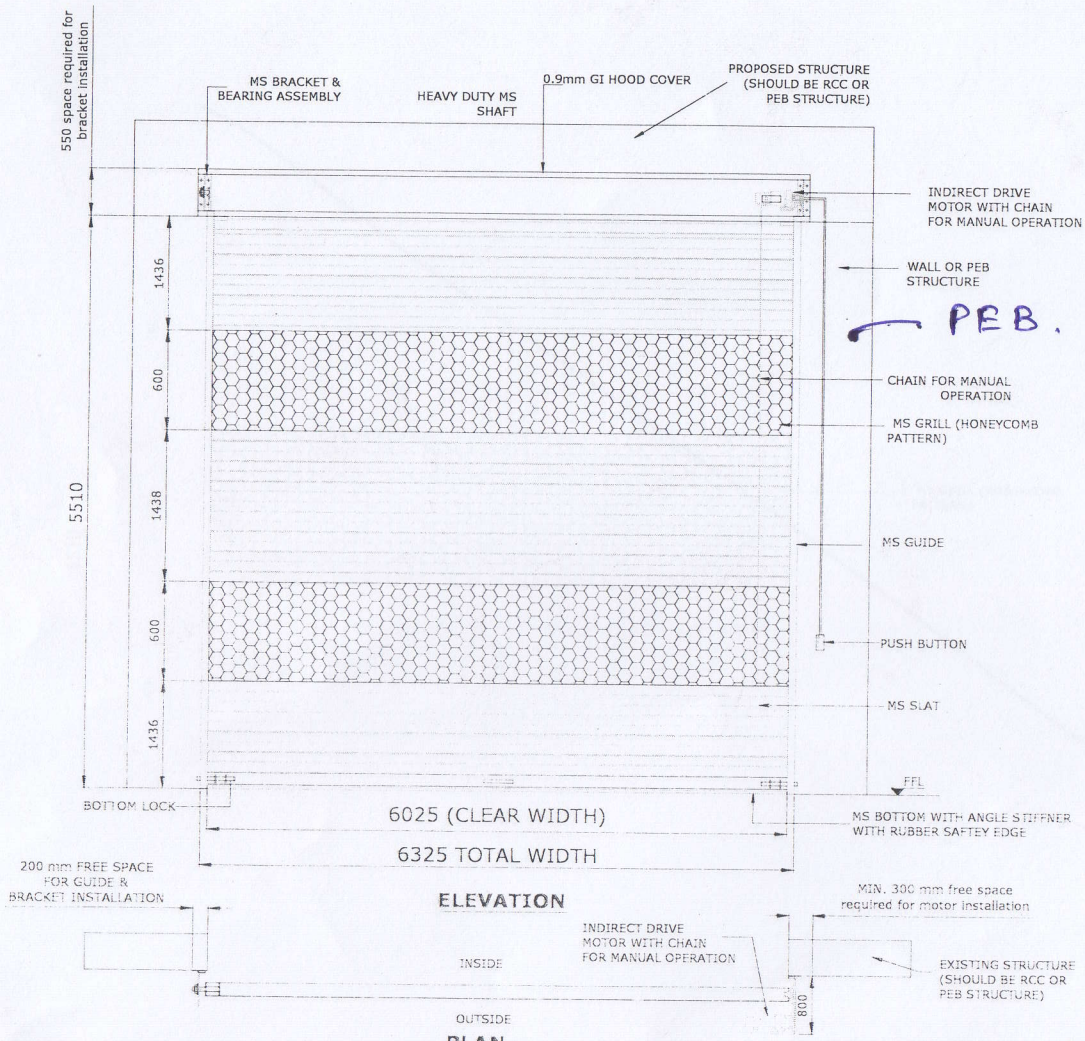


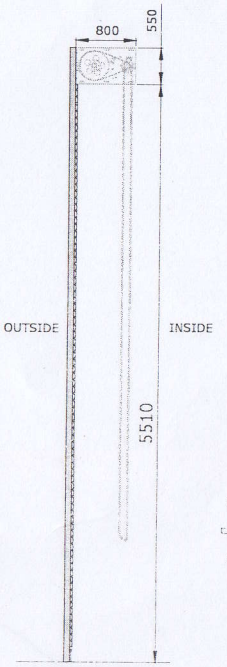



SIDE VIEW

1mm Thk.Curve Type MS Shutter lath AT TOP & BOTTOM

M.S. BOTTOM RAIL PROFILE 2.5MM THK WITH ANGLE STIFFNER & EPDM RUBBER

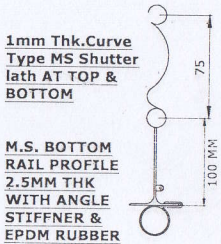

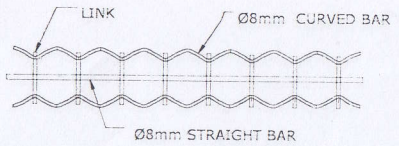

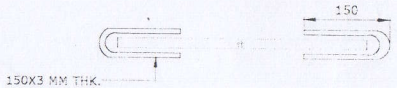

DIMENSION :		
CLEAR WIDTH	CLEAR HEIGHT	QUANTITY
6025	5510	1

MATERIAL :

THICKNESS :

NOTE-
1.ONE COAT OF RED OXIDE WILL BE GIVEN SHUTTER (ONLY MS PART).
2. HOOD COVER WILL BE IN GI.
3.SINGLE PHASE SUPPLY SHOULD BE GIVEN TO THE SHUTTER.
4. REQUIRED STRUCTURE FOR SHUTTER SHALL BE IN CLIENT'S SCOPE.
5. ALL CIVIL WORK WILL BE IN CLIENT'S SCOPE.
6. TOLERANCE FOR GRILL SIZE SHALL BE PLUS/MINUS 15mm

NIHVA TECHNOLOGIES PVT. LTD. PUNE
NIHVA TECHNOLOGIES PVT. LTD.
Email:- info@nihva.com
Website:- www.nihva.com

TITLE:

MOTORIZED GRILLED ROLLING SHUTTER

CLIENT'S APPROVAL :

CLIENT - VAICHAL CONSTRUCTION
PROJECT - TAGMA CENTRE
SITE LOCATION - CHAKAN
DWG. NO. :NIHVA/17-18/0124

SCALE: NTS	WT:	SHEET:1 OF 1
DRAWN BY: OMKAR		DATE: 11-07-2017
CHECK : SHEKHAR		DATE: 11-07-2017
APPROVED :SHEKHAR		DATE: 11-07-2017

If any queries contact : projects@nihva.com
NOTE: ALL DIMENSIONS ARE IN mm


THIS DRAWING & DESIGN IS THE PROPERTY OF NIHVA TECHNOLOGIES. NOT TO BE SOLD OR COPY TO ANY OTHER CONCERN.

Color - one coat of zinc chromate red oxide primer.


checked & Verified
02/08/2017

CLEAR WIDTH	CLEAR HEIGHT	QUANTITY
6025	5510	1
5975	5510	1


Abbrevation's:
WOW-Wall Opening Width
WOH-Wall Opening Height
DH- Door Height
UC-Under Cut
FFL-Finished Floor Level

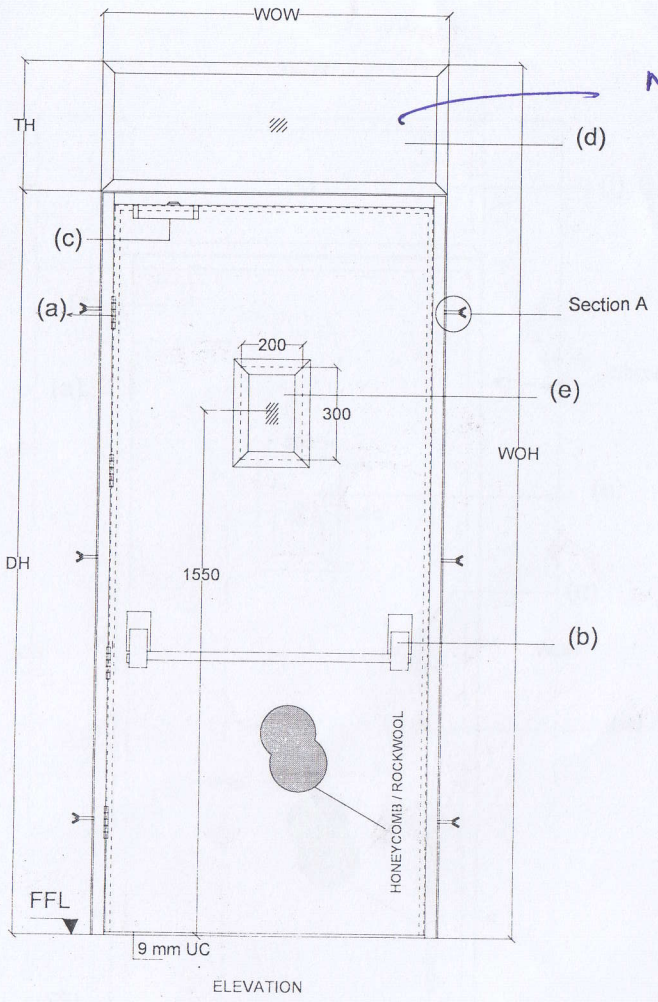

ELEVATION

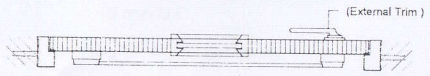

Top View

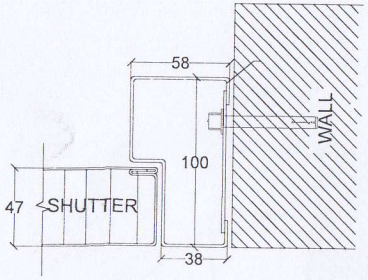

ASSESORIES DETALES

(a) HINGES: SS hinges 100x75x3mm

(b) LOCK : Mortise Lock with half cylinder.
Panic Bar
Outer trim

(c) DOOR CLOSER : F 8500

(d) FIXED GLASS(5mm THK.) WITH FRAME.

(e) VISION PANEL- 5mm THK. FIRE GLASS SIZE- 200X300mm.

Shutter thickness : 47 mm
Frame Sheet thick : 1.20mm
Shutter sheet thick : 0.80mm
Fixing : On Soliid Brick plasterd wall with Anchors

NOTE:- *All Dimensions are in mm.
*Tolerance:-All Linear Dimensions ±3mm,Others ±0.5mm.
*The Drawing Is For Location of Hardware only. Drawing Does Not Represent The Hardware For More Clarity, Please Go Through Hardware Broucher.

Fire door size

WOW	WOH	DH	TH	TYPE 1	TYPE 2	TYPE 3	TYPE 4	QUANTITY
1191	3000	2400	600				✓	1
1180	3121	2400	721				✓	1
1180	3029	2400	629			✓		1
1195	3033	2400	633			✓		1
1205	3017	2400	617			✓		1
1194	2958	2400	558				✓	1
1192	3000	2400	600			✓		1

NOTE- CLIENT SHOULD SELECT DOOR TYPE FROM DOOR HANDLING SHEET & COLOR OF DOOR.

checked & verified.
02/08/2017

Color - RAL 3001 (Signal Red).

REVISION 1- UPPER VISION PANEL IS IN SINGLE PARTITION AS PER CLIENT'S REQUIREMENT.


This drawing & designing is the property of NIHVA TECHNOLOGIES. Not to be sold or copied to any other concern.

TITLE	FIRE RATED DOORS WITH FIXED GLASS		
	SIGN	DATE	
DRAWN	OMKAR	19/07/17	
CHECK	SHEKHAR	19/07/17	
REV.	00		
APPROVAL			
if any queries contact projects@nihva.com			
ALL DIMENSION ARE IN mm			


NIHVA TECHNOLOGIES PVT. LTD.
NIHVA TECHNOLOGIES PVT. LTD. PUNE
Tel : 020 66304033
Email:- info@nihva.com
Website:- www.nihva.com

CLIENT - VAICHAL CONSTRUCTION
PROJECT - TAGMA CENTRE
SITE - CHAKAN
DWG. NO. : NIHVA/17-18/0128/R01
SCALE: NTS | WT: | SHEET: 01 OF 01


Abbrevation's:
WOW-Wall Opening Width
WOH-Wall Opening Height
CH- Clear Height
UC-Under Cut
FFL-Finished Floor Level

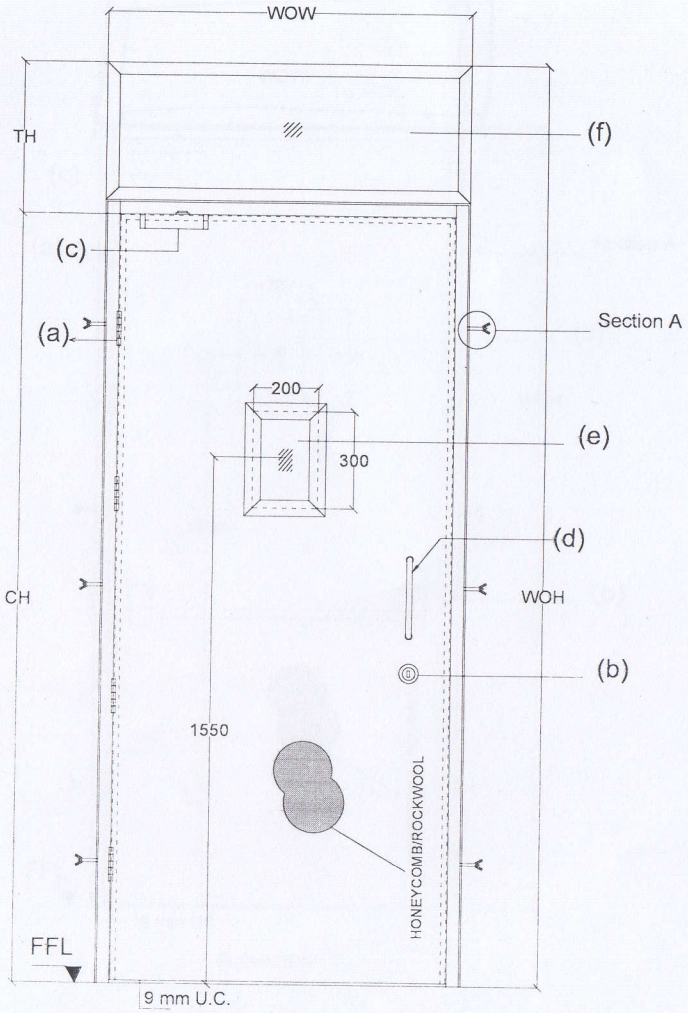

ELEVATION

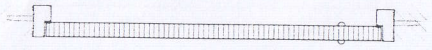

TOP VIEW

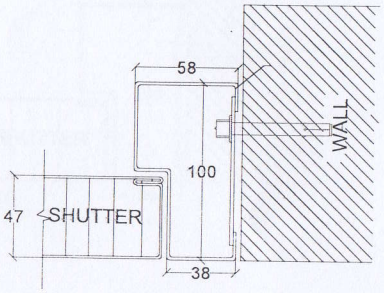

ASSESORIES DETALES

(a) HINGES: SS hinges 100x75x3mm

(b) LOCK : Mortise dead Lock with cylinder(One side key & thumb turn on other side)with escutcheon.

(c) DOOR CLOSER : B4W

(d) HANDLE : D Handle (300x22) pair.

(e) VISION PANEL - 5mm THK. GLASS OF SIZE-200X300mm

(f) FIXED GLASS- 5mm THK. FIXED GLASS WITH FRAME.

Shutter thickness : 47 mm
Frame Sheet thick : 1.20mm
Shutter sheet thick : 0.80mm
Fixing : On Soliid Brick plasterd wall with Anchors

NOTE:- *All Dimensions are in mm.
*Tolerance:-All Linear Dimensions ±3mm,Others ±0.5mm.
*The Drawing Is For Location of Hardware only. Drawing Does Not Represent The Hardware For More Clarity, Please Go Through Hardware Broucher.

Fire door size

WOW	WOH	CH	TH	TYPE 1	TYPE 2	TYPE 3	TYPE 4	QUANTITY
1192	2985	2400	585			✓		1

NOTE- CLIENT SHOULD SELECT DOOR TYPE FROM DOOR HANDLING SHEET & COLOR OF DOOR.

checked & verified
02/08/2017


RAL 3001 (Signal red)

REVISION 1- UPPER VISION PANEL IS IN SINGLE PARTITION AS PER CLIENT'S REQUIREMENT.


This drawing & designing is the property of NIHVA TECHNOLOGIES. Not to be sold or copied to any other concern.

TITLE	STEEL DOOR WITH FIXED GLASS		NIHVA TECHNOLOGIES PVT. LTD. PUNE
	SIGN	DATE	Tel : 020 66304033
DRAWN	OMKAR	19/07/17	Email:- info@nihva.com
CHECK	SHEKHAR	19/07/17	Website:- www.nihva.com
REV.	00		CLIENT - VAICHAL CONSTRUCTION
APPROVAL			PROJECT - TAGMA CENTRE
If any queries contact projects@nihva.com			SITE - CHAKAN
ALL DIMENSION ARE IN mm			DWG. NO. : NIHVA/17-18/0130/R01
			SCALE: NTS WT: SHEET: 01 OF 01


Abbrevation's:
WOW-Wall Opening Width
WOH-Wall Opening Height
CH- Clear Height
UC-Under Cut
FFL-Finished Floor Level

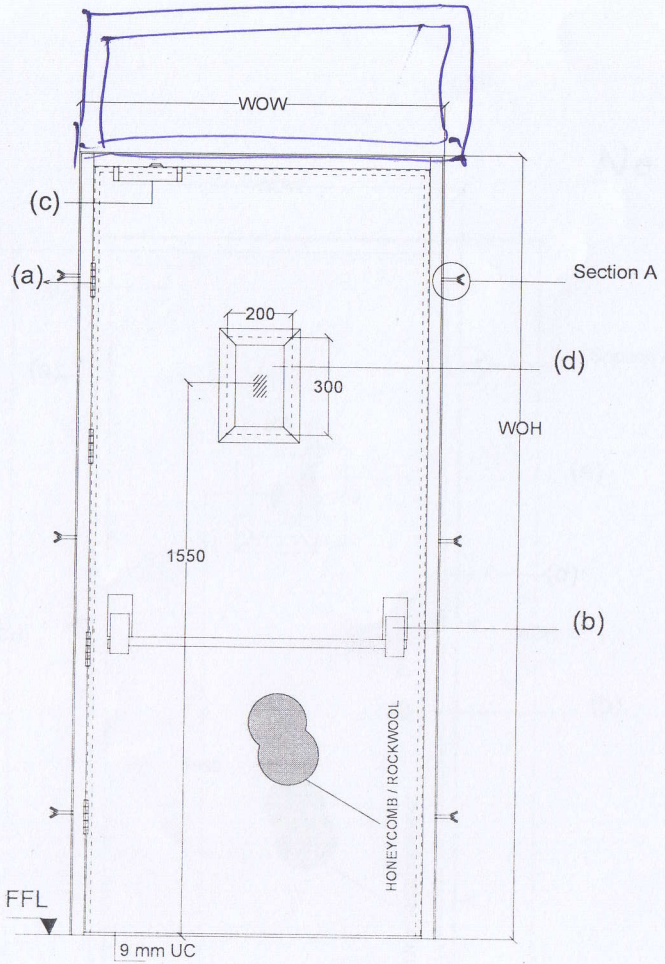

ELEVATION

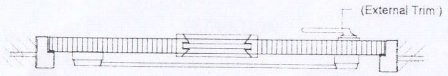

Top View

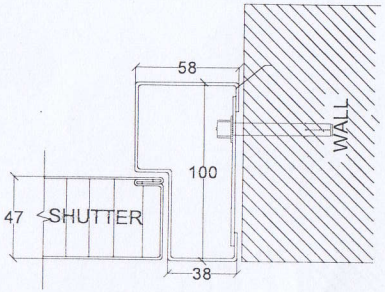

ASSESORIES DETALES

(a) HINGES: SS hinges 100x75x3mm

(b) LOCK : Mortise Lock with half cylinder.
Panic Bar
Outer trim

(c) DOOR CLOSER : F 8500

(d) VISION PANEL- 5mm THK. FIRE GLASS SIZE- 200X300mm.

Shutter thickness : 47 mm
Frame Sheet thick : 1.20mm
Shutter sheet thick : 0.80mm
Fixing : On Soliid Brick plasterd wall with Anchors

NOTE:- *All Dimensions are in mm.
*Tolerance:-All Linear Dimensions ±3mm,Others ±0.5mm.
*The Drawing Is For Location of Hardware only. Drawing Does Not Represent The Hardware For More Clarity, Please Go Through Hardware Broucher.

Top panel should be placed.

Fire door size						
WOW	WOH	TYPE 1	TYPE 2	TYPE 3	TYPE 4	QUANTITY
1198	2977				✓	1

NOTE- CLIENT SHOULD SELECT DOOR TYPE FROM DOOR HANDLING SHEET & COLOR OF DOOR.

checked & verified
02/08/2017

Color -


This drawing & designing is the property of NIHVA TECHNOLOGIES. Not to be sold or copied to any other concern.

TITLE	FIRE RATED DOORS		
	SIGN	DATE	
DRAWN	OMKAR	11/07/17	CLIENT - VAICHAL CONSTRUCTION
CHECK	SHEKHAR	11/07/17	PROJECT - TAGMA CENTRE
REV.	00		SITE - CHAKAN
APPROVAL			DWG. NO. : NIHVA/17-18/0129
If any queries contact : projects@nihva.com			SCALE: NTS WT: SHEET: 01 OF 01
ALL DIMENSION ARE IN mm			


NIHVA TECHNOLOGIES PVT. LTD.
NIHVA TECHNOLOGIES PVT. LTD. PUNE
Tel : 020 66304033
Email:- info@nihva.com
Website:- www.nihva.com

Abbrevation's:
WOW-Wall Opening Width
WOH-Wall Opening Height
CH- Clear Height
UC-Under Cut
FFL-Finished Floor Level


No panel at Top.

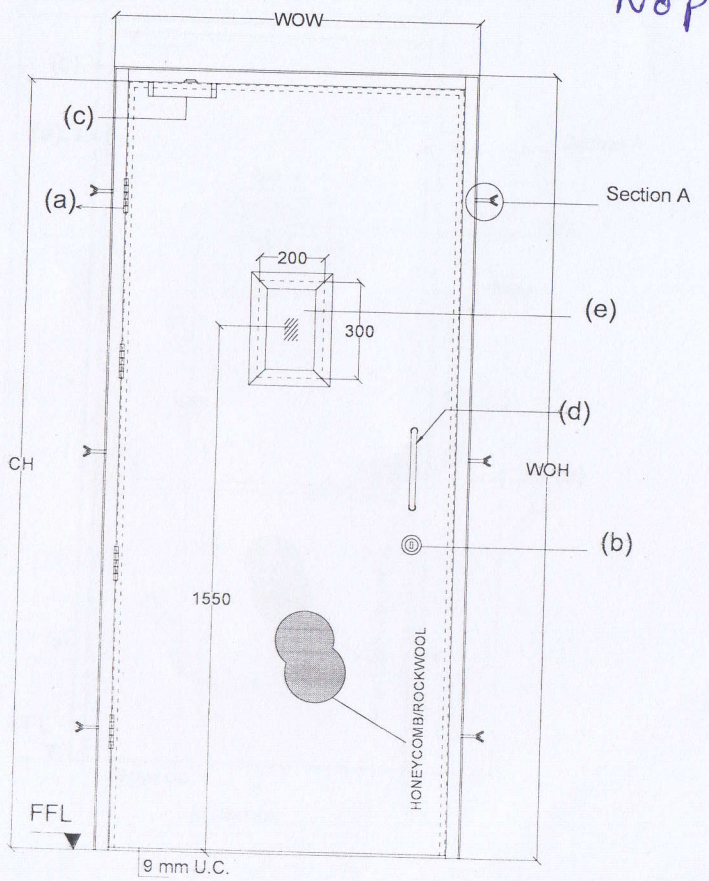

ELEVATION

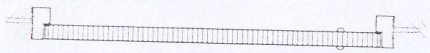

TOP VIEW

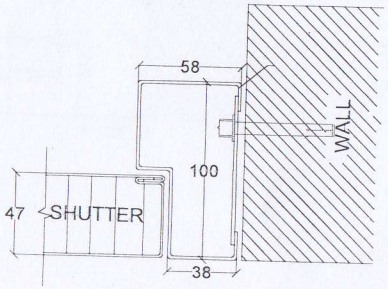

ASSESORIES DETALES

(a) HINGES: SS hinges 100x75x3mm

(b) LOCK : Mortise dead Lock with cylinder(One side key & thumb turn on other side)with escutcheon.

(c) DOOR CLOSER : B4W

(d) HANDLE : D Handle (300x22) pair.

(e) VISION PANEL - 5mm THK. GLASS OF SIZE-200X300mm

Shutter thickness : 47 mm
Frame Sheet thick : 1.20mm
Shutter sheet thick : 0.80mm
Fixing : On Soliid Brick plasterd wall with Anchors

NOTE:- *All Dimensions are in mm.
*Tolerance:-All Linear Dimensions ±3mm,Others ±0.5mm.
*The Drawing Is For Location of Hardware only. Drawing Does Not Represent The Hardware For More Clarity, Please Go Through Hardware Broucher.

Fire door size						
WOW	WOH	TYPE 1	TYPE 2	TYPE 3	TYPE 4	QUANTITY
1200	2125			✓		1

NOTE- CLIENT SHOULD SELECT DOOR TYPE FROM DOOR HANDLING SHEET & COLOR OF DOOR.

RAL 3001 signal red.

checked & verified
02/08/2017.

This drawing & designing is the property of NIHVA TECHNOLOGIES. Not to be sold or copied to any other concern.

TITLE	STEEL DOOR		NIHVA TECHNOLOGIES PVT. LTD. PUNE
	SIGN	DATE	NIHVA TECHNOLOGIES PVT. LTD. Tel : 020 66304033 Email:- info@nihva.com Website:- www.nihva.com
DRAWN	OMKAR	11/07/17	CLIENT - VAICHAL CONSTRUCTION
CHECK	SHEKHAR	11/07/17	PROJECT - TAGMA CENTRE
REV.	00		SITE - CHAKAN
APPROVAL			DWG. NO. : NIHVA/17-18/0131
If any queries contact : projects@nihva.com			SCALE: NTS WT: SHEET: 01 OF 01
ALL DIMENSION ARE IN mm			