
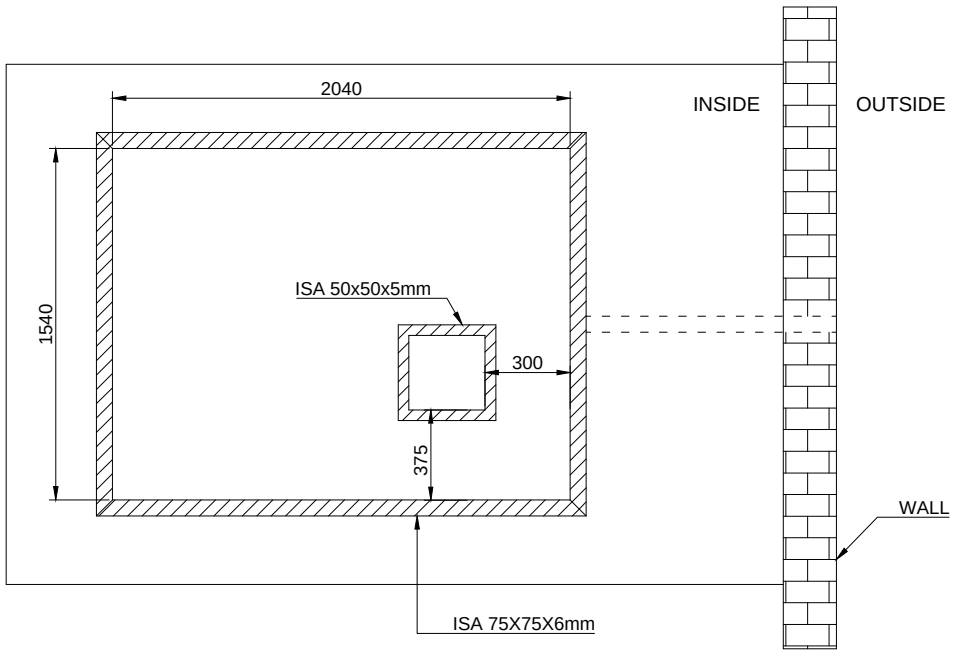


PLAN

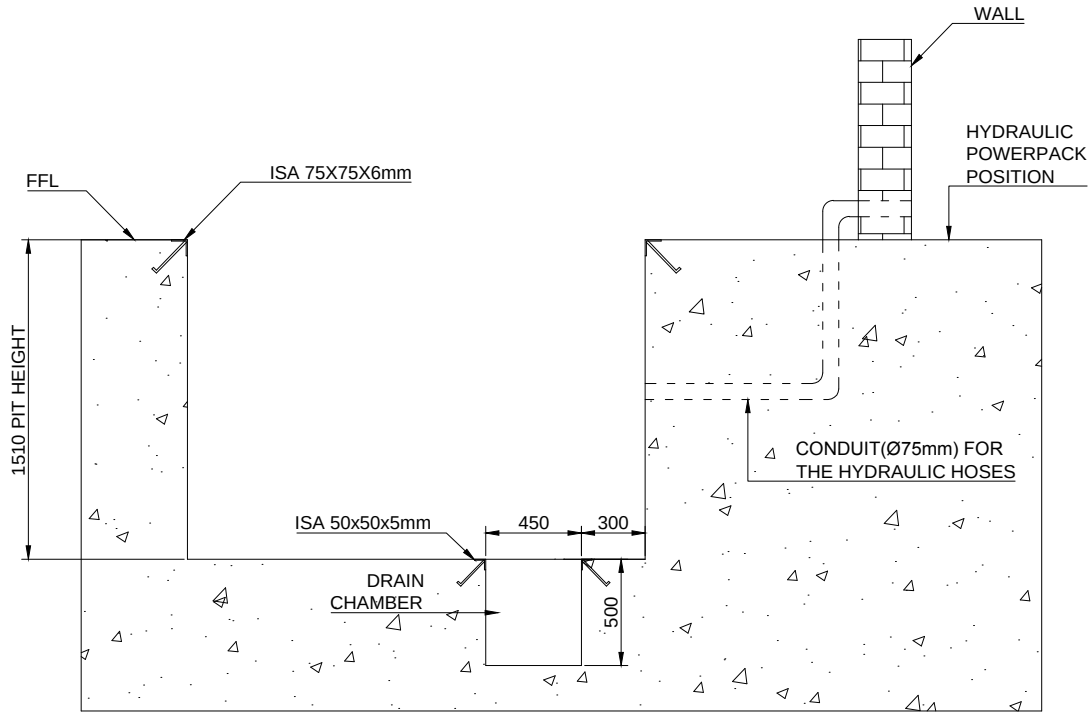

ELEVATION

REVISION 01:–PIT SIZE HAS REVISED.
REVISION 02:–PIT SIZE HAS REVISED TO 1540X2040X1510mm.

This drawing & design is the property of NIHVA TECHNOLOGIES. Not to be sold or copied to any other concern.

TITLE

SCISSOR LIFT
PIT DRAWING

CLIENT APPROVAL

ALL DIMENSION ARE IN mm

NIHVA TECHNOLOGIES PVT. LTD.

NIHVA TECHNOLOGIES
PVT. LTD. PUNE
Tel : 020 66304033
Email:- info@nihva.com
Website:- www.nihva.com

	SIGN	DATE
DRAWN	OMKAR	16/09/17
CHECK	SHEKHAR	16/09/17
REV.		
APPRD.	SHEKHAR	16/09/17
MFG		
Ref. No.		

CLIENT - FUJITA CORPORATION

PROJECT - FUJIKURA KASEI COATING INDIA

SITE -

DWG. NO. - NIHVA/17-18/0199/R02

SCALE: NTS | WT: | SHEET: 01 OF 01

If any queries contact : projects@nihva.com