
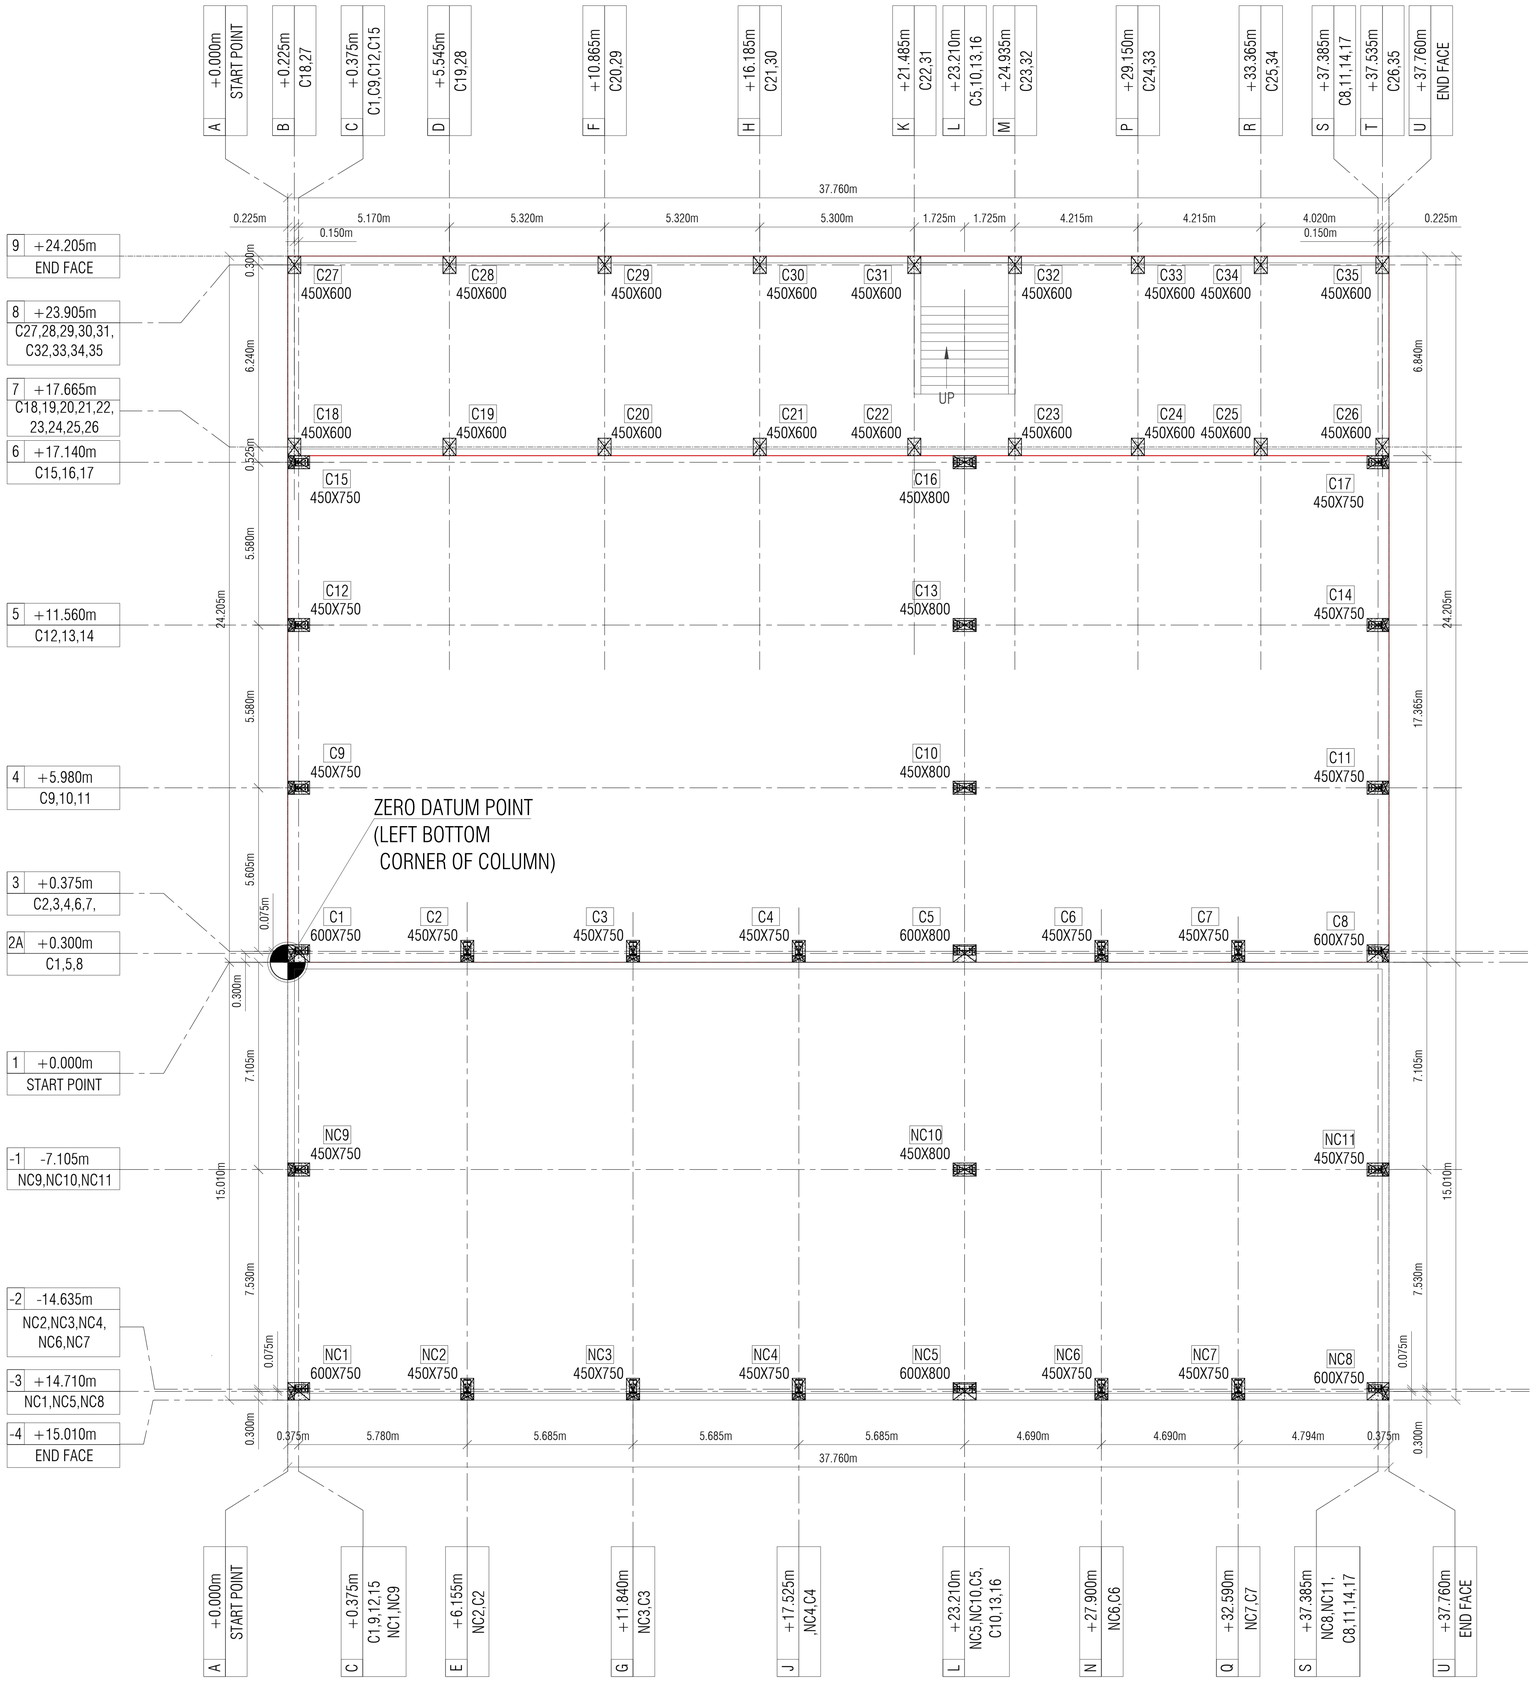


RC COLUMN CENTER LINE DETAILS

SCALE 1:150

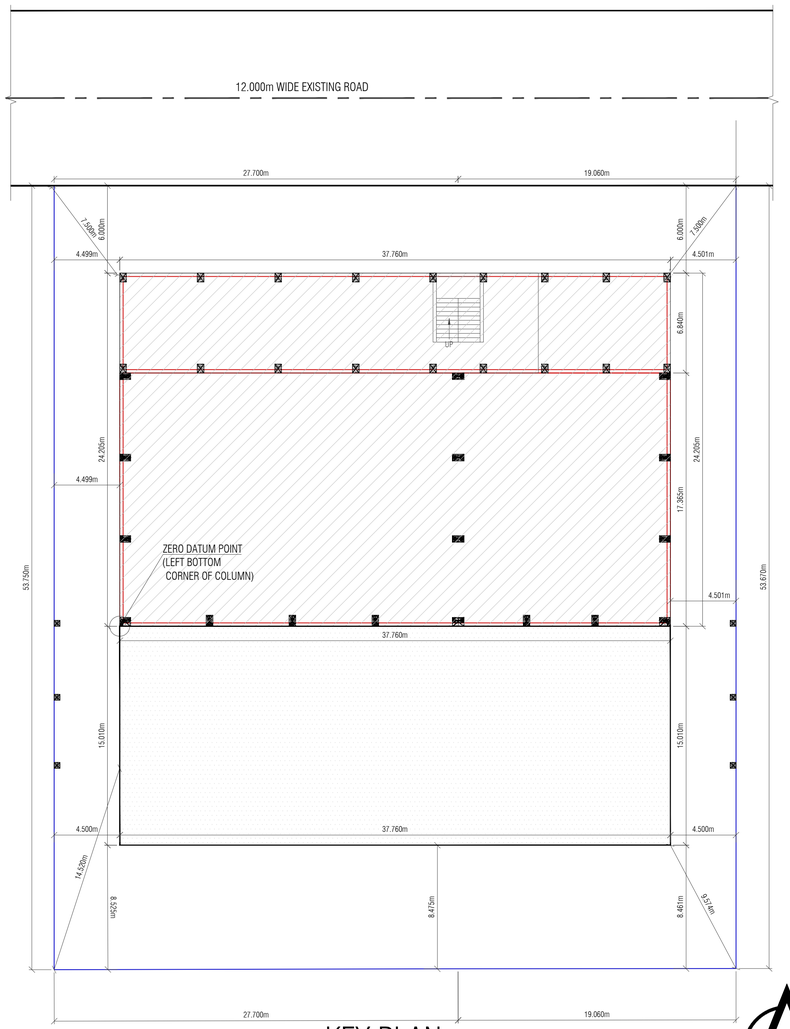

KEY PLAN

SCALE 1:300

No.	Revision/Issue	Date
R1	FOR APPROVAL	23.09.2021
R0	FOR APPROVAL	06.07.2021

Grade of Concrete :-	Design Live Load :-
Grade of Steel :-	Floor Finish Load :-
S.B.C. :-	

RELEASE FOR :- APPROVAL :- ● CONSTRUCTION :-

Firm Name and Address

DYNAMIC CONSULTANTS

STRUCTURAL DESIGNERS AND CHARTERED ENGINEERS

Office No.D-103,Jai Ganesh Varadhast,
Opp Kamgar Bhavan,Pimpri,Pune-411018.
Contact No. - +91 9730738324,9765007893
E-mail - dynamicstruct.consultant@gmail.com
Web - www.dynamicconsultant.co.in

PROJECT :-	PROPOSED INDUSTRIAL BUILDING AT GAT NO. 218. VILLAGE-BHAMBOLI, TAL. - KHED, DIST. - PUNE.
ARCHITECT :-	M/S. DYNAMIC CONSULTANTS, PIMPRI, PUNE
CLIENT :-	MR.PATIL AND MR. GARGOTE
TITLE :-	RC COLUMN CENTER LINE DETALS

CHEKED :-	DESIGN :-	DRAWN :-	JOB NO :-	DWG NO :-
YOGESH	POONAM	POONAM	19167	C100

THIS DRAWING IS PROPERTY OF DYNAMIC CONSULTANTS AND SHALL NOT BE REPRODUCED OR USED WITHOUT EXPLICT PERMISSION OF THIS OFFICE.