





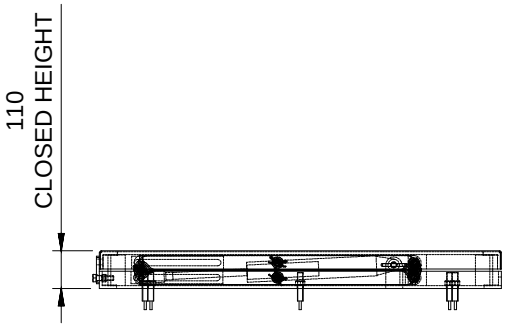

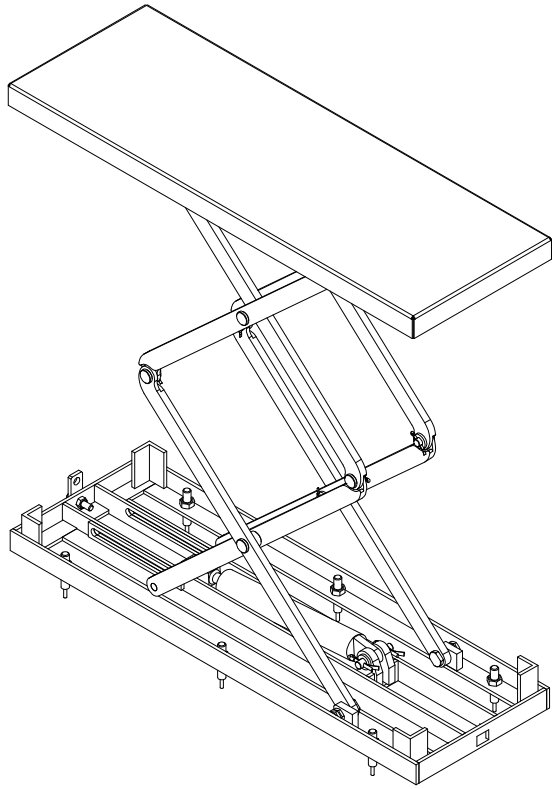

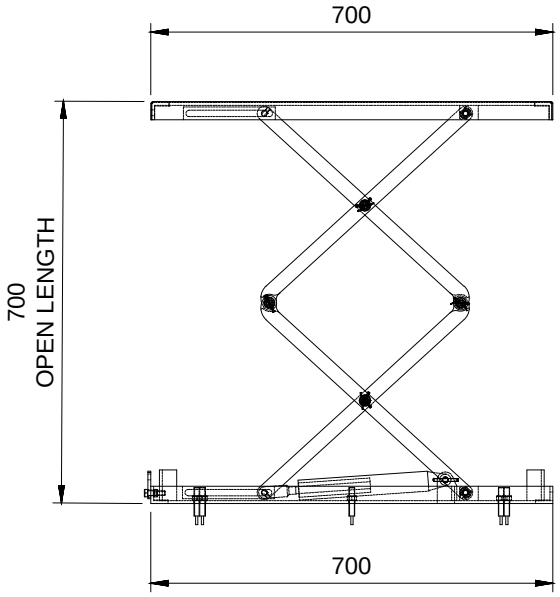

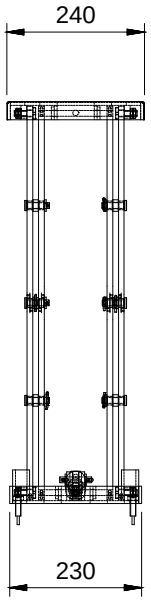

This drawing & designing is the property of NIHVA TECHNOLOGIES. Not to be sold or copied to any other concern.

TITLE: SCISSOR LIFT			NIHVA TECHNOLOGIES PVT. LTD. PUNE Tel : 020 66304033 Email:- info@nihva.com Website:- www.nihva.com
	SIGN	DATE	
DRAWN	OMKAR	21/02/17	CLIENT -
CHECK	SAGAR P.	21/02/17	PROJECT -
REV.			SITE -
APPROVAL	R.K.	21/02/17	DWG. NO. : NIHVA/16-17/VDR/052
If any queries contact : projects@nihva.com			SCALE: NTS | WT: | SHEET: 01 OF 01
ALL DIMENSION ARE IN mm			