
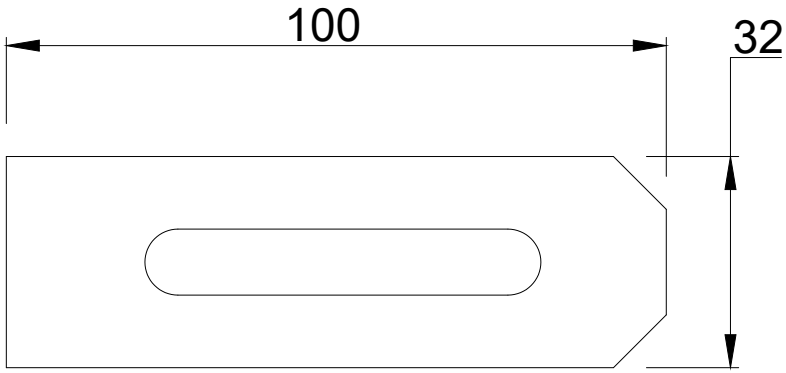


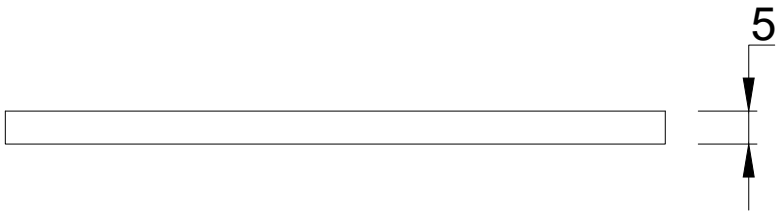

QTY=20 NOS

MTRL : MS

This drawing & design is the property of NIHVA TECHNOLOGIES. Not to be sold or copied to any other concern.

TITLE:- TOWER BOLT HANDLE PLATE			NIHVA TECHNOLOGIES PVT. LTD. PUNE Tel : 020 66304033 Email:- info@nihva.com Website:- www.nihva.com
	NAME	DATE	SIGN
DRAWN	M.SUTAR	15/06/2022	
CHECK	M.SUTAR	15/06/2022	
APPRD.			
CLIENT - NIHVA TECHNOLOGIES PVT.LTD			
LOCATION -			
PRODUCT - SLIDING DOOR			
If any queries contact : design@nihva.com			DWG NO:-NIHVA/22-23/VDR/0015 REV- 0
ALL DIMENSION ARE IN mm			SCALE: NTS SCALE:-- 1:1 SHEET: 01 OF 01

	Date	Revised By